

PROJECT TEAM

DESIGNED BY: VICTOR O.
CONTACT: Available via Upwork messages
WEBSITE: Victor O, Upwork Profile

CLIENT / OWNER

OWNER: DANIEL REYES
LOCATION: 1611 MAPLECREST DRIVE,
AUSTIN, TX 78745

APPLICABLE CODES

INTERNATIONAL RESIDENTIAL CODE (IRC),
2021 EDITION
INTERNATIONAL FIRE CODE (IFC),
2021 EDITION
INTERNATIONAL PLUMBING CODE (IPC),
2021 EDITION
INTERNATIONAL MECHANICAL CODE (IMC),
2021 EDITION
INTERNATIONAL FUEL GAS CODE (IFGC),
2021 EDITION
NATIONAL ELECTRICAL CODE (NEC),
2023 EDITION
INTERNATIONAL ENERGY CONSERVATION
CODE (IECC), 2021 EDITION.

VICINITY MAP



PROJECT DATA

PROJECT DESCRIPTION

ACCESSORY DWELLING UNIT

1611 MAPLECREST DRIVE, AUSTIN, TX 78745

ZONING: SF-3 -- FAMILY RESIDENCE
JURISDICTION: CITY OF AUSTIN, TEXAS
BUILDING USE: ACCESSORY DWLLING UNIT
DENSITY: 2 DWELLING UNIT-7948SQFT
OCCUPANCY CLASS: R-3
CONSTRUCTION TYPE: TYPE V-B (WOOD FRAME)
FRONT SETBACK: EXISTING
SIDE SETBACK: 12FT
REAR SETBACK: 12FT
MAX BLDG HEIGHT: 17FT
A.D.U SQ FOOTAGE: 460 SQFT
EXUSTING S.F.H 1437 SQFT
SITE SQ FOOTAGE: 7948 SQFT
LOT COVERAGE: 23.87%
PARKING: [E] (S.F.H) 2 SPACES (TANDEM)
[N] (A.D.U): 1 SPACE

PERSPECTIVE



SHEET INDEX

- G0.0 COVER PAGE
- G0.1 GENERAL NOTES
- A1.0 SITE PLAN
- A1.1 FOUNDATION PLAN
- A1.2 1ST FLOOR PLAN
- A1.3 ROOF PLAN
- A1.4 RCP/ELECTRICAL
- A2.0 SOUTH & NORTH ELEVATION
- A2.1 EAST & WEST ELEVATION
- A3.0 LONGITUDINAL SECTION
- A3.1 TRANSVERSE SECTION 1 & 2
- A4.0 DETAIL PLAN/ ELEVATIONS
- A4.1 INTERIOR ELEVATIONS
- A4.2 DETAILS
- A5.0 DOORS & WINDOWS
- A5.1 SCHEDULES
- A6.0 3D VIEW
- A6.1 PERSPECTIVE VIEW 1
- A6.2 PERSPECTIVE VIEW 2
- A6.3 AXONOMETRIC VIEW
- A6.4 INTERIOR 3D VIEW


SYMBOLS LEGEND

- SECTION MARKER
- ELEVATION MARKER
- INT ELEVATIONS
- DETAIL CALLOUT
- COMPASS (TRUE)
- DATUM MARKER
- WINDOW CALLOUT
- DOOR CALLOUT
- FIXTURE CALLOUT
- FINISH CALLOUT
- CONTOURS (FEET)
- SOIL
- CONCRETE
- BRICK
- CMU BLOCK
- RIGID INSULATION
- BATT INSULATION

NOTES:

B	Y REVISED	JS	
A	X REVISED	JS	
REV	DESCRIPTION	BY	DATE
AMENDMENTS			
ARCHITECT'S CONTACT DETAILS			
NAME:		VICTOR OMEH	
EMAIL:		omehvictor@gmail.com	
WEBSITE:		www.victoromeh.github.io	
PROJECT TITLE			
ACCESSORY DWELLING UNIT			
SITE			
1611 MAPLECREST DRIVE, AUSTIN, TX 78745			
CLIENT			
DANIEL REYES			
SCALE	DATE.	DRAWN BY.	
NTS	JUNE 2024	VICTOR OMEH	
SHEET NAME COVER PAGE		SHEET NO.	
PROJECT NO. VO-2024-102		A0.0	

NOTES:			
B	Y REVISED	JS	
A	X REVISED	JS	
REV	DESCRIPTION	BY	DATE
AMENDMENTS			
ARCHITECT'S CONTACT DETAILS			
NAME:	VICTOR OMEH		
EMAIL:	omehvictor@gmail.com		
WEBSITE:	www.victoromeh.github.io		
PROJECT TITLE			
ACCESSORY DWELLING UNIT			
SITE			
1611 MAPLECREST DRIVE, AUSTIN, TX 78745			
CLIENT			
DANIEL REYES			
SCALE	DATE.	DRAWN BY.	
NTS	JUNE 2024	VICTOR OMEH	
SHEET NAME	GENERAL NOTES		SHEET NO. A0.1
PROJECT NO.	VO-2024-102		
GENERAL NOTES			
1. WORK SHALL CONFORM TO ALL APPLICABLE CODES AND ORDINANCES, INCLUDING BUT NOT LIMITED TO: BUILDING, PLUMBING, ELECTRICAL, AND MECHANICAL CODES.			
2. ANY ERRORS, OMISSIONS, OR CONFLICTS FOUND WITHIN THESE DRAWINGS SHALL BE BROUGHT TO THE ATTENTION OF THE OWNER OR THEIR REPRESENTATIVE BEFORE PROCEEDING WITH THE WORK.			
3. DO NOT SCALE THESE DRAWINGS. WRITTEN DIMENSIONS TAKE PRECEDENCE OVER MEASUREMENTS.			
4. DIMENSIONS ARE TAKEN FROM FACE OF FRAMING LUMBER, FACE OF CONCRETE/ MASONRY, CENTER OF COLUMN, AND CENTERLINE OF FIXTURE, UNLESS NOTED OTHERWISE.			
5. ALL DIMENSIONS NOTED "VERIFY IN FIELD (V.I.F.)" SHALL BE MEASURED BY THE CONTRACTOR PRIOR TO CONSTRUCTION. REPORT ANY DISCREPANCIES TO THE OWNER OR THEIR REPRESENTATIVE.			
6. DETAILS SHOWN ARE TYPICAL. SIMILAR DETAILS APPLY IN SIMILAR SITUATIONS.			
7. IN THE CASE OF DISCREPANCIES WITHIN DESCRIPTIONS OF SIMILAR ITEMS, PRECEDENCE SHALL BE GIVEN TO NOTES & DRAWINGS OF GREATER DETAIL.			
8. ALL REQUIRED EXITS SHALL BE OPERABLE FROM THE INSIDE, WITHOUT THE USE OF A KEY OR ANY SPECIAL KNOWLEDGE.			
9. ANY ELECTRICAL, PLUMBING AND/OR HVAC SYSTEMS INCLUDED IN THE WORK SHALL BE INSTALLED ON A DESIGN-BUILD BASIS, AND SHALL NOT SIGNIFICANTLY ALTER THE STRUCTURE OR FINISHES.			
10. SMOKE DETECTORS AND CARBON MONOXIDE DETECTORS SHALL BE INSTALLED PER APPLICABLE CODES.			
11. GRADING AND SITEWORK SHALL BE MINIMAL IN ALL AREAS NOT DIRECTLY AFFECTED BY THE NEW CONSTRUCTION. FOLLOW BEST PRACTICES AND LOCAL REQUIREMENTS IN ORDER TO MINIMIZE ENVIRONMENTAL DAMAGE.			
12. FINISH GRADE MUST SLOPE AWAY FROM EXTERIOR FOUNDATION WALL, AT A HEIGHT OF 6 INCHES OVER A 10 FOOT DISTANCE.			
13. ANY SURVEY MARKERS WITHIN THE AREA OF CONSTRUCTION SHALL BE PRESERVED OR RESET BY A REGISTERED CIVIL ENGINEER OR LICENSED LAND SURVEYOR.			
14. BEFORE GRADING OPERATIONS, A TEMPORARY PROTECTION FENCE SHALL BE CONSTRUCTED AROUND ANY TREE WITHIN 30 FEET OF THE FOUNDATION, AND A SILT FENCE MUST BE CONSTRUCTED DOWNSLOPE OF ANY AREA WHERE THE SOIL IS DISTURBED.			
15. DEPICTED FOUNDATION SHOWS ONLY A PROPOSED DESIGN BASED ON FICTIONAL CONDITIONS. CONDUCT A SOIL TEST AND STRUCTURAL ENGINEERING FOR A SITE-SPECIFIC FOUNDATION.			
16. FOOTINGS SHALL EXTEND DOWN BEYOND THE LOCAL FROST LINE.			
17. PERFORATED DRAIN PIPES SHALL BE LOCATED WITHIN A GRAVEL PERIMETER AROUND THE FOUNDATION, WITH MULTIPLE DRAINAGE OUTLETS LEADING DOWNSLOPE AWAY FROM THE BUILDING.			
18. FIRE BLOCKING AND FIRE-RATED SHEATHING SHALL BE PROVIDED AS REQUIRED AT CEILINGS, FLOORS, AND ENCLOSED USABLE SPACE UNDER STAIRS.			
19. ALL WOOD WITHIN 8 INCHES OF THE GROUND SHALL BE PRESSURE TREATED OR COMPRISE A SUITABLY ROT RESISTANT MATERIAL. METAL CONNECTIONS WHICH TOUCH THIS WOOD SHOULD BE GALVANIZED OR STAINLESS STEEL.			
20 PROVIDE ADEQUATE BLOCKING AROUND CABINETRY, PLUMBING FIXTURES, AND OTHER APPLICABLE AREAS.			
21. PROVIDE MINIMUM R-13 INSULATION IN ALL EXTERIOR WALLS AND R-21 INSULATION AT ROOFS OF CONDITIONED SPACES.			
22. DEPICTED WEATHERPROOFING METHODS (SUCH AS SEALANT, CAULKING, AND FLASHING) ARE NOT COMPREHENSIVE. FOLLOW REQUIREMENTS AND RECOMMENDATIONS OF BUILDING CODES, PRODUCT MANUFACTURERS, AND CONSTRUCTION BEST PRACTICES.			
23. CONTRACTOR TO ENSURE THAT INTERIOR SHEATHING IS FLUSH, CLEAN AND FREE OF DUST AND DEFECTS BEFORE APPLICATION OF PAINT COATINGS.			
24. FLOOR MATERIAL TRANSITIONS OCCUR AT THE CENTERLINE OF DOORS OR FRAMED OPENINGS.			
25. PROVIDE ONE COAT PRIMER AND TWO FINISH COATS OF PAINT AT INTERIOR AND EXTERIOR SURFACES.			
26. ALL GLASS SHALL CONFORM WITH HUMAN IMPACT AND SAFETY REQUIREMENTS.			
27. THE MINIMUM STAIRCASE TREAD SHALL BE 10" AND THE MINIMUM RISER 7.75", WITH A MAXIMUM 3⁄8" VARIATION WITHIN A FLIGHT.			
28. HANDRAILS SHALL BE LOCATED 34-38 INCHES ABOVE STAIR TREADS, AS MEASURED FROM THE NOSINGS.			
29. GUARDRAILS SHALL BE LOCATED ALONG ANY FLOOR EDGES THAT DROP 30 INCHES OR MORE TO THE FLOOR OR GROUND BELOW.			
30. DO NOT USE SCREW-ON, NON-OPERABLE WINDOW SHUTTERS. THEY ARE AS TACKY AS CLIP-ON TIES. DO NOT USE VINYL OR ALUMINUM SIDING. THAT WOULD MAKE THIS HOUSE LOOK LIKE A CHEAP PLASTIC TOY. IT IS ABSOLUTELY FORBIDDEN.			
31. ALL CONSTRUCTION SHALL BE TRUE, PLUMB, LEVEL, SQUARE, AND IN PROPER ALIGNMENT.			
32. THE GENERAL CONTRACTOR SHALL MAINTAIN A CURRENT AND COMPLETE SET OF DRAWINGS ON THE JOB SITE DURING ALL PHASES OF CONSTRUCTION. ALL SUBCONTRACTORS SHALL BE PROVIDED WITH A SET OF DRAWINGS.			
33. THE GENERAL CONTRACTOR SHALL VERIFY AND ASSUME RESPONSIBILITY FOR ALL DIMENSIONS AND SITE CONDITIONS, AS WELL AS INSPECT THE PREMISES AND TAKE NOTE OF EXISTING CONDITIONS PRIOR TO SUBMITTING PRICES. NO CLAIM SHALL BE ALLOWED FOR PROBLEMS WHICH COULD HAVE BEEN PREVENTED BY A THOROUGH EXAMINATION.			
34. PROVIDE TEMPORARY SUPPORT AS NECESSARY TO ENSURE THE STRUCTURAL INTEGRITY OF THE BUILDING UNDER CONSTRUCTION. THE GENERAL CONTRACTOR IS RESPONSIBLE FOR ALL CONSTRUCTION-RELATED ACTIVITIES.			
35. INSTALL FIXTURES, MATERIALS, AND EQUIPMENT ACCORDING TO MANUFACTURER'S SPECIFICATIONS. SHOULD THOSE SPECS CONFLICT WITH THE DRAWINGS, IMMEDIATELY NOTIFY THE OWNER OR THE OWNER'S REPRESENTATIVE.			
36. VERIFY CLEARANCES FOR FIXTURES, VENTS, CHASES, ETC. BEFORE ORDERING OR INSTALLING RELATED WORK ITEMS.			
37. COORDINATE ALL WORK WITH EXISTING CONDITIONS, INCLUDING BUT NOT LIMITED TO: IRRIGATION PIPES, ELECTRICAL CONDUITS, WATER LINES, GAS LINES, AND DRAINAGE LINES.			
38. THE GENERAL CONTRACTOR SHALL BE RESPONSIBLE FOR REGULARLY REMOVING THE WASTE MATERIALS OF ALL SUBCONTRACTORS, AND MAINTAIN STRICT CONTROL OVER JOB CLEANING TO PREVENT DUST AND RUBBISH FROM INTERFERING WITH OPERATIONS.			
39. CONSTRUCTION EQUIPMENT NOISE SHALL BE MINIMIZED DURING THE CONSTRUCTION PHASES BY MUFFLING AND SHIELDING IMPACT TOOLS WHENEVER POSSIBLE.			

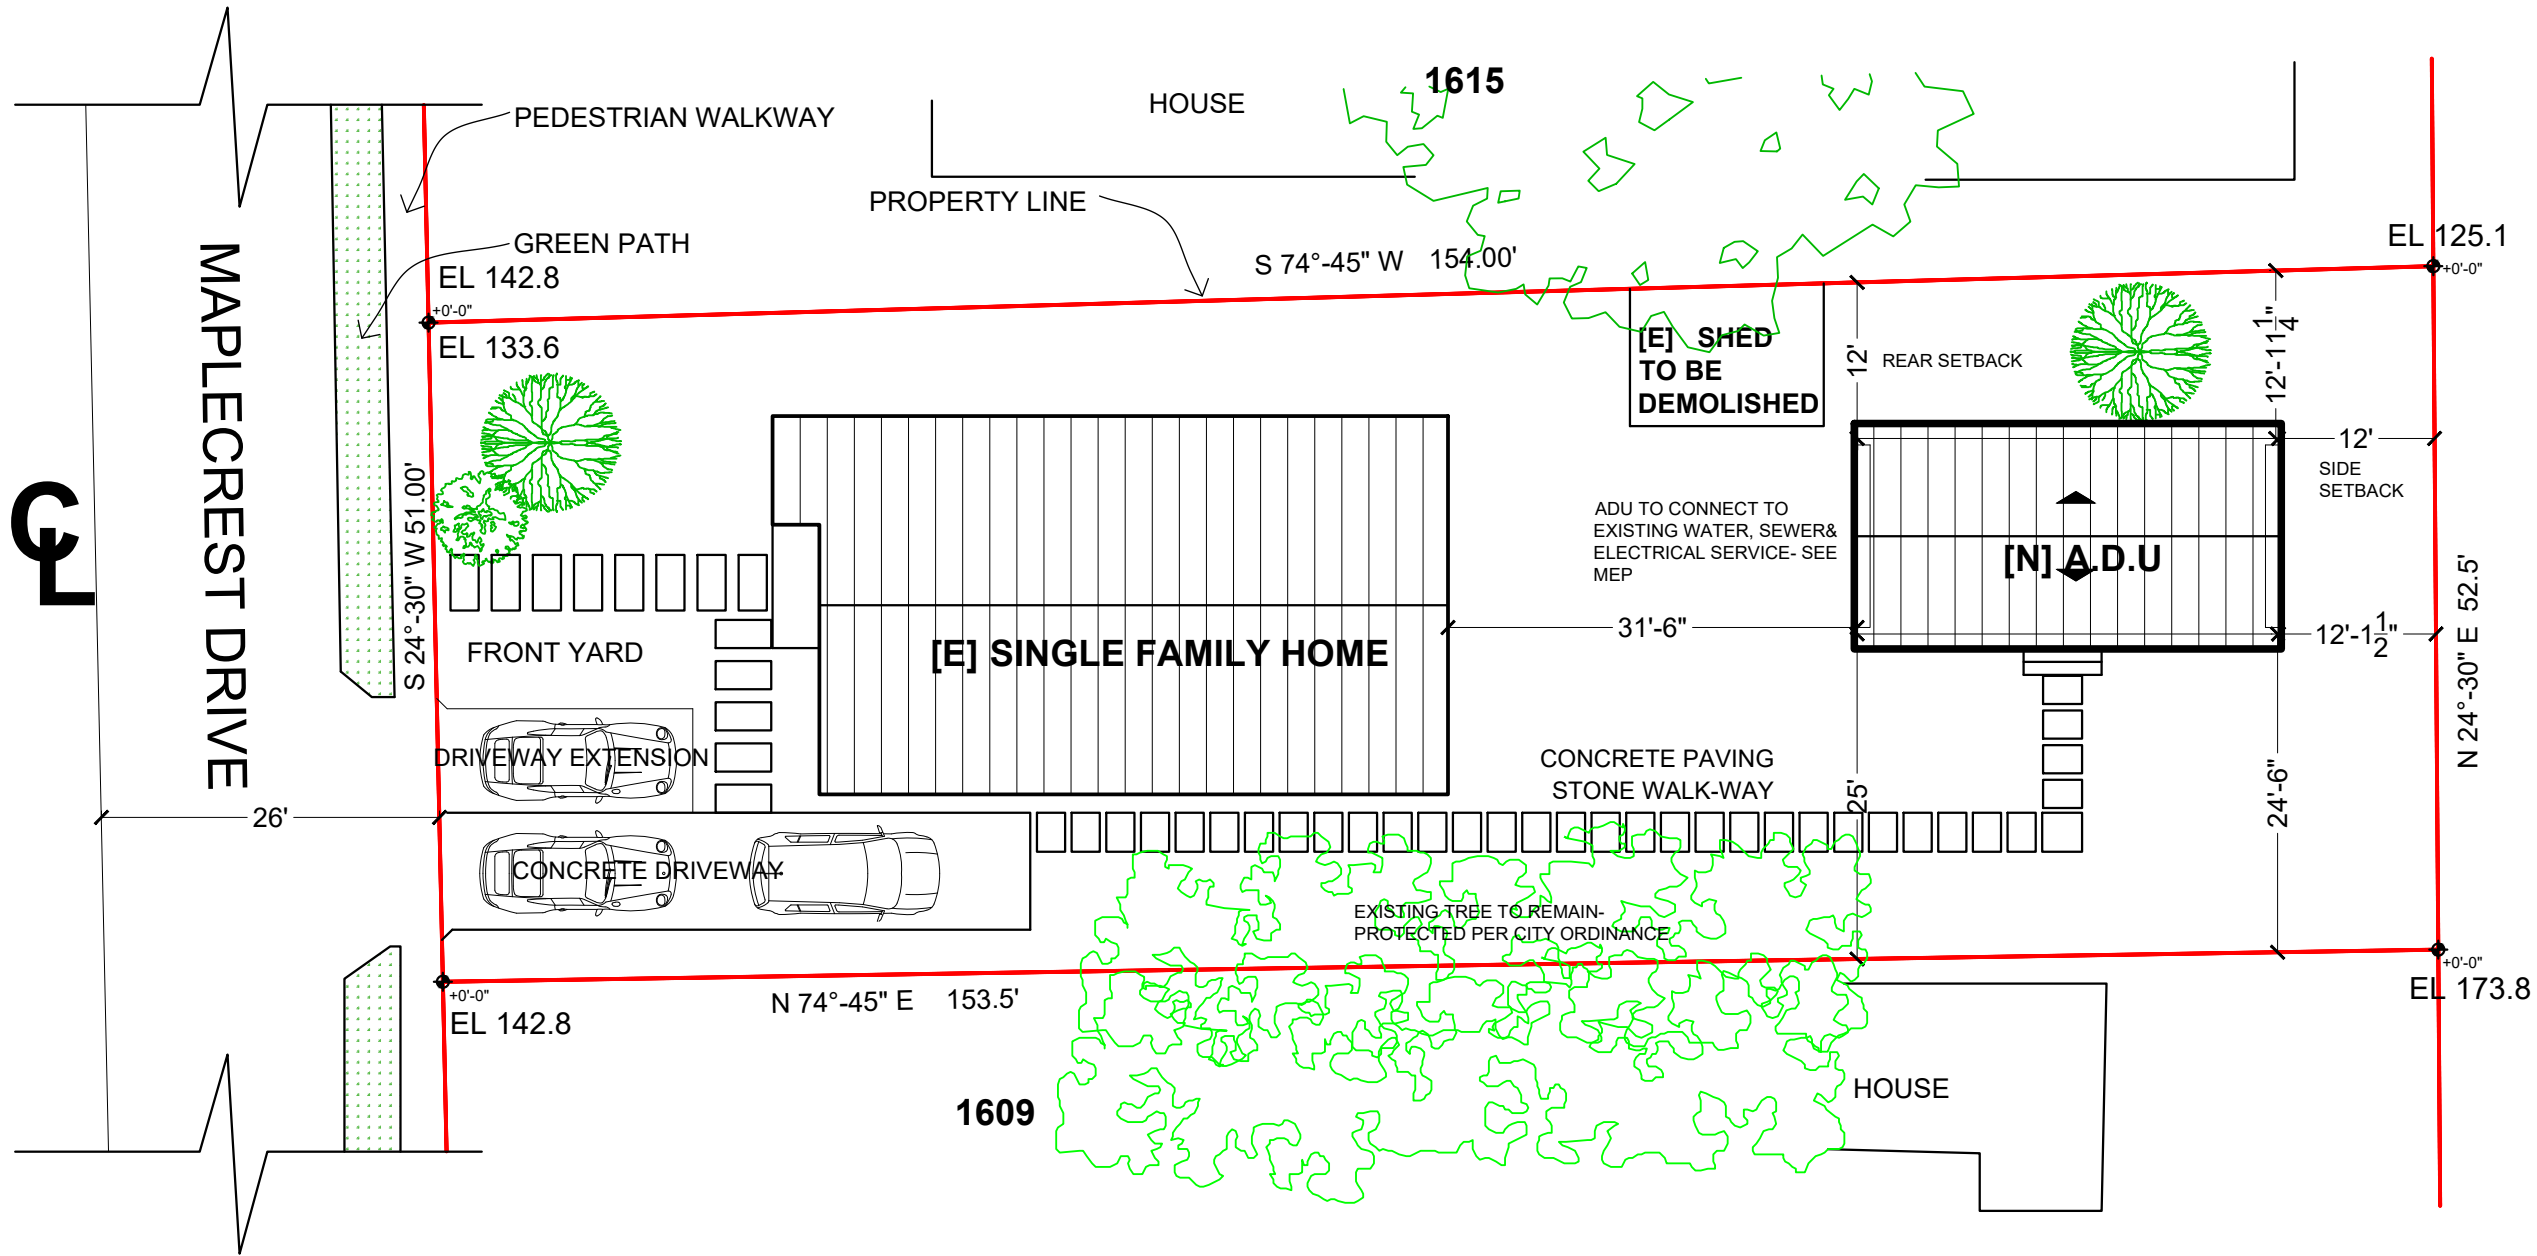

1 SITE / LANDSCAPE PLAN

NOTE: ADU DIMENSIONS ARE MEASURED TO FOUNDATION

NOTES:

B	Y REVISED	JS	
A	X REVISED	JS	
REV	DESCRIPTION	BY	DATE

AMENDMENTS

ARCHITECT'S CONTACT DETAILS

NAME: VICTOR OMEH

EMAIL: omehvictor@gmail.com

WEBSITE: www.victoromeh.github.io

PROJECT TITLE

ACCESSORY DWELLING UNIT

SITE


1611 MAPLECREST DRIVE,
AUSTIN, TX 78745

CLIENT

DANIEL REYES

SCALE	DATE	DRAWN BY.
NTS	JUNE 2024	VICTOR OMEH

SHEET NAME	SITE PLAN	SHEET NO.
PROJECT NO.	VO-2024-102	A1.0

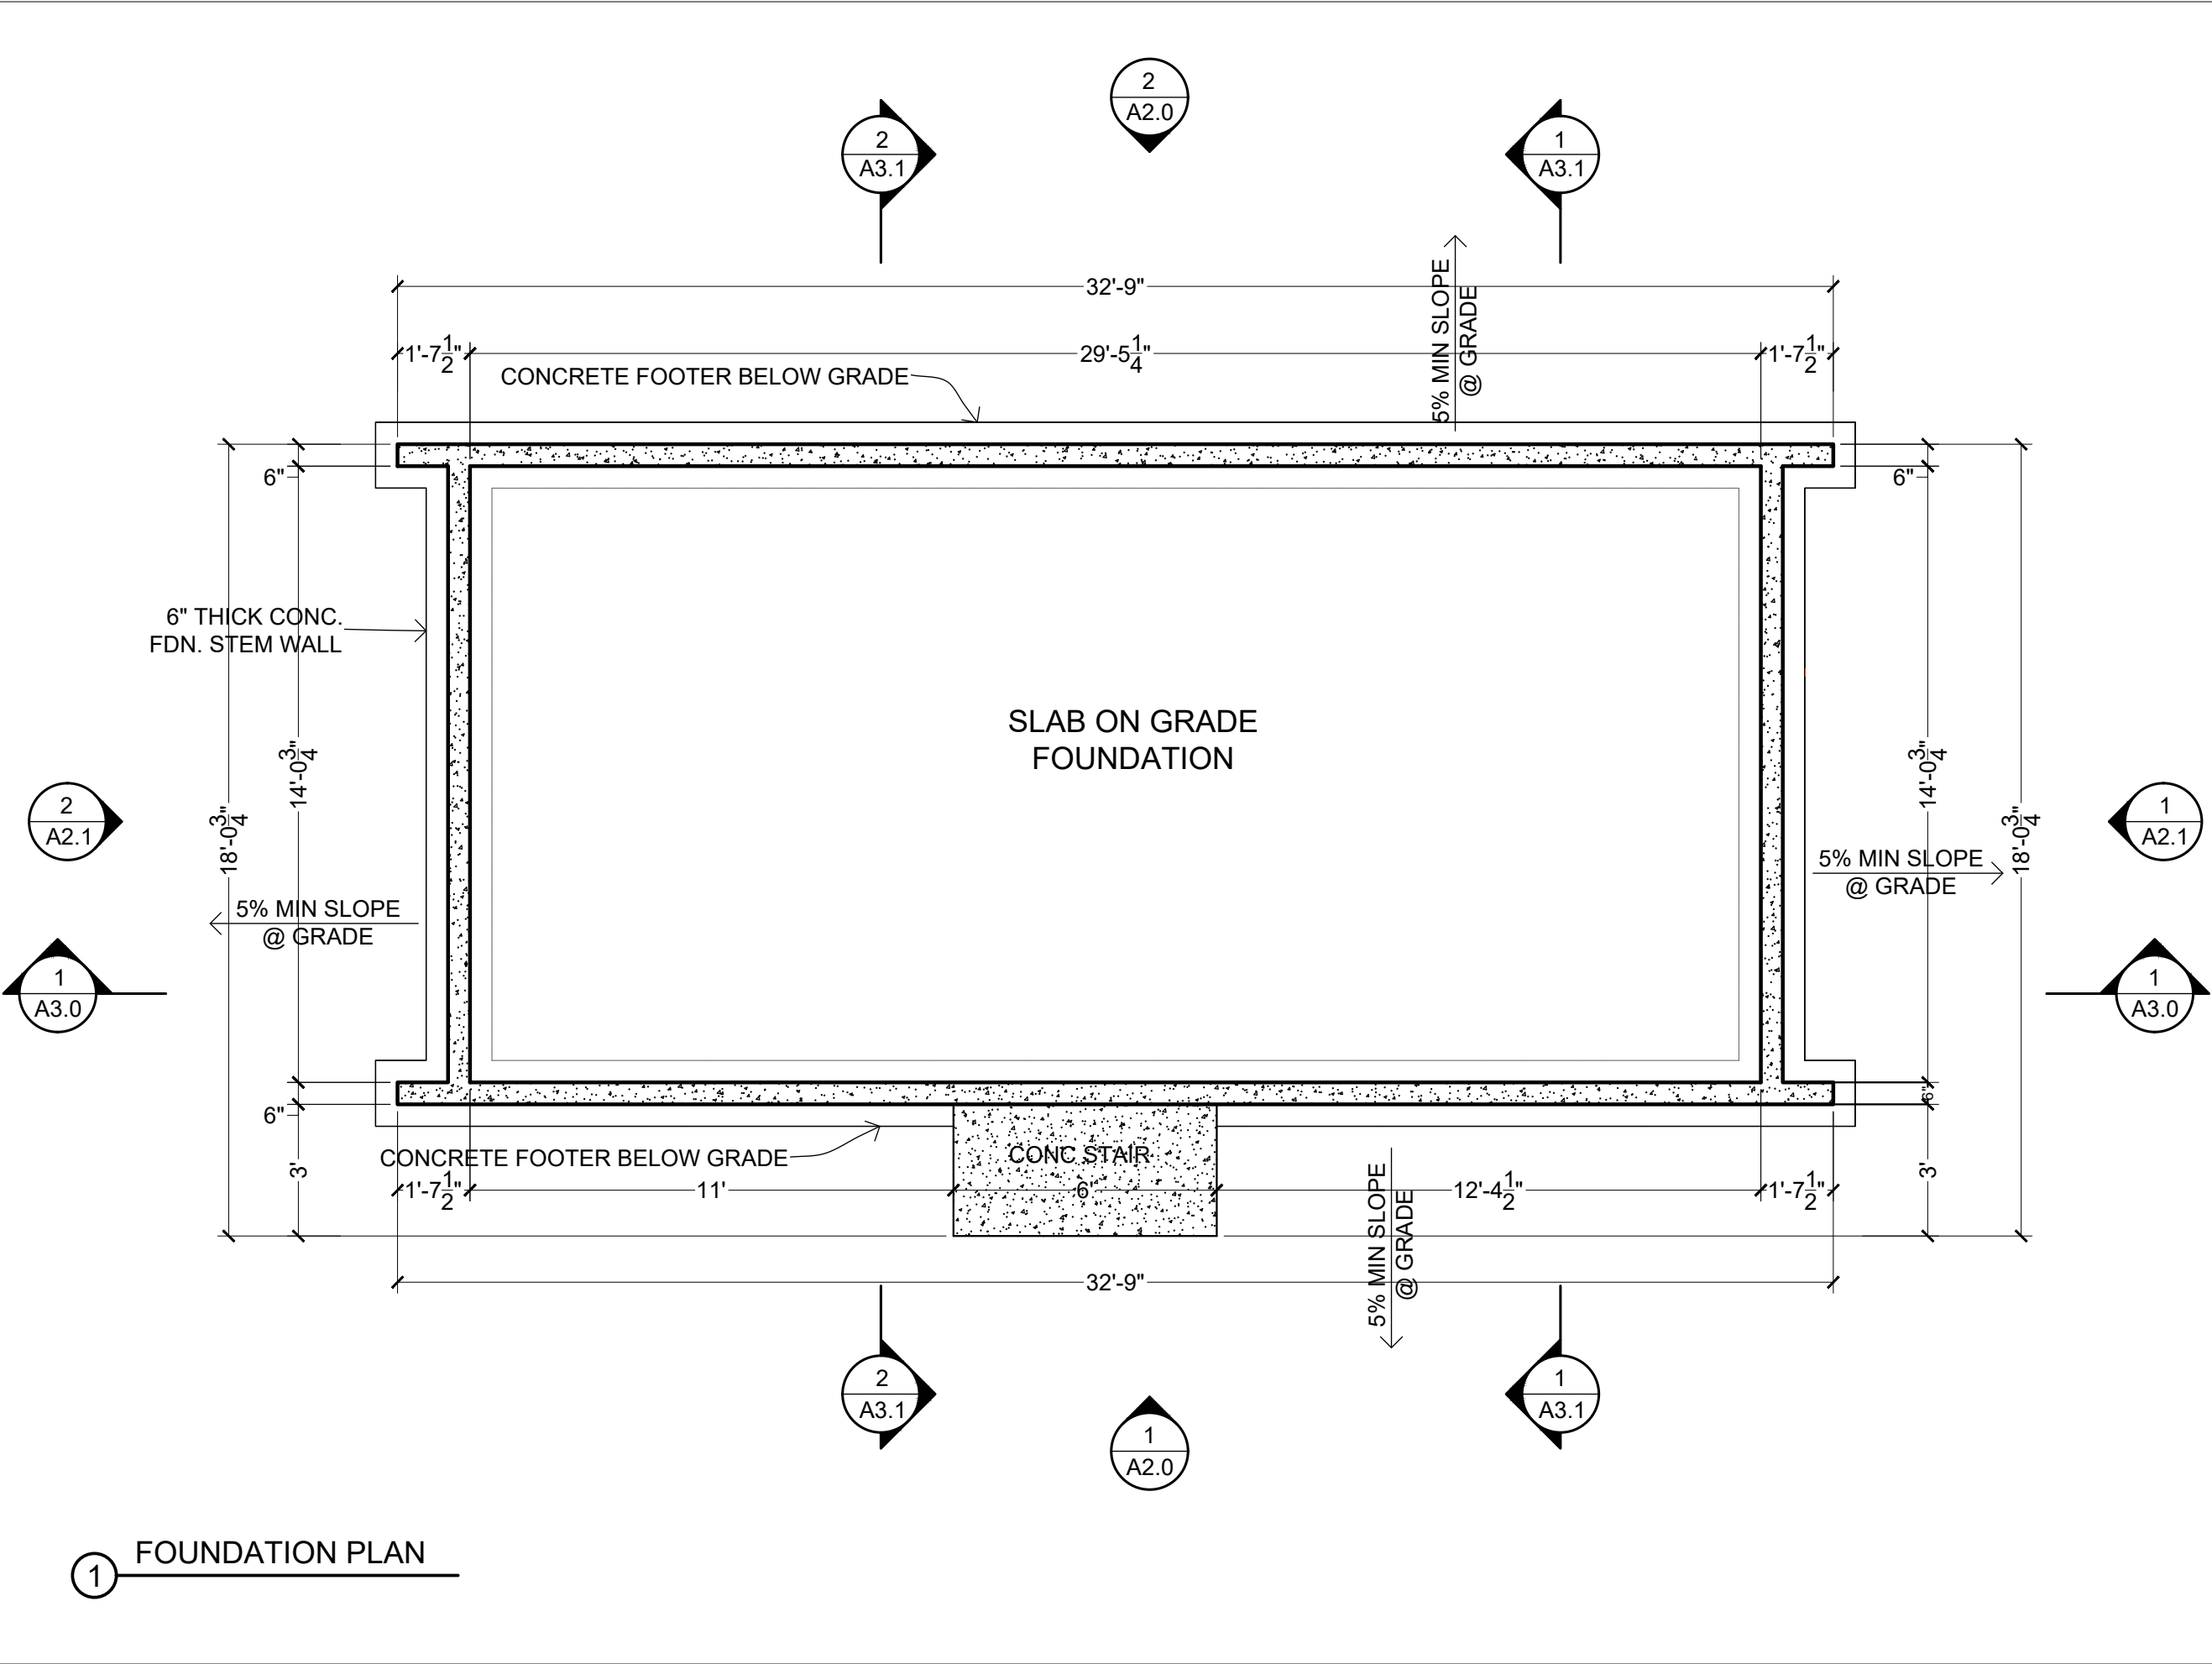

1 FOUNDATION PLAN

NOTES:

B	Y REVISED	JS	
A	X REVISED	JS	
REV	DESCRIPTION	BY	DATE

AMENDMENTS

ARCHITECT'S CONTACT DETAILS

NAME: VICTOR OMEH
EMAIL: omehvictor@gmail.com
WEBSITE: www.victoromeh.github.io

PROJECT TITLE

ACCESSORY DWELLING UNIT

SITE


1611 MAPLECREST DRIVE,
AUSTIN, TX 78745

CLIENT

DANIEL REYES

SCALE	DATE	DRAWN BY.
NTS	JUNE 2024	VICTOR OMEH

SHEET NAME	FOUNDATION PLAN	SHEET NO.
PROJECT NO.	VO-2024-102	A1.1

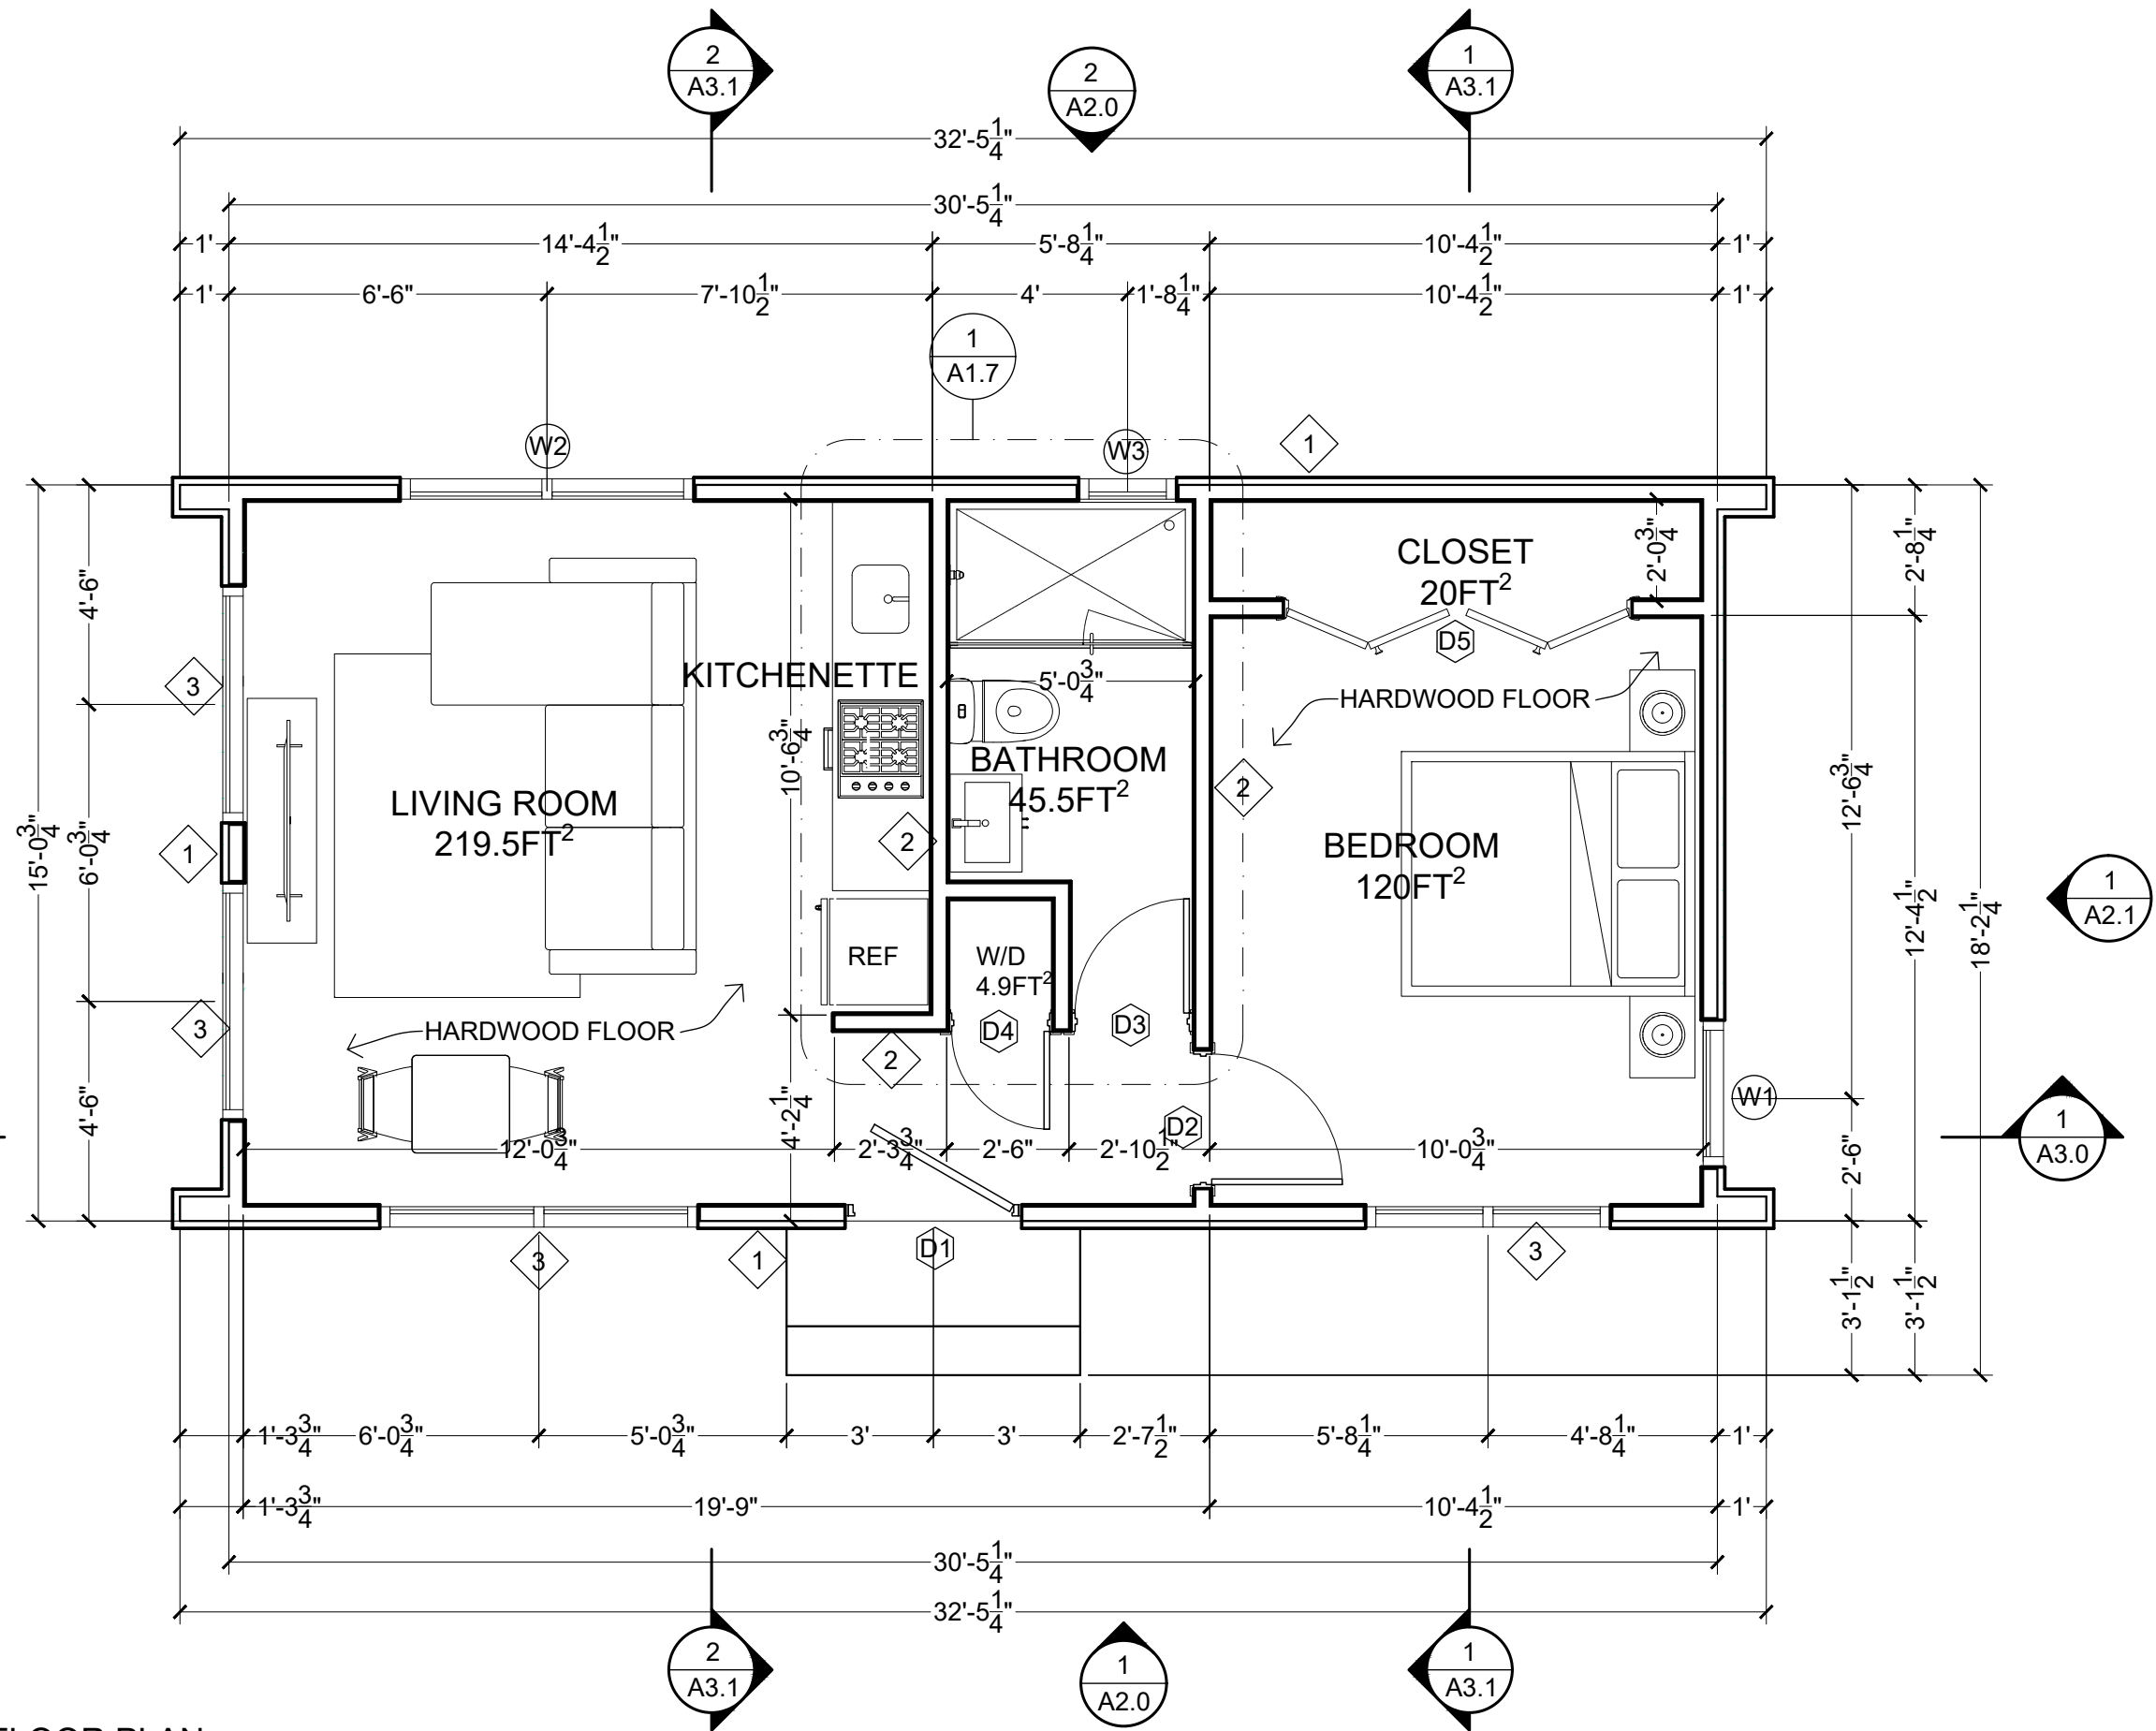

1 FIRST FLOOR PLAN

NOTES:

B	Y REVISED	JS	
A	X REVISED	JS	
REV	DESCRIPTION	BY	DATE

AMENDMENTS

ARCHITECT'S CONTACT DETAILS

NAME: VICTOR OMEH
EMAIL: omehvictor@gmail.com
WEBSITE: www.victoromeh.github.io

PROJECT TITLE

ACCESSORY DWELLING UNIT

SITE


1611 MAPLECREST DRIVE,
AUSTIN, TX 78745

CLIENT

DANIEL REYES

SCALE	DATE.	DRAWN BY.
NTS	JUNE 2024	VICTOR OMEH


SHEET NAME	FIRST FLOOR PLAN	SHEET NO.
PROJECT NO.	VO-2024-102	A1.2

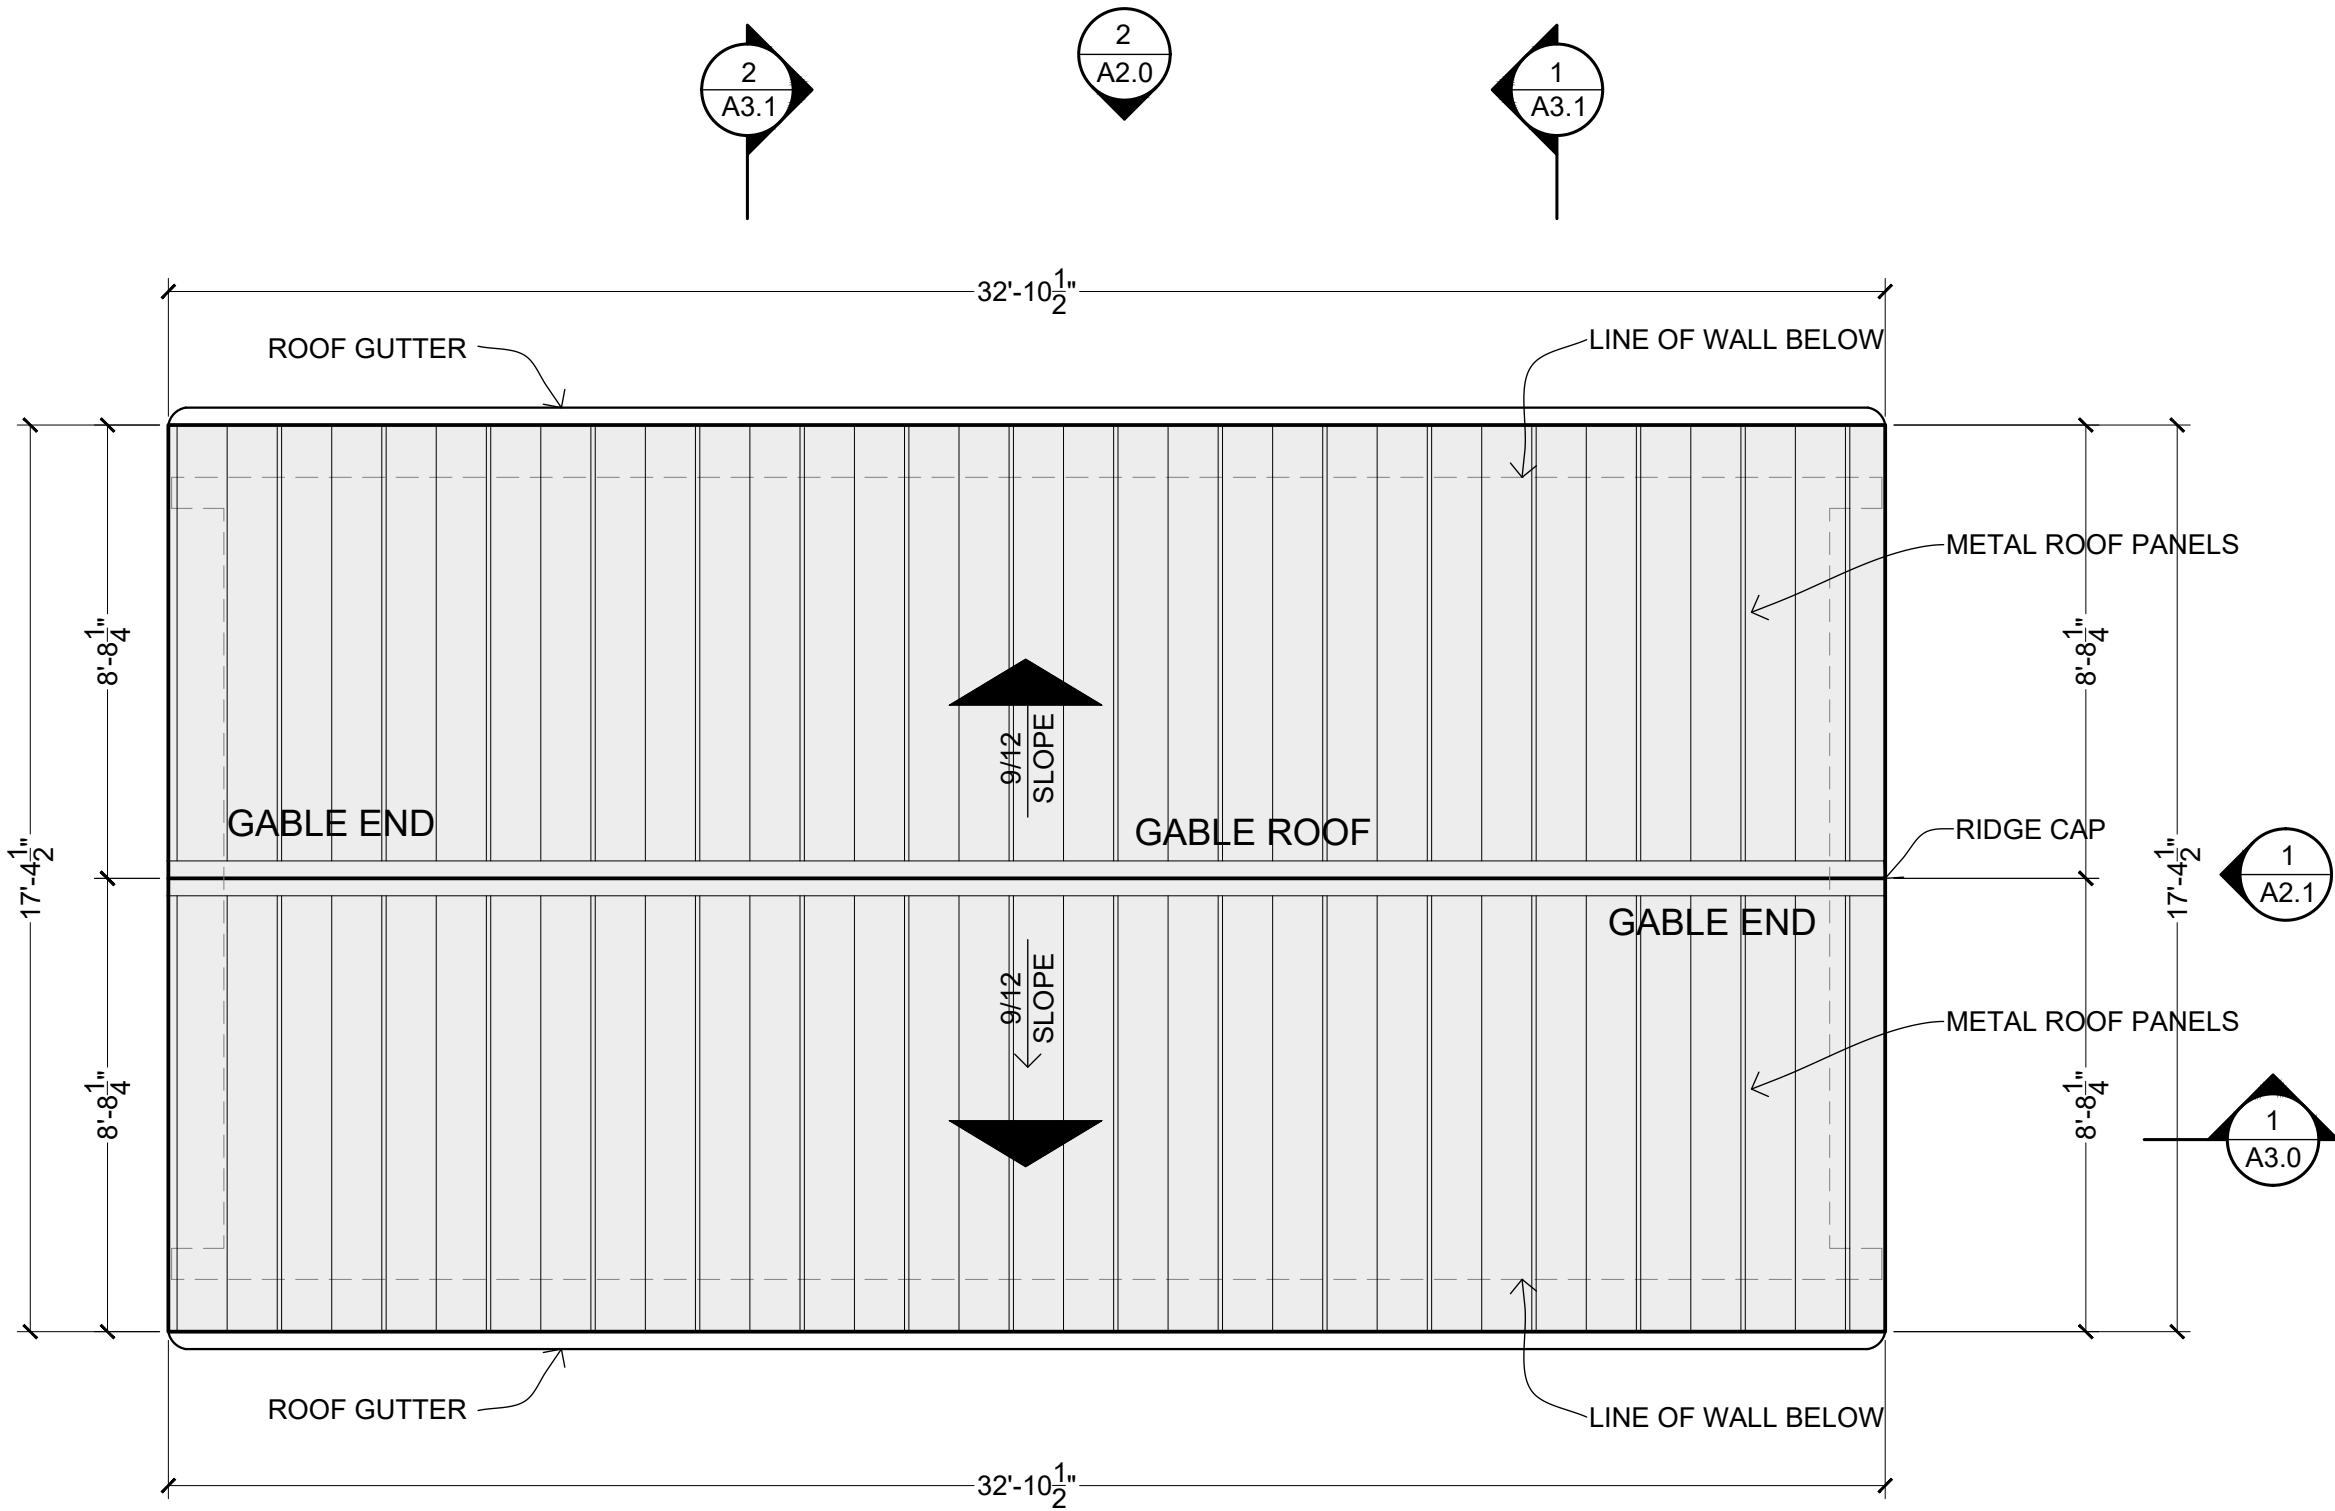

1 ROOF PLAN

NOTES:

B	Y REVISED	JS	
A	X REVISED	JS	
REV	DESCRIPTION	BY	DATE
AMENDMENTS			
ARCHITECT'S CONTACT DETAILS			
NAME:	VICTOR OMEH		
EMAIL:	omehvictor@gmail.com		
WEBSITE:	www.victoromeh.github.io		
PROJECT TITLE			
ACCESSORY DWELLING UNIT			
SITE			
1611 MAPLECREST DRIVE, AUSTIN, TX 78745			
CLIENT			
DANIEL REYES			
SCALE	DATE.	DRAWN BY.	
NTS	JUNE 2024	VICTOR OMEH	
SHEET NAME		SHEET NO.	
ROOF PLAN		A1.3	
PROJECT NO.		VO-2024-102	

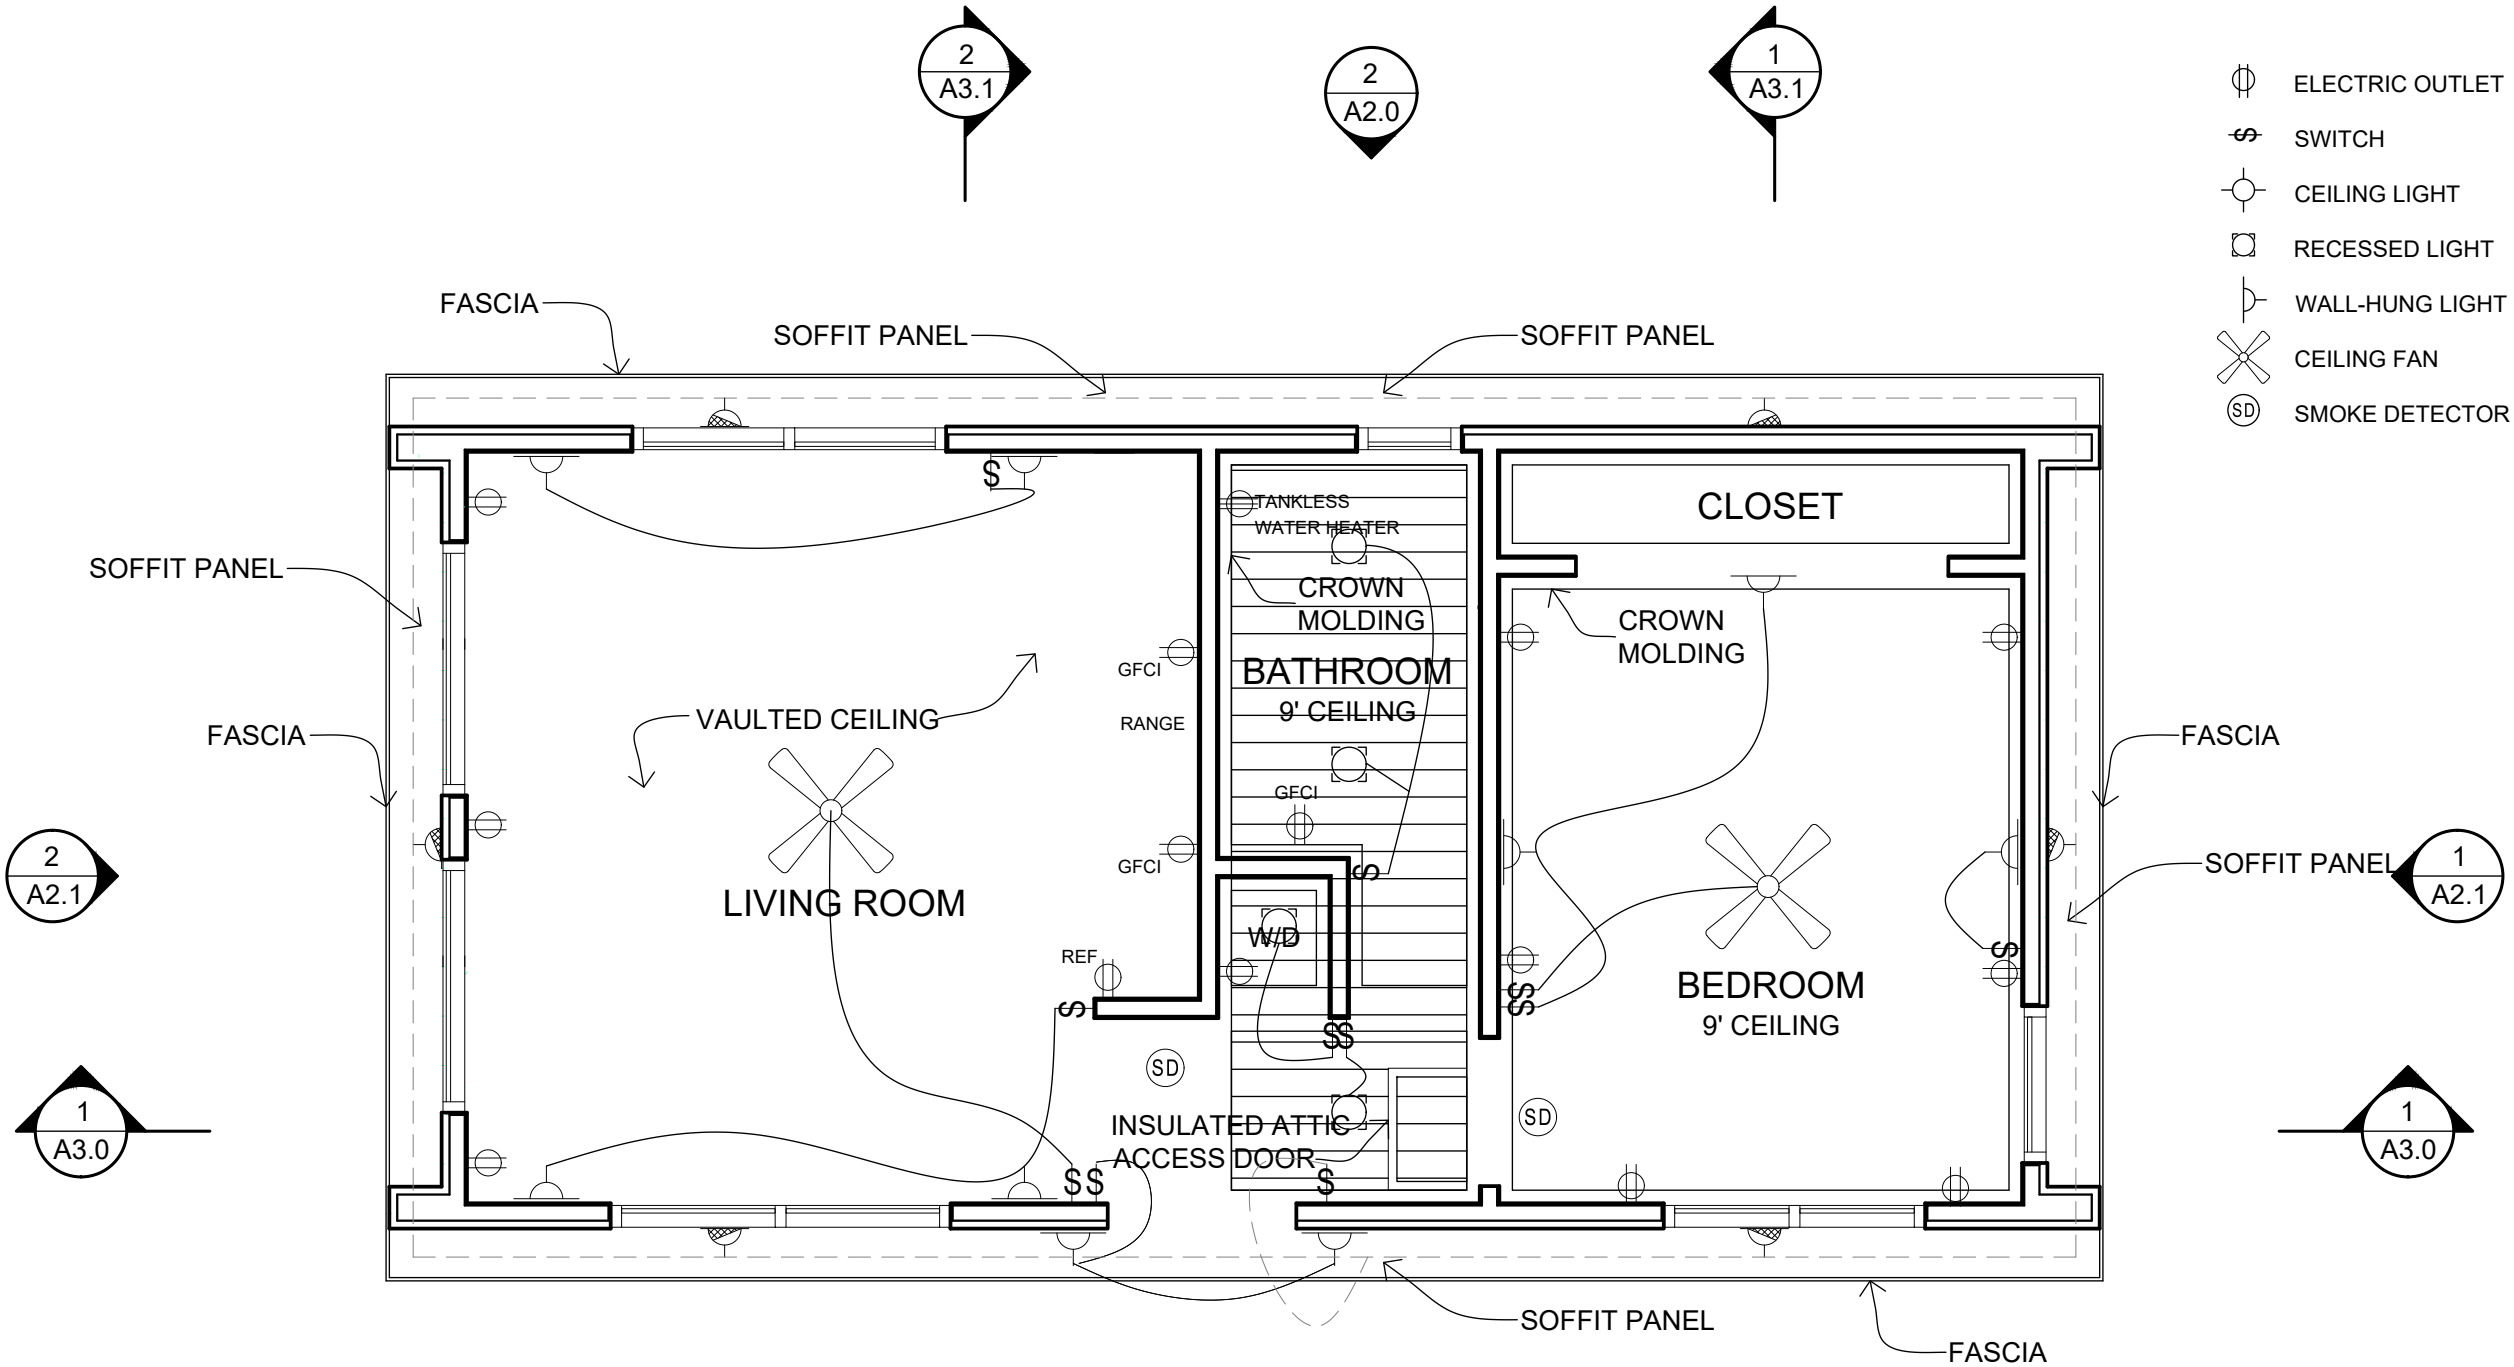

1 REFLECTED CEILING PLAN/ ELECTRICAL

NOTES:

B	Y REVISED	JS	
A	X REVISED	JS	
REV	DESCRIPTION	BY	DATE

AMENDMENTS

ARCHITECT'S CONTACT DETAILS

NAME: VICTOR OMEH

EMAIL: omehvictor@gmail.com

WEBSITE: www.victoromeh.github.io

PROJECT TITLE

ACCESSORY DWELLING UNIT

SITE


1611 MAPLECREST DRIVE,
AUSTIN, TX 78745

CLIENT


DANIEL REYES

SCALE	DATE	DRAWN BY.
NTS	JUNE 2024	VICTOR OMEH

SHEET NAME	RCP/ ELECTRICAL	SHEET NO.
PROJECT NO.	VO-2024-102	A1.4

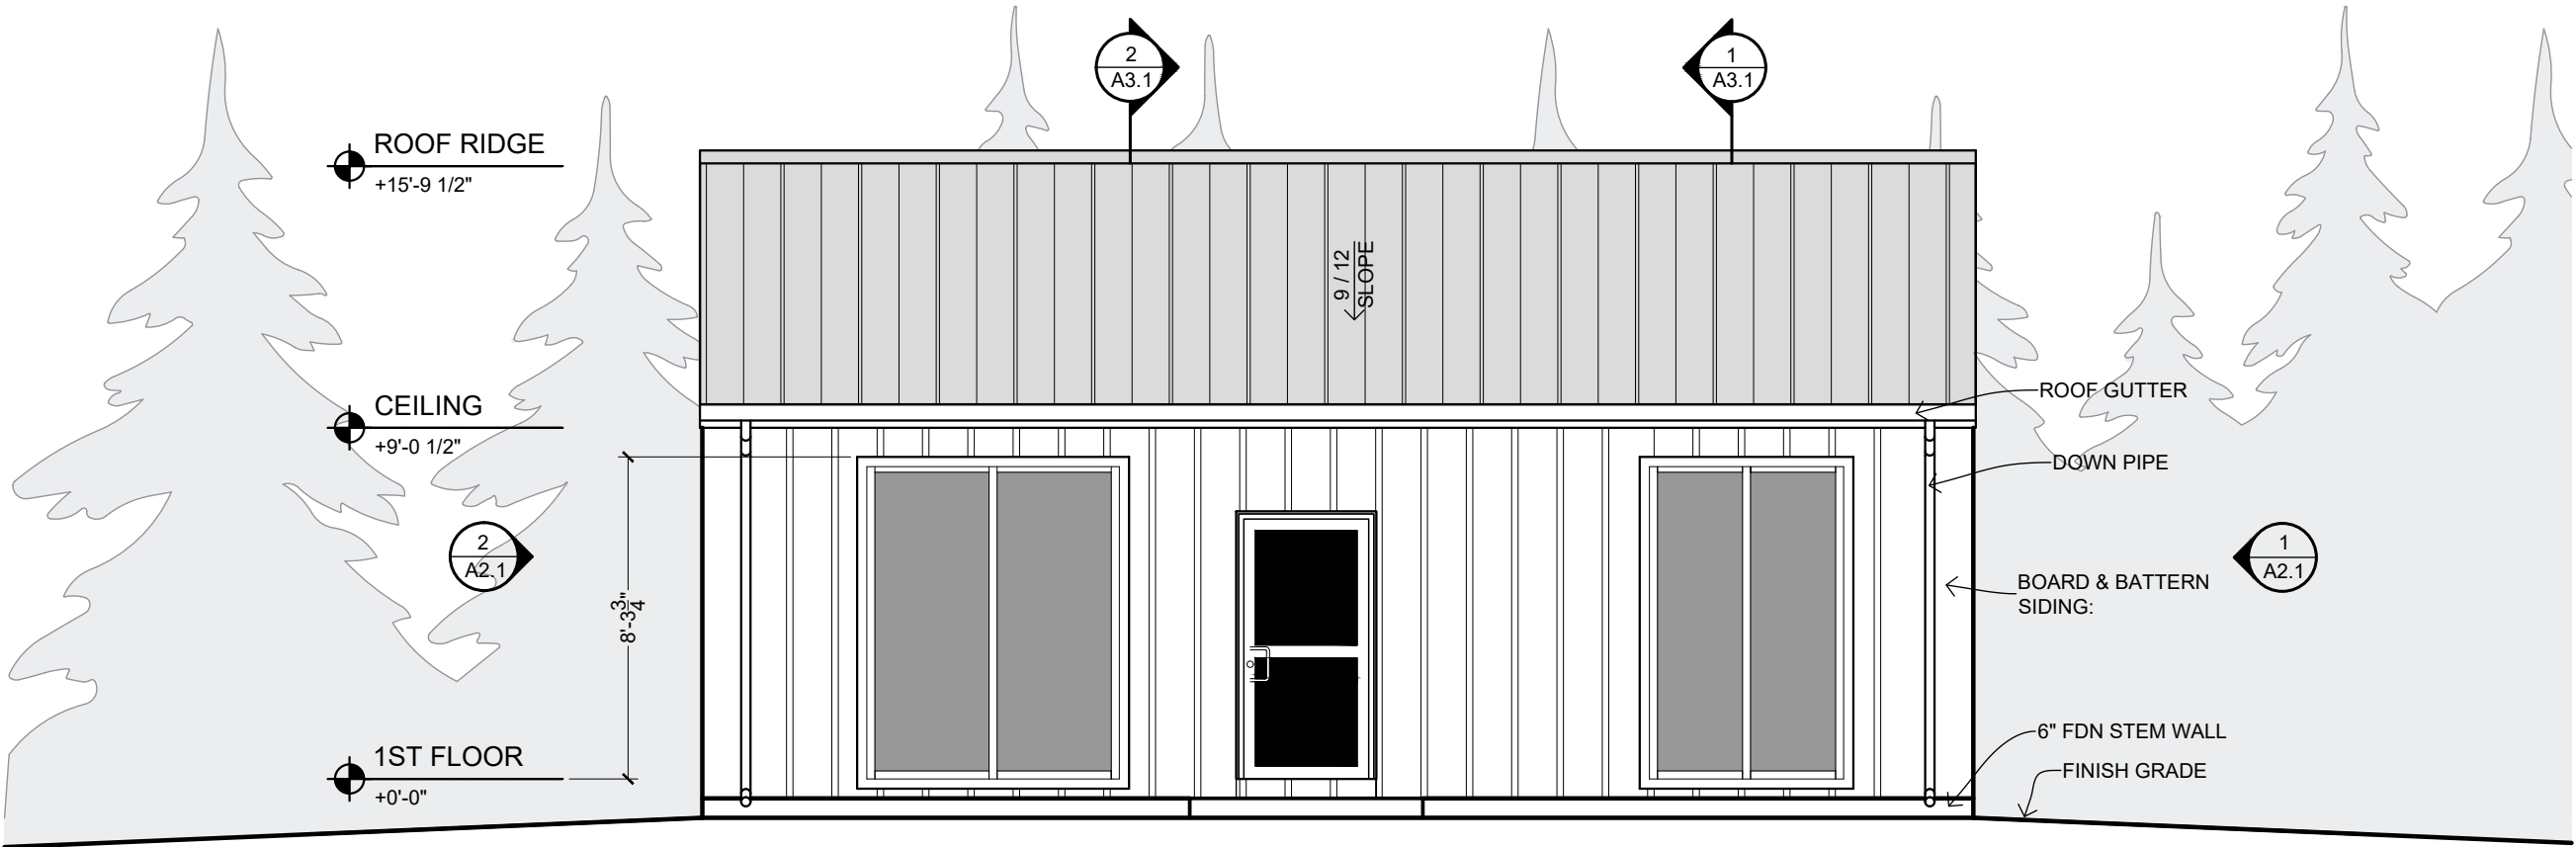

1 FRONT ELEVATION (SOUTH)

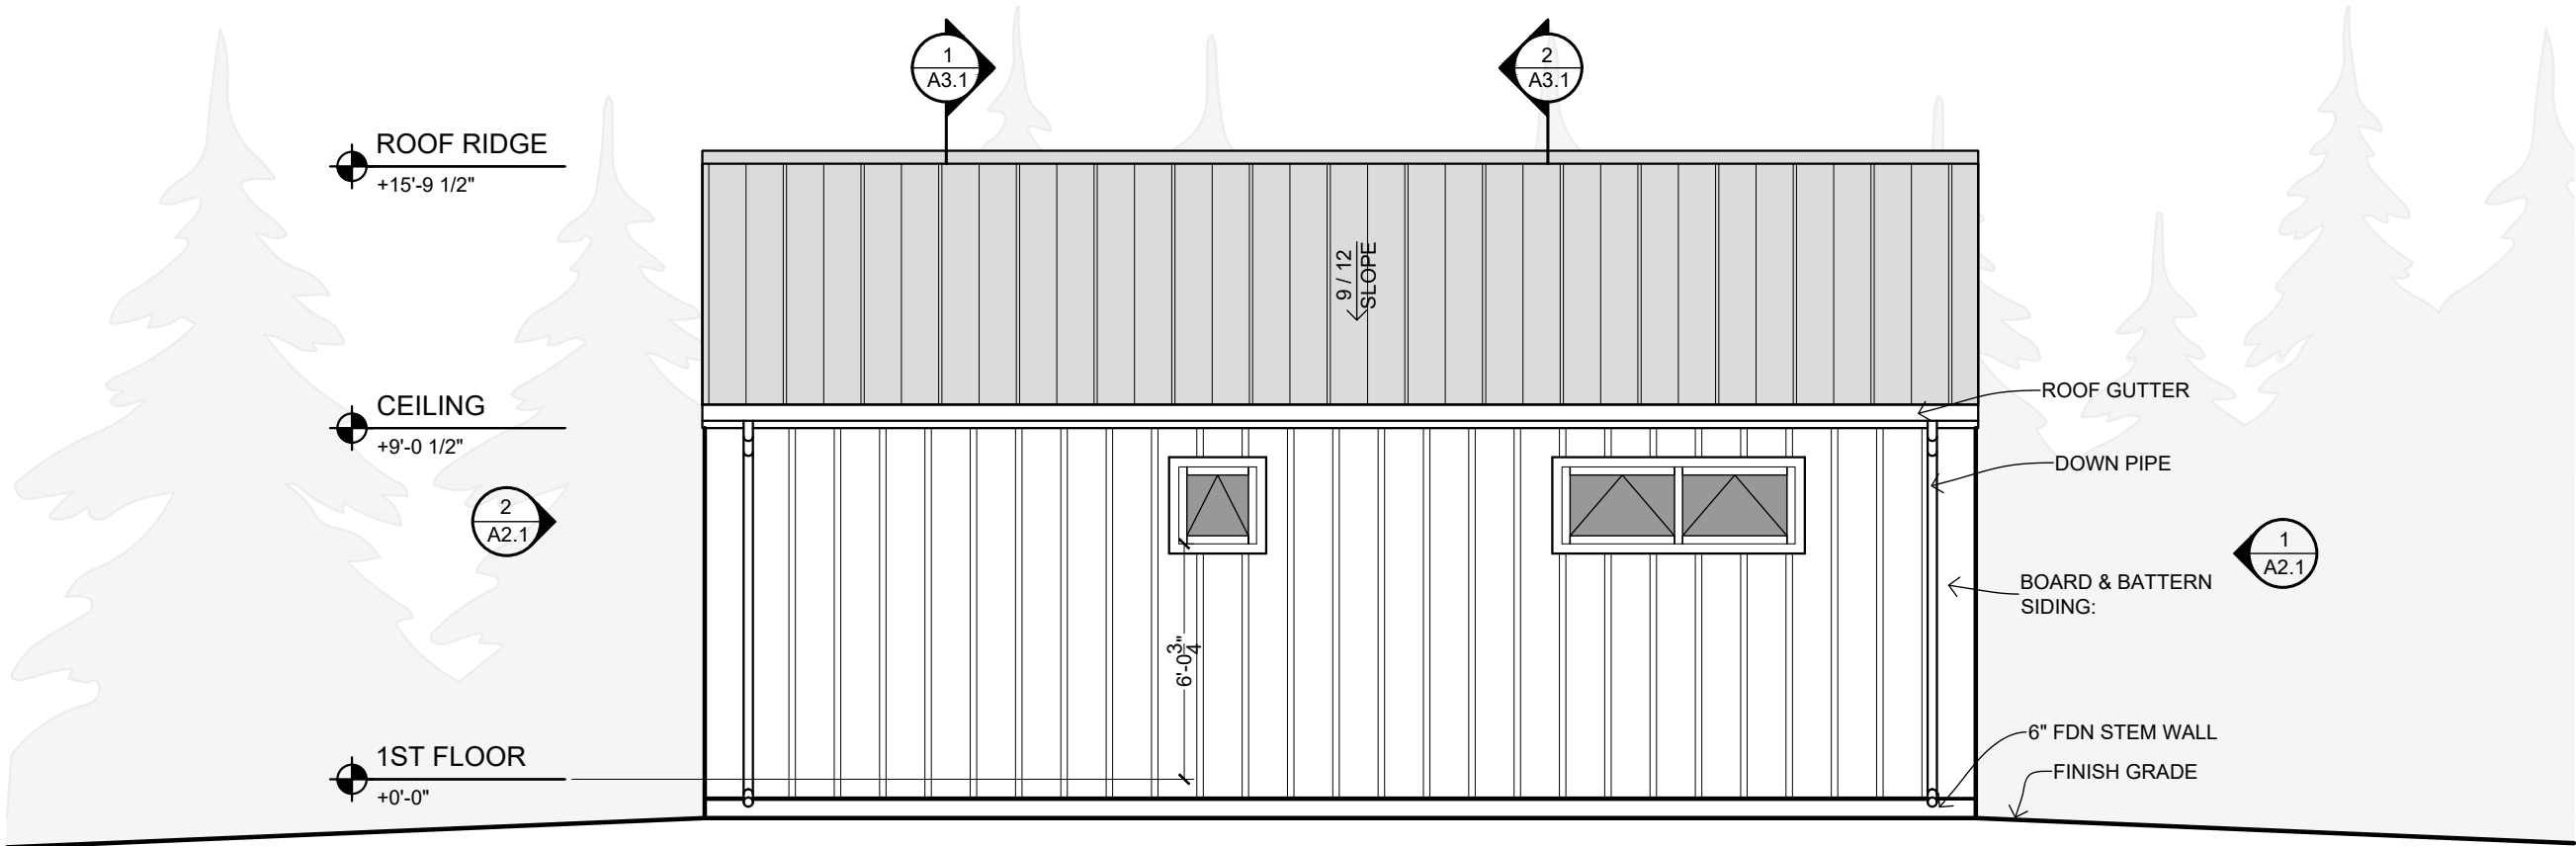

1 BACK ELEVATION (NORTH)

NOTES:

B	Y REVISED	JS	
A	X REVISED	JS	
REV	DESCRIPTION	BY	DATE

AMENDMENTS

ARCHITECT'S CONTACT DETAILS

NAME: VICTOR OMEH

EMAIL: omehvictor@gmail.com

WEBSITE: www.victoromeh.github.io

PROJECT TITLE

ACCESSORY DWELLING UNIT

SITE


1611 MAPLECREST DRIVE,
AUSTIN, TX 78745

CLIENT


DANIEL REYES

SCALE	DATE.	DRAWN BY.
NTS	JUNE 2024	VICTOR OMEH

SHEET NAME	NORTH & SOUTH ELEVATION	SHEET NO.
PROJECT NO.	VO-2024-102	A2.0

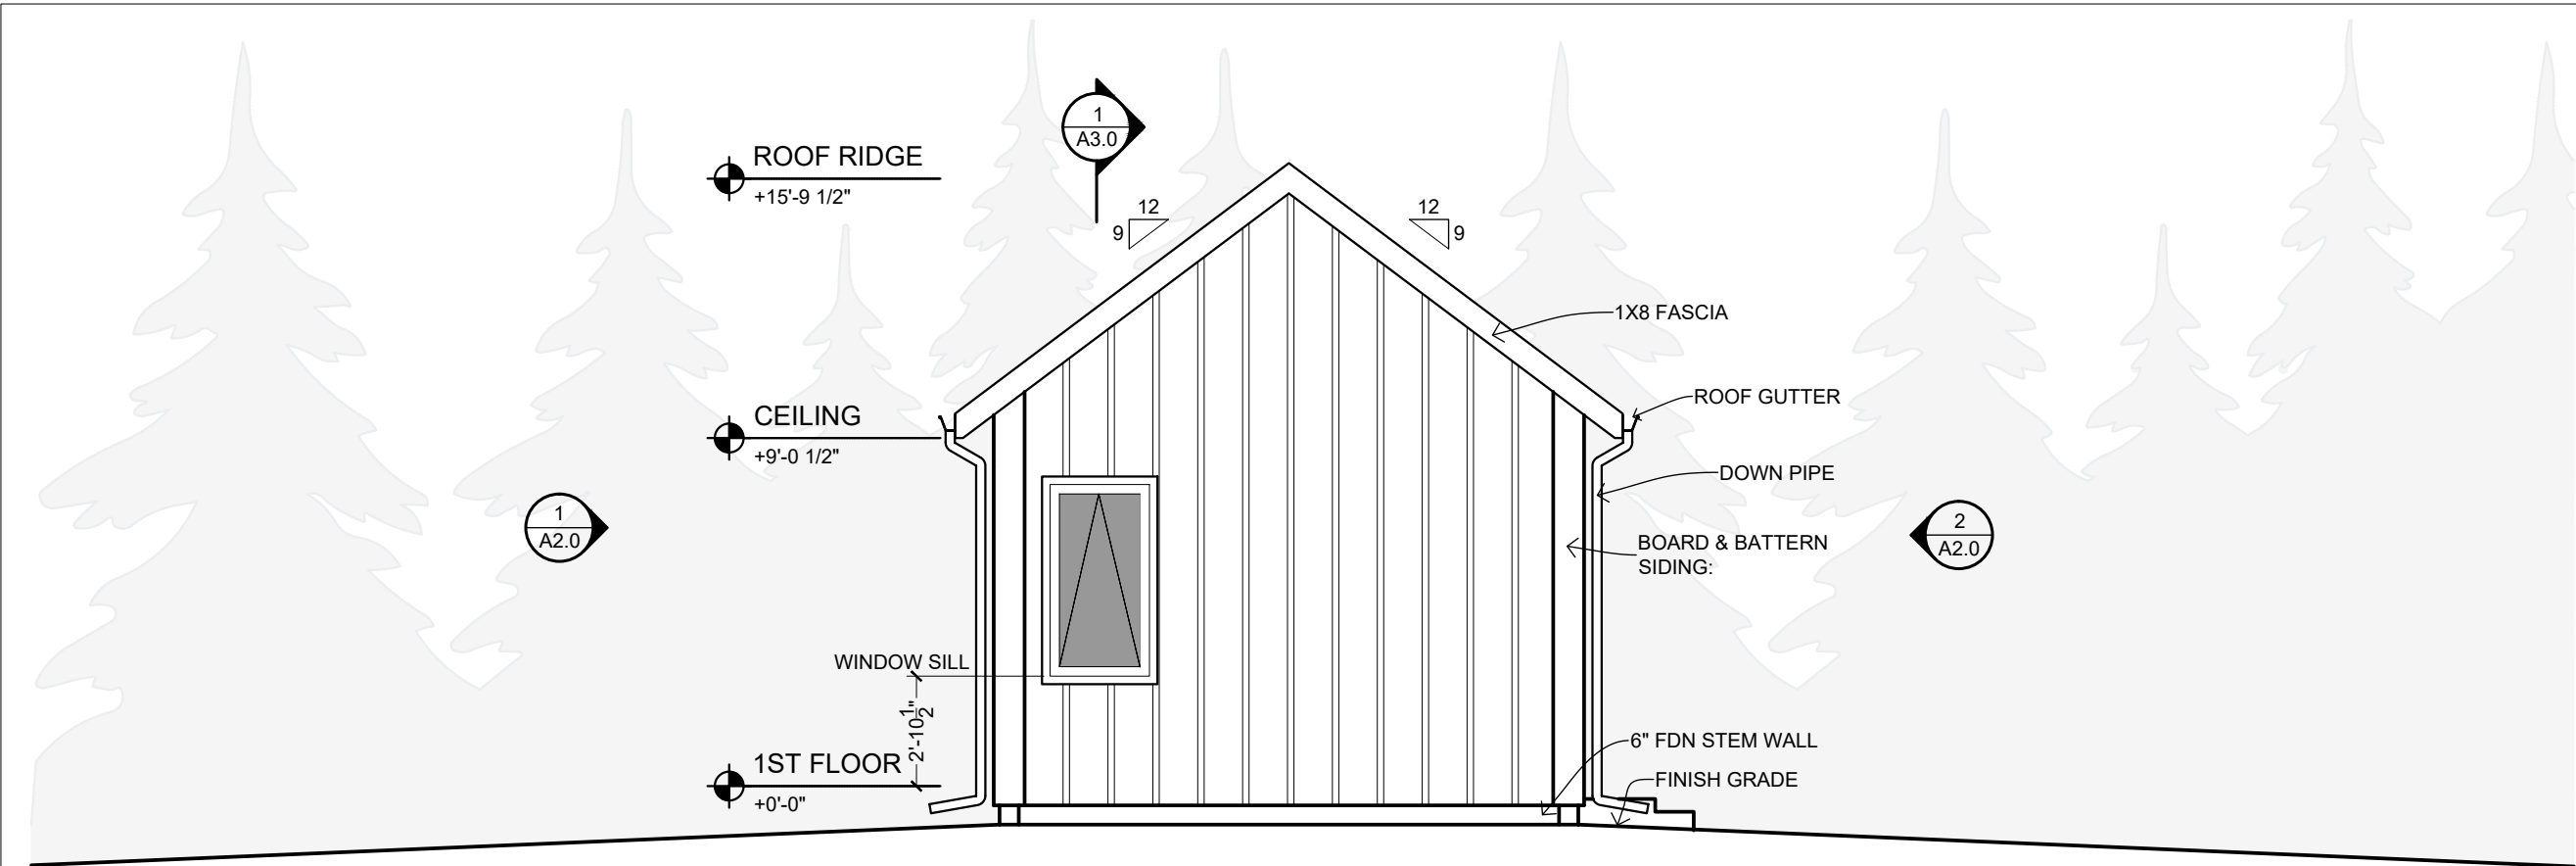

1 SIDE ELEVATION (EAST)

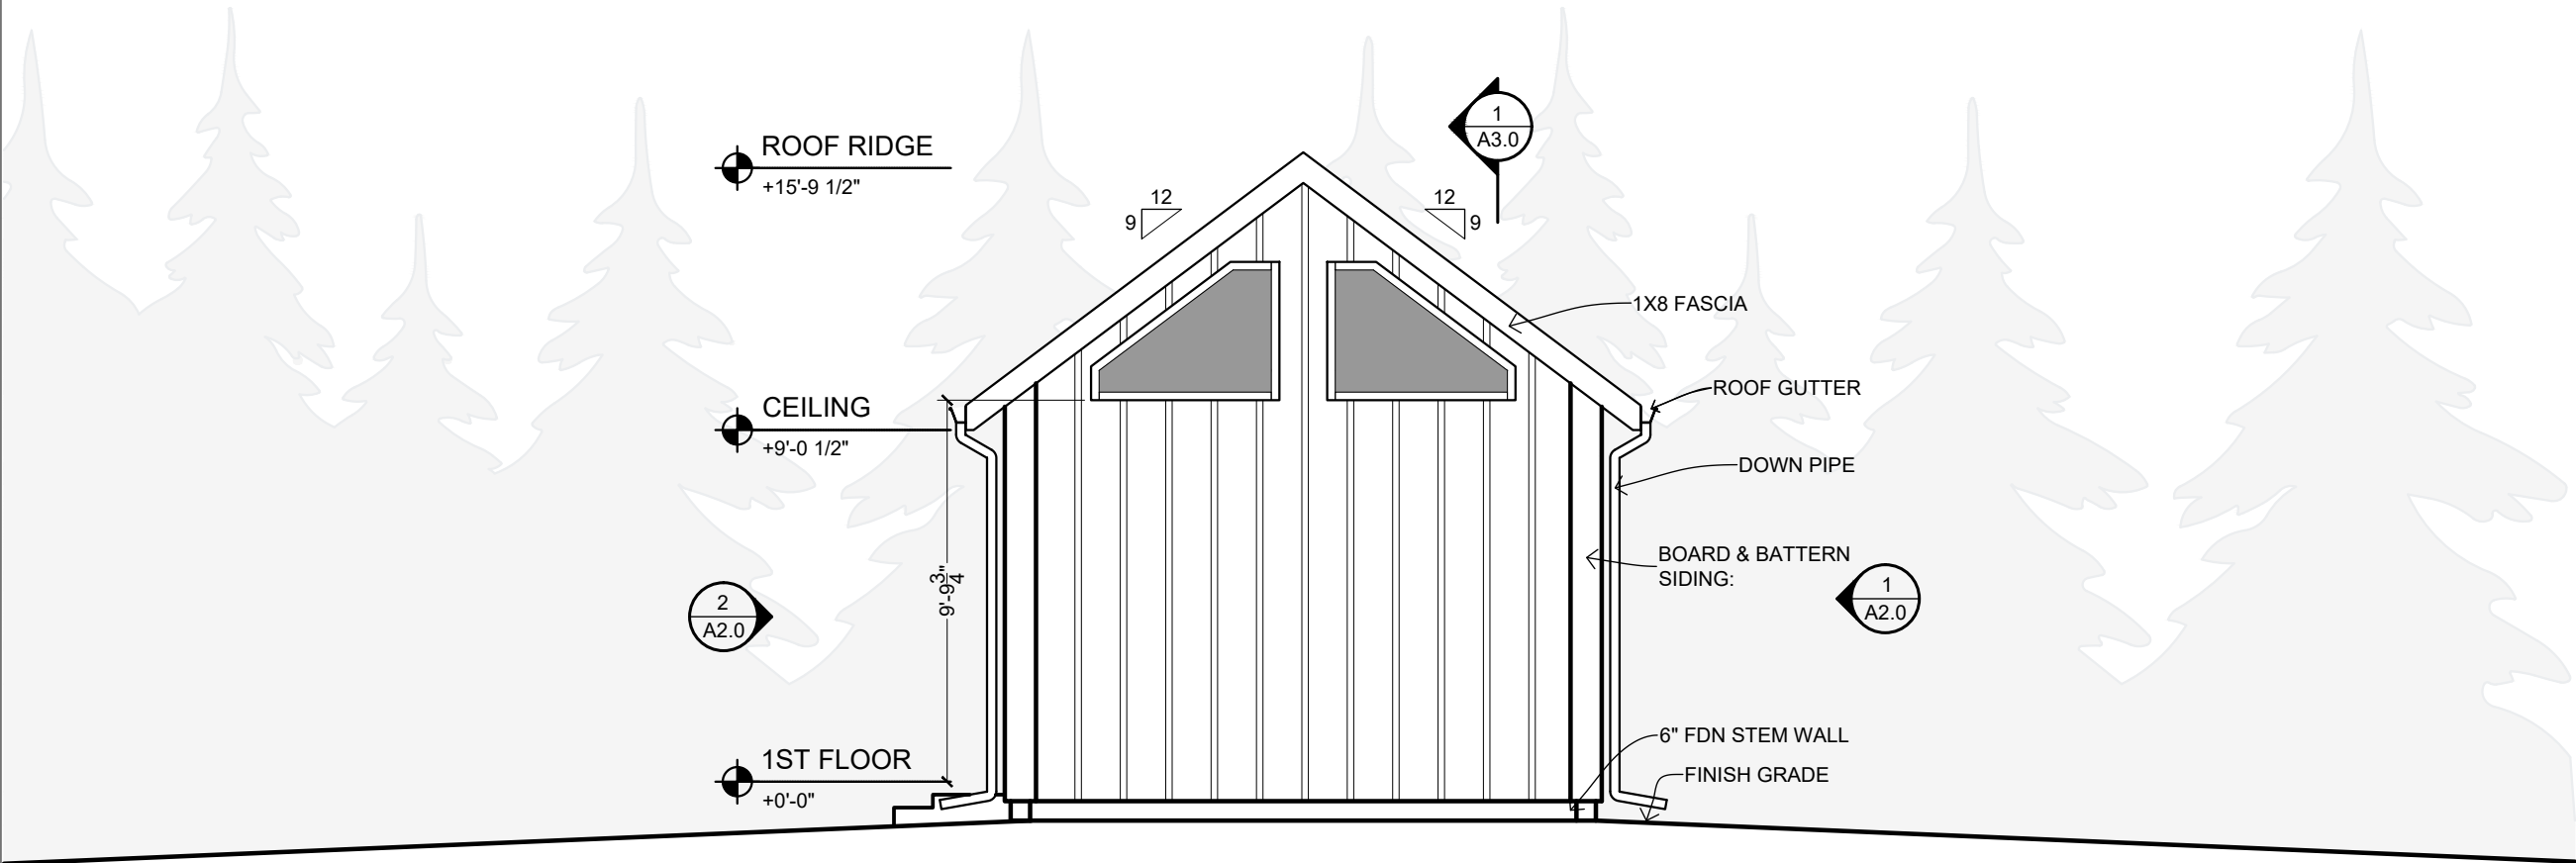

2 SIDE ELEVATION (WEST)

NOTES:

B	Y REVISED	JS	
A	X REVISED	JS	
REV	DESCRIPTION	BY	DATE

AMENDMENTS

ARCHITECT'S CONTACT DETAILS

NAME: VICTOR OMEH

EMAIL: omehvictor@gmail.com

WEBSITE: www.victoromeh.github.io

PROJECT TITLE

ACCESSORY DWELLING UNIT

SITE

1611 MAPLECREST DRIVE,
AUSTIN, TX 78745

CLIENT


DANIEL REYES

SCALE	DATE.	DRAWN BY.
NTS	JUNE 2024	VICTOR OMEH

SHEET NAME	EAST & WEST ELEVATION	SHEET NO.
------------	--------------------------	-----------

PROJECT NO. VO-2024-102

A2.1

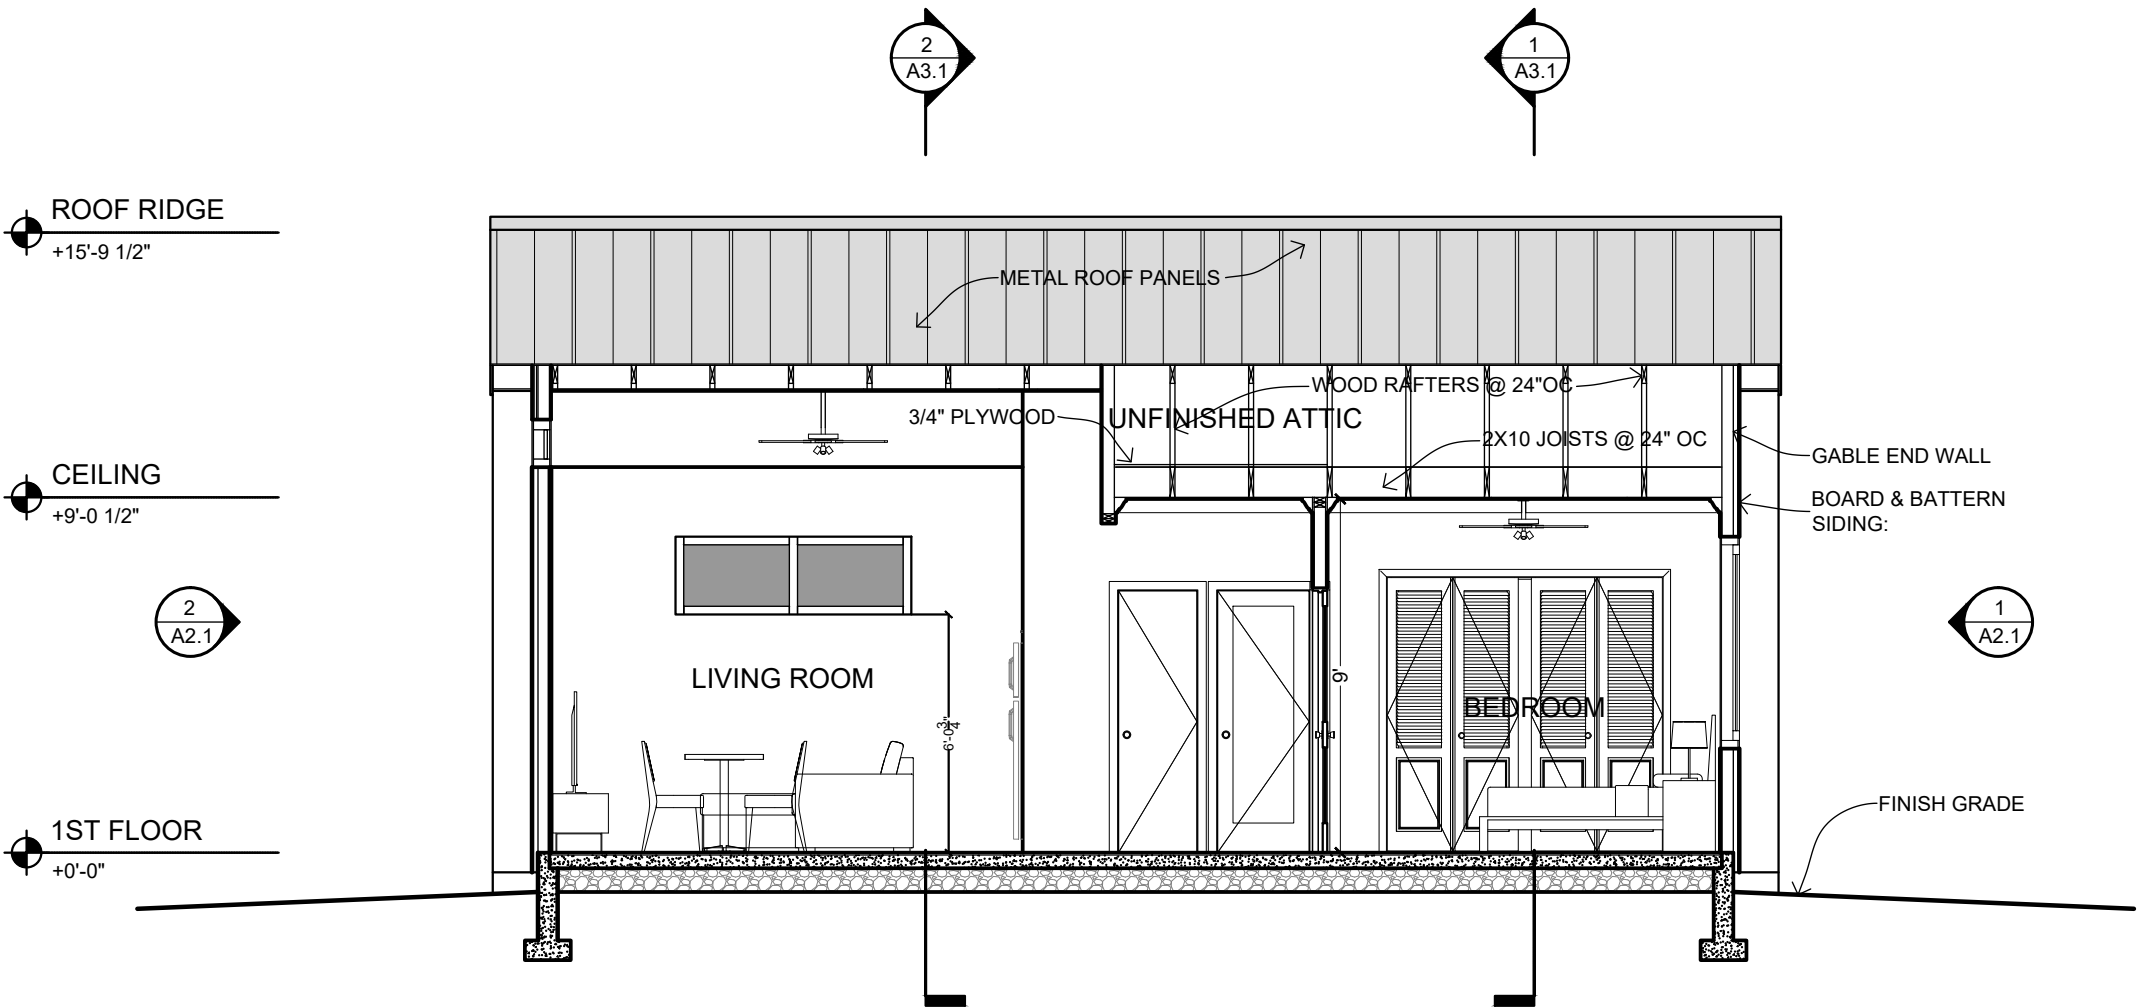

NOTES:

B	Y REVISED	JS	
A	X REVISED	JS	
REV	DESCRIPTION	BY	DATE

AMENDMENTS

ARCHITECT'S CONTACT DETAILS

NAME: VICTOR OMEH

EMAIL: omehvictor@gmail.com

WEBSITE: www.victoromeh.github.io

PROJECT TITLE

ACCESSORY DWELLING UNIT

SITE


1611 MAPLECREST DRIVE,
AUSTIN, TX 78745

CLIENT


DANIEL REYES

SCALE	DATE	DRAWN BY.
NTS	JUNE 2024	VICTOR OMEH

SHEET NAME	LONGITUDINAL SECTION	SHEET NO.
PROJECT NO.	VO-2024-102	A3.0

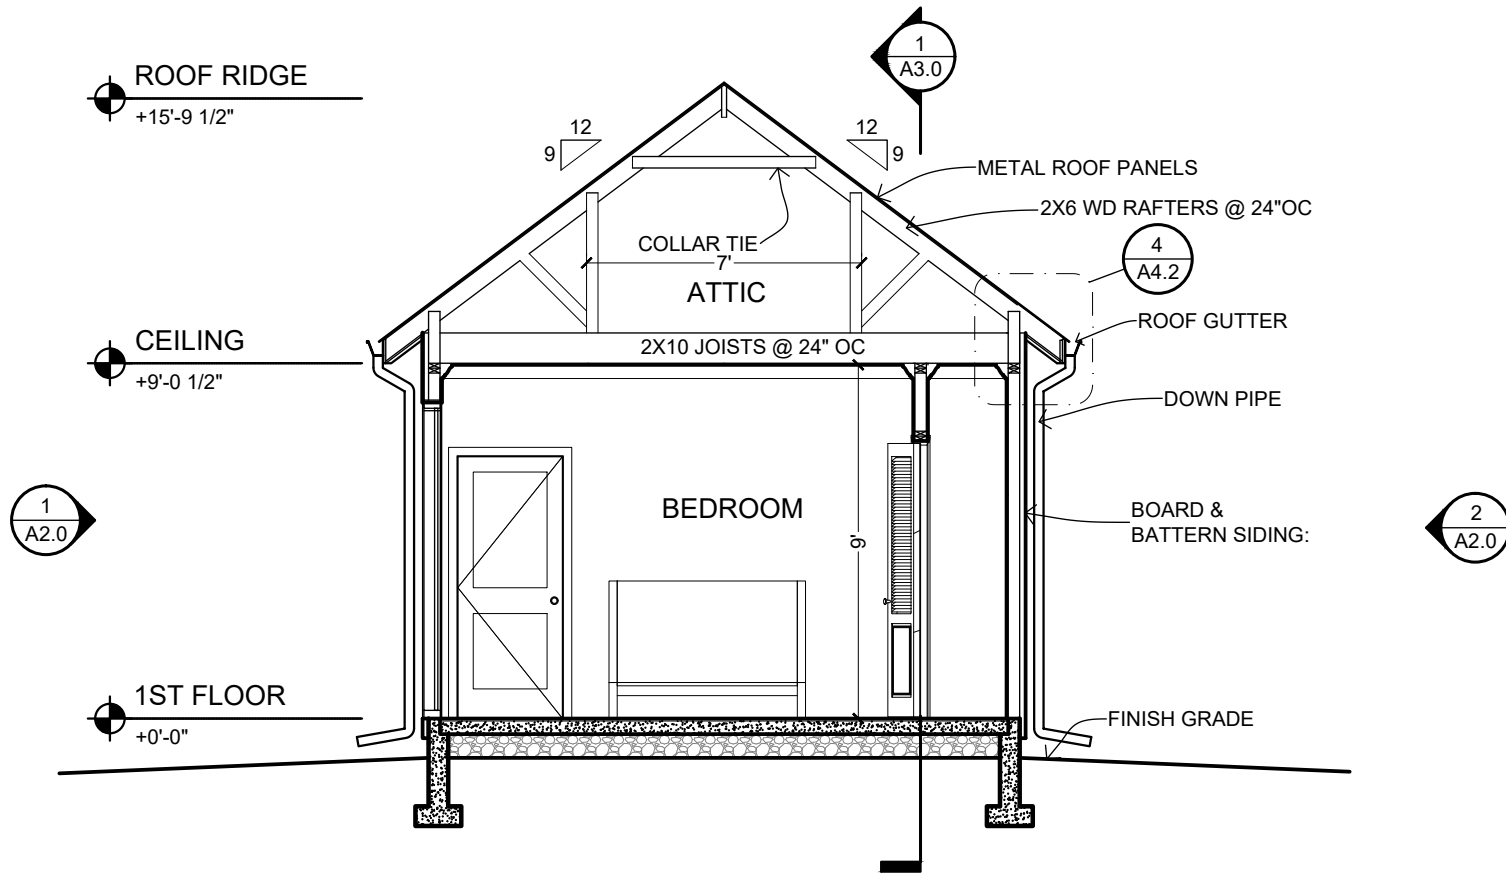

1 TRANSVERSE SECTION

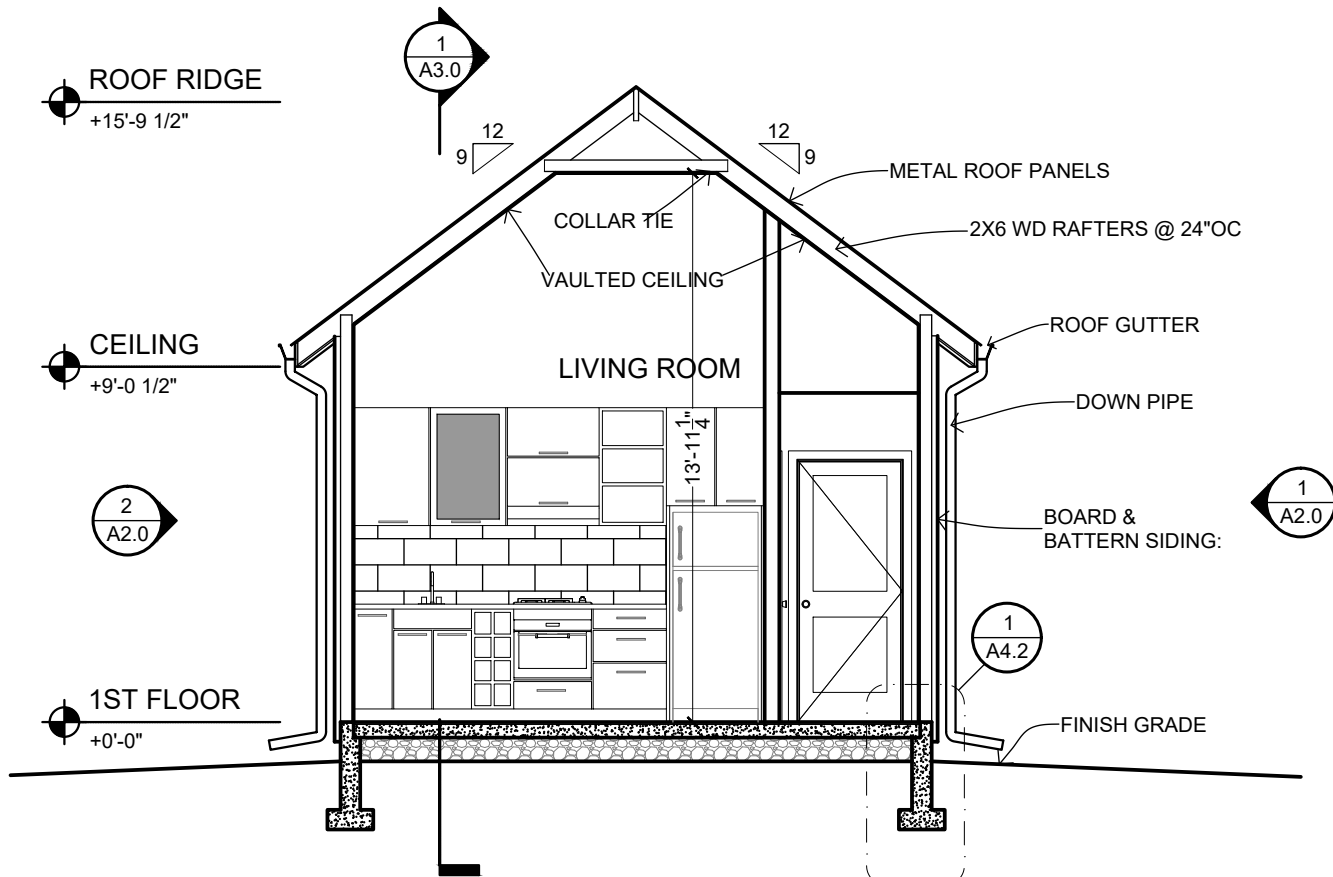

2 TRANSVERSE SECTION 2

NOTES:

B	Y REVISED	JS	
A	X REVISED	JS	
REV	DESCRIPTION	BY	DATE

AMENDMENTS

ARCHITECT'S CONTACT DETAILS

NAME:

EMAIL:

WEBSITE:

PROJECT TITLE

ACCESSORY DWELLING UNIT

SITE


1611 MAPLECREST DRIVE,
AUSTIN, TX 78745

CLIENT


DANIEL REYES

SCALE	DATE	DRAWN BY.
NTS	JUNE 2024	

SHEET NAME	TRANSVERSE SECTIONS	SHEET NO.
PROJECT NO.	VO-2024-102	A3.1

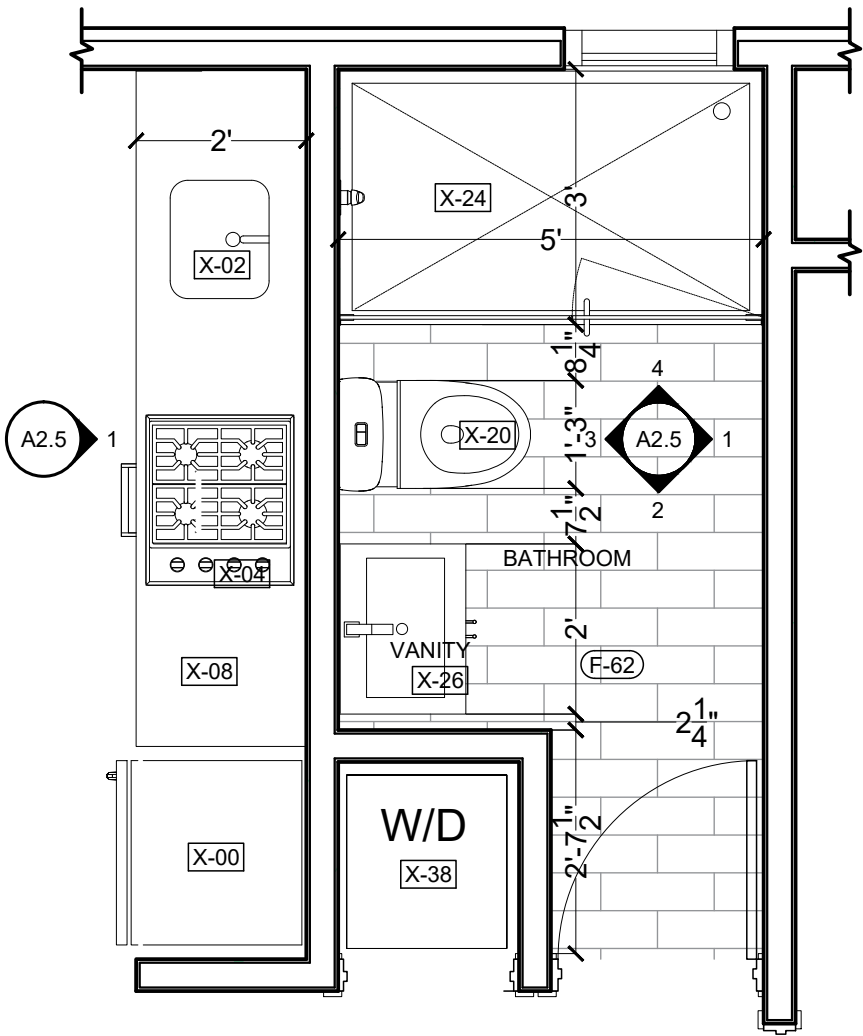

1 KITCHENETTE/ BATHROOM FLOOR PLAN DETAIL

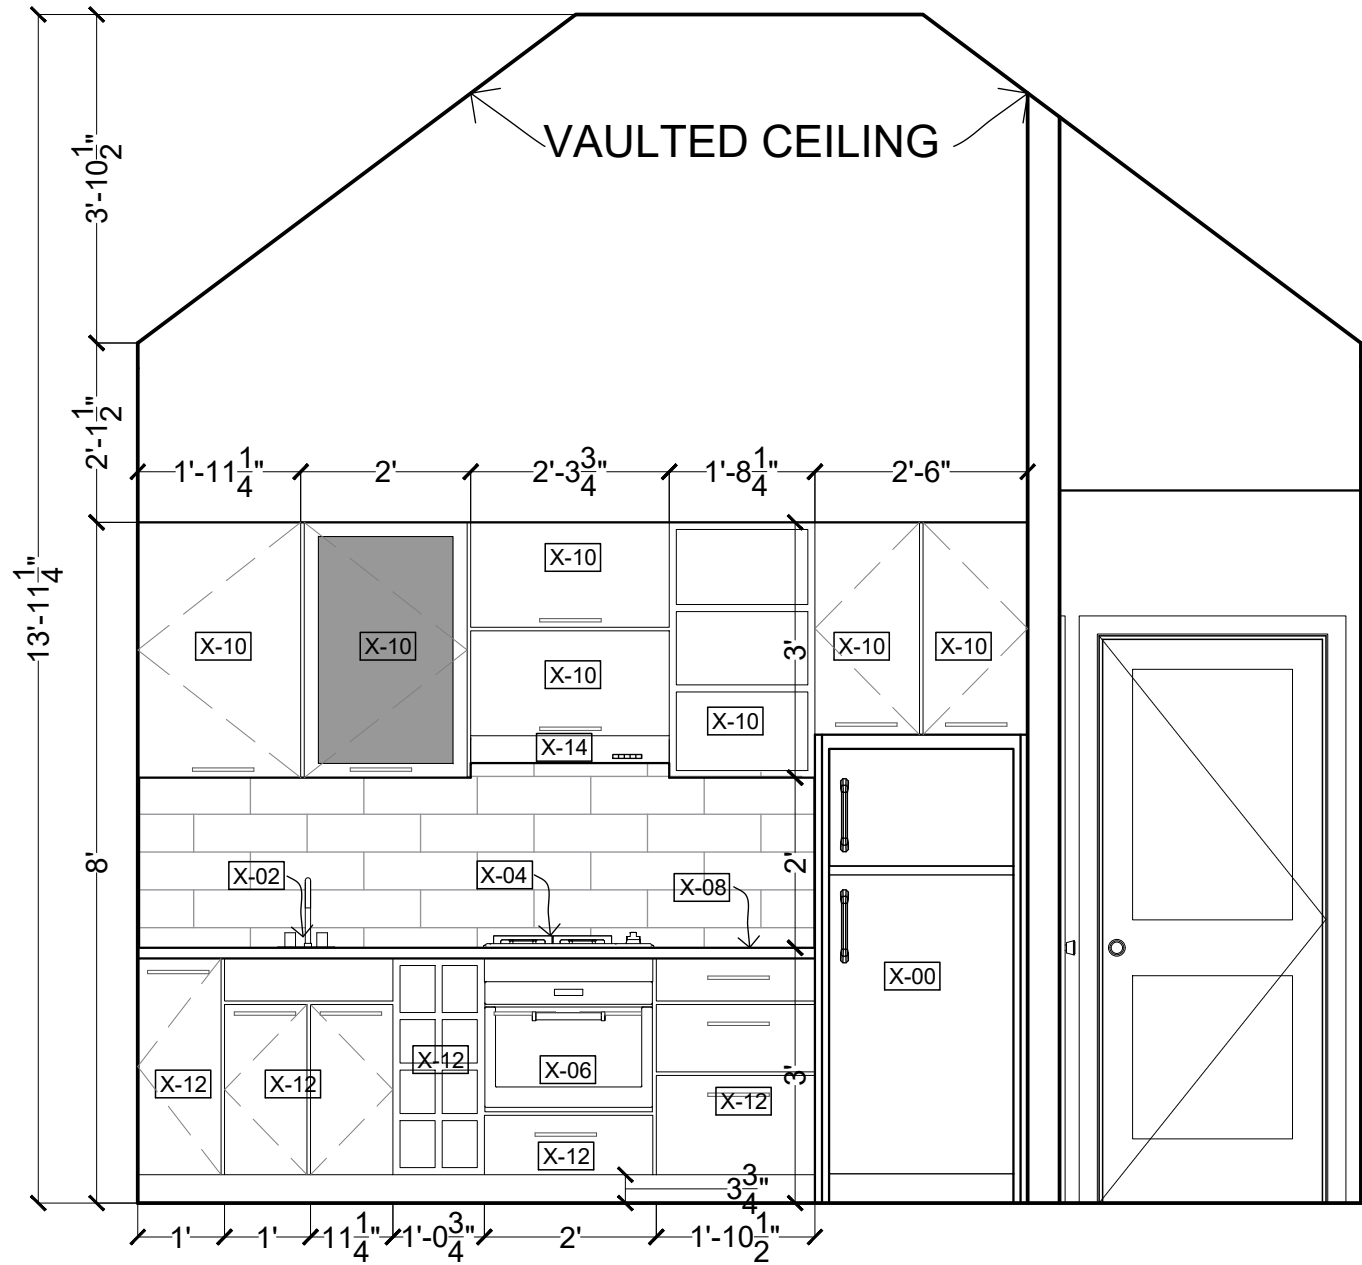

2 KITCHENETTE ELEVATION

- KEY NOTES
- FIXTURES
(SEE SCHEDULE ON A5.0)
- X-00 REFRIDGERATOR
 - X-02 KITCHEN SINK
 - X-04 STOVE
 - X-06 OVEN
 - X-08 COUNTERTOP
 - X-10 WALL CABINETS
 - X-12 FLOOR CABINETS
 - X-14 EXHAUST HOOD
 - X-20 WC TOILET
 - X-22 VANITY
 - X-24 SHOWER TRAY
 - X-26 MIRROR
 - X-28 SHOWER HEAD
 - X-30 SHOWER SWITCH
 - X-32 SHOWER DOOR
 - X-34 SHOWER GLASS
 - X-36 LIGHTS
 - X-40 WASHER/ DRYER
 - X-42 WATER HEATER
 - X-44 CEILING FAN

NOTES:

B	Y REVISED	JS	
A	X REVISED	JS	
REV	DESCRIPTION	BY	DATE

AMENDMENTS

ARCHITECT'S CONTACT DETAILS

NAME: VICTOR OMEH
EMAIL: omehvictor@gmail.com
WEBSITE: www.victoromeh.github.io

PROJECT TITLE

ACCESSORY DWELLING UNIT

SITE


1611 MAPLECREST DRIVE,
AUSTIN, TX 78745

CLIENT


DANIEL REYES

SCALE	DATE	DRAWN BY.
NTS	JUNE 2024	VICTOR OMEH

SHEET NAME	DETAIL PLAN/ ELEVATIONS	SHEET NO.
PROJECT NO.	VO-2024-102	A4.0

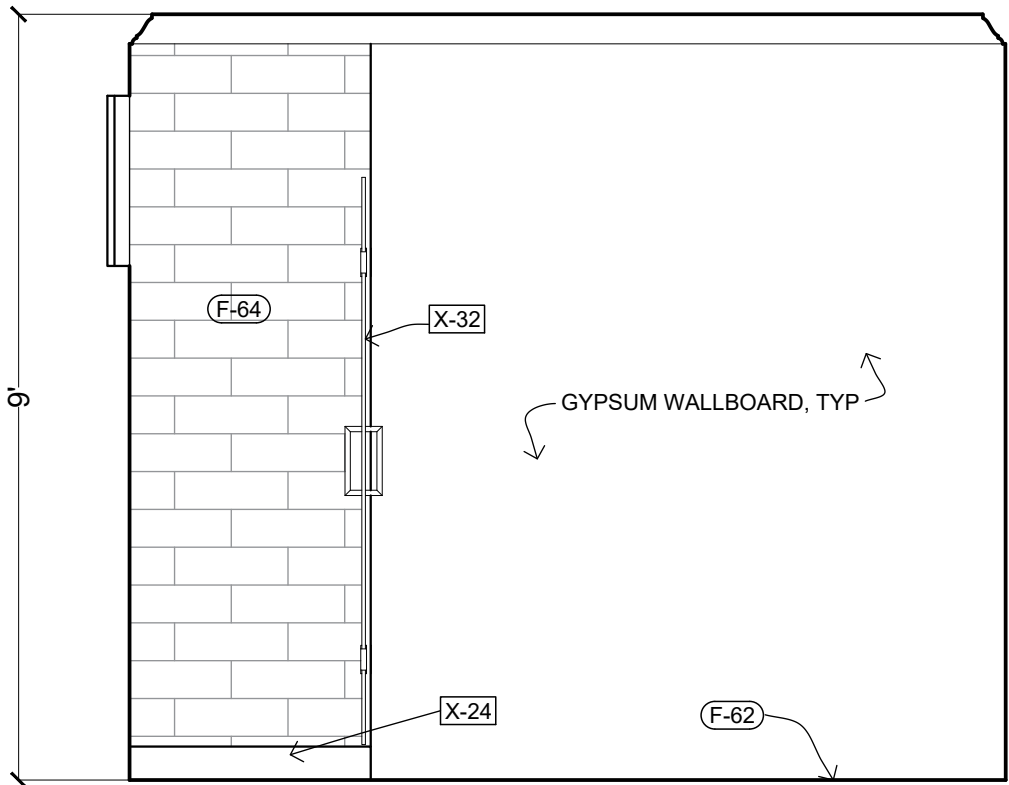

1 BATHROOM ELEVATION

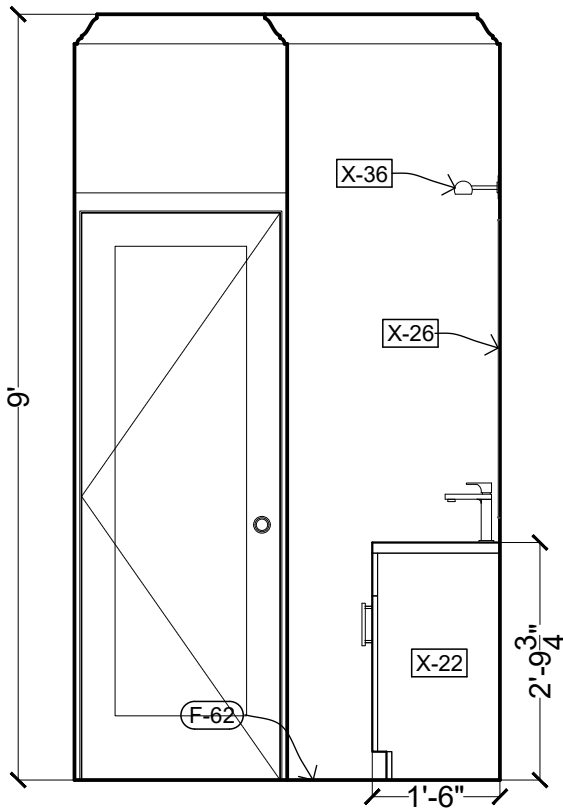


2 BATHROOM ELEVATION


KEY NOTES

FIXTURES
(SEE SCHEDULE ON A5.0)

- X-20 WC TOILET
- X-22 VANITY
- X-24 SHOWER TRAY
- X-26 MIRROR
- X-28 SHOWER HEAD
- X-30 SHOWER SWITCH
- X-32 SHOWER DOOR
- X-34 SHOWER GLASS
- X-36 LIGHTS

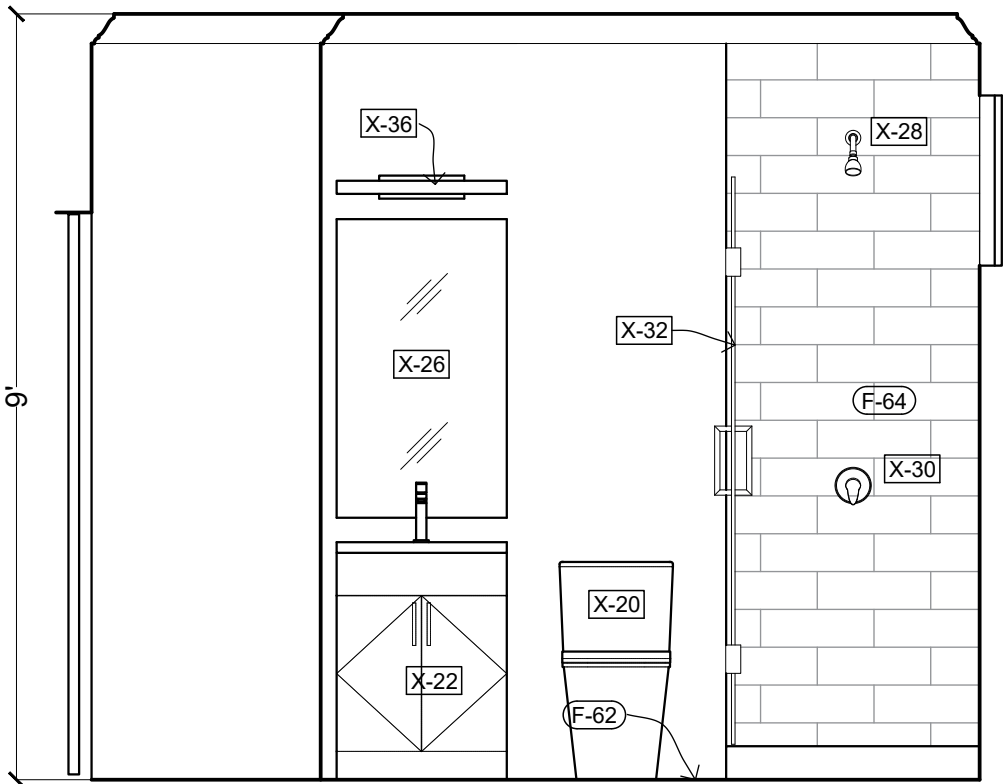

3 BATHROOM ELEVATION

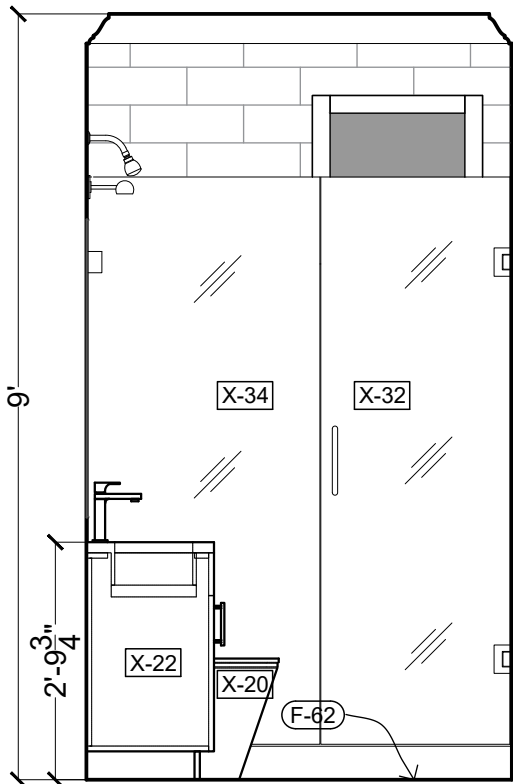

4 BATHROOM ELEVATION

NOTES:

B	Y REVISED	JS	
A	X REVISED	JS	
REV	DESCRIPTION	BY	DATE

AMENDMENTS

ARCHITECT'S CONTACT DETAILS

NAME: VICTOR OMEH
EMAIL: omehvictor@gmail.com
WEBSITE: www.victoromeh.github.io

PROJECT TITLE

ACCESSORY DWELLING UNIT

SITE


1611 MAPLECREST DRIVE,
AUSTIN, TX 78745

CLIENT


DANIEL REYES

SCALE	DATE.	DRAWN BY.
NTS	JUNE 2024	VICTOR OMEH


SHEET NAME	INTERIOR ELEVATIONS	SHEET NO.
PROJECT NO.	VO-2024-102	A4.1

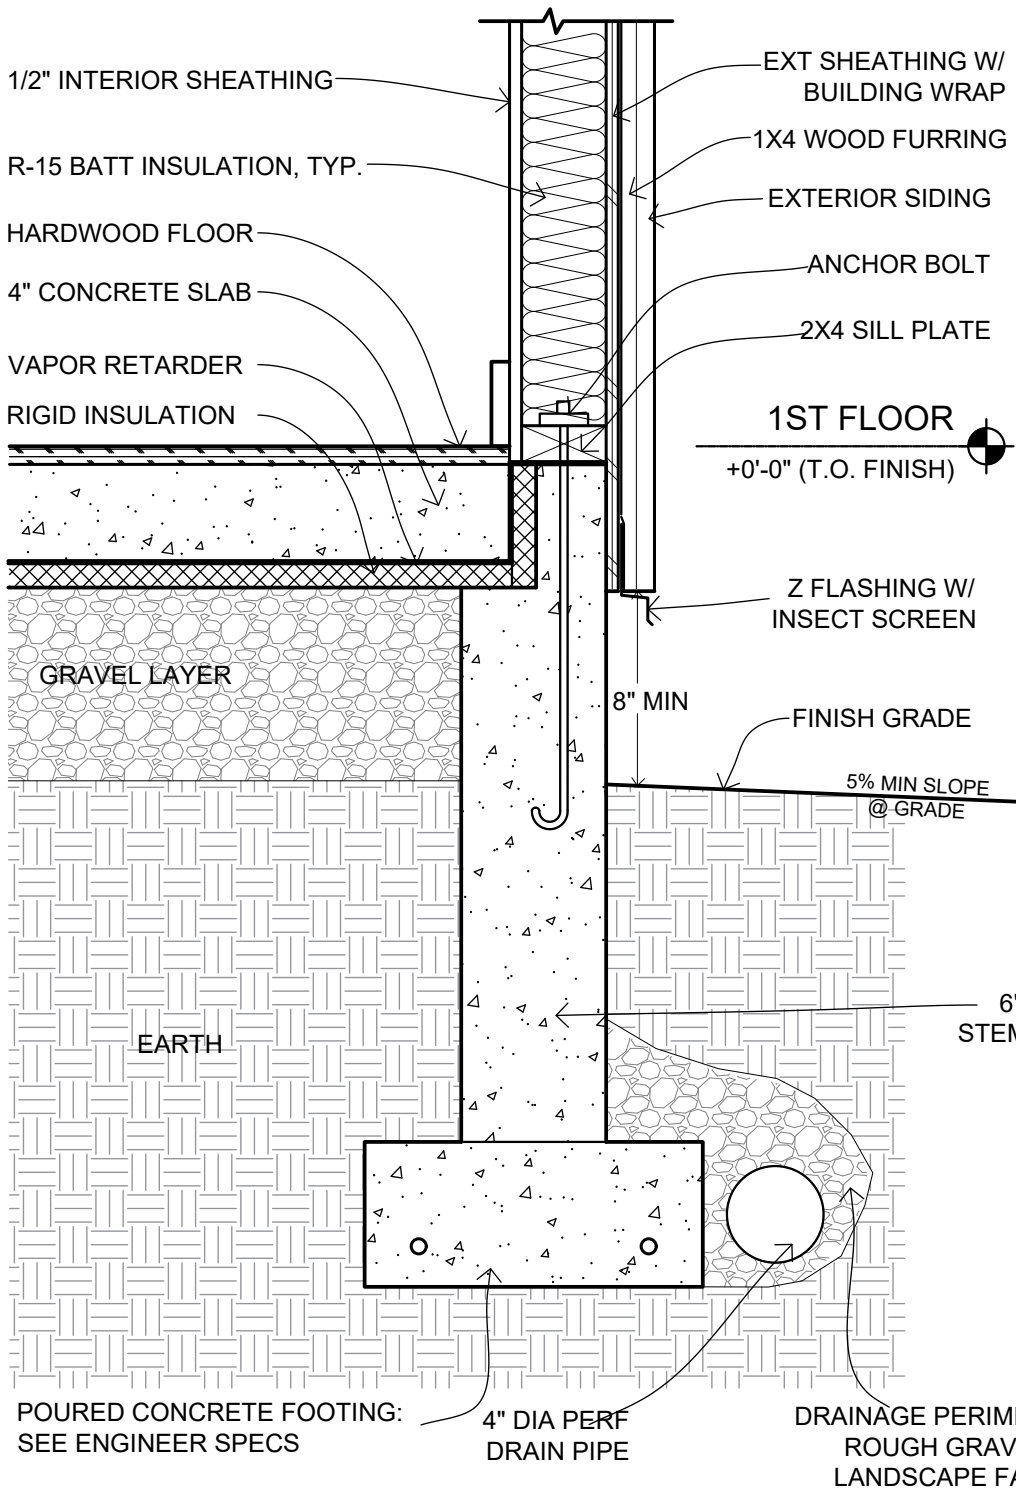


1 FONDATION WALL SECTION

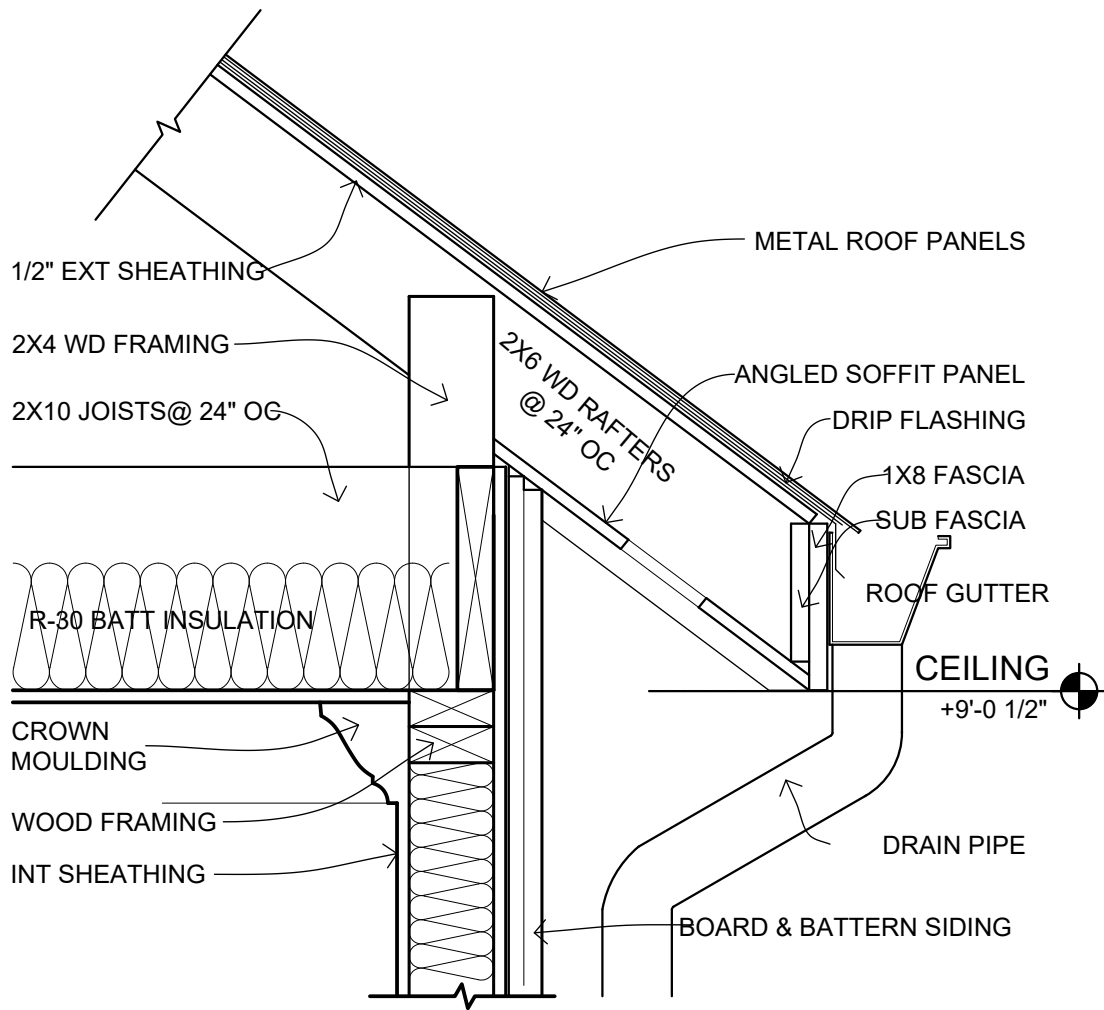


2 ROOF EAVE SECTION

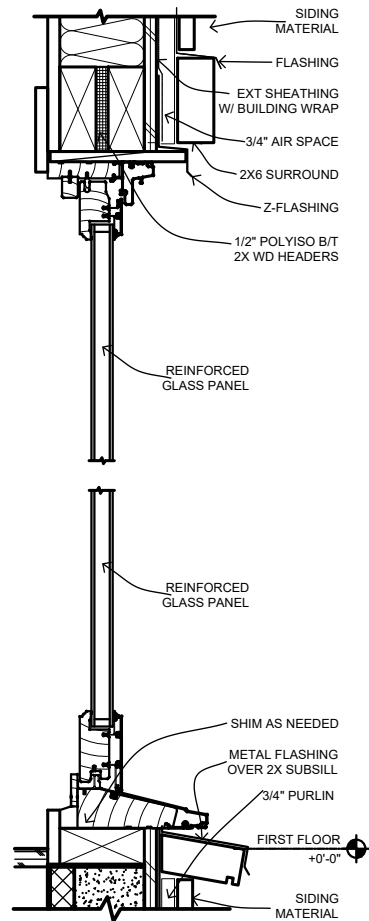

3 TYPICAL CURTAIN WALL

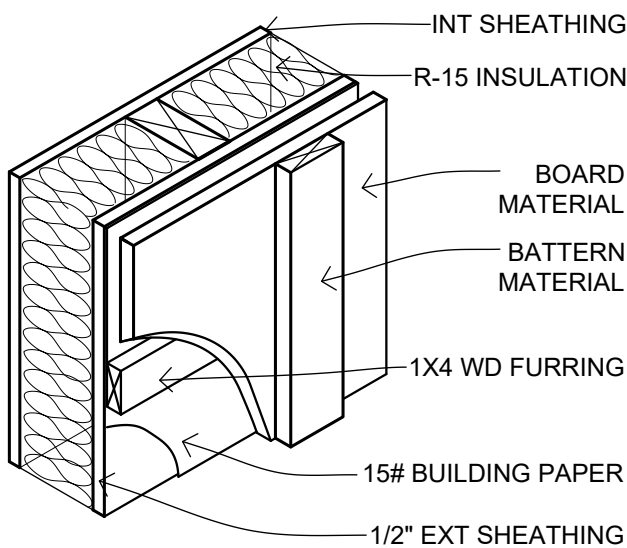

1 TYPICAL EXTERIOR WALL

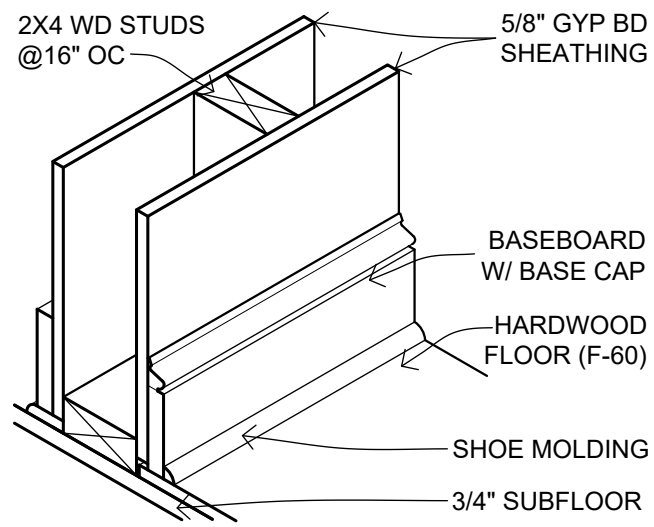

2 TYPICAL INTERIOR WALL

NOTES:

B	Y REVISED	JS	
A	X REVISED	JS	
REV	DESCRIPTION	BY	DATE

AMENDMENTS

ARCHITECT'S CONTACT DETAILS

NAME: VICTOR OMEH

EMAIL: omehvictor@gmail.com

WEBSITE: www.victoromeh.github.io

PROJECT TITLE

ACCESSORY DWELLING UNIT

SITE


1611 MAPLECREST DRIVE,
AUSTIN, TX 78745

CLIENT


DANIEL REYES

SCALE	DATE	DRAWN BY
NTS	JUNE 2024	VICTOR OMEH


SHEET NAME	DETAILS	SHEET NO.
PROJECT NO.	VO-2024-102	A4.2

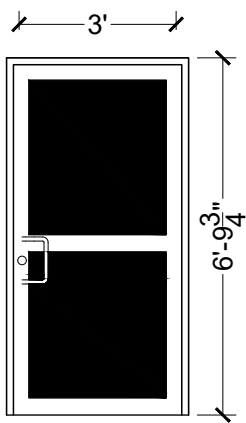


D1 FRONT DOOR

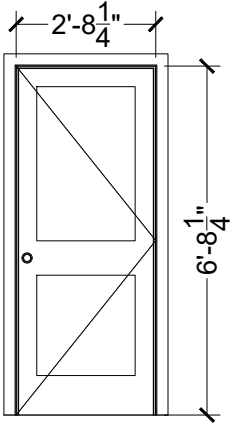


D3 BEDROOM DOOR

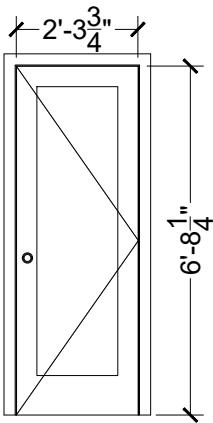

D4 BATHROOM DOOR

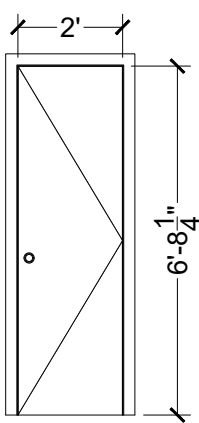


D4 W/D DOOR

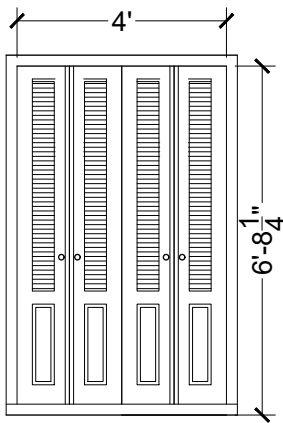


D5 CLOSET DOOR


1 DOOR ELEVATION DETAILS

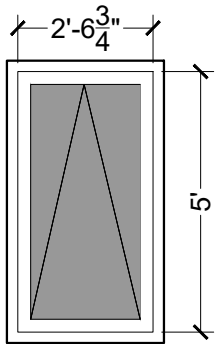

1 31" X 60"

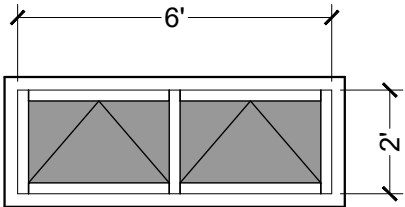

2 72" X 24"

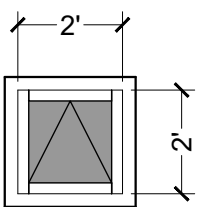

3 24" X 24"

6 WINDOW ELEVATION DETAILS

DOOR SCHEDULE

MARK	SIZE	MATERIAL	TYPE	NOTE	MAKE / MODEL
D1	36"x82"	ALUMINUM/GLASS	GLAZED, PANELLED	3/3 LITES	MARVIN / CLAD ULTIMATE
D2	32"x80"	WOOD	2-PANEL	2/2 LITES	MARVIN / CLAD ULTIMATE
D3	28"x80"	WOOD	1-PANEL	SOLID WOOD	ANTIQUE PREFERRED
D4	24"x80"	WOOD	1-PANEL	SOLID WOOD	ANTIQUE PREFERRED
D5	48"x80"	WOOD	2-PANEL	SOLID WOOD	ANTIQUE PREFERRED

WINDOW SCHEDULE

MARK	SIZE	MATERIAL	TYPE	NOTE	MAKE / MODEL
1	31"x60"	COMPOSITE	AWNING	2/2 LITES	MARVIN / ULTIMATE DH
2	72"x24"	COMPOSITE	AWNING	2/2 LITES	MARVIN / ULTIMATE DH
3	24"x24"	COMPOSITE	AWNING	2/2 LITES	MARVIN / ULTIMATE DH

FOR RELATED TRIM AND ACCESSORIES: SEE FINISHES SCHEDULE A5.1

ABBREVIATIONS

#	POUNDS OR NUMBER	INT	INTERIOR
AC	AIR CONDITIONING	MAX	MAXIMUM
B.O.	BOTTOM OF	MIN	MINIMUM
B/T	BETWEEN	(N)	NEW
BD	BOARD	NTS	NOT TO SCALE
BM	BEAM	OC	ON CENTER
CLG	CEILING	PERF	PERFORATED
CLR	CLEAR	PT	PRESSURE-TREATED
CMU	CONC MASONRY UNIT	QTY	QUANTITY
CONC	CONCRETE	R	RADIUS OR RISER
CONT	CONTINUOUS	RCP	REFLECTED CEILING
D	DRYER		PLAN
DEMO	DEMOLISH	REF	REFRIGERATOR
DIA	DIAMETER	SD	SMOKE DETECTOR
DIM	DIMENSION	SF	SQUARE FEET
DM	DIMMER	SPEC	SPECIFICATION
DN	DOWN	SYM	SYMMETRICAL
DW	DISHWASHER	T.O.	TOP OF
(E)	EXISTING	T&G	TONGUE & GROOVE
EL	ELEVATION	TYP	TYPICAL
ELEC	ELECTRICAL	W	WASHER OR WATT
EQ	EQUAL	W/	WITH
EXT	EXTERIOR	W/D	WASHER & DRYER
FIN	FINISH	W/O	WITHOUT
FT	FOOT	WC	WATER CLOSET
GALV	GALVANIZED	WD	WOOD
GFCI	CIRCUIT INTERRUPTER	WH	WATER HEATER
GYP	GYP SUM	WP	WEATHERPROOF

NOTES:

B	Y REVISED	JS	
A	X REVISED	JS	
REV	DESCRIPTION	BY	DATE

AMENDMENTS

ARCHITECT'S CONTACT DETAILS

NAME:	VICTOR OMEH
EMAIL:	omehvictor@gmail.com
WEBSITE:	www.victoromeh.github.io

PROJECT TITLE

ACCESSORY DWELLING UNIT

SITE

1611 MAPLECREST DRIVE,
AUSTIN, TX 78745

CLIENT

DANIEL REYES

SCALE	DATE	DRAWN BY
NTS	JUNE 2024	VICTOR OMEH

SHEET NAME	DOORS & WINDOWS	SHEET NO.
PROJECT NO.	VO-2024-102	A5.0

FIXTURE & EQUIPMENT SCHEDULE					NOTES:				
MARK	ITEM	SIZE	NOTES	MANUFACTURER / MODEL					
X-00	REFRIGERATOR	26x26x64"	ENERGY STAR	BLOMBERG / BRFB1042SS					
X-02	KITCHEN SINK	14"x16.5"	UNDERMOUNT SINGLE BOWL, VITREOUS CHINA	HIGHPOINT COLLECTION / FIRECLAY					
X-04	STOVE	24"x21"	-	-					
X-06	OVEN	19"x24"x36"	-	-					
X-08	KITCHEN COUNTERTOP	1.5-2" THICK	WHITE PORCELEIN TILE OVER COMPOSITE BOARD, WITH ROUNDED EDGES	-					
X-10	WALL CABINETS	12" WIDE	PAINTED, GLAZED DOORS PREFERRED	IKEA / SEKTION					
X-12	FLOOR CABINETS	12", 24" WIDE	INCLUDES (3) 12" WALL UNITS AS FLOOR CABINETS WITH OPEN SHELVES	IKEA / SEKTION					
X-14	EXHAUST HOOD	18"x28"x24"	-	-					
X-20	WC TOILET	2' MAX LENGTH	1.6 GPF, SIZE IS CRITICAL FOR PROPER CLEARANCES	AQUIA / WALL HUNG DUAL FLUSH TOILET CT418F					
X-22	BATHROOM VANITY	24"x18"x34"	CENTERED WITH MIRROR	-					
X-24	SHOWER TRAY	36"x60"x5"	INSTALL LOW-FLOW SHOWER HEAD	KOHLER / STERLING 71091120 OR EQUIVALENT					
X-26	MIRROR	24"x42"		-					
X-28	SHOWER HEAD	-		-					
X-30	SHOWER SWITCH	-		-					
X-32	SHOWER GLASS DOOR	27"x80"x1"	TOUGHENED TEMPERED GLASS	-					
X-34	SHOWER GLASS WALL	33"x80"x1"	TOUGHENED TEMPERED GLASS	-					
X-36	MIRROR LIGHTS	-	-	-					
X-40	WASHER / DRYER COMBO	20"x34"x23"	VENTLESS, ENERGY STAR PREFERRED	HAIER / HWD1600BW					
X-42	WATER HEATER	8"x7"x3"	INSTANT, TANKLESS	STIEBEL / ELTRON MINI					
X-44	INTERIOR CEILING FAN	48" DIA MAX	INCLUDES LIGHTING	-					
MATERIALS SCHEDULE									
MARK	ITEM	SIZE	MATERIAL	NOTES	MANUFACTURER / MODEL				
F-62	FLOOR TILE	16"X5"	CERAMIC	HEXAGONAL PATTERN	-				
F-64	WALL TILE	16"X5"	CERAMIC	WHITE OR LIGHT BLUE					
	BOARD SIDING	3/4" THICK	FIBER CEMENT	JAMES HARDIE / ARTISAN LAP SIDING	-				
	BATTERN SIDING	1"X2"	FIBER CEMENT	JAMES HARDIE / ARTISAN LAP SIDING	-				
	EXT OPENING CASING	5-6"	FIBER CEMENT	.75" THICK HARDIPLANK	-				
	BED MOLDING	2.5"	ROT-RESISTANT	PAINTED	-				
	CROWN MOLDING	3"	ROT-RESISTANT	PAINTED	-				
	METAL ROOF PANELS	24"OC	GALVALUME	OPTIONAL: STANDING SEAM METAL ROOF PANELS	-				
	BULBED RIDGE CAP	4"	GALVALUME	USE SAME SUPPLIER AND PRODUCT LINE AS 5V PANELS	-				
	ROOF GUTTER	3 1/2" DIA	GALV STEEL OR COPPER	DOWNSPOUTS TO FOLLOW CORNER BOARDS	-				
	DRAIN PIPE	2 1/2" DIA	GALV STEEL OR COPPER	DOWNSPOUTS TO FOLLOW CORNER BOARDS	-				
FOR WINDOW & DOOR SCHEDULES: SEE SHEET A5.0 PREFERENCE SHALL BE GIVEN TO LOCALLY PRODUCED									
				B		Y REVISED		JS	
				A		X REVISED		JS	
REV		DESCRIPTION		BY		DATE			
AMENDMENTS									
ARCHITECT'S CONTACT DETAILS									
NAME:				VICTOR OMEH					
EMAIL:				omehvictor@gmail.com					
WEBSITE:				www.victoromeh.github.io					
PROJECT TITLE									
ACCESSORY DWELLING UNIT									
SITE									
1611 MAPLECREST DRIVE, AUSTIN, TX 78745									
CLIENT									
DANIEL REYES									
SCALE		DATE.		DRAWN BY.					
NTS		JUNE 2024		VICTOR OMEH					
SHEET NAME SCHEDULES								SHEET NO.	
PROJECT NO. VO-2024-102								A5.1	



① 3D VIEW (EXTERIOR)

NOTES:

B	Y REVISED	JS	
A	X REVISED	JS	
REV	DESCRIPTION	BY	DATE

AMENDMENTS

ARCHITECT'S CONTACT DETAILS

NAME: VICTOR OMEH
EMAIL: omehvictor@gmail.com
WEBSITE: www.victoromeh.github.io

PROJECT TITLE

ACCESSORY DWELLING UNIT

SITE

1611 MAPLECREST DRIVE,
AUSTIN, TX 78745

CLIENT

DANIEL REYES

SCALE	DATE	DRAWN BY.
NTS	JUNE 2024	VICTOR OMEH

SHEET NAME	DETAIL PLAN/ ELEVATIONS	SHEET NO.
PROJECT NO.	VO-2024-102	A6.0



1 PERSPECTIVE VIEW (FRONT)

NOTES:

B	Y REVISED	JS	
A	X REVISED	JS	
REV	DESCRIPTION	BY	DATE

AMENDMENTS

ARCHITECT'S CONTACT DETAILS

NAME: VICTOR OMEH
EMAIL: omehvictor@gmail.com
WEBSITE: www.victoromeh.github.io

PROJECT TITLE

ACCESSORY DWELLING UNIT

SITE

1611 MAPLECREST DRIVE,
AUSTIN, TX 78745

CLIENT

DANIEL REYES

SCALE	DATE	DRAWN BY.
NTS	JUNE 2024	VICTOR OMEH

SHEET NAME	DETAIL PLAN/ ELEVATIONS	SHEET NO.
PROJECT NO.	VO-2024-102	A6.1



① PERSPECTIVE VIEW (BACK)

NOTES:

B	Y REVISED	JS	
A	X REVISED	JS	
REV	DESCRIPTION	BY	DATE

AMENDMENTS

ARCHITECT'S CONTACT DETAILS

NAME: VICTOR OMEH
EMAIL: omehvictor@gmail.com
WEBSITE: www.victoromeh.github.io

PROJECT TITLE

ACCESSORY DWELLING UNIT

SITE

1611 MAPLECREST DRIVE,
AUSTIN, TX 78745

CLIENT

DANIEL REYES

SCALE	DATE	DRAWN BY.
NTS	JUNE 2024	VICTOR OMEH

SHEET NAME	DETAIL PLAN/ ELEVATIONS	SHEET NO.
PROJECT NO.	VO-2024-102	A6.2



① 3D VIEW (AXONOMETRIC)

NOTES:

B	Y REVISED	JS	
A	X REVISED	JS	
REV	DESCRIPTION	BY	DATE

AMENDMENTS

ARCHITECT'S CONTACT DETAILS

NAME: VICTOR OMEH

EMAIL: omehvictor@gmail.com

WEBSITE: www.victoromeh.github.io

PROJECT TITLE

ACCESSORY DWELLING UNIT

SITE

1611 MAPLECREST DRIVE,
AUSTIN, TX 78745

CLIENT

DANIEL REYES

SCALE	DATE	DRAWN BY.
NTS	JUNE 2024	VICTOR OMEH

SHEET NAME	DETAIL PLAN/ ELEVATIONS	SHEET NO.
------------	----------------------------	-----------

PROJECT NO. VO-2024-102

A6.3



① 3D VIEW (KITCHEN)

NOTES:

B	Y REVISED	JS	
A	X REVISED	JS	
REV	DESCRIPTION	BY	DATE

AMENDMENTS

ARCHITECT'S CONTACT DETAILS

NAME: VICTOR OMEH
EMAIL: omehvictor@gmail.com
WEBSITE: www.victoromeh.github.io

PROJECT TITLE

ACCESSORY DWELLING UNIT

SITE

1611 MAPLECREST DRIVE,
AUSTIN, TX 78745

CLIENT

DANIEL REYES

SCALE	DATE	DRAWN BY.
NTS	JUNE 2024	VICTOR OMEH

SHEET NAME	DETAIL PLAN/ ELEVATIONS	SHEET NO.
PROJECT NO.	VO-2024-102	A6.4