

PROJECT TEAM

DESIGNED BY: VICTOR OMEH  
EMAIL: omehvictor@gmail.com  
WEBSITE: https://victoromeh.github.io

CLIENT/ OWNER

THOMAS & RACHEL MERCER

APPLICABLE CODES

INTERNATIONAL RESIDENTIAL CODE (IRC), 2021 EDITION.  
INTERNATIONAL FIRE CODE (IFC), 2021 EDITION.  
INTERNATIONAL PLUMBING CODE (IPC), 2021 EDITION.  
INTERNATIONAL MECHANICAL CODE (IMC), 2021 EDITION.  
INTERNATIONAL FUEL GAS CODE (IFGC), 2021 EDITION.  
NATIONAL ELECTRICAL CODE (NEC), 2023 EDITION.  
INTERNATIONAL ENERGY CONSERVATION CODE (IECC), 2021 EDITION.

VICINITY MAP



PROJECT DATA


PROJECT DESCRIPTION

THREE BEDROOM SINGLE STOREY RESIDENCE

2841 BIRCHWOOD COURT, MURFREESBORO, TN 37129.

**ZONING:** R2-- LOW DENSITY SINGLE FAMILY RESIDENTIAL  
**JURISDICTION:** CITY OF MURFREESBORO  
**BUILDING USE:** SINGLE FAMILY RESIDENCE  
**DENSITY:** 1 DWELLING UNIT/ 13338 SQ FT  
**FRONT SETBACK:** 47FT  
**SIDE SETBACK:** 14 FT  
**REAR SETBACK:** 20 FT  
**MAX BLDG HEIGHT:** 22 FT  
**SITE SQUARE FOOTAGE:** 13338 SQ FT

3D VIEW

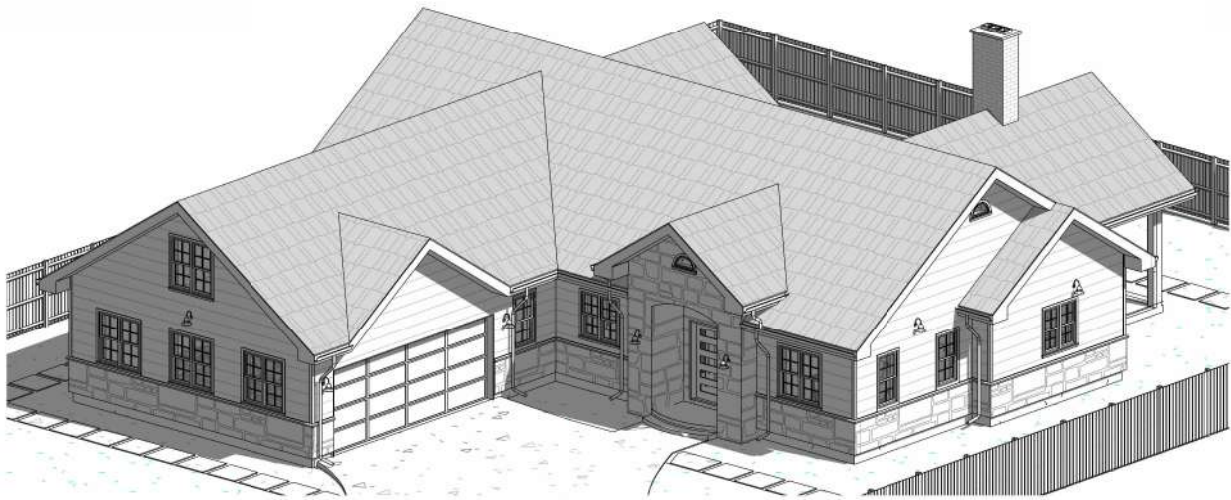

| Sheet List |                              |
|------------|------------------------------|
| Sheet No   | Sheet Name                   |
| A0.0       | COVER PAGE                   |
| A0.1       | GENERAL NOTES                |
| A1.0       | SITE PLAN                    |
| A1.1       | FOUNDATION PLAN              |
| A1.2       | FIRST FLOOR PLAN             |
| A1.3       | ROOF PLAN                    |
| A1.4       | RCP/ ELECTRICAL              |
| A2.0       | SOUTH & NORTH ELEVATION      |
| A2.1       | EAST & WEST ELEVATION        |
| A3.0       | SECTION                      |
| A4.0       | CALLOUT PLANS                |
| A4.1       | INTERIOR ELEVATION(KITCHEN)  |
| A4.2       | INTERIOR ELEVATION(BATHROOM) |
| A5.0       | TYPICAL DETAILS              |
| A5.1       | WALL DETAILS                 |
| A6.0       | DOORS & WINDOWS              |
| A6.1       | SCHEDULES 1                  |
| A6.2       | SCHEDULES 2                  |
| A7.0       | AXONOMETRIC VIEW             |
| A7.1       | EXTERIOR PERSPECTIVE         |
| A7.2       | INTERIOR PERSPECTIVE         |
| A7.3       | 3D VIEW INTERIOR             |
| A7.4       | 3D VIEW                      |

SYMBOLS LEGEND

|  |                  |  |                  |
|--|------------------|--|------------------|
|  | SECTION MARKER   |  | SOIL             |
|  | ELEVATION MARKER |  | CONCRETE         |
|  | INT ELEVATIONS   |  | BRICK            |
|  | DETAIL CALLOUT   |  | CMU BLOCK        |
|  | COMPASS (TRUE)   |  | RIGID INSULATION |
|  | DATUM MARKER     |  | BATT INSULATION  |
|  | WINDOW CALLOUT   |  | FINISH CALLOUT   |
|  | DOOR CALLOUT     |  | CONTOURS (FEET)  |
|  | FIXTURE CALLOUT  |  |                  |


NOTES:

|                                                 |                       |                              |      |
|-------------------------------------------------|-----------------------|------------------------------|------|
| B                                               | Y REVISED             | JS                           |      |
| A                                               | X REVISED             | JS                           |      |
| REV                                             | DESCRIPTION           | BY                           | DATE |
| AMENDMENTS                                      |                       |                              |      |
| ARCHITECT'S CONTACT DETAILS                     |                       |                              |      |
| NAME:                                           |                       | VICTOR O.                    |      |
| EMAIL:                                          |                       | omehvictor@gmail.com         |      |
| WEBSITE:                                        |                       | https://victoromeh.github.io |      |
| PROJECT TITLE                                   |                       |                              |      |
| 3 BEDROOM SINGLE-STORY<br>RESIDENCE WITH ATTIC  |                       |                              |      |
| SITE                                            |                       |                              |      |
| 2841 BIRCHWOOD COURT,<br>MURFREESBORO, TN 37129 |                       |                              |      |
| CLIENT                                          |                       |                              |      |
| THOMAS & RACHEL MERCER                          |                       |                              |      |
| SCALE<br><br>As indicated                       | DATE<br><br>JUNE 2026 | DRAWN BY.<br><br>VICTOR OMEH |      |
| SHEET NAME. COVER PAGE                          |                       | SHEET NO.                    |      |
| PROJECT NO. VO-2026-104                         |                       | A0.0                         |      |

| GENERAL NOTES   |   |      |                   |
|---|---|------|-------------------|
| 1. WORK SHALL CONFORM TO ALL APPLICABLE CODES AND ORDINANCES, INCLUDING BUT NOT LIMITED TO: BUILDING, PLUMBING, ELECTRICAL, AND MECHANICAL CODES.                                                                          | 16. FOOTINGS SHALL EXTEND DOWN BEYOND THE LOCAL FROST LINE.   |      |                   |
| 2. ANY ERRORS, OMISSIONS, OR CONFLICTS FOUND WITHIN THESE DRAWINGS SHALL BE BROUGHT TO THE ATTENTION OF THE OWNER OR THEIR REPRESENTATIVE BEFORE PROCEEDING WITH THE WORK.                                                 | 17. PERFORATED DRAIN PIPES SHALL BE LOCATED WITHIN A GRAVEL PERIMETER AROUND THE FOUNDATION, WITH MULTIPLE DRAINAGE OUTLETS LEADING DOWNSLOPE AWAY FROM THE BUILDING.   |      |                   |
| 3. DO NOT SCALE THESE DRAWINGS. WRITTEN DIMENSIONS TAKE PRECEDENCE OVER MEASUREMENTS.   | 18. FIRE BLOCKING AND FIRE-RATED SHEATHING SHALL BE PROVIDED AS REQUIRED AT CEILINGS, FLOORS, AND ENCLOSED USABLE SPACE UNDER STAIRS.   |      |                   |
| 4. DIMENSIONS ARE TAKEN FROM FACE OF FRAMING LUMBER, FACE OF CONCRETE/ MASONRY, CENTER OF COLUMN, AND CENTERLINE OF FIXTURE, UNLESS NOTED OTHERWISE.                                                                       | 19. ALL WOOD WITHIN 8 INCHES OF THE GROUND SHALL BE PRESSURE TREATED OR COMPRISE A SUITABLY ROT RESISTANT MATERIAL. METAL CONNECTIONS WHICH TOUCH THIS WOOD SHOULD BE GALVANIZED OR STAINLESS STEEL.   |      |                   |
| 5. ALL DIMENSIONS NOTED "VERIFY IN FIELD (V.I.F.)" SHALL BE MEASURED BY THE CONTRACTOR PRIOR TO CONSTRUCTION. REPORT ANY DISCREPANCIES TO THE OWNER OR THEIR REPRESENTATIVE.                                               | 20 PROVIDE ADEQUATE BLOCKING AROUND CABINETRY, PLUMBING FIXTURES, AND OTHER APPLICABLE AREAS.   |      |                   |
| 6. DETAILS SHOWN ARE TYPICAL. SIMILAR DETAILS APPLY IN SIMILAR SITUATIONS.   | 21. PROVIDE MINIMUM R-13 INSULATION IN ALL EXTERIOR WALLS AND R-21 INSULATION AT ROOFS OF CONDITIONED SPACES.   |      |                   |
| 7. IN THE CASE OF DISCREPANCIES WITHIN DESCRIPTIONS OF SIMILAR ITEMS, PRECEDENCE SHALL BE GIVEN TO NOTES & DRAWINGS OF GREATER DETAIL.                                                                                     | 22. DEPICTED WEATHERPROOFING METHODS (SUCH AS SEALANT, CAULKING, AND FLASHING) ARE NOT COMPREHENSIVE. FOLLOW REQUIREMENTS AND RECOMMENDATIONS OF BUILDING CODES, PRODUCT MANUFACTURERS, AND CONSTRUCTION BEST PRACTICES.                                                                                     |      |                   |
| 8. ALL REQUIRED EXITS SHALL BE OPERABLE FROM THE INSIDE, WITHOUT THE USE OF A KEY OR ANY SPECIAL KNOWLEDGE.   | 23. CONTRACTOR TO ENSURE THAT INTERIOR SHEATHING IS FLUSH, CLEAN AND FREE OF DUST AND DEFECTS BEFORE APPLICATION OF PAINT COATINGS.   |      |                   |
| 9. ANY ELECTRICAL, PLUMBING AND/OR HVAC SYSTEMS INCLUDED IN THE WORK SHALL BE INSTALLED ON A DESIGN-BUILD BASIS, AND SHALL NOT SIGNIFICANTLY ALTER THE STRUCTURE OR FINISHES.                                              | 24. FLOOR MATERIAL TRANSITIONS OCCUR AT THE CENTERLINE OF DOORS OR FRAMED OPENINGS.   |      |                   |
| 10. SMOKE DETECTORS AND CARBON MONOXIDE DETECTORS SHALL BE INSTALLED PER APPLICABLE CODES.   | 25. PROVIDE ONE COAT PRIMER AND TWO FINISH COATS OF PAINT AT INTERIOR AND EXTERIOR SURFACES.   |      |                   |
| 11. GRADING AND SITEWORK SHALL BE MINIMAL IN ALL AREAS NOT DIRECTLY AFFECTED BY THE NEW CONSTRUCTION. FOLLOW BEST PRACTICES AND LOCAL REQUIREMENTS IN ORDER TO MINIMIZE ENVIRONMENTAL DAMAGE.                              | 26. ALL GLASS SHALL CONFORM WITH HUMAN IMPACT AND SAFETY REQUIREMENTS.   |      |                   |
| 12. FINISH GRADE MUST SLOPE AWAY FROM EXTERIOR FOUNDATION WALL, AT A HEIGHT OF 6 INCHES OVER A 10 FOOT DISTANCE.   | 27. THE MINIMUM STAIRCASE TREAD SHALL BE 10" AND THE MINIMUM RISER 7.75", WITH A MAXIMUM 3/8" VARIATION WITHIN A FLIGHT.   |      |                   |
| 13. ANY SURVEY MARKERS WITHIN THE AREA OF CONSTRUCTION SHALL BE PRESERVED OR RESET BY A REGISTERED CIVIL ENGINEER OR LICENSED LAND SURVEYOR.                                                                               | 28. HANDRAILS SHALL BE LOCATED 34-38 INCHES ABOVE STAIR TREADS, AS MEASURED FROM THE NOSINGS.   |      |                   |
| 14. BEFORE GRADING OPERATIONS, A TEMPORARY PROTECTION FENCE SHALL BE CONSTRUCTED AROUND ANY TREE WITHIN 30 FEET OF THE FOUNDATION, AND A SILT FENCE MUST BE CONSTRUCTED DOWNSLOPE OF ANY AREA WHERE THE SOIL IS DISTURBED. | 29. GUARDRAILS SHALL BE LOCATED ALONG ANY FLOOR EDGES THAT DROP 30 INCHES OR MORE TO THE FLOOR OR GROUND BELOW.   |      |                   |
| 15. DEPICTED FOUNDATION SHOWS ONLY A PROPOSED DESIGN BASED ON FICTIONAL CONDITIONS. CONDUCT A SOIL TEST AND STRUCTURAL ENGINEERING FOR A SITE-SPECIFIC FOUNDATION.                                                         | 30. DO NOT USE SCREW-ON, NON-OPERABLE WINDOW SHUTTERS. THEY ARE AS TACKY AS CLIP-ON TIES. DO NOT USE VINYL OR ALUMINUM SIDING. THAT WOULD MAKE THIS HOUSE LOOK LIKE A CHEAP PLASTIC TOY. IT IS ABSOLUTELY FORBIDDEN.                                                                                         |      |                   |
|   | 31. ALL CONSTRUCTION SHALL BE TRUE, PLUMB, LEVEL, SQUARE, AND IN PROPER ALIGNMENT.   |      |                   |
|   | 32. THE GENERAL CONTRACTOR SHALL MAINTAIN A CURRENT AND COMPLETE SET OF DRAWINGS ON THE JOB SITE DURING ALL PHASES OF CONSTRUCTION. ALL SUBCONTRACTORS SHALL BE PROVIDED WITH A SET OF DRAWINGS.   |      |                   |
|   | 33. THE GENERAL CONTRACTOR SHALL VERIFY AND ASSUME RESPONSIBILITY FOR ALL DIMENSIONS AND SITE CONDITIONS, AS WELL AS INSPECT THE PREMISES AND TAKE NOTE OF EXISTING CONDITIONS PRIOR TO SUBMITTING PRICES. NO CLAIM SHALL BE ALLOWED FOR PROBLEMS WHICH COULD HAVE BEEN PREVENTED BY A THOROUGH EXAMINATION. |      |                   |
|   | 34. PROVIDE TEMPORARY SUPPORT AS NECESSARY TO ENSURE THE STRUCTURAL INTEGRITY OF THE BUILDING UNDER CONSTRUCTION. THE GENERAL CONTRACTOR IS RESPONSIBLE FOR ALL CONSTRUCTION-RELATED ACTIVITIES.   |      |                   |
|   | 35. INSTALL FIXTURES, MATERIALS, AND EQUIPMENT ACCORDING TO MANUFACTURER'S SPECIFICATIONS. SHOULD THOSE SPECS CONFLICT WITH THE DRAWINGS, IMMEDIATELY NOTIFY THE OWNER OR THE OWNER'S REPRESENTATIVE.   |      |                   |
|   | 36. VERIFY CLEARANCES FOR FIXTURES, VENTS, CHASES, ETC. BEFORE ORDERING OR INSTALLING RELATED WORK ITEMS.   |      |                   |
|   | 37. COORDINATE ALL WORK WITH EXISTING CONDITIONS, INCLUDING BUT NOT LIMITED TO: IRRIGATION PIPES, ELECTRICAL CONDUITS, WATER LINES, GAS LINES, AND DRAINAGE LINES.   |      |                   |
|   | 38. THE GENERAL CONTRACTOR SHALL BE RESPONSIBLE FOR REGULARLY REMOVING THE WASTE MATERIALS OF ALL SUBCONTRACTORS, AND MAINTAIN STRICT CONTROL OVER JOB CLEANING TO PREVENT DUST AND RUBBISH FROM INTERFERING WITH OPERATIONS.                                                                                |      |                   |
|   | 39. CONSTRUCTION EQUIPMENT NOISE SHALL BE MINIMIZED DURING THE CONSTRUCTION PHASES BY MUFFLING AND SHIELDING IMPACT TOOLS WHENEVER POSSIBLE.   |      |                   |
| ABBREVIATIONS   |   |      |                   |
| #   | POUNDS OR NUMBER   | INT  | INTERIOR          |
| AC   | AIR CONDITIONING   | MAX  | MAXIMUM           |
| B.O.   | BOTTOM OF   | MIN  | MINIMUM           |
| B/T   | BETWEEN   | (N)  | NEW               |
| BD   | BOARD   | NTS  | NOT TO SCALE      |
| BM   | BEAM   | OC   | ON CENTER         |
| CLG   | CEILING   | PERF | PERFORATED        |
| CLR   | CLEAR   | PT   | PRESSURE-TREATED  |
| CMU   | CONC MASONRY UNIT   | QTY  | QUANTITY          |
| CONC   | CONCRETE   | R    | RADIUS OR RISER   |
| CONT   | CONTINUOUS   | RCP  | REFLECTED CEILING |
| D   | DRYER   |      | PLAN              |
| DEMO   | DEMOLISH   | REF  | REFRIGERATOR      |
| DIA   | DIAMETER   | SD   | SMOKE DETECTOR    |
| DIM   | DIMENSION   | SF   | SQUARE FEET       |
| DM   | DIMMER   | SPEC | SPECIFICATION     |
| DN   | DOWN   | SYM  | SYMMETRICAL       |
| DW   | DISHWASHER   | T.O. | TOP OF            |
| (E)   | EXISTING   | T&G  | TONGUE & GROOVE   |
| EL   | ELEVATION   | TYP  | TYPICAL           |
| ELEC   | ELECTRICAL   | W    | WASHER OR WATT    |
| EQ   | EQUAL   | W/   | WITH              |
| EXT   | EXTERIOR   | W/D  | WASHER & DRYER    |
| FIN   | FINISH   | W/O  | WITHOUT           |
| FT   | FOOT   | WC   | WATER CLOSET      |
| GALV   | GALVANIZED   | WD   | WOOD              |
| GFCI   | CIRCUIT INTERRUPTER   | WH   | WATER HEATER      |
| GYP   | GYPSUM   | WP   | WEATHERPROOF      |

| NOTES: |  |  |  |
|--------|--|--|--|
|        |  |  |  |
|        |  |  |  |
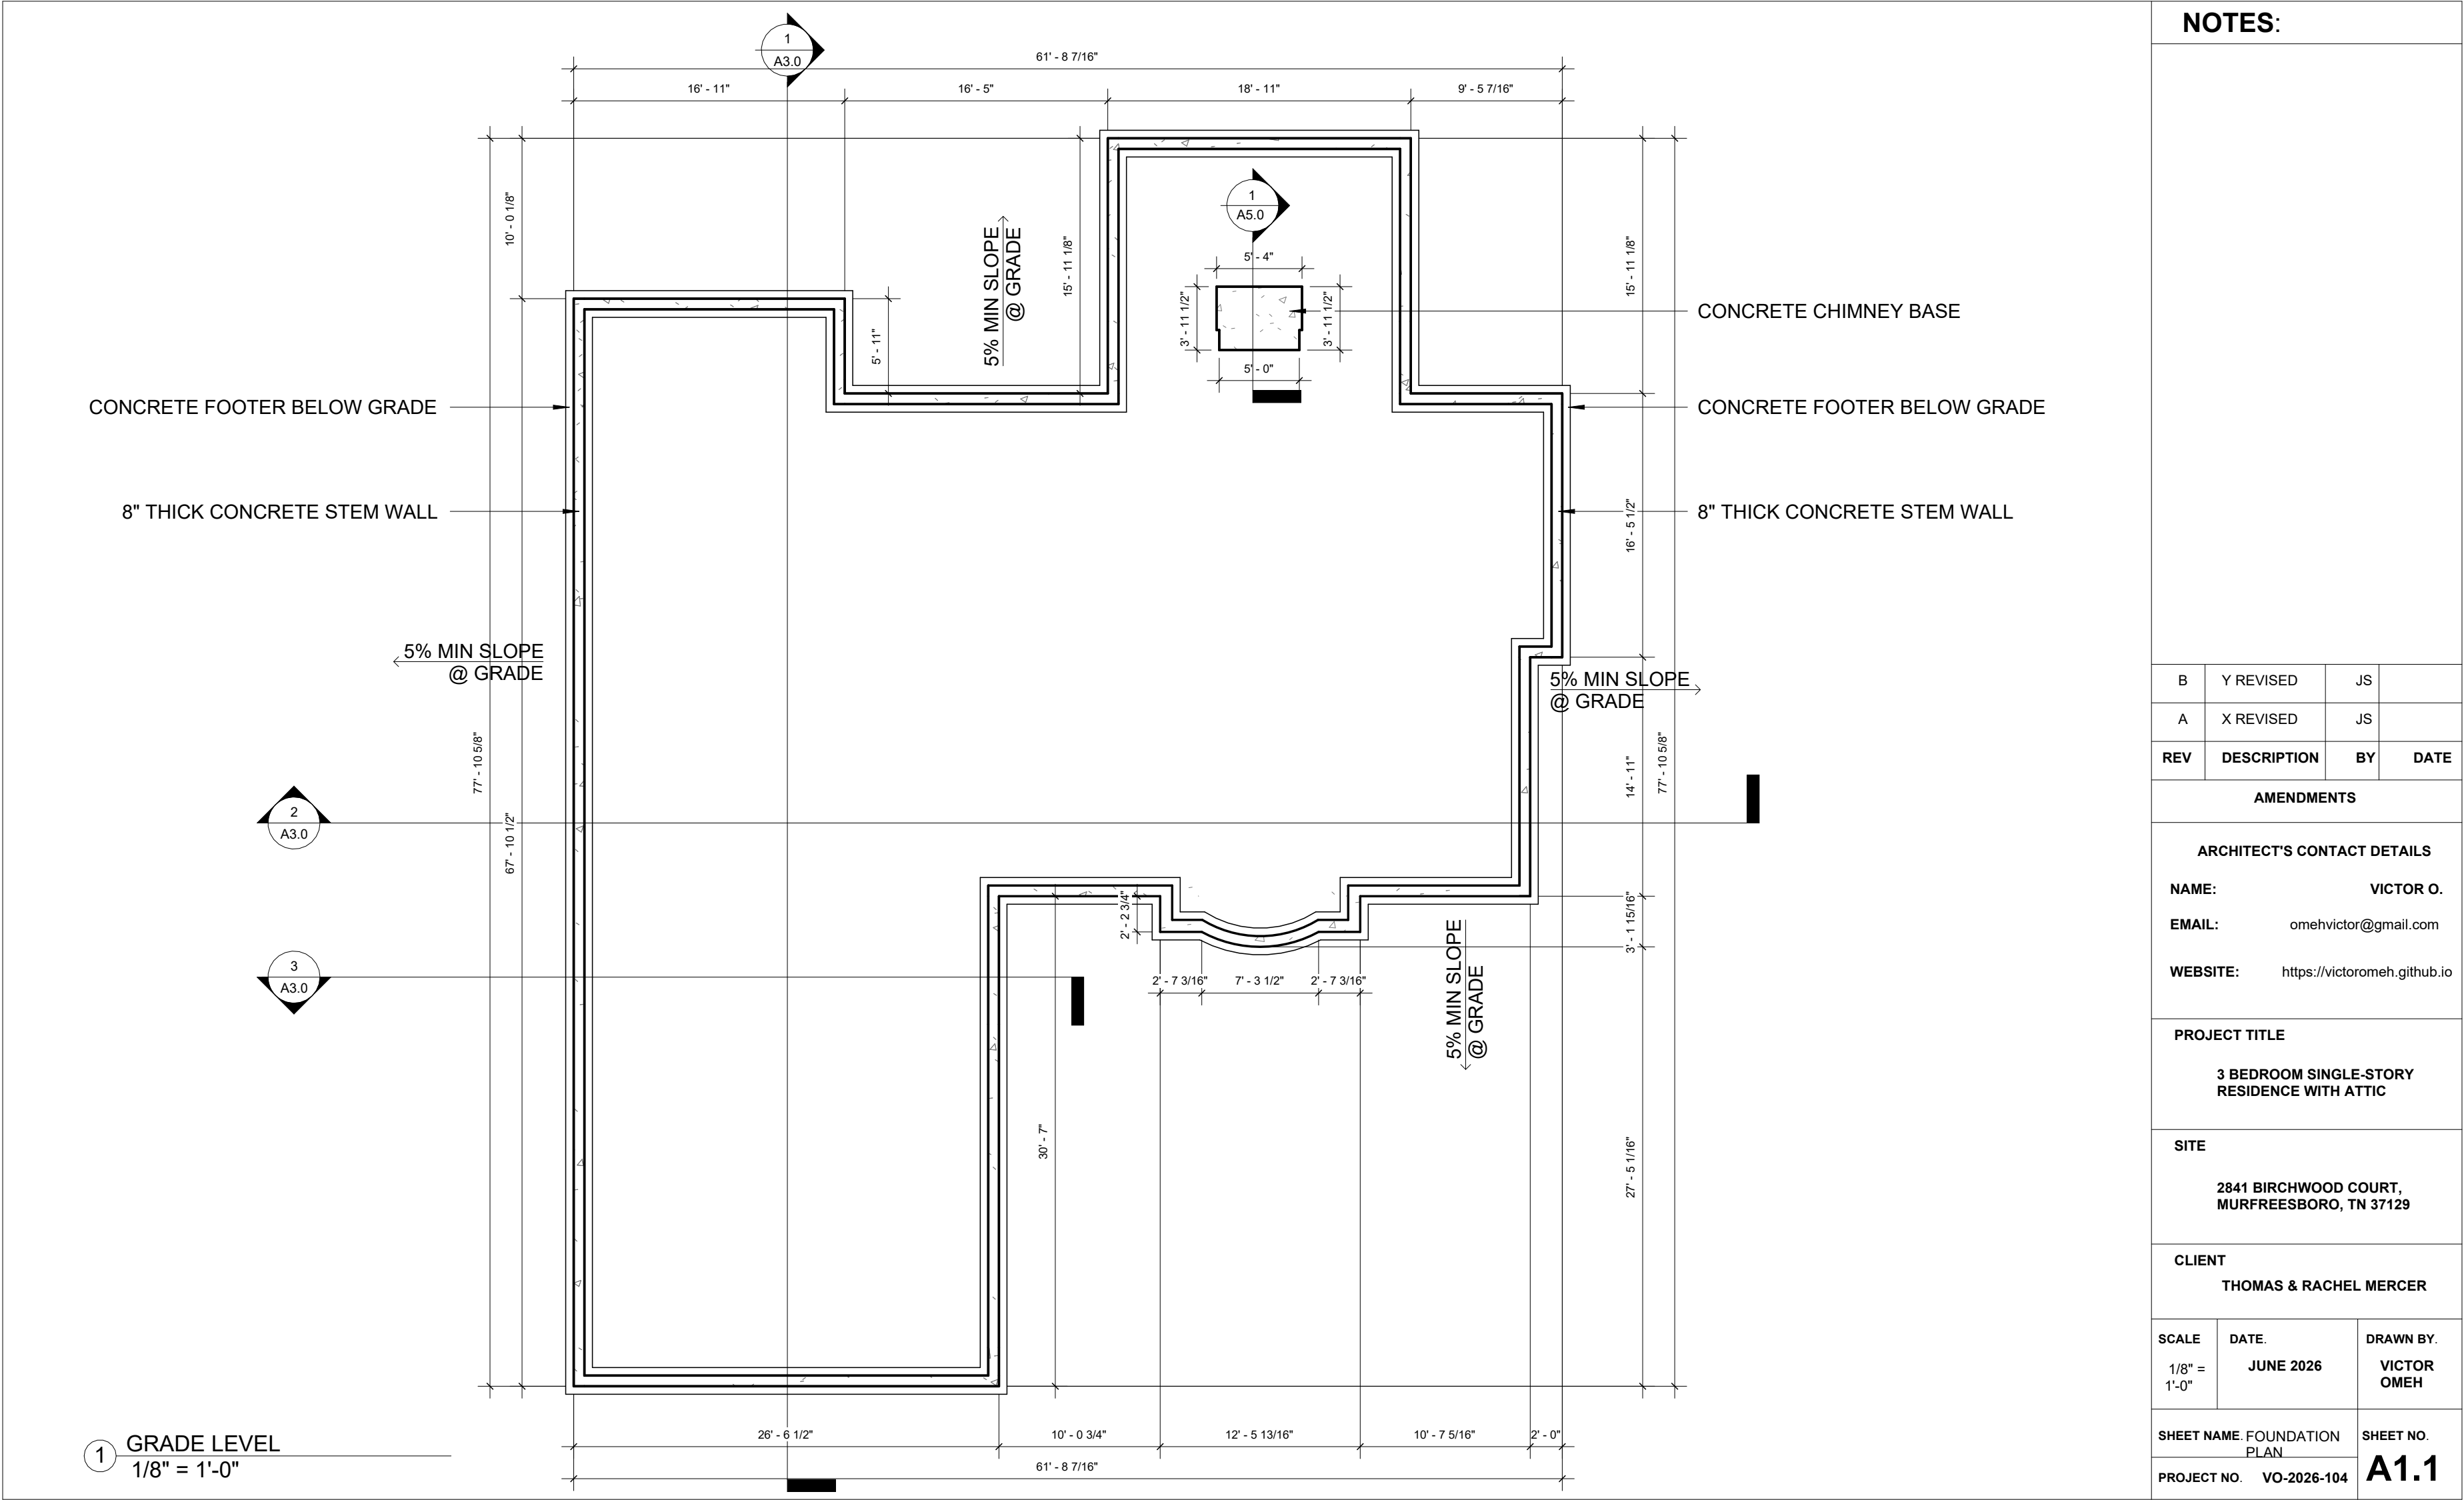

NOTES:

|     |             |    |      |
|-----|-------------|----|------|
| B   | Y REVISED   | JS |      |
| A   | X REVISED   | JS |      |
| REV | DESCRIPTION | BY | DATE |

AMENDMENTS

|                             |                              |  |  |
|-----------------------------|------------------------------|--|--|
| ARCHITECT'S CONTACT DETAILS |                              |  |  |
| NAME:                       | VICTOR O.                    |  |  |
| EMAIL:                      | omehvictor@gmail.com         |  |  |
| WEBSITE:                    | https://victoromeh.github.io |  |  |


|                                             |
|---------------------------------------------|
| PROJECT TITLE                               |
| 3 BEDROOM SINGLE-STORY RESIDENCE WITH ATTIC |

|                                              |
|----------------------------------------------|
| SITE                                         |
| 2841 BIRCHWOOD COURT, MURFREESBORO, TN 37129 |


|                        |
|------------------------|
| CLIENT                 |
| THOMAS & RACHEL MERCER |

|              |           |             |
|--------------|-----------|-------------|
| SCALE        | DATE      | DRAWN BY.   |
| 1/8" = 1'-0" | JUNE 2026 | VICTOR OMEH |

|                             |                |
|-----------------------------|----------------|
| SHEET NAME. FOUNDATION PLAN | SHEET NO. A1.1 |
| PROJECT NO. VO-2026-104     |                |

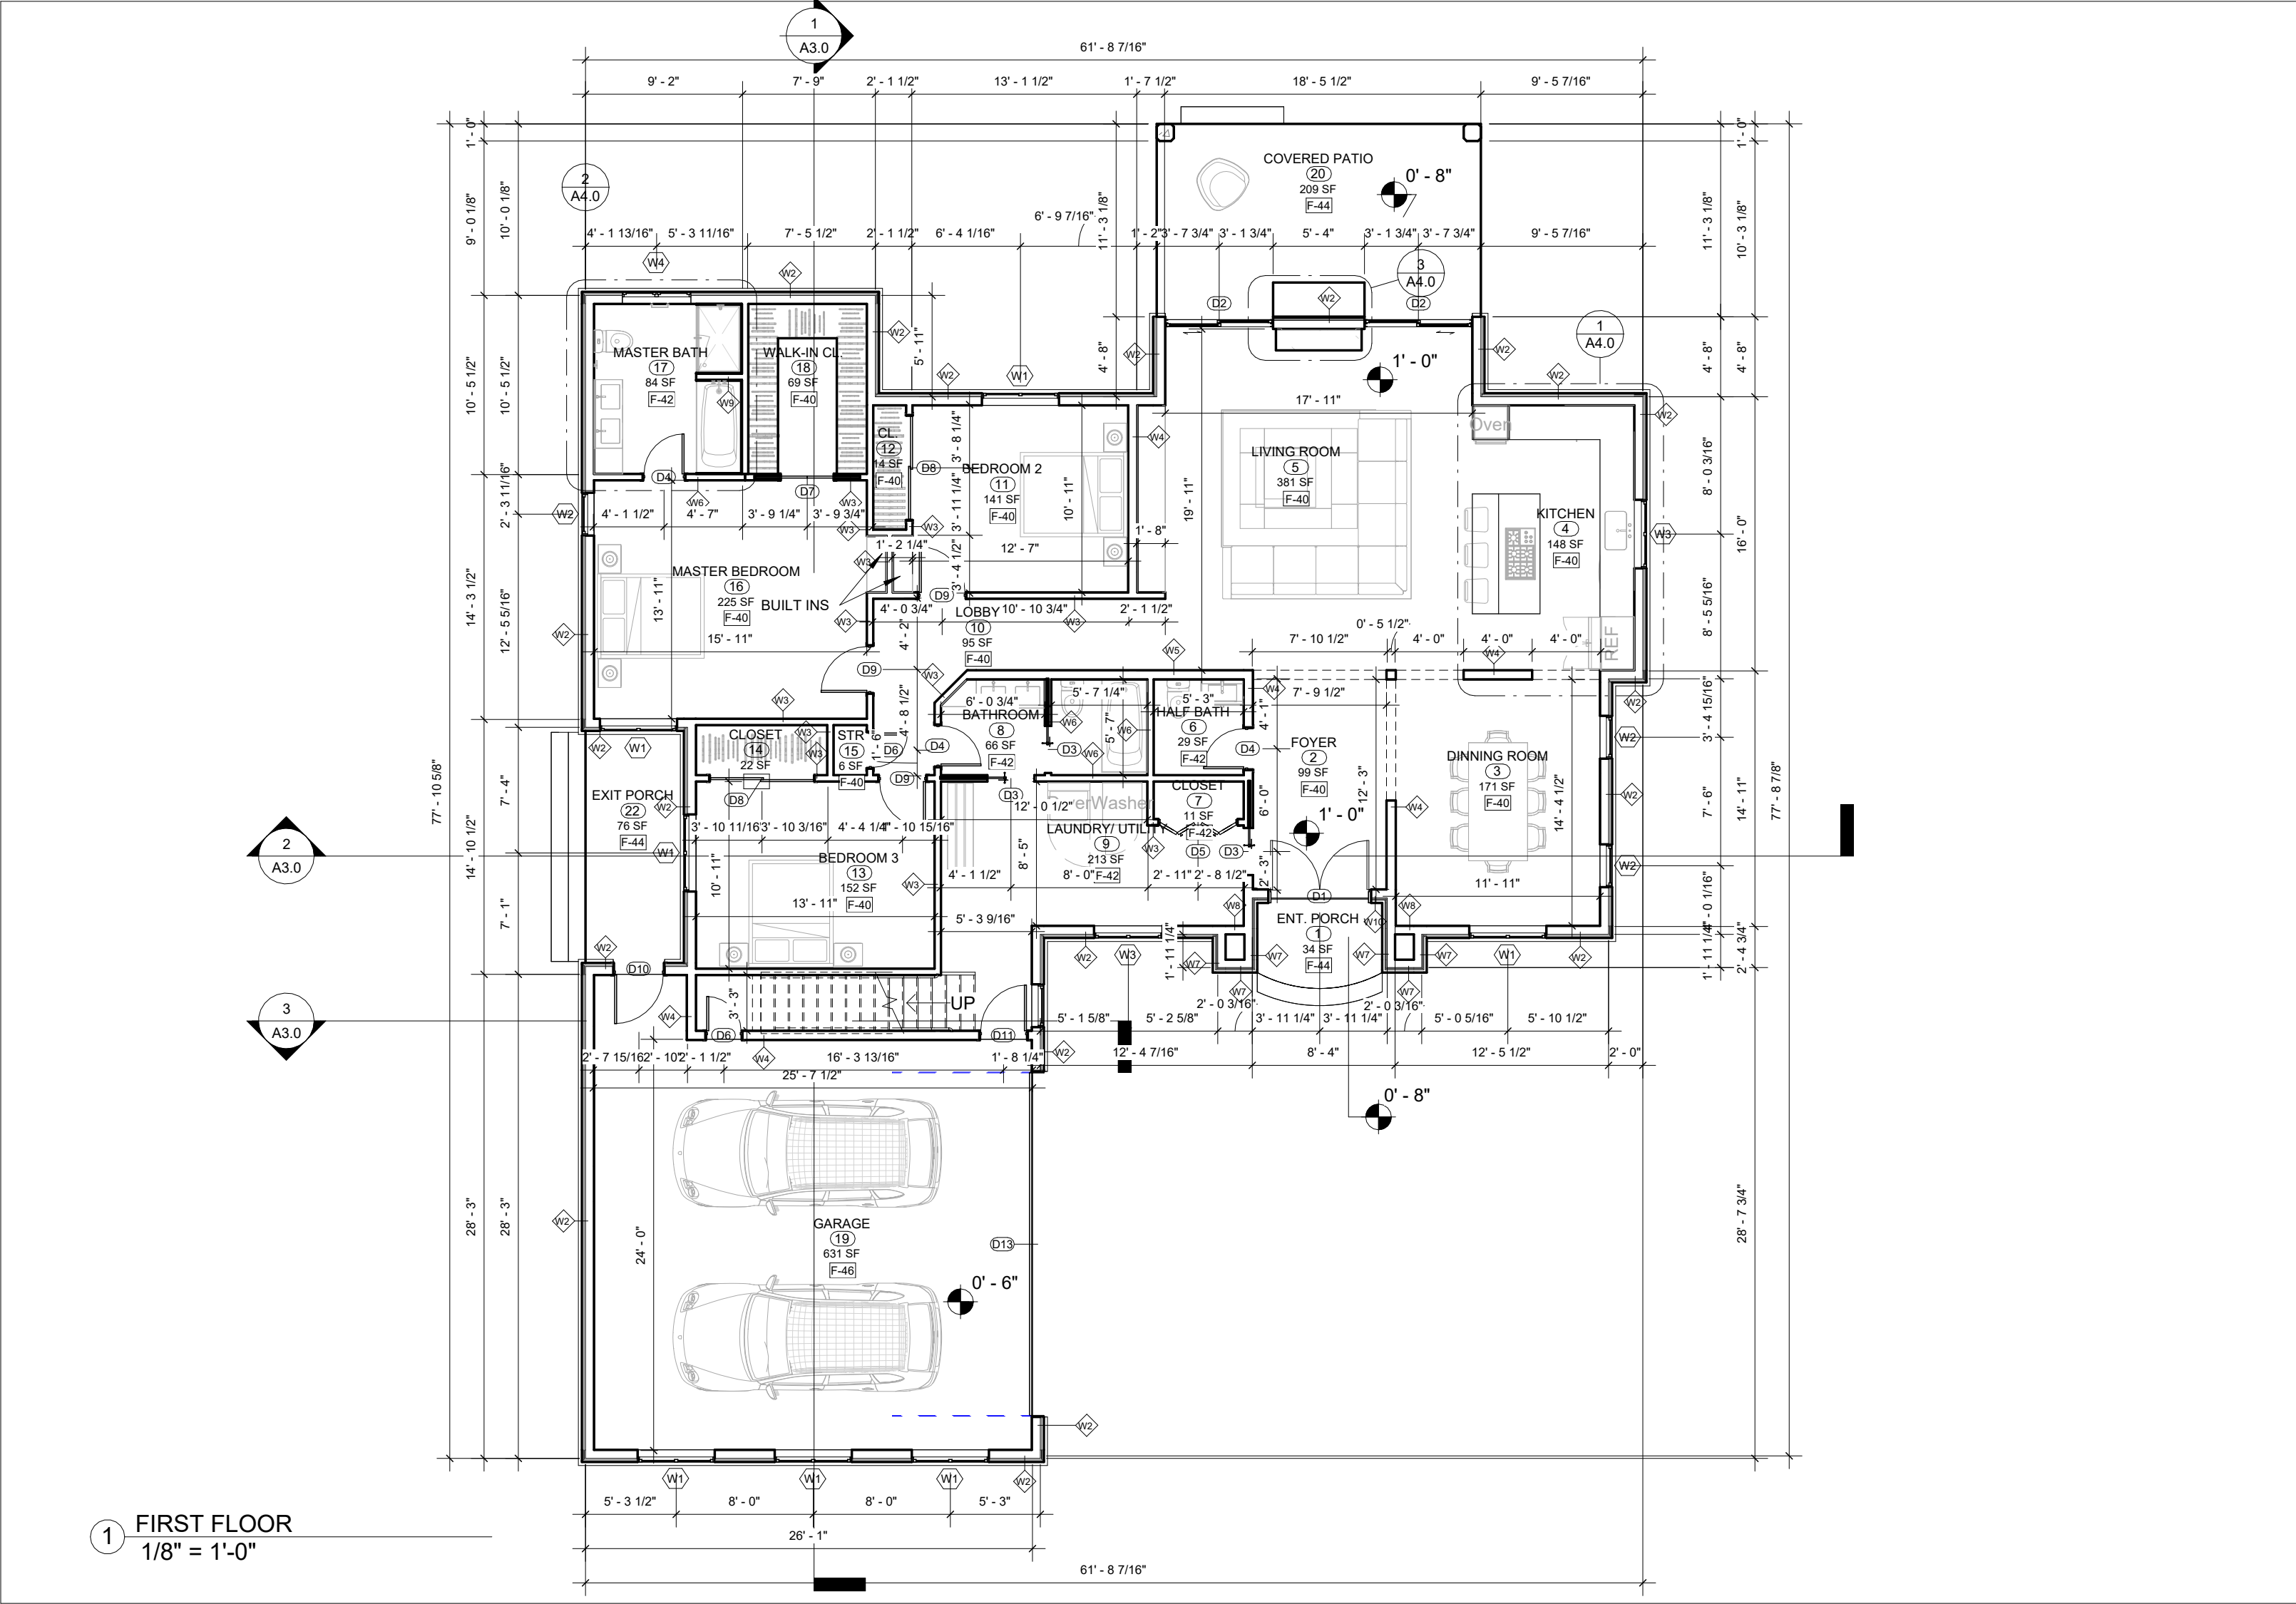

| NOTES:                                       |             |                              |                |
|----------------------------------------------|-------------|------------------------------|----------------|
|                                              |             |                              |                |
| B                                            | Y REVISED   | JS                           |                |
| A                                            | X REVISED   | JS                           |                |
| REV                                          | DESCRIPTION | BY                           | DATE           |
| AMENDMENTS                                   |             |                              |                |
| ARCHITECT'S CONTACT DETAILS                  |             |                              |                |
| NAME:                                        |             | VICTOR O.                    |                |
| EMAIL:                                       |             | omehvictor@gmail.com         |                |
| WEBSITE:                                     |             | https://victoromeh.github.io |                |
| PROJECT TITLE                                |             |                              |                |
| 3 BEDROOM SINGLE-STORY RESIDENCE WITH ATTIC  |             |                              |                |
| SITE                                         |             |                              |                |
| 2841 BIRCHWOOD COURT, MURFREESBORO, TN 37129 |             |                              |                |
| CLIENT                                       |             |                              |                |
| THOMAS & RACHEL MERCER                       |             |                              |                |
| SCALE                                        | DATE        |                              | DRAWN BY.      |
| 1/8" = 1'-0"                                 | JUNE 2026   |                              | VICTOR OMEH    |
| SHEET NAME. FIRST FLOOR PLAN                 |             |                              | SHEET NO. A1.2 |
| PROJECT NO. VO-2026-104                      |             |                              |                |

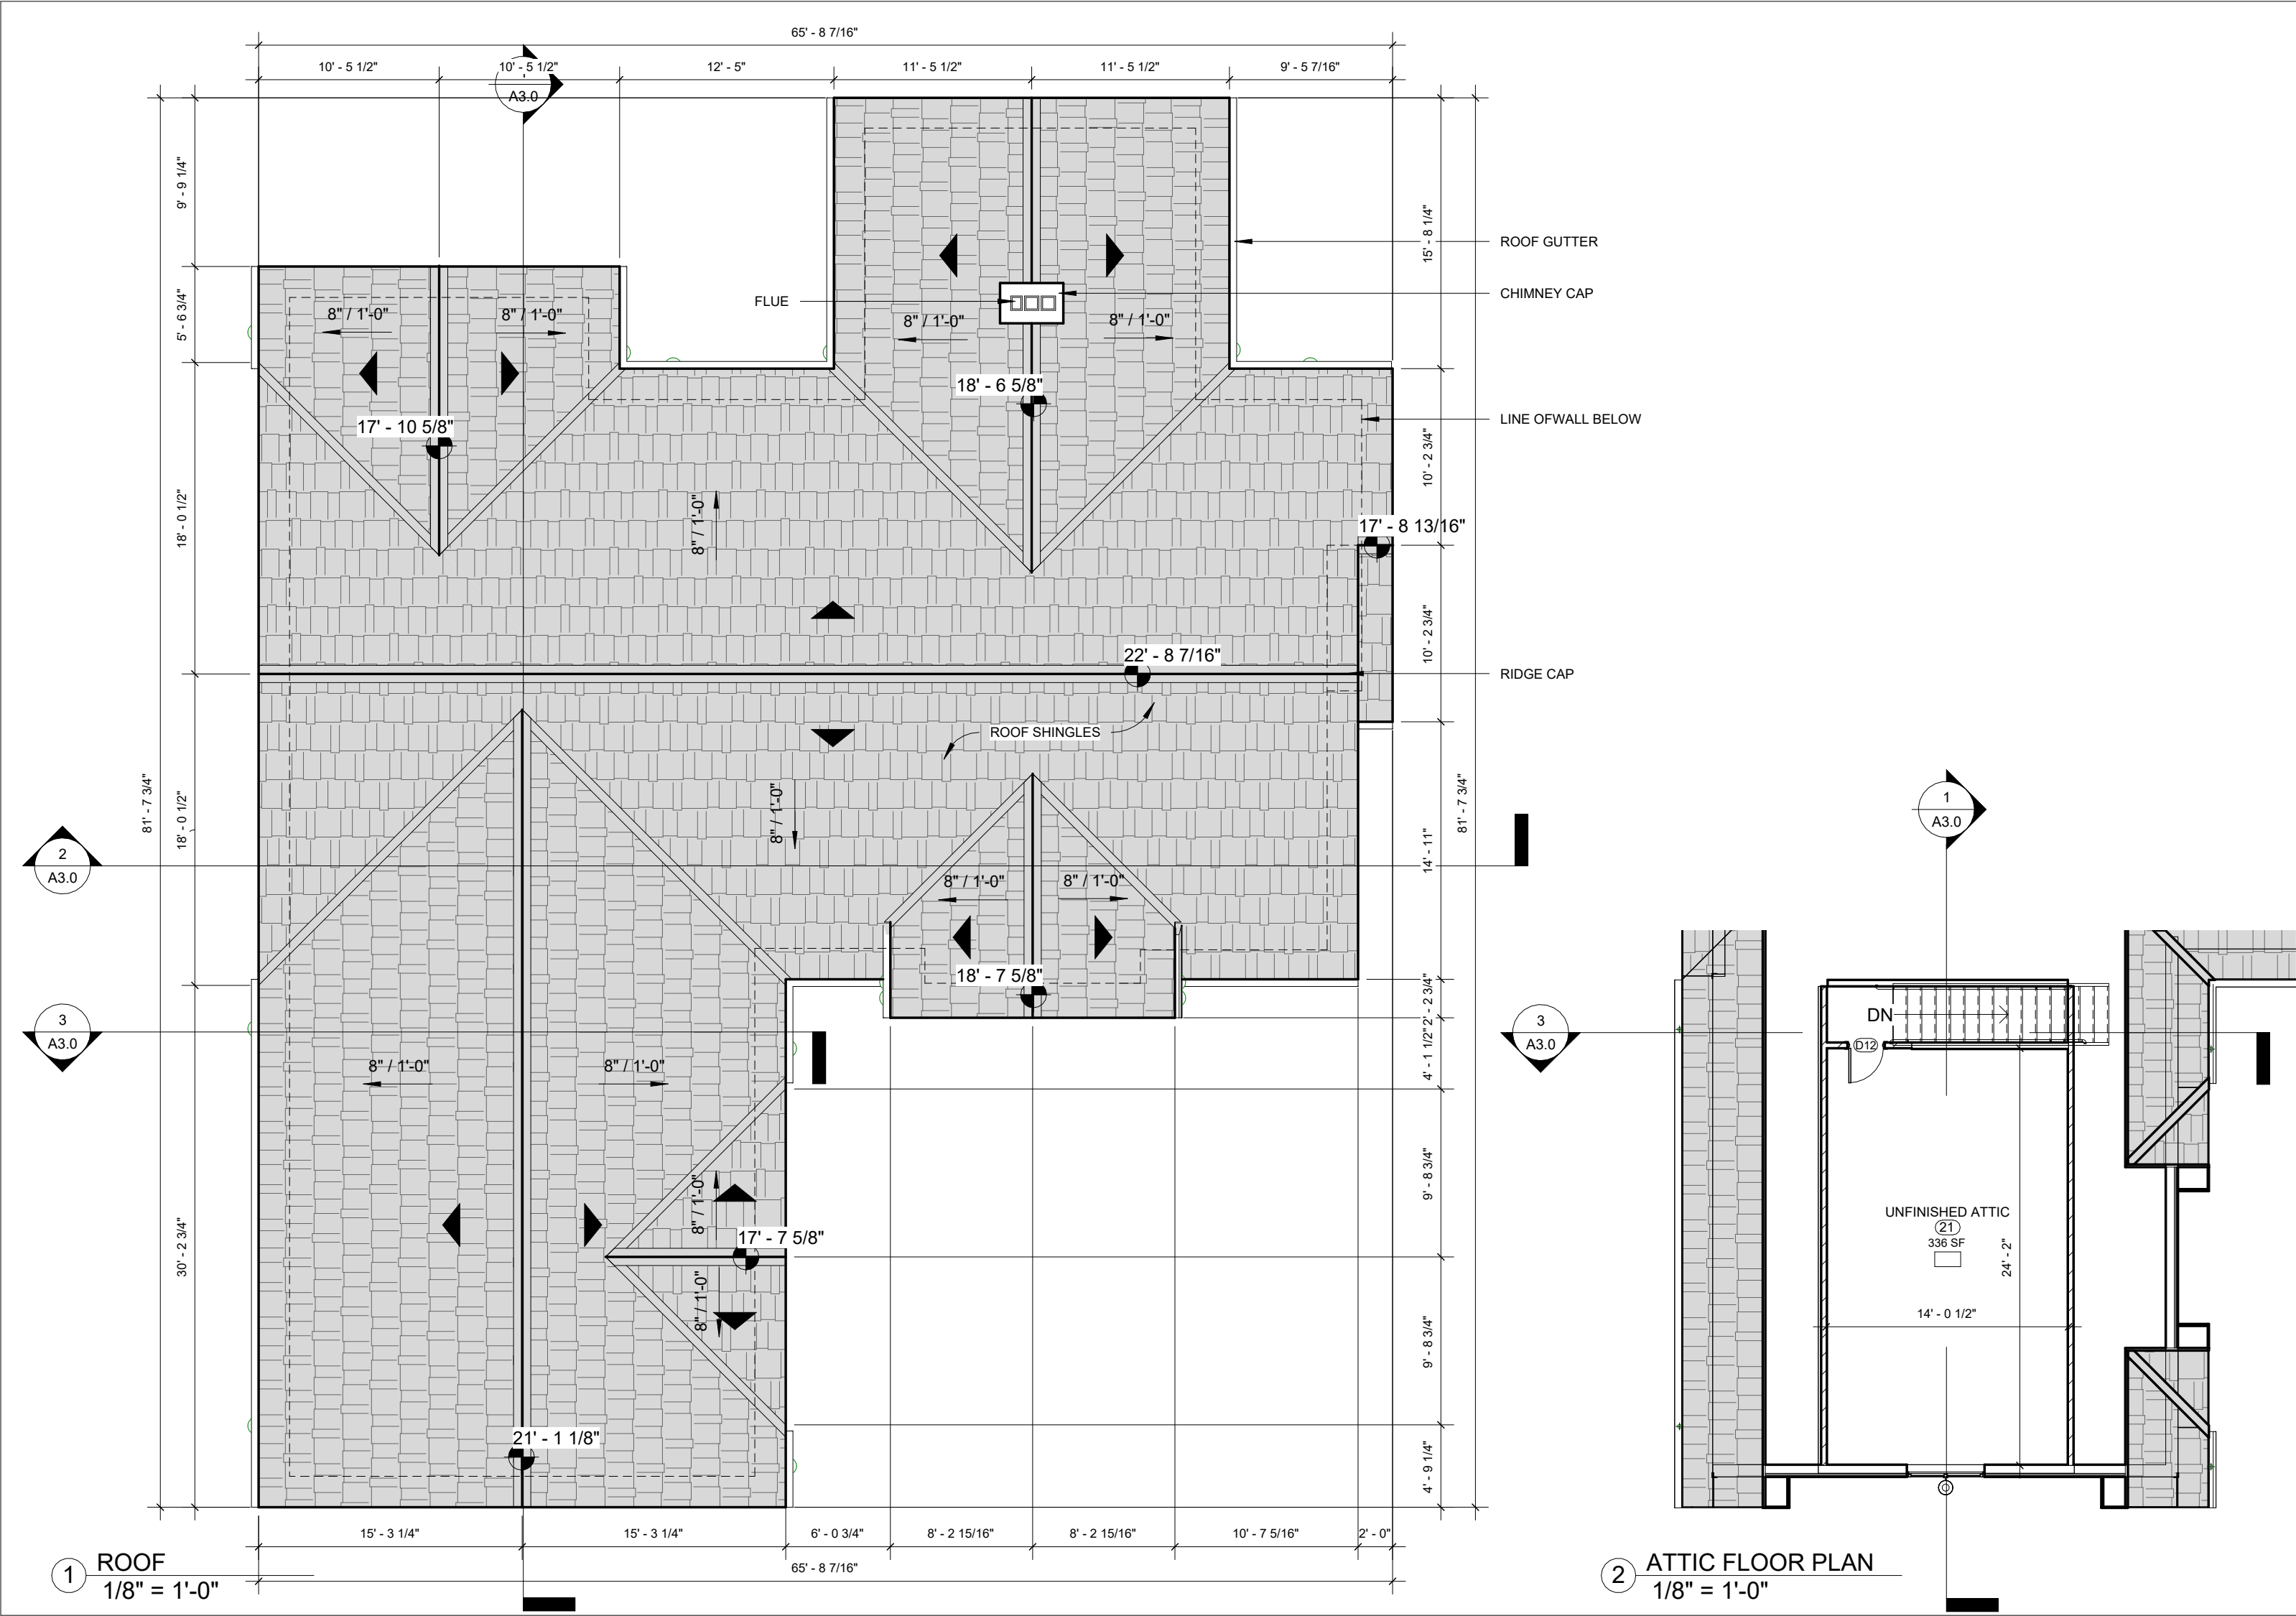

NOTES:

| B   | Y REVISED   | JS |      |
|-----|-------------|----|------|
| A   | X REVISED   | JS |      |
| REV | DESCRIPTION | BY | DATE |

AMENDMENTS

ARCHITECT'S CONTACT DETAILS

|          |                              |
|----------|------------------------------|
| NAME:    | VICTOR O.                    |
| EMAIL:   | omehvictor@gmail.com         |
| WEBSITE: | https://victoromeh.github.io |

PROJECT TITLE

3 BEDROOM SINGLE-STORY  
RESIDENCE WITH ATTIC

SITE

2841 BIRCHWOOD COURT,  
MURFREESBORO, TN 37129

CLIENT

THOMAS & RACHEL MERCER


|                 |           |                |
|-----------------|-----------|----------------|
| SCALE           | DATE      | DRAWN BY.      |
| 1/8" =<br>1'-0" | JUNE 2026 | VICTOR<br>OMEH |

SHEET NAME. ROOF PLAN

PROJECT NO. VO-2026-104

SHEET NO.

A1.3

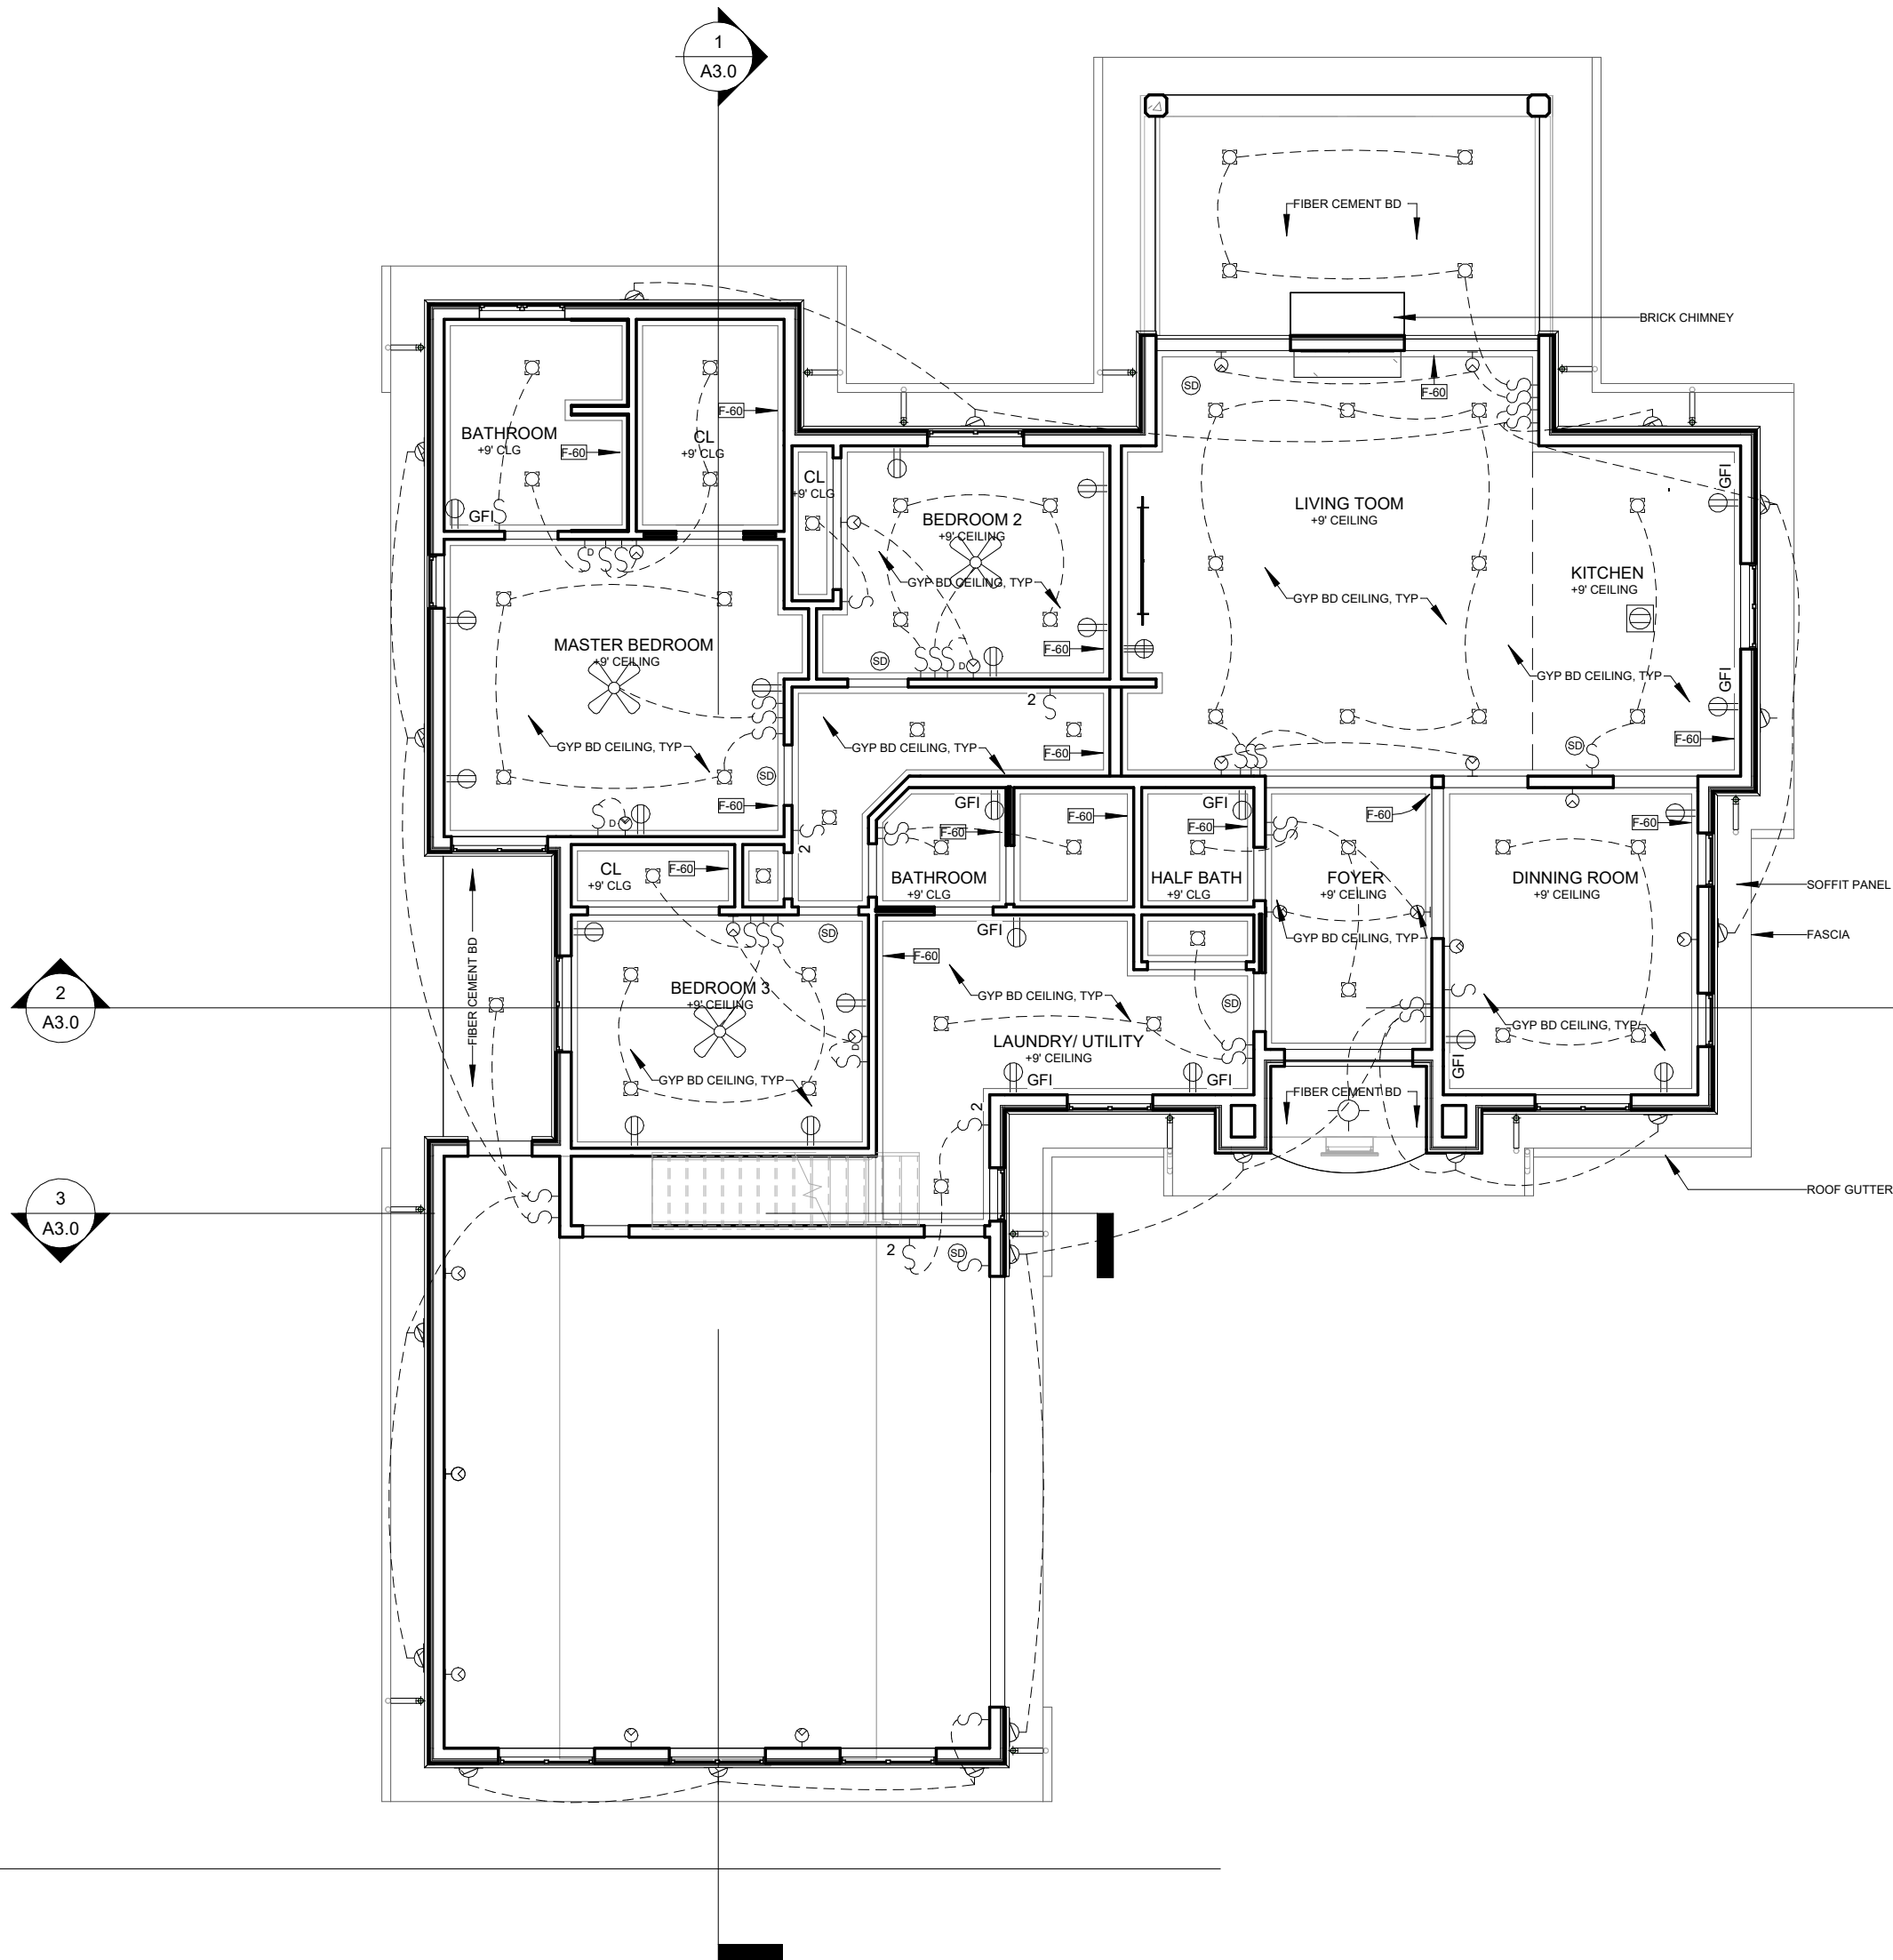

- FLOOR OUTLET
- ELECTRIC OUTLET (TRIPLE)
- FLOOR OUTLET (GFI)
- ELECTRIC OUTLET
- SWITCH
- SWITCH (DIMMER)
- SWITCH (2 WAY)
- SWITCH (3 WAY)
- CEILING LIGHT
- RECESSED LIGHT
- WALL-HUNG LIGHT
- CEILING FAN
- SMOKE DETECTOR
- CEILING FAN REGULATOR
- W.P SECURITY LIGHT
- WALL BRACKET LIGHTING

NOTES:

| B   | Y REVISED   | JS |      |
|-----|-------------|----|------|
| A   | X REVISED   | JS |      |
| REV | DESCRIPTION | BY | DATE |

| AMENDMENTS                  |                              |  |  |
|-----------------------------|------------------------------|--|--|
| ARCHITECT'S CONTACT DETAILS |                              |  |  |
| NAME:                       | VICTOR O.                    |  |  |
| EMAIL:                      | omehvector@gmail.com         |  |  |
| WEBSITE:                    | https://victoromeh.github.io |  |  |



| PROJECT TITLE                               |
|---------------------------------------------|
| 3 BEDROOM SINGLE-STORY RESIDENCE WITH ATTIC |

| SITE                                         |
|----------------------------------------------|
| 2841 BIRCHWOOD COURT, MURFREESBORO, TN 37129 |

| CLIENT                 |
|------------------------|
| THOMAS & RACHEL MERCER |



| SCALE        | DATE      | DRAWN BY.   |
|--------------|-----------|-------------|
| As indicated | JUNE 2026 | VICTOR OMEH |

| SHEET NAME  | RCP/ ELECTRICAL | SHEET NO. |
|-------------|-----------------|-----------|
| PROJECT NO. | VO-2026-104     | A1.4      |

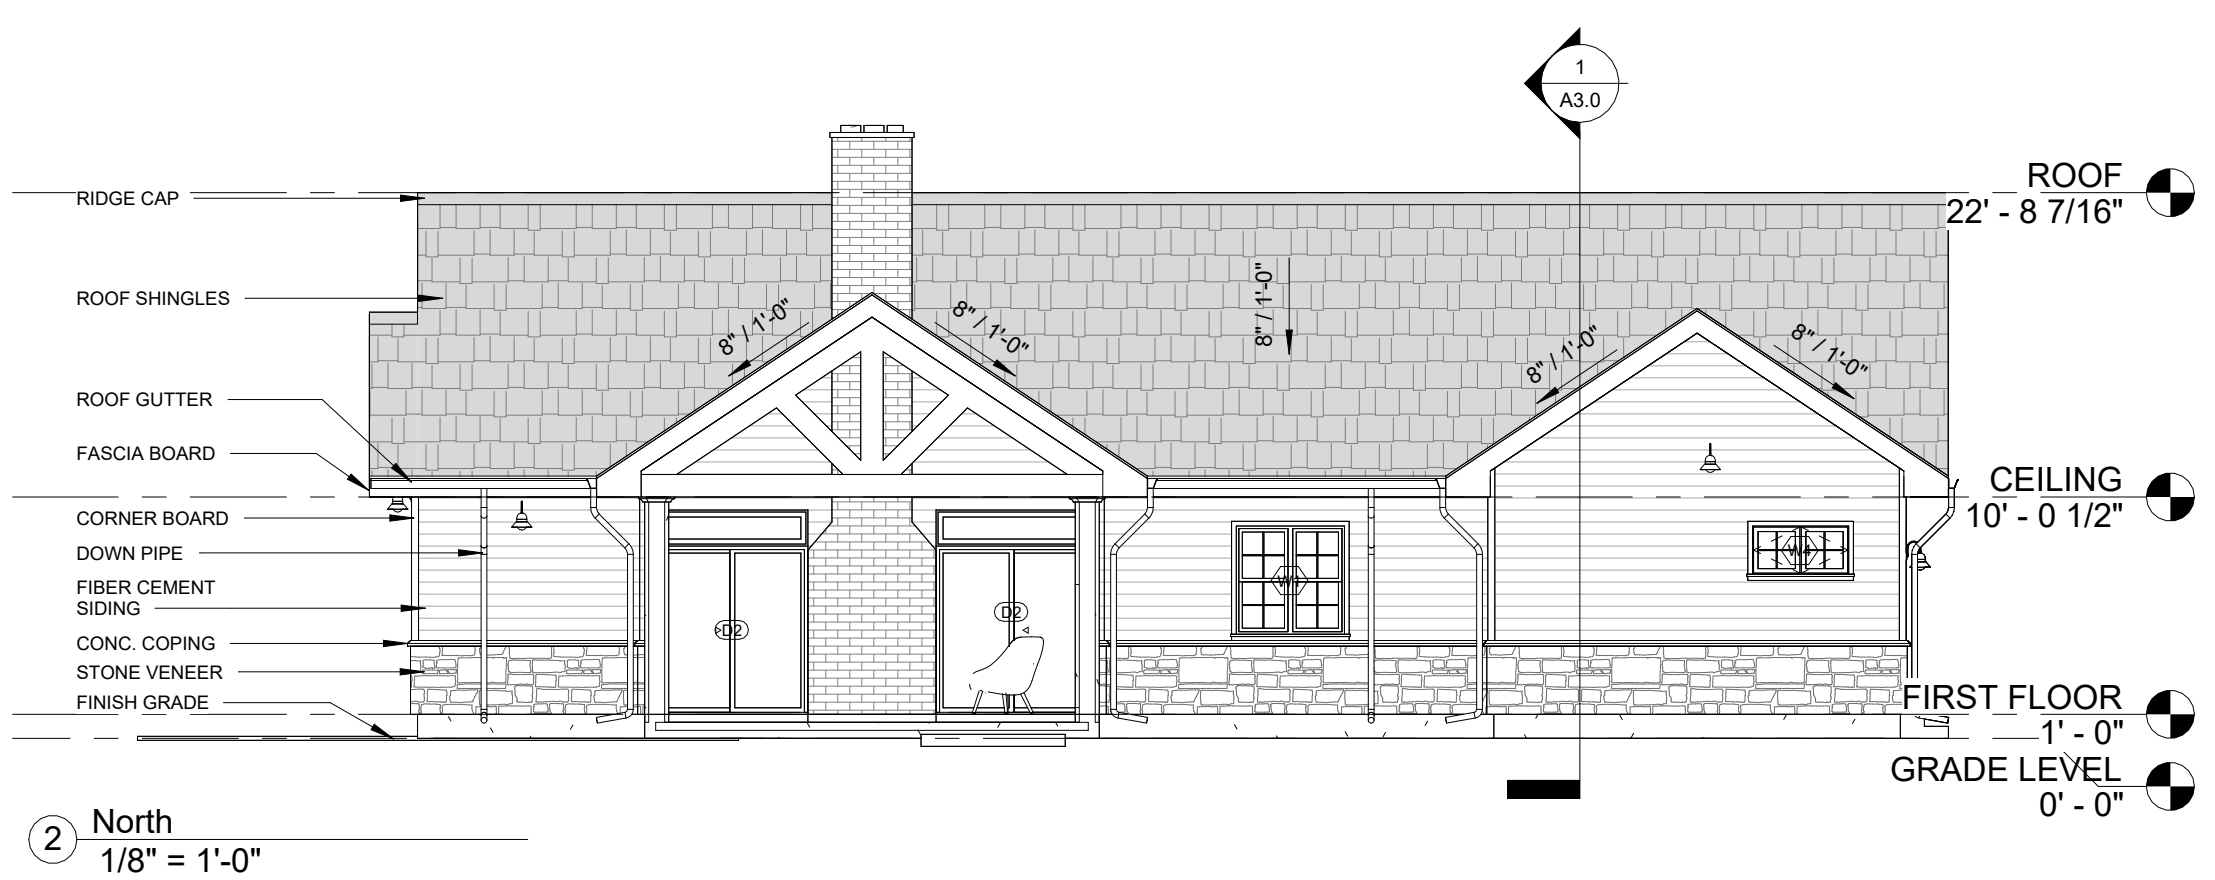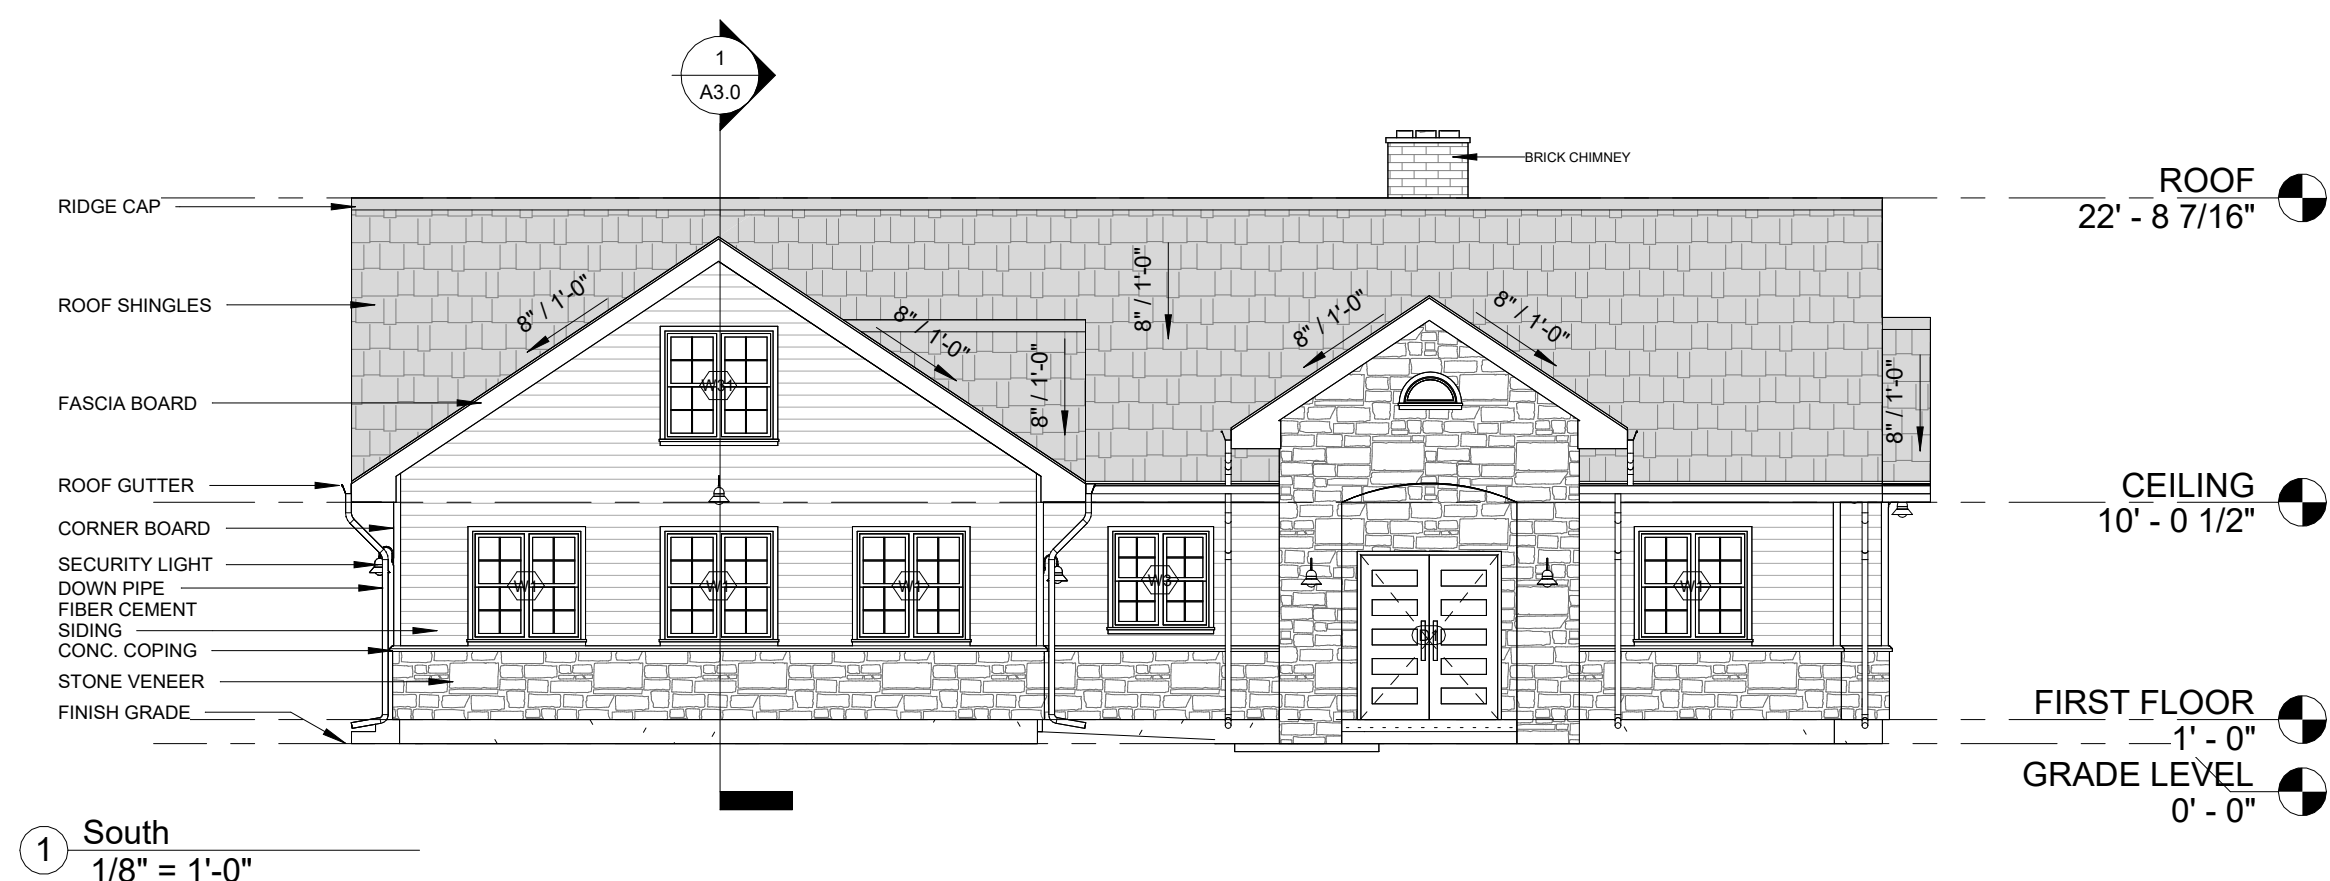


| NOTES:                                          |             |                              |                |
|-------------------------------------------------|-------------|------------------------------|----------------|
|                                                 |             |                              |                |
| B                                               | Y REVISED   | JS                           |                |
| A                                               | X REVISED   | JS                           |                |
| REV                                             | DESCRIPTION | BY                           | DATE           |
| AMENDMENTS                                      |             |                              |                |
| ARCHITECT'S CONTACT DETAILS                     |             |                              |                |
| NAME:                                           |             | VICTOR O.                    |                |
| EMAIL:                                          |             | omehvictor@gmail.com         |                |
| WEBSITE:                                        |             | https://victoromeh.github.io |                |
| PROJECT TITLE                                   |             |                              |                |
| 3 BEDROOM SINGLE-STORY<br>RESIDENCE WITH ATTIC  |             |                              |                |
| SITE                                            |             |                              |                |
| 2841 BIRCHWOOD COURT,<br>MURFREESBORO, TN 37129 |             |                              |                |
| CLIENT                                          |             |                              |                |
| THOMAS & RACHEL MERCER                          |             |                              |                |
| SCALE                                           | DATE:       |                              | DRAWN BY.      |
| 1/8" =<br>1'-0"                                 | JUNE 2026   |                              | VICTOR<br>OMEH |
| SHEET NAME. SOUTH & NORTH<br>ELEVATION          |             |                              | SHEET NO.      |
| PROJECT NO. VO-2026-104                         |             |                              | A2.0           |


NOTES:

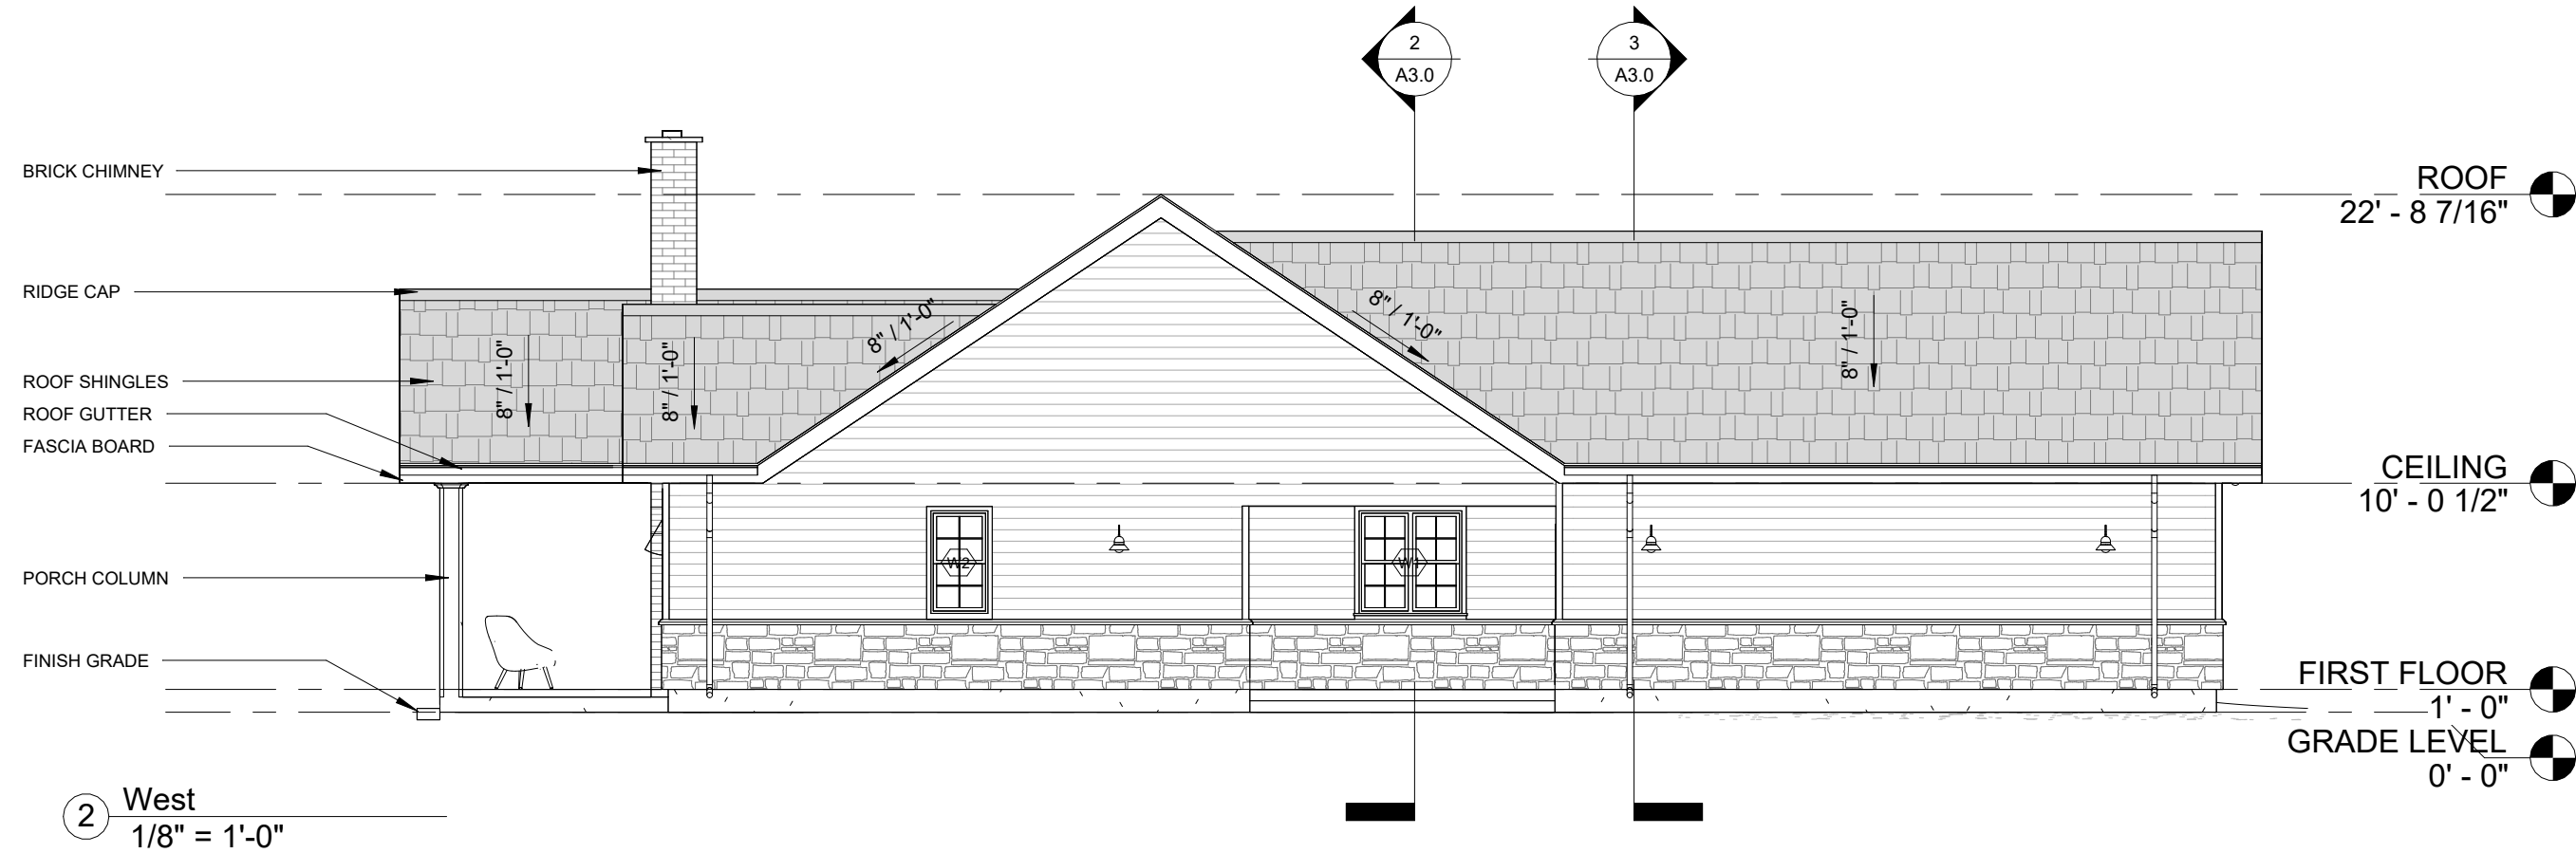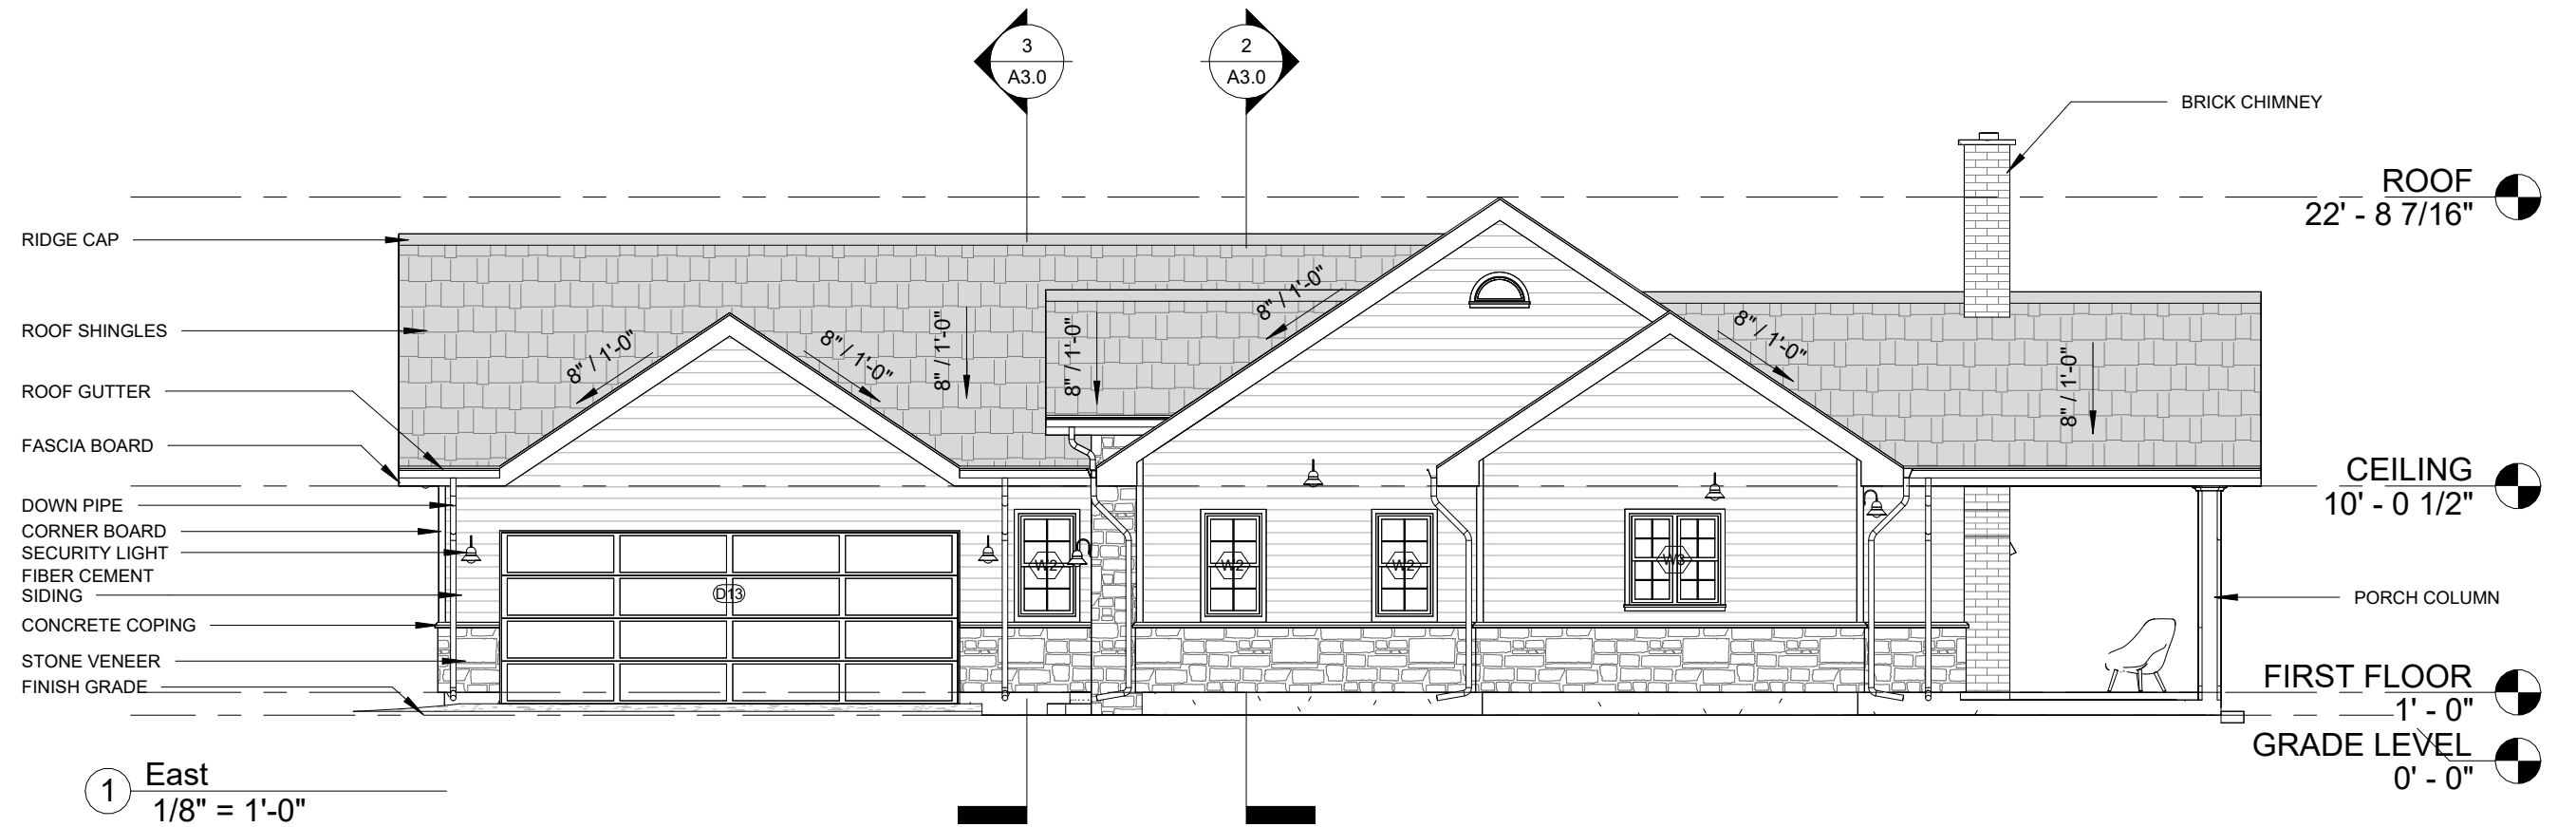


|                                                 |             |                              |      |
|-------------------------------------------------|-------------|------------------------------|------|
| B                                               | Y REVISED   | JS                           |      |
| A                                               | X REVISED   | JS                           |      |
| REV                                             | DESCRIPTION | BY                           | DATE |
| AMENDMENTS                                      |             |                              |      |
| ARCHITECT'S CONTACT DETAILS                     |             |                              |      |
| NAME:                                           |             | VICTOR O.                    |      |
| EMAIL:                                          |             | omehvictor@gmail.com         |      |
| WEBSITE:                                        |             | https://victoromeh.github.io |      |
| PROJECT TITLE                                   |             |                              |      |
| 3 BEDROOM SINGLE-STORY<br>RESIDENCE WITH ATTIC  |             |                              |      |
| SITE                                            |             |                              |      |
| 2841 BIRCHWOOD COURT,<br>MURFREESBORO, TN 37129 |             |                              |      |
| CLIENT                                          |             |                              |      |
| THOMAS & RACHEL MERCER                          |             |                              |      |
| SCALE                                           | DATE:       | DRAWN BY.                    |      |
| 1/8" =<br>1'-0"                                 | JUNE 2026   | VICTOR<br>OMEH               |      |
| SHEET NAME. EAST & WEST<br>ELEVATION            |             | SHEET NO.                    |      |
| PROJECT NO. VO-2026-104                         |             | A2.1                         |      |

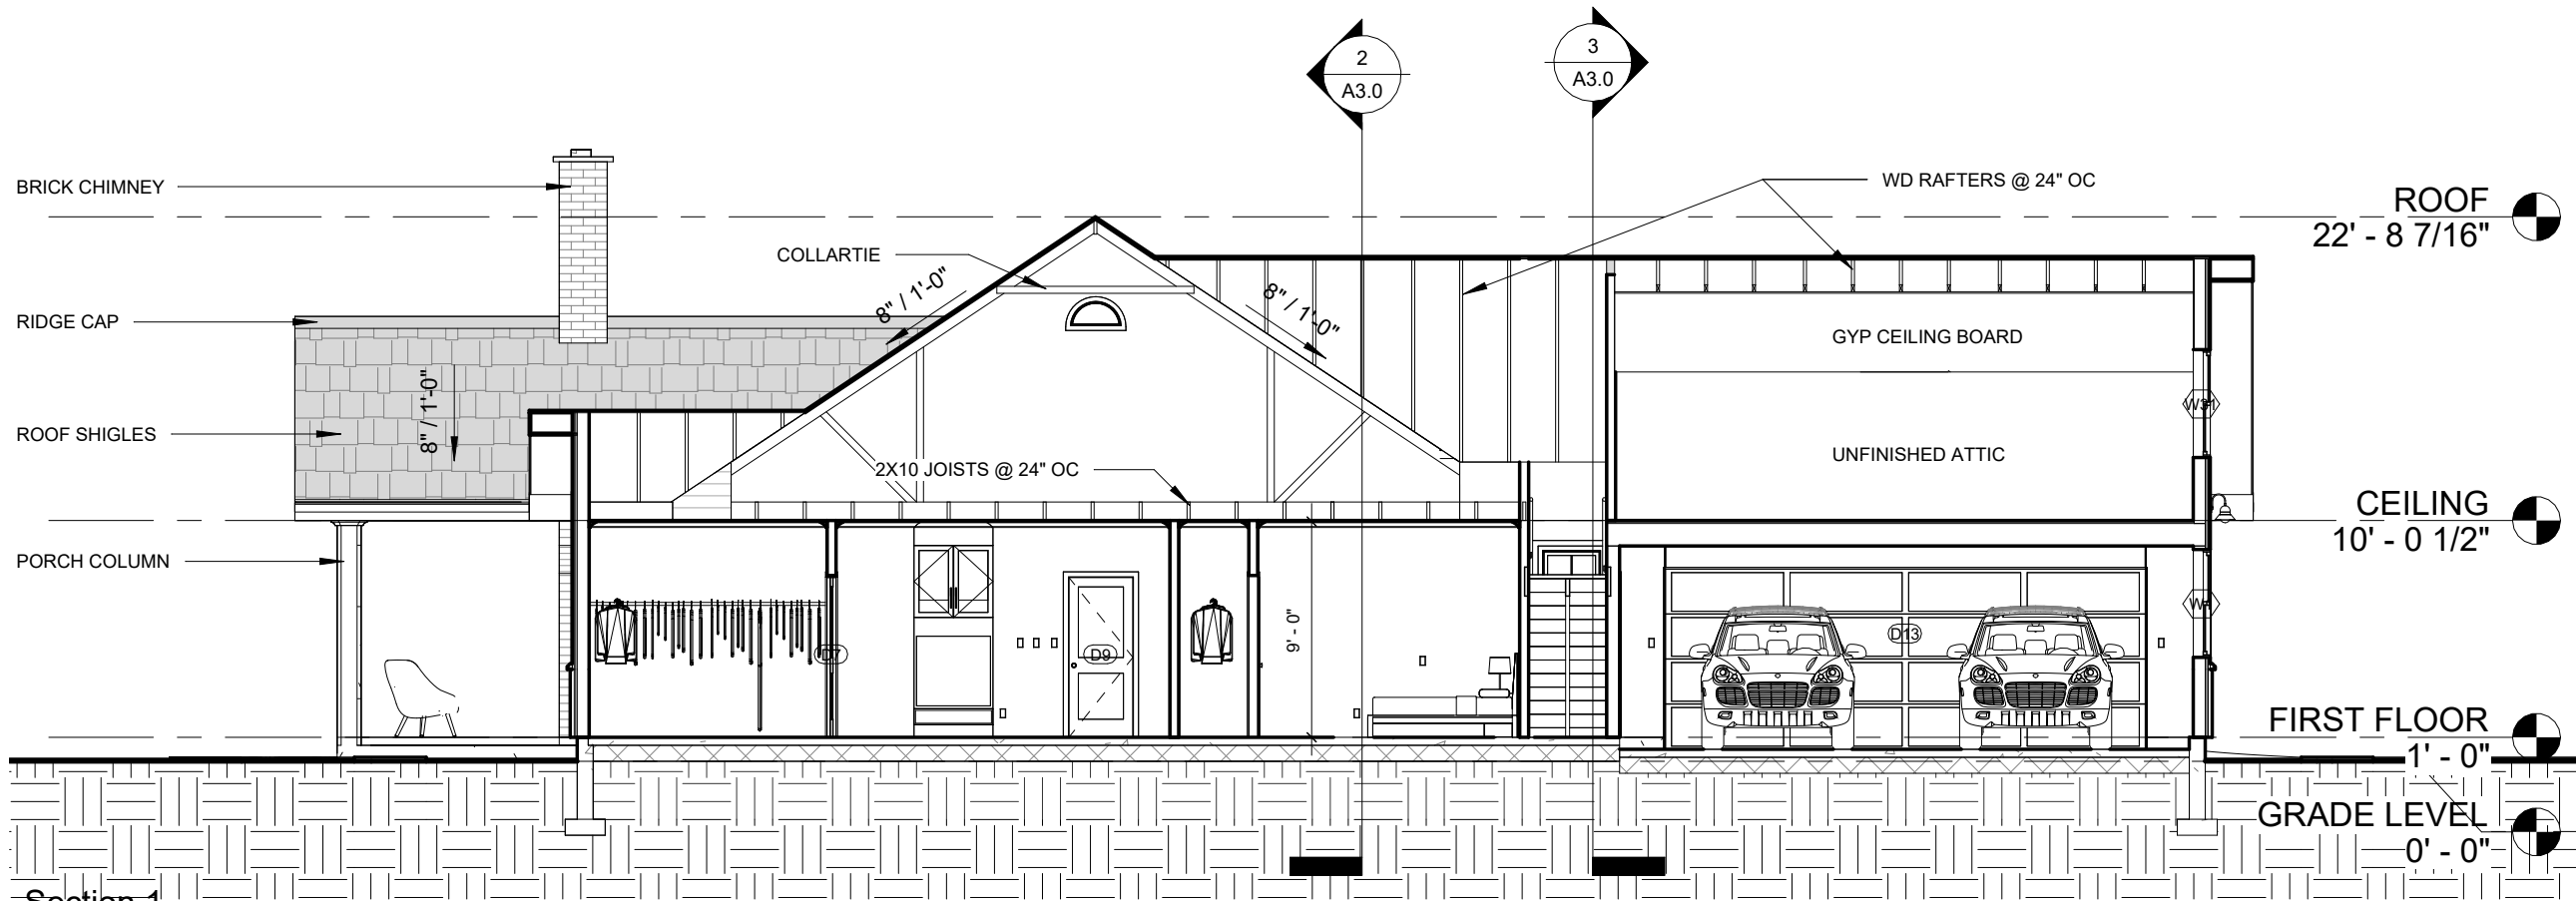

1 Section 1  
1/8" = 1'-0"

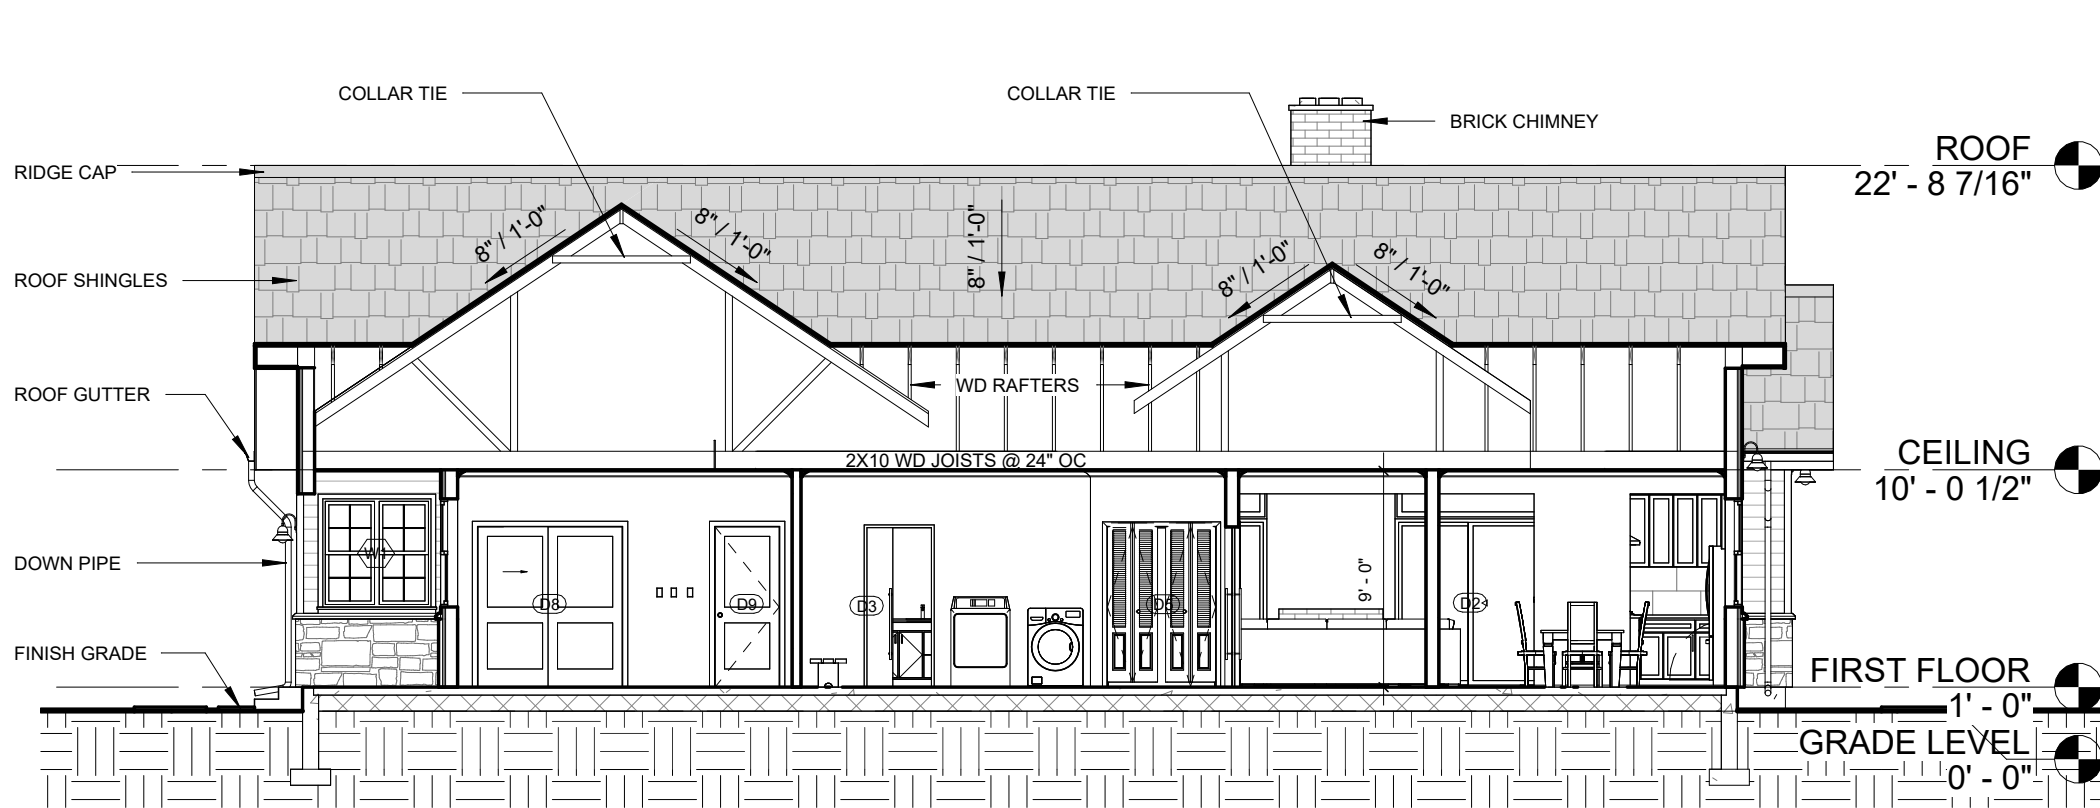

2 Section 2  
1/8" = 1'-0"

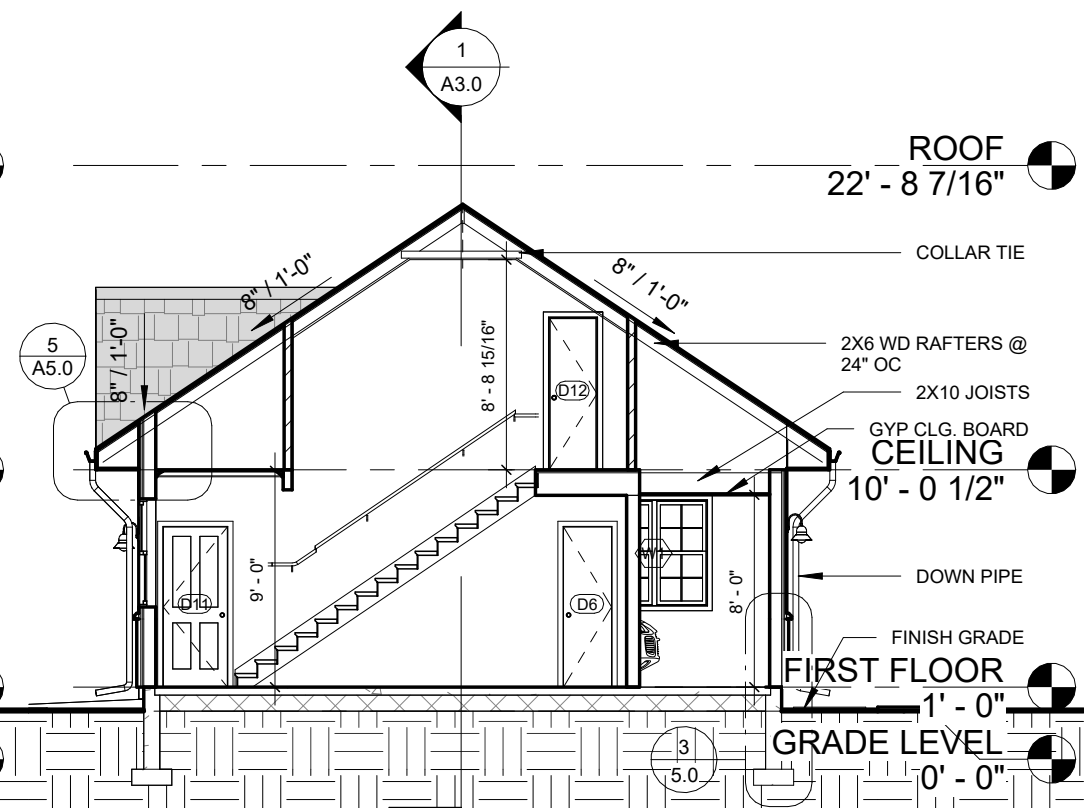

3 Section 3  
1/8" = 1'-0"

NOTES:

| B   | Y REVISED   | JS |      |
|-----|-------------|----|------|
| A   | X REVISED   | JS |      |
| REV | DESCRIPTION | BY | DATE |

AMENDMENTS

| ARCHITECT'S CONTACT DETAILS |                              |
|-----------------------------|------------------------------|
| NAME:                       | VICTOR O.                    |
| EMAIL:                      | omehvictor@gmail.com         |
| WEBSITE:                    | https://victoromeh.github.io |




| PROJECT TITLE                               |
|---------------------------------------------|
| 3 BEDROOM SINGLE-STORY RESIDENCE WITH ATTIC |

| SITE                                            |
|-------------------------------------------------|
| 2841 BIRCHWOOD COURT,<br>MURFREESBORO, TN 37129 |

| CLIENT                 |
|------------------------|
| THOMAS & RACHEL MERCER |

| SCALE        | DATE      | DRAWN BY    |
|--------------|-----------|-------------|
| 1/8" = 1'-0" | JUNE 2026 | VICTOR OMEH |

| SHEET NAME. SECTION     | SHEET NO. |
|-------------------------|-----------|
| PROJECT NO. VO-2026-104 | A3.0      |

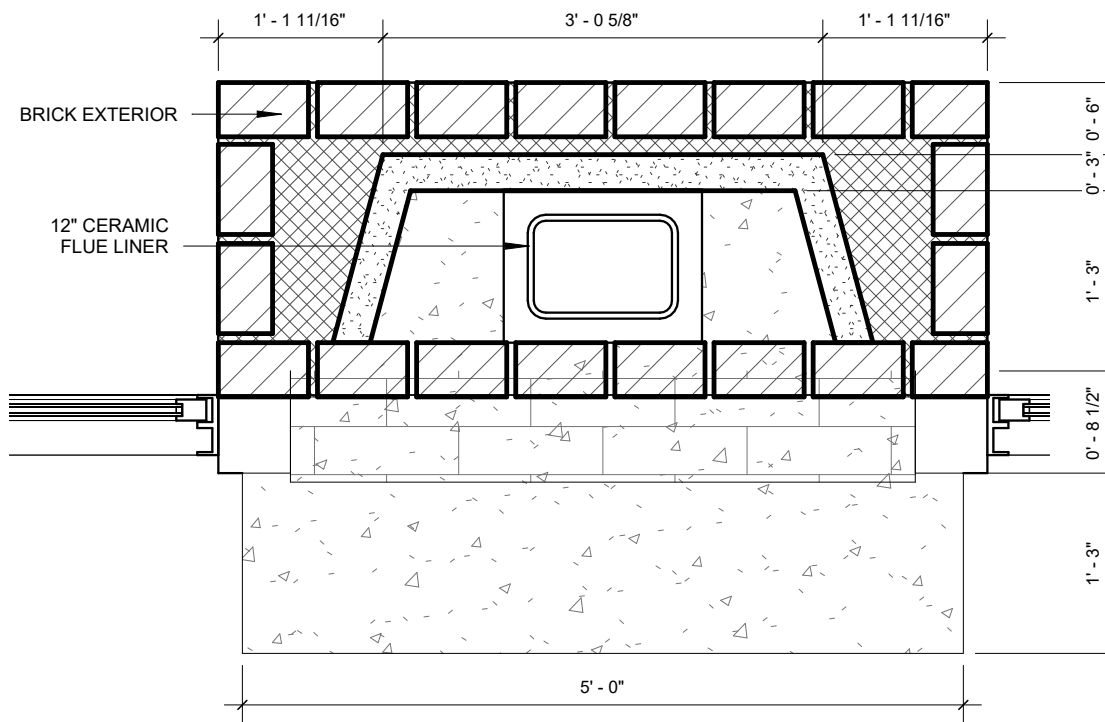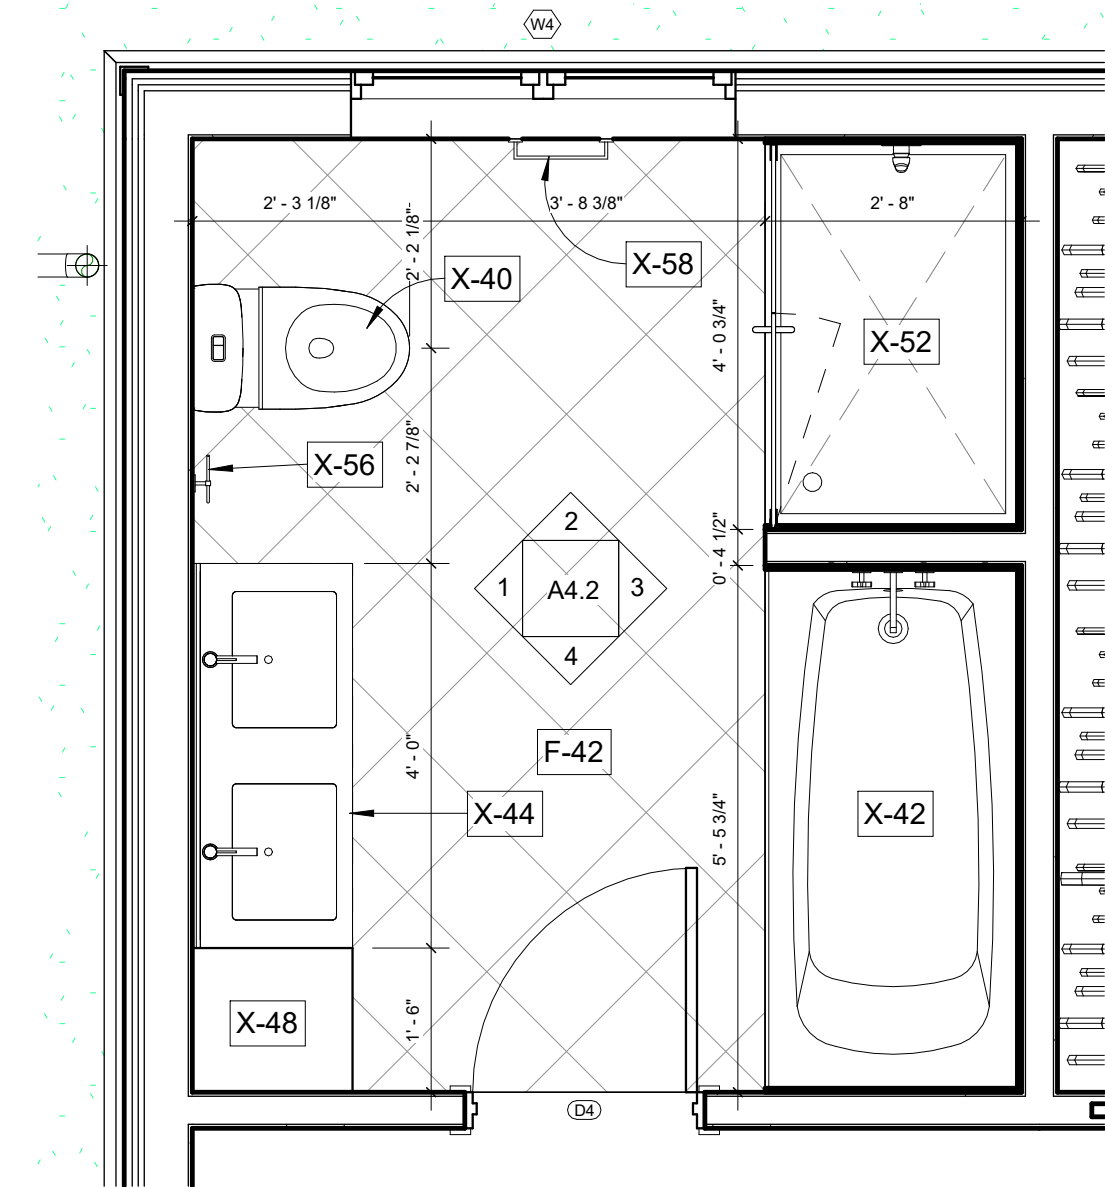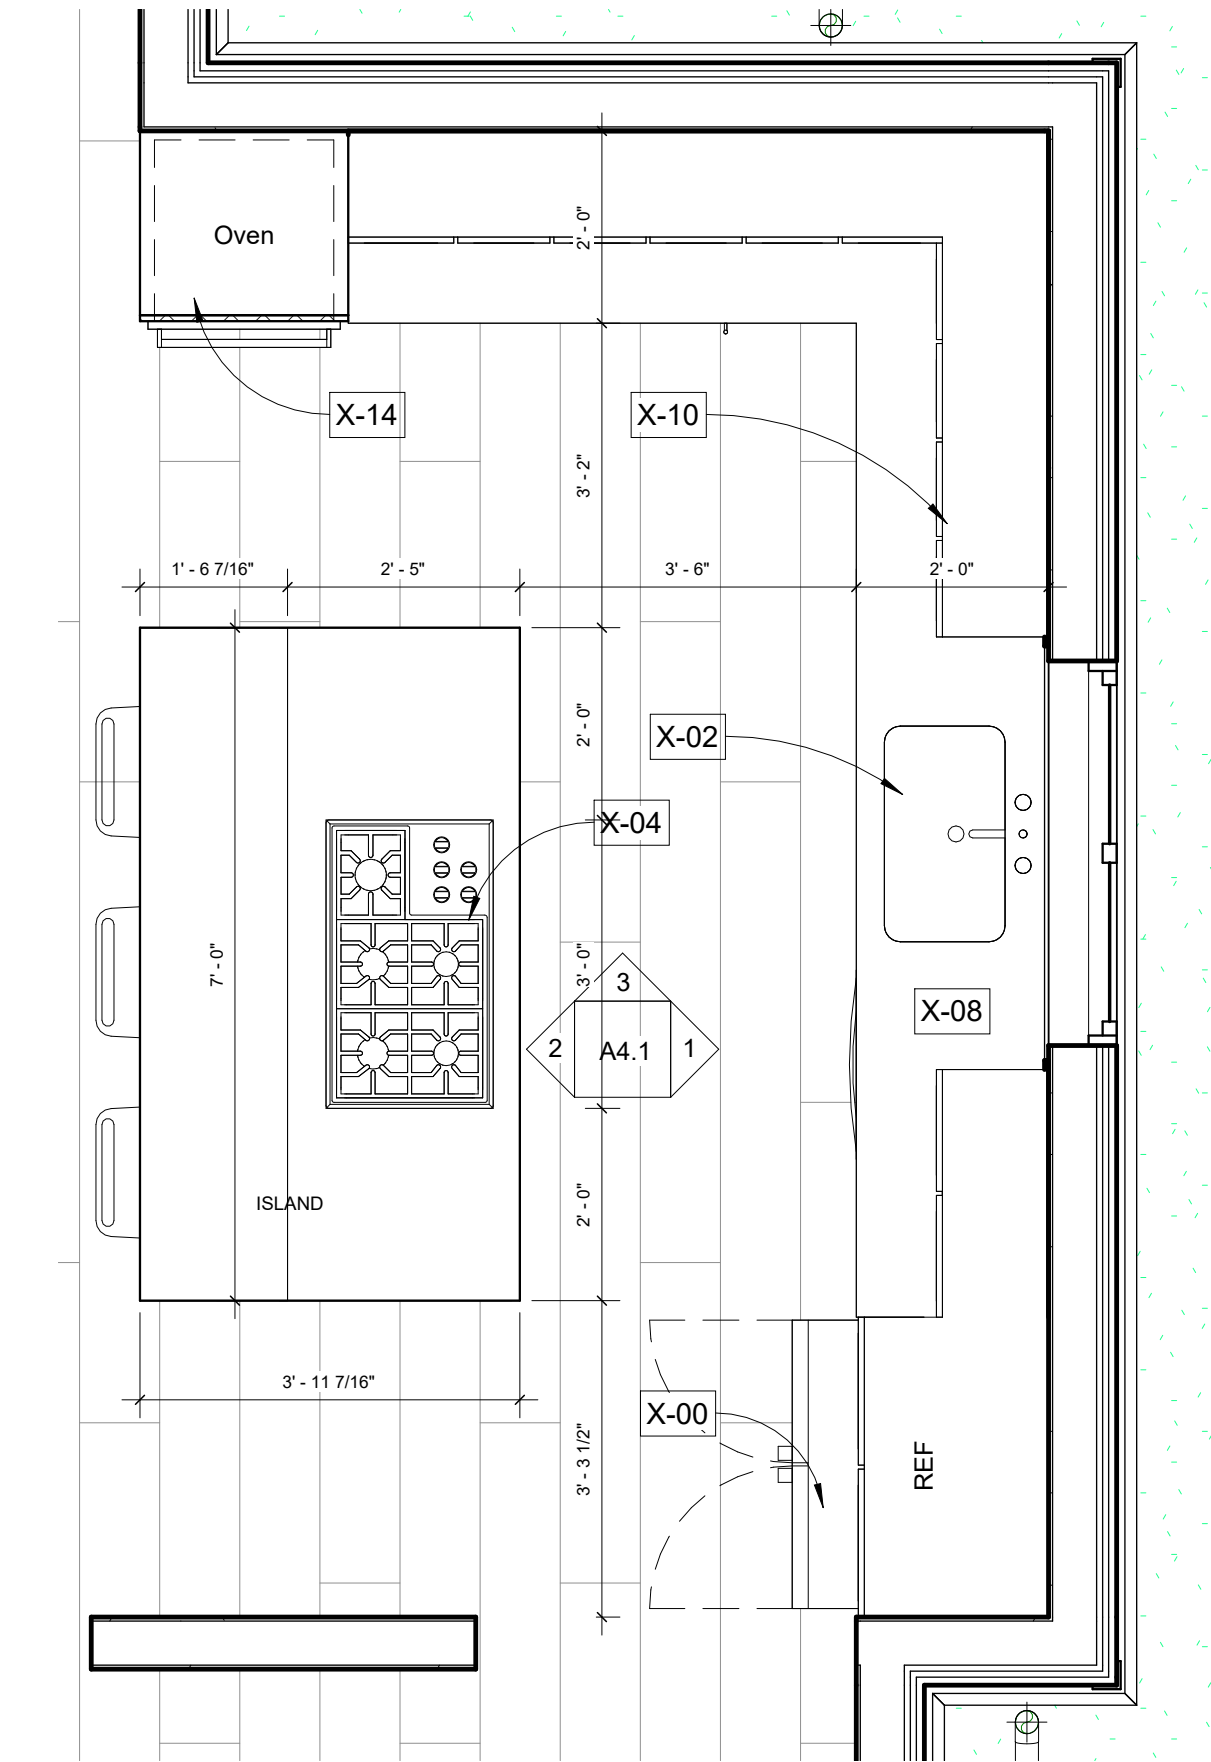

NOTES:

|     |             |    |      |
|-----|-------------|----|------|
| B   | Y REVISED   | JS |      |
| A   | X REVISED   | JS |      |
| REV | DESCRIPTION | BY | DATE |

AMENDMENTS

|                             |                              |  |  |
|-----------------------------|------------------------------|--|--|
| ARCHITECT'S CONTACT DETAILS |                              |  |  |
| NAME:                       | VICTOR O.                    |  |  |
| EMAIL:                      | omehvictor@gmail.com         |  |  |
| WEBSITE:                    | https://victoromeh.github.io |  |  |


|                                             |
|---------------------------------------------|
| PROJECT TITLE                               |
| 3 BEDROOM SINGLE-STORY RESIDENCE WITH ATTIC |

|                                              |
|----------------------------------------------|
| SITE                                         |
| 2841 BIRCHWOOD COURT, MURFREESBORO, TN 37129 |


|                        |
|------------------------|
| CLIENT                 |
| THOMAS & RACHEL MERCER |

|              |           |             |
|--------------|-----------|-------------|
| SCALE        | DATE      | DRAWN BY.   |
| As indicated | JUNE 2026 | VICTOR OMEH |


|                           |           |
|---------------------------|-----------|
| SHEET NAME. CALLOUT PLANS | SHEET NO. |
| PROJECT NO. VO-2026-104   | A4.0      |

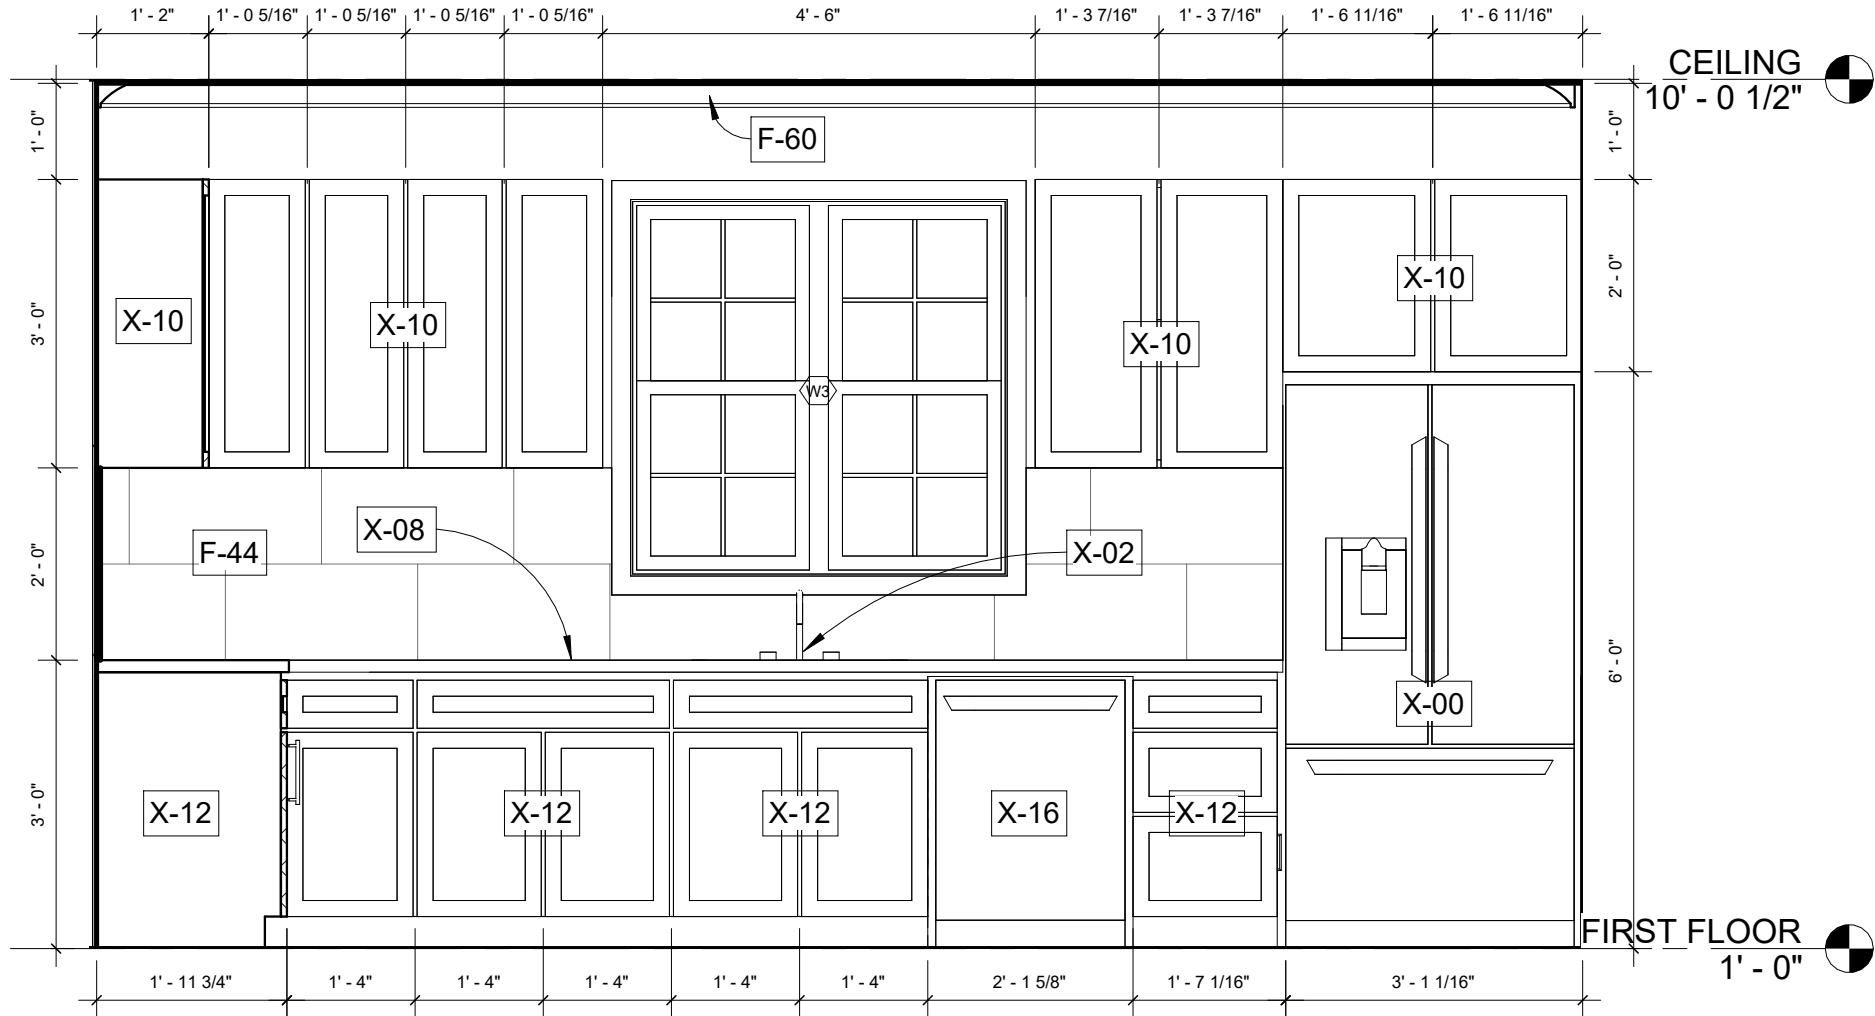

1 KITCHEN ELEVATION 1  
1/2" = 1'-0"

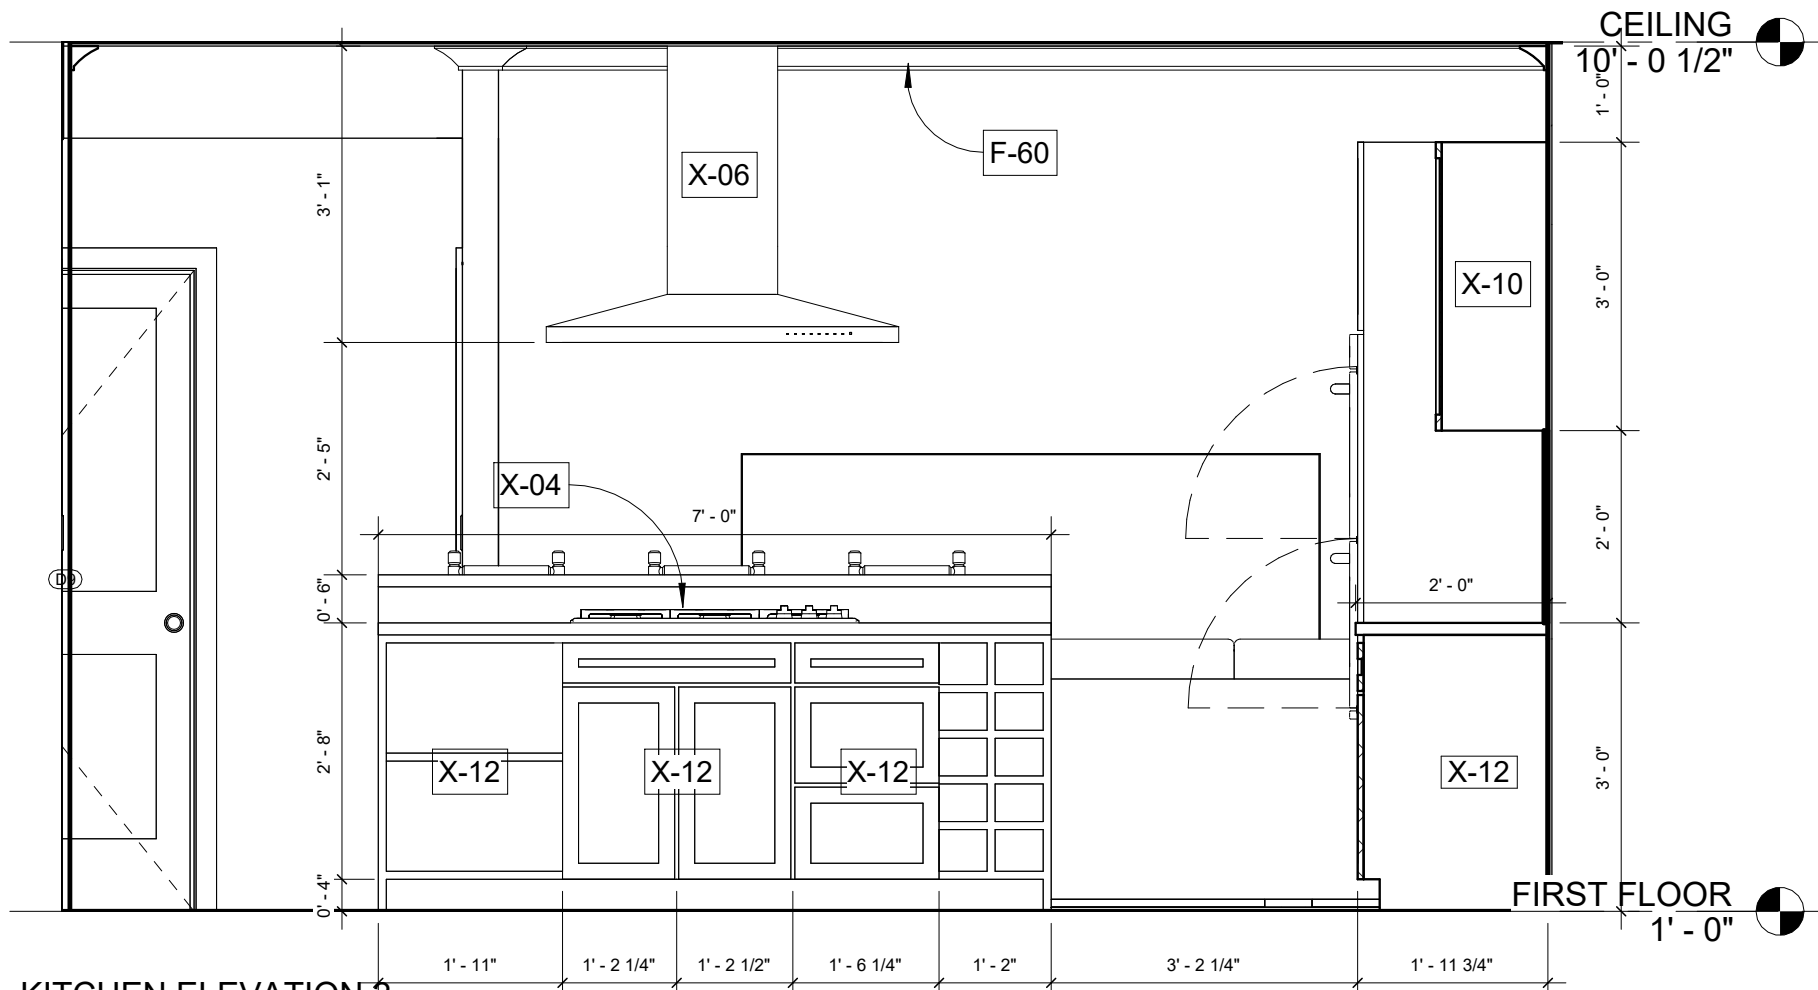

2 KITCHEN ELEVATION 2  
1/2" = 1'-0"

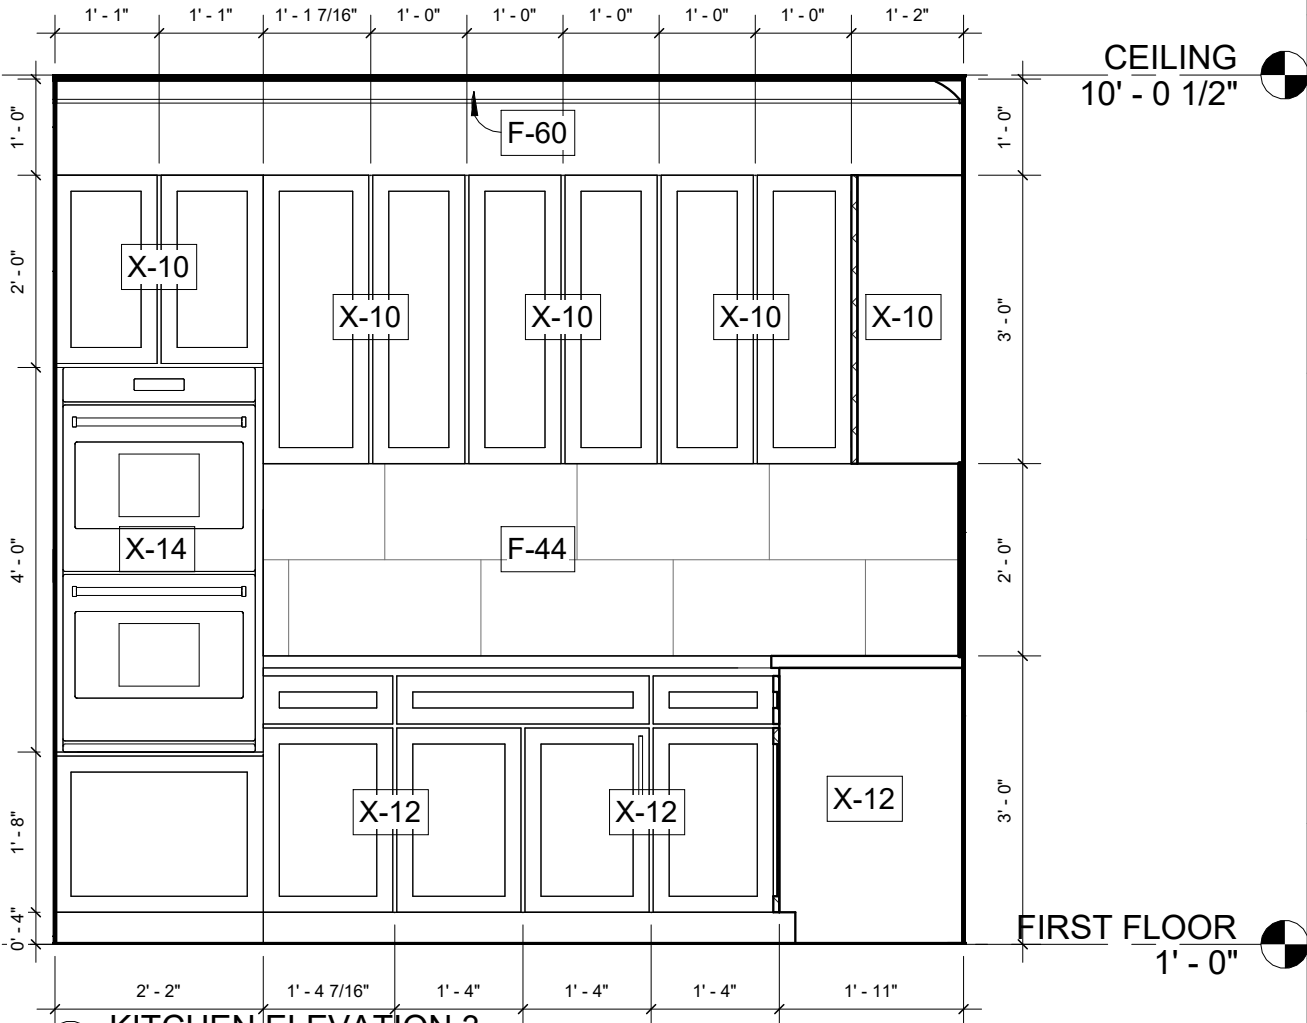


3 KITCHEN ELEVATION 3  
1/2" = 1'-0"


NOTES:

| B   | Y REVISED   | JS |      |
|-----|-------------|----|------|
| A   | X REVISED   | JS |      |
| REV | DESCRIPTION | BY | DATE |


| AMENDMENTS                                      |                              |                |
|-------------------------------------------------|------------------------------|----------------|
| ARCHITECT'S CONTACT DETAILS                     |                              |                |
| NAME:                                           | VICTOR O.                    |                |
| EMAIL:                                          | omehvictor@gmail.com         |                |
| WEBSITE:                                        | https://victoromeh.github.io |                |
| PROJECT TITLE                                   |                              |                |
| 3 BEDROOM SINGLE-STORY<br>RESIDENCE WITH ATTIC  |                              |                |
| SITE                                            |                              |                |
| 2841 BIRCHWOOD COURT,<br>MURFREESBORO, TN 37129 |                              |                |
| CLIENT                                          |                              |                |
| THOMAS & RACHEL MERCER                          |                              |                |
| SCALE                                           | DATE                         | DRAWN BY.      |
| 1/2" =<br>1'-0"                                 | JUNE 2026                    | VICTOR<br>OMEH |
| SHEET NAME. INTERIOR<br>ELEVATION(KITCHEN)      |                              | SHEET NO.      |
| PROJECT NO. VO-2026-104                         |                              | A4.1           |

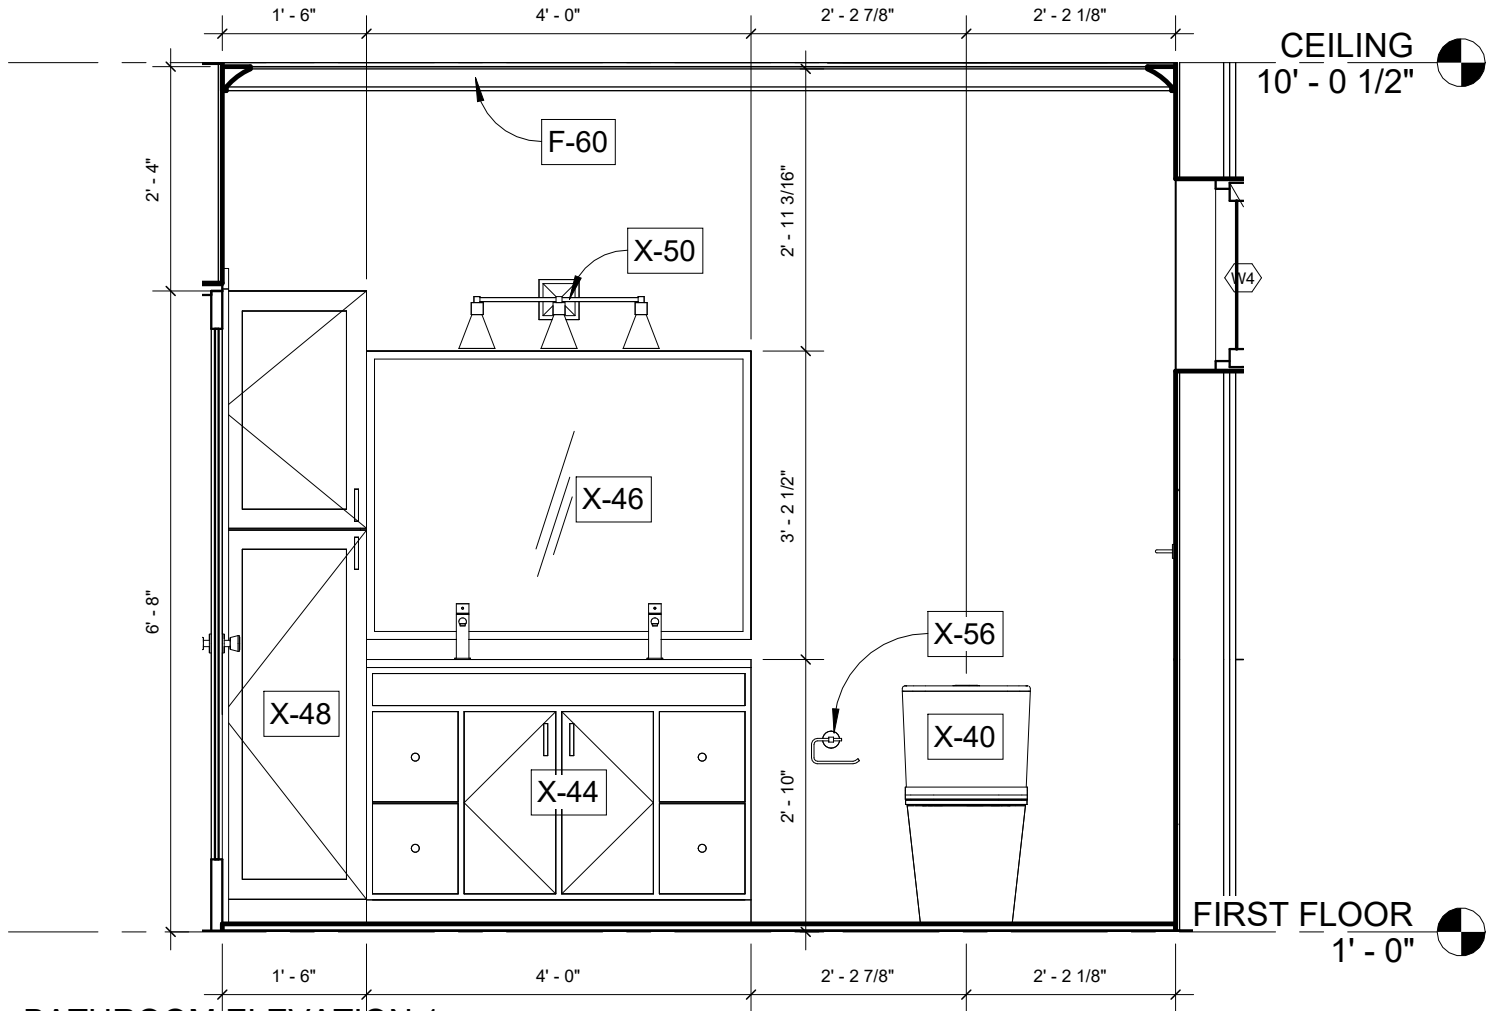


1 BATHROOM ELEVATION 1  
1/2" = 1'-0"

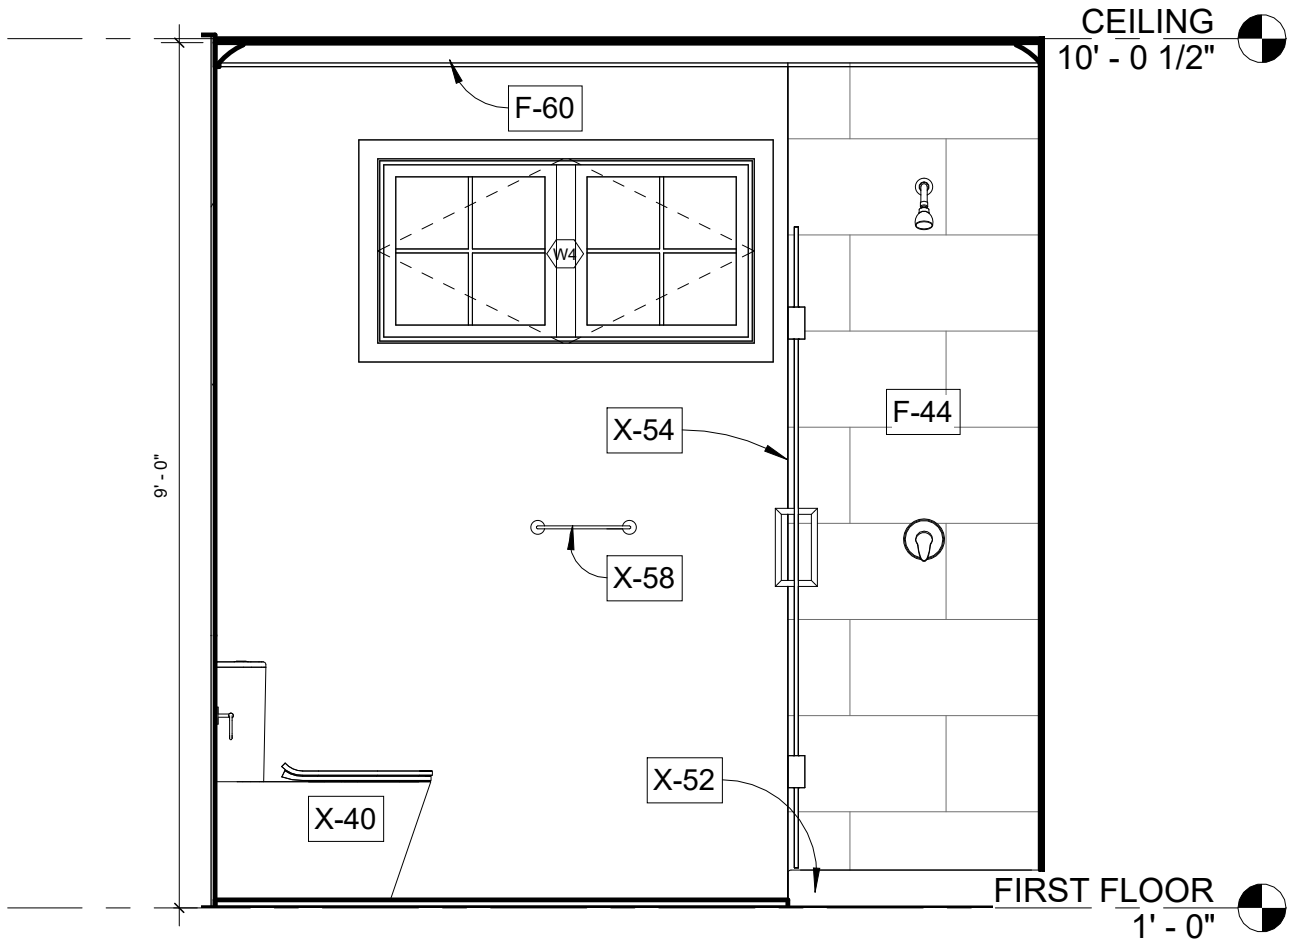

2 BATHROOM ELEVATION 2  
1/2" = 1'-0"

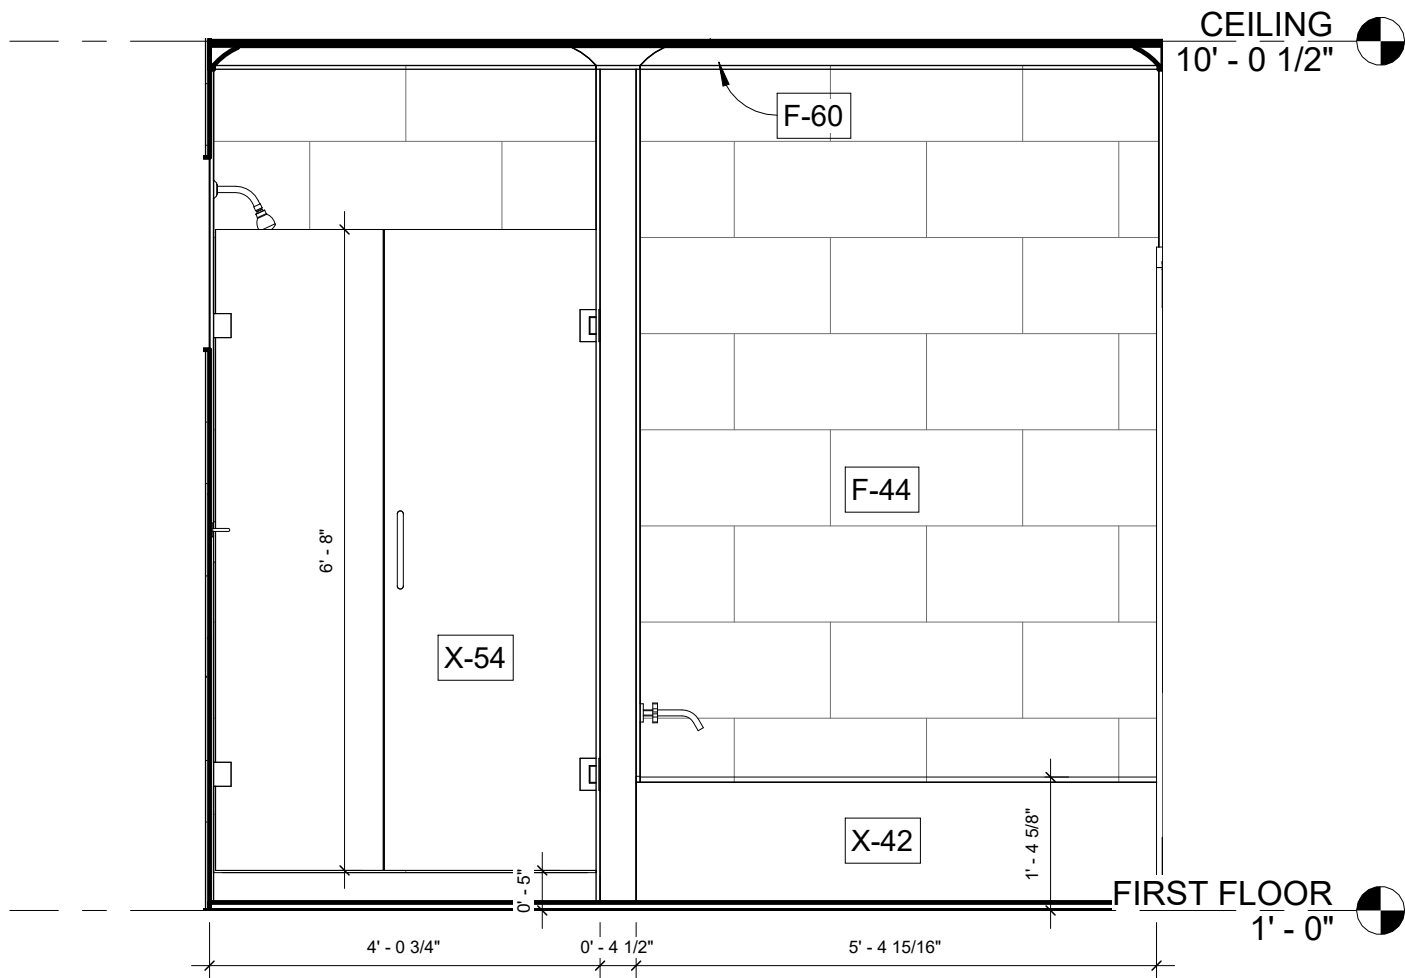

3 BATHROOM ELEVATION 3  
1/2" = 1'-0"

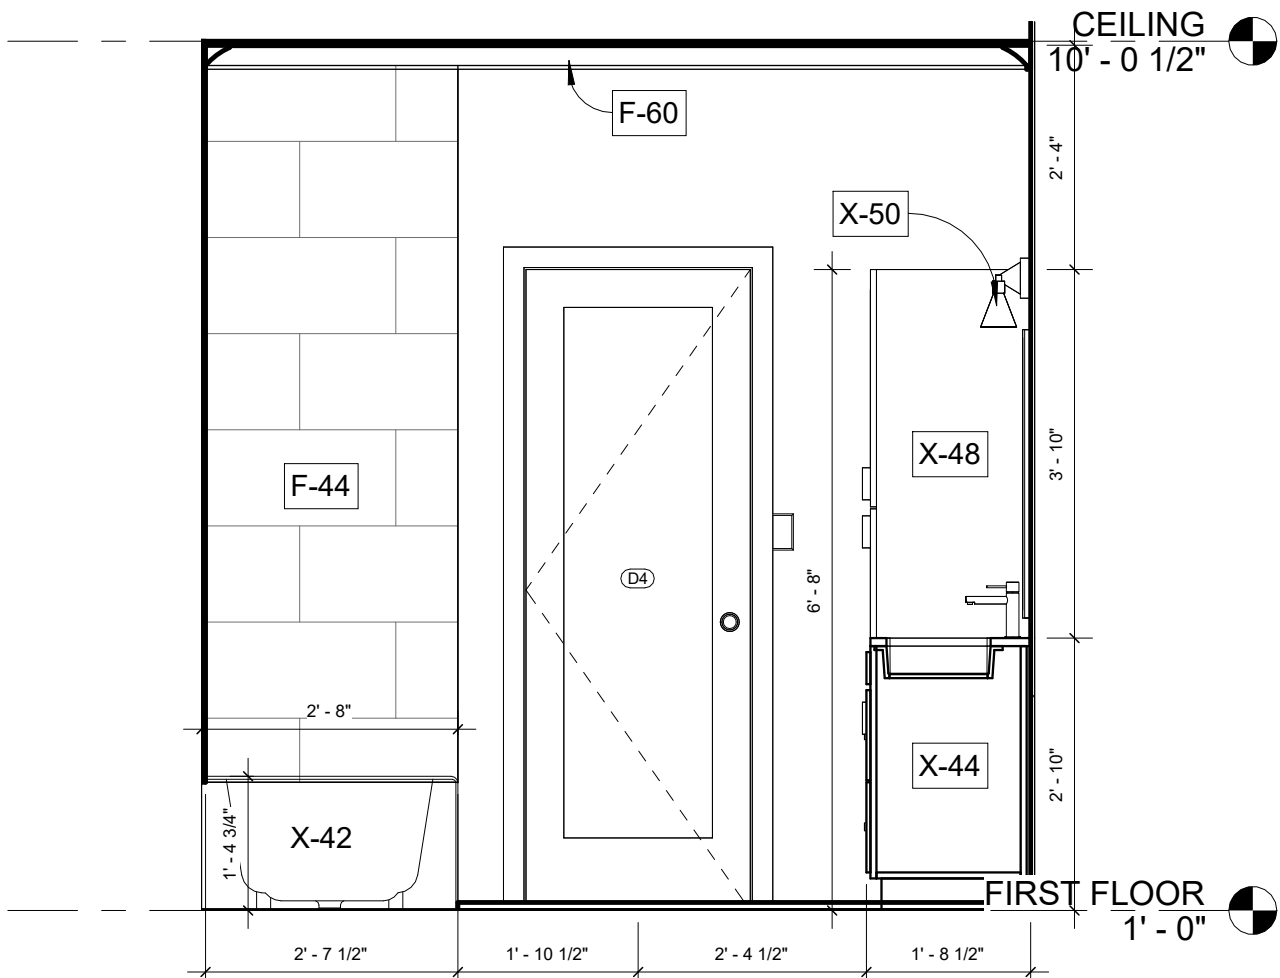

4 BATHROOM ELEVATION 4  
1/2" = 1'-0"

NOTES:

| B   | Y REVISED   | JS |      |
|-----|-------------|----|------|
| A   | X REVISED   | JS |      |
| REV | DESCRIPTION | BY | DATE |

AMENDMENTS

| ARCHITECT'S CONTACT DETAILS |                              |  |  |
|-----------------------------|------------------------------|--|--|
| NAME:                       | VICTOR O.                    |  |  |
| EMAIL:                      | omehvictor@gmail.com         |  |  |
| WEBSITE:                    | https://victoromeh.github.io |  |  |



| PROJECT TITLE                               |
|---------------------------------------------|
| 3 BEDROOM SINGLE-STORY RESIDENCE WITH ATTIC |

| SITE                                         |
|----------------------------------------------|
| 2841 BIRCHWOOD COURT, MURFREESBORO, TN 37129 |


| CLIENT                 |
|------------------------|
| THOMAS & RACHEL MERCER |

| SCALE        | DATE      | DRAWN BY.   |
|--------------|-----------|-------------|
| 1/2" = 1'-0" | JUNE 2026 | VICTOR OMEH |


| SHEET NAME                   | SHEET NO.   |
|------------------------------|-------------|
| INTERIOR ELEVATION(BATHROOM) | A4.2        |
| PROJECT NO.                  | VO-2026-104 |

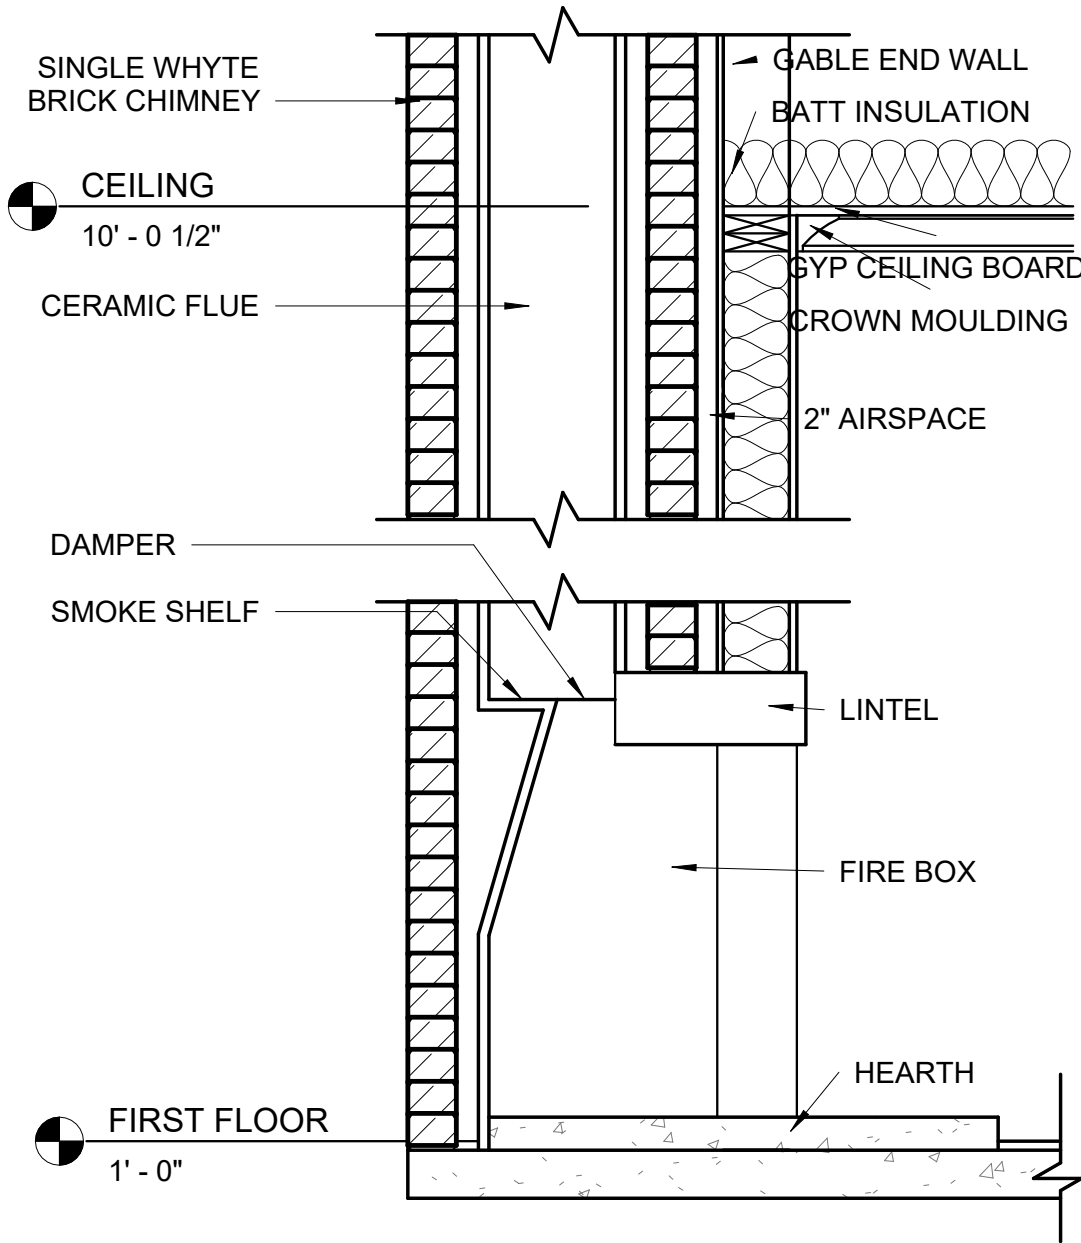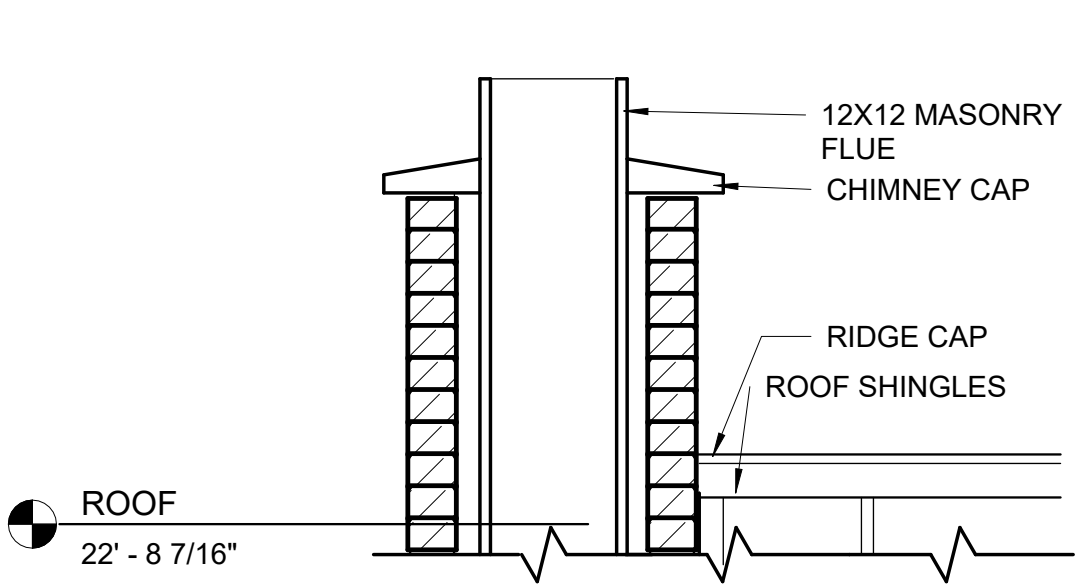


1 DETAIL SECTION THROUGH CHIMNEY  
3/4" = 1'-0"

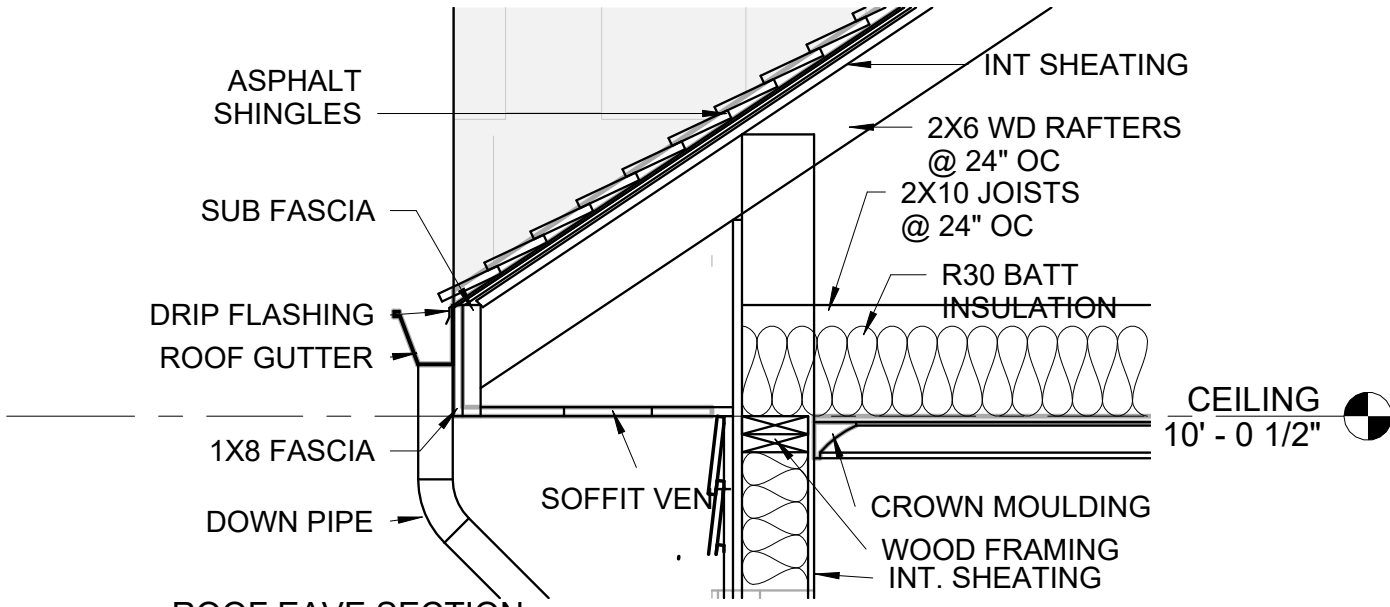


5 ROOF EAVE SECTION  
3/4" = 1'-0"

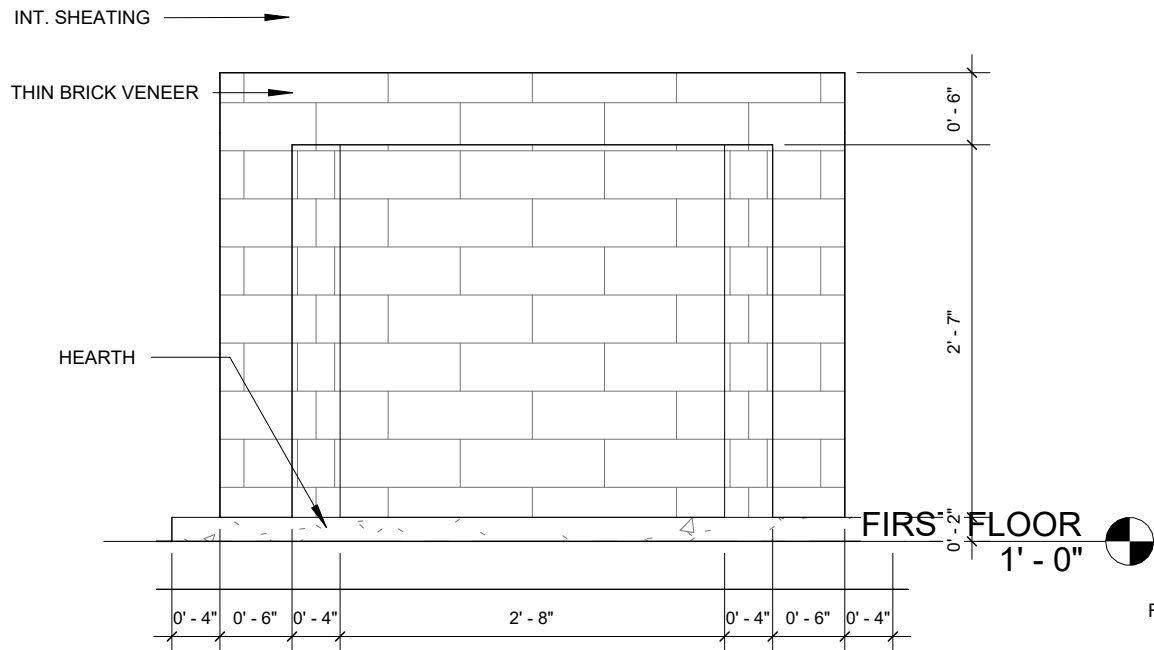


2 CHIMNEY ELEVATION  
3/4" = 1'-0"

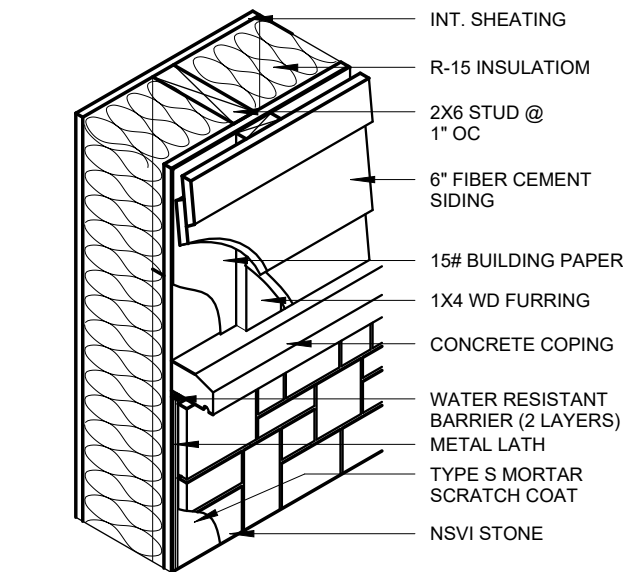


6 TYP EXT WALL  
1" = 1'-0"

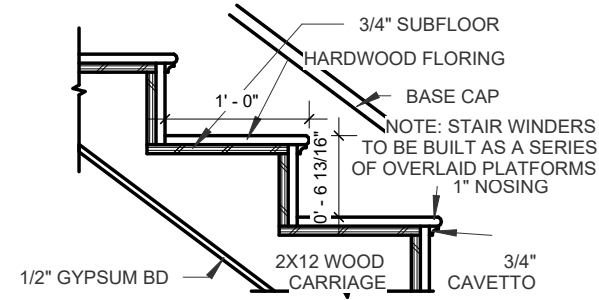

4 ATTIC STAIR SECTION DETAIL  
3/4" = 1'-0"

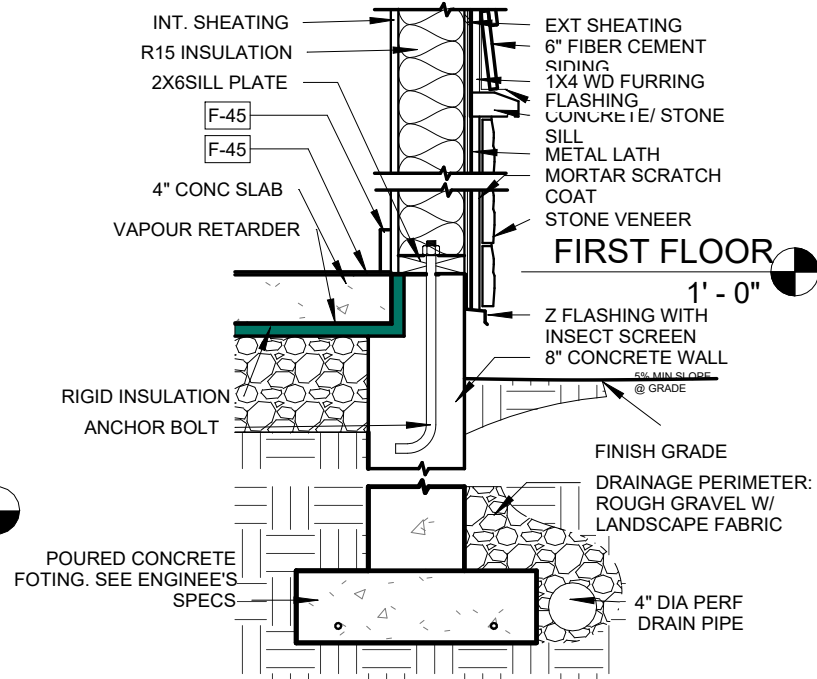

3 FOUNDATION DETAIL  
3/4" = 1'-0"

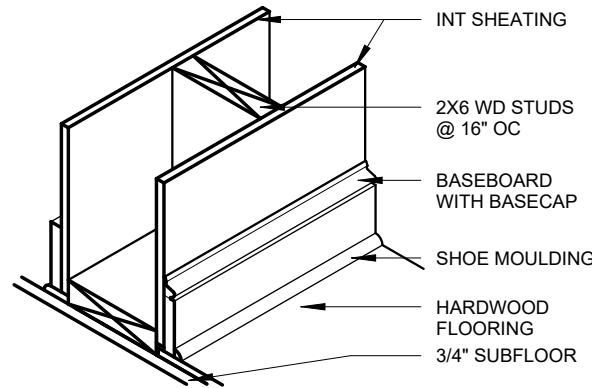

7 TYP INT WALL  
1" = 1'-0"

NOTES:

| REV | DESCRIPTION | BY | DATE |
|-----|-------------|----|------|
| B   | Y REVISED   | JS |      |
| A   | X REVISED   | JS |      |

AMENDMENTS

| ARCHITECT'S CONTACT DETAILS |                              |  |  |
|-----------------------------|------------------------------|--|--|
| NAME:                       | VICTOR O.                    |  |  |
| EMAIL:                      | omehvictor@gmail.com         |  |  |
| WEBSITE:                    | https://victoromeh.github.io |  |  |


| PROJECT TITLE                               |
|---------------------------------------------|
| 3 BEDROOM SINGLE-STORY RESIDENCE WITH ATTIC |

| SITE                                            |
|-------------------------------------------------|
| 2841 BIRCHWOOD COURT,<br>MURFREESBORO, TN 37129 |

| CLIENT                 |
|------------------------|
| THOMAS & RACHEL MERCER |

| SCALE        | DATE      | DRAWN BY    |
|--------------|-----------|-------------|
| As indicated | JUNE 2026 | VICTOR OMEH |

| SHEET NAME. TYPICAL DETAILS | SHEET NO. |
|-----------------------------|-----------|
| PROJECT NO. VO-2026-104     | A5.0      |

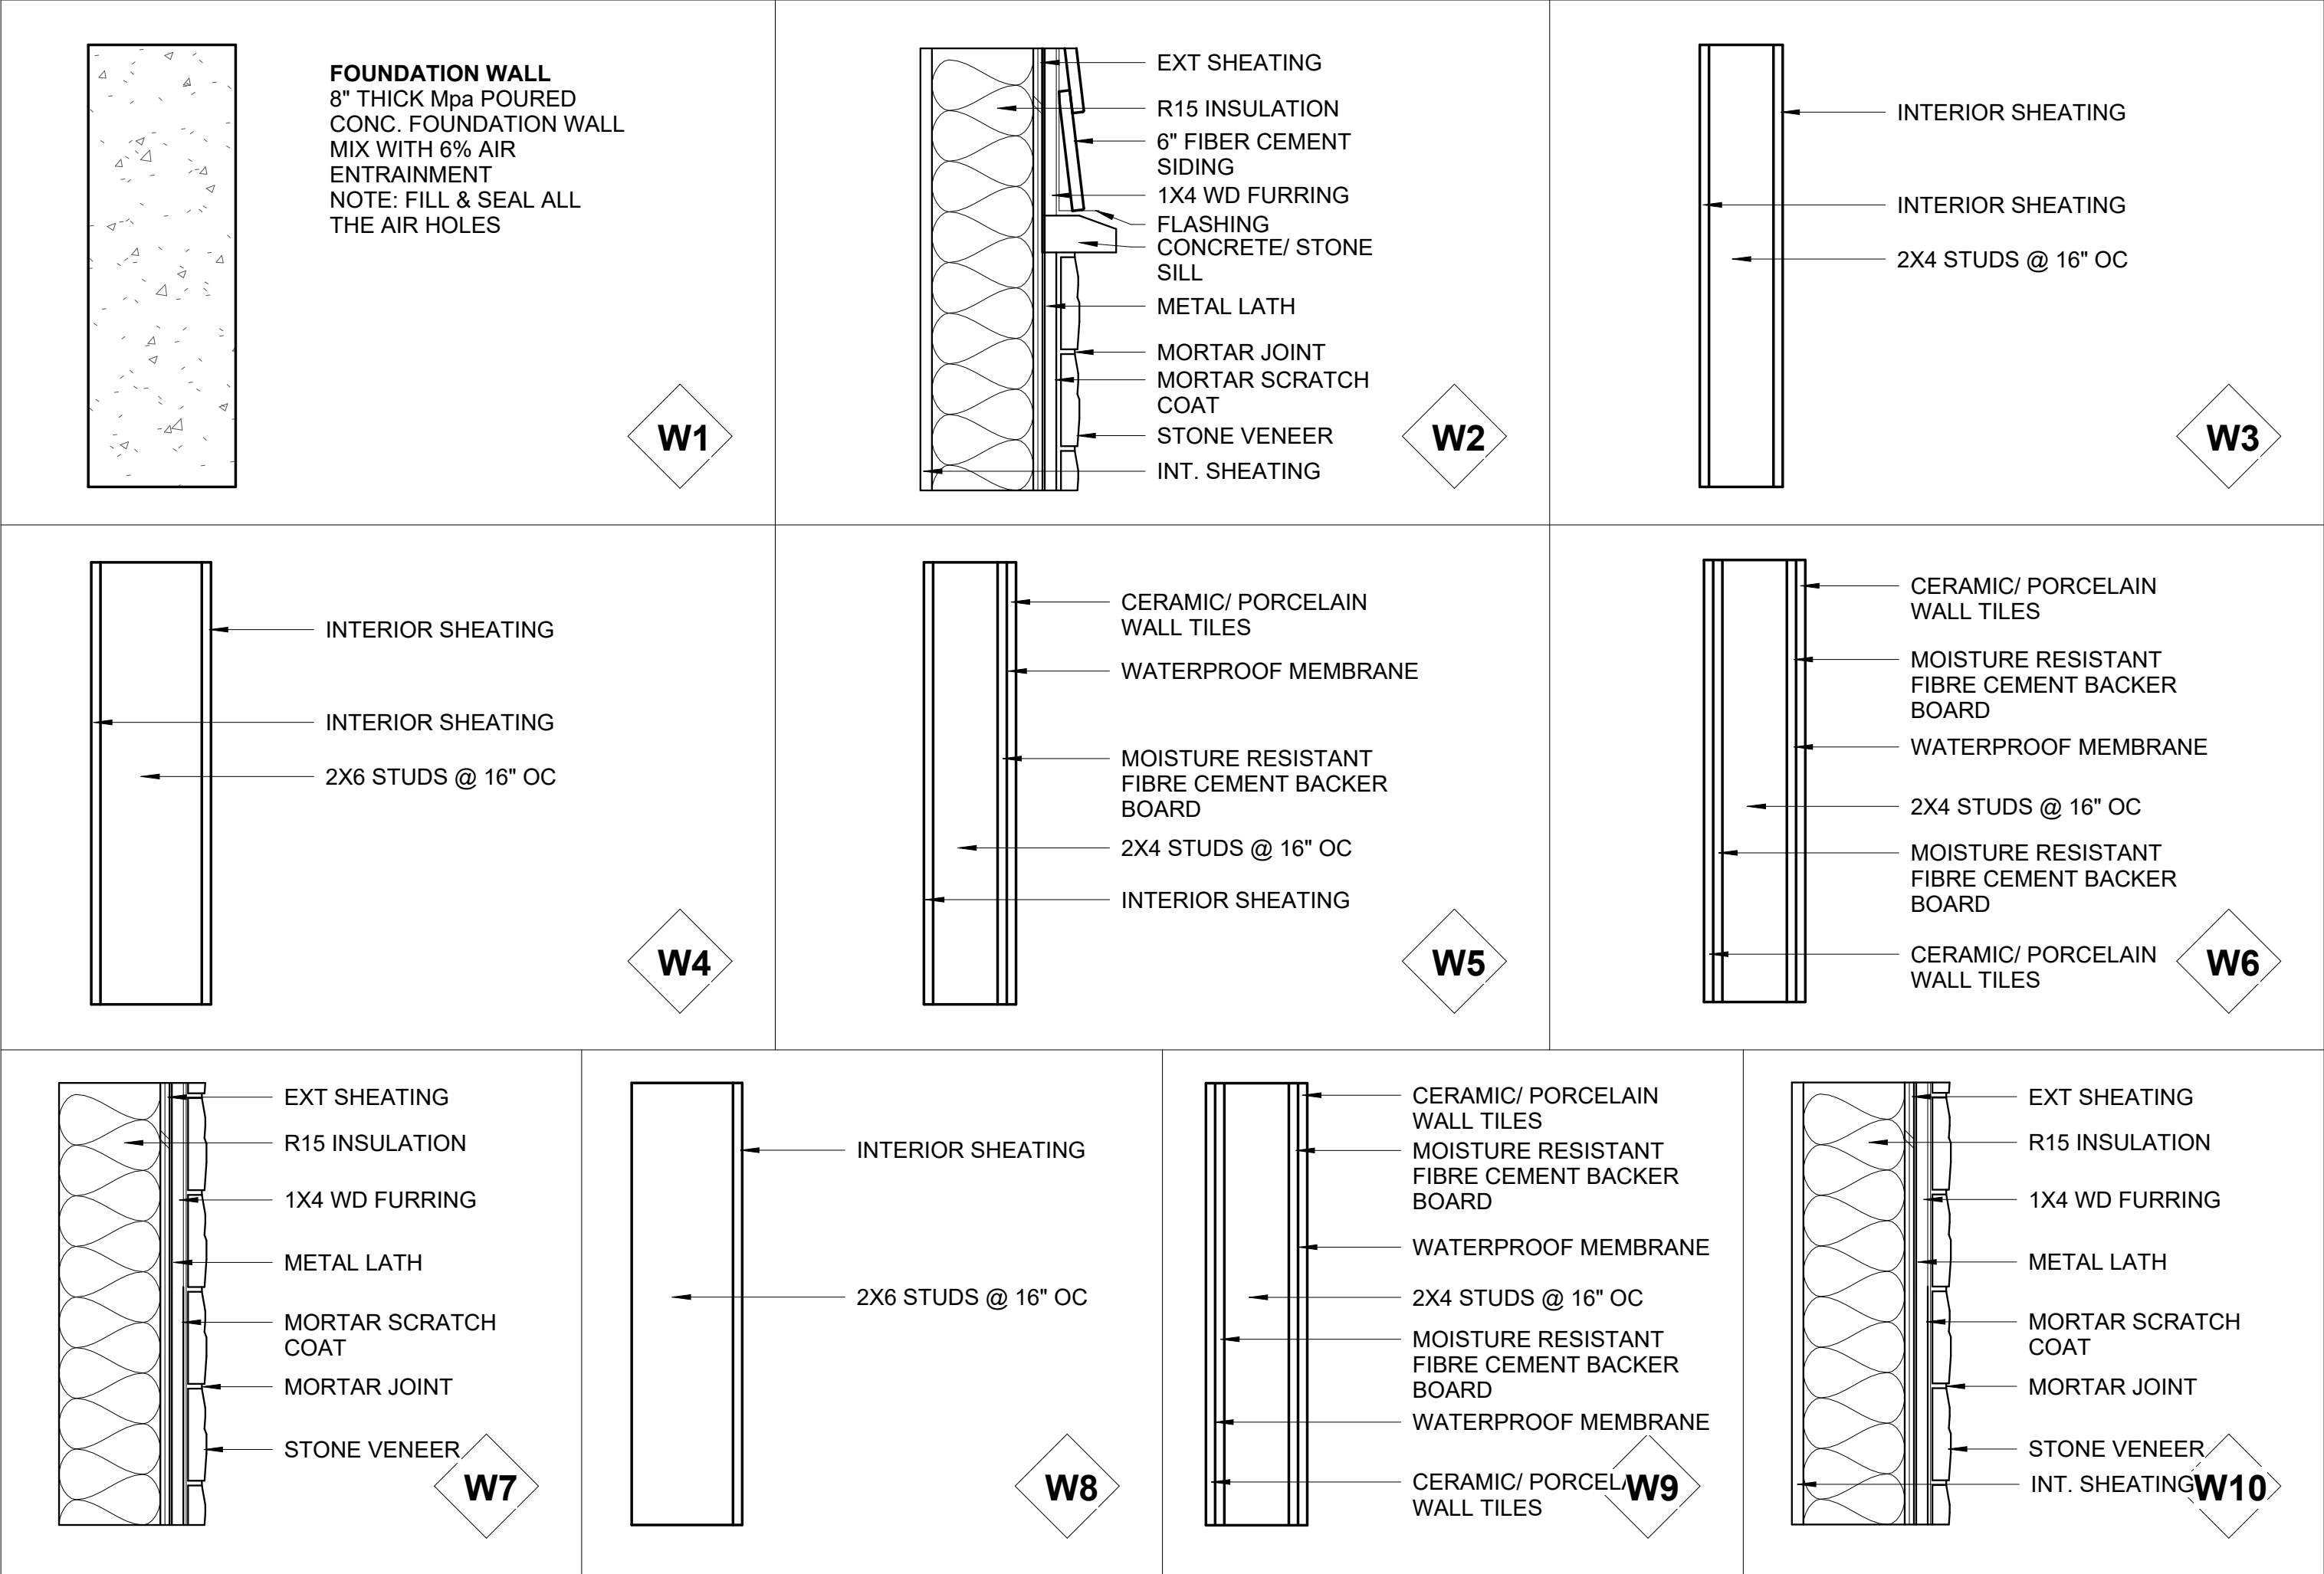

| NOTES: |  |  |  |
|--------|--|--|--|
|        |  |  |  |
|        |  |  |  |
|                |    |    |    |    |    |    |    |    |    |     |
|----------------|----|----|----|----|----|----|----|----|----|-----|
| PLAN VIEW      |    |    |    |    |    |    |    |    |    |     |
| ELEVATION VIEW |    |    |    |    |    |    |    |    |    |     |
| DOOR TAG       | D1 | D2 | D3 | D4 | D5 | D6 | D7 | D8 | D9 | D10 |

|                |     |     |     |
|----------------|-----|-----|-----|
| PLAN VIEW      |     |     |     |
| ELEVATION VIEW |     |     |     |
| DOOR TAG       | D11 | D12 | D13 |

 DOOR LEGEND  
1/8" = 1'-0"

|                |    |    |    |    |
|----------------|----|----|----|----|
| PLAN VIEW      |    |    |    |    |
| ELEVATION VIEW |    |    |    |    |
| WINDOW TAG     | W1 | W2 | W3 | W4 |

 WINDOW LEGEND  
1/8" = 1'-0"

| ROOM SCHEDULE |                  |        |                |                     |                                     |                |                     |
|---------------|------------------|--------|----------------|---------------------|-------------------------------------|----------------|---------------------|
| Number        | Name             | Area   | Ceiling Height | Floor Finish        | Wall Finish                         | Ceiling Finish | Comments            |
| 1             | ENT. PORCH       | 34 SF  | 9' - 4"        | Concrete            | Brick Veneer                        | Fiber Cement   | Unheated            |
| 2             | FOYER            | 99 SF  | 9' - 0"        | Engineered Hardwood | Gypsum Board/ Paint                 | Gypsum Board   | Unheated            |
| 3             | DINNING ROOM     | 171 SF | 9' - 0"        | Engineered Hardwood | Gypsum Board/ Paint                 | Gypsum Board   | Unheated            |
| 4             | KITCHEN          | 148 SF | 9' - 0"        | Engineered Hardwood | Gypsum Board/ Paint                 | Gypsum Board   | Unheated            |
| 5             | LIVING ROOM      | 381 SF | 9' - 0"        | Engineered Hardwood | Gypsum Board/ Paint                 | Gypsum Board   | Unheated            |
| 6             | HALF BATH        | 29 SF  | 9' - 0"        | Ceramic/ Porcelain  | Moisture Resistant Gyp Board/ Paint | Gypsum Board   | Waterproof Membrane |
| 7             | CLOSET           | 11 SF  | 9' - 0"        | Engineered Hardwood | Gypsum Board/ Paint                 | Gypsum Board   | Unheated            |
| 8             | BATHROOM         | 66 SF  | 9' - 0"        | Ceramic/ Porcelain  | Moisture Resistant Gyp Board/ Paint | Gypsum Board   | Waterproof Membrane |
| 9             | LAUNDRY/ UTILITY | 213 SF | 9' - 0"        | Ceramic/ Porcelain  | Gypsum Board/ Paint                 | Gypsum Board   | Waterproof Membrane |
| 10            | LOBBY            | 95 SF  | 9' - 0"        | Engineered Hardwood | Unfinished                          | Gypsum Board   | Unheated            |
| 11            | BEDROOM 2        | 141 SF | 9' - 0"        | Engineered Hardwood | Gypsum Board/ Paint                 | Gypsum Board   | Unheated            |
| 12            | CL.              | 14 SF  | 9' - 0"        | Engineered Hardwood | Gypsum Board/ Paint                 | Gypsum Board   | Unheated            |
| 13            | BEDROOM 3        | 152 SF | 9' - 0"        | Engineered Hardwood | Gypsum Board/ Paint                 | Gypsum Board   | Unheated            |
| 14            | CLOSET           | 22 SF  | 9' - 0"        | Engineered Hardwood | Gypsum Board/ Paint                 | Gypsum Board   | Unheated            |
| 15            | STR              | 6 SF   | 9' - 0"        | Engineered Hardwood | Gypsum Board/ Paint                 | Gypsum Board   | Unheated            |
| 16            | MASTER BEDROOM   | 225 SF | 9' - 0"        | Engineered Hardwood | Gypsum Board/ Paint                 | Gypsum Board   | Unheated            |
| 17            | MASTER BATH      | 84 SF  | 9' - 0"        | Ceramic/ Porcelain  | Moisture Resistant Gyp Board/ Paint | Gypsum Board   | Waterproof Membrane |
| 18            | WALK-IN CL.      | 69 SF  | 9' - 0"        | Engineered Hardwood | Gypsum Board/ Paint                 | Gypsum Board   | Unheated            |
| 19            | GARAGE           | 631 SF | 8' - 0"        | Epoxy/ Polyaspatic  | Painted CMU/ Gypsum                 | Gypsum Board   | Unheated            |
| 20            | COVERED PATIO    | 209 SF | VAULTED        | Concrete            | Fiber Cement/ BrickVeneer           | Fiber Cement   | Unheated            |
| 21            | UNFINISHED ATTIC | 336 SF | Unfinished     | Unfinished          | Gypsum Board/ Paint                 | Gypsum Board   | -                   |
| 22            | EXIT PORCH       | 76 SF  | 9' - 4"        | Concrete            | Fiber Cement/ BrickVeneer           | Fiber Cement   | Unheated            |

NOTES:

|     |             |    |      |
|-----|-------------|----|------|
| B   | Y REVISED   | JS |      |
| A   | X REVISED   | JS |      |
| REV | DESCRIPTION | BY | DATE |

| AMENDMENTS                                      |                              |                                 |
|-------------------------------------------------|------------------------------|---------------------------------|
| ARCHITECT'S CONTACT DETAILS                     |                              |                                 |
| NAME:                                           | VICTOR O.                    |                                 |
| EMAIL:                                          | omehvictor@gmail.com         |                                 |
| WEBSITE:                                        | https://victoromeh.github.io |                                 |
| PROJECT TITLE                                   |                              |                                 |
| 3 BEDROOM SINGLE-STORY<br>RESIDENCE WITH ATTIC  |                              |                                 |
| SITE                                            |                              |                                 |
| 2841 BIRCHWOOD COURT,<br>MURFREESBORO, TN 37129 |                              |                                 |
| CLIENT                                          |                              |                                 |
| THOMAS & RACHEL MERCER                          |                              |                                 |
| SCALE<br><br>1/8" =<br>1'-0"                    | DATE.<br><br>JUNE 2026       | DRAWN BY.<br><br>VICTOR<br>OMEH |
| SHEET NAME. DOORS &<br>WINDOWS                  |                              | SHEET NO.<br><br>A6.0           |
| PROJECT NO. VO-2026-104                         |                              |                                 |

| WINDOW SCHEDULE |                   |                  |                |     |                                                          |                  |             |        |                       |
|-----------------|-------------------|------------------|----------------|-----|----------------------------------------------------------|------------------|-------------|--------|-----------------------|
| MARK            | SIZE              | ROUGH<br>OPENING | SILL<br>HEIGHT | QTY | LOCATION                                                 | MATERIAL         | OPERATION   | EGRESS | W_COMMENTS            |
| W1              | 4' - 6" X 4' - 6" | 56" X 56<br>1/2" | VARIES         | 8   | MASTER BEDROOM, BEDRRROM 2 & 3,<br>ATTIC, DINNING,GARAGE | COMPOSITE/ VINYL | DOUBLE HUNG | Yes    | EXTERIOR LOW-E GLASS  |
| W2              | 2' - 6" X 4' - 6" | 72" X 56<br>1/2" | 3' 4"          | 3   | DINING ROOM, MASTER BEDROOM                              | COMPOSITE/ VINYL | DOUBLE HUNG | Yes    | EXTERIOR LOW-E GLASS  |
| W3              | 4' - 0" X 4' - 0" | 50" X 50<br>1/2" | 3' 10"         | 2   | KITCHEN, LAUNDRY/ UTILITY                                | COMPOSITE/ VINYL | DOUBLE HUNG | Yes    | ABOVE SINK            |
| W4              | 4' - 0" X 2' - 0" | 50" X 26<br>1/2" | 5' 10"         | 1   | PRIMARY BATHROOM                                         | COMPOSITE/ VINYL | AWNING      | No     | PRIVACY / VENTILATION |

| DOOR SCHEDULE |                       |                   |         |                                 |                               |                          |                |                                                  |
|---------------|-----------------------|-------------------|---------|---------------------------------|-------------------------------|--------------------------|----------------|--------------------------------------------------|
| MAR<br>K      | SIZE                  | ROUGH<br>OPENING  | QT<br>Y | LOCATION                        | MATERIAL                      | OPERATIO<br>N            | FIRE<br>RATING | COMMENTS                                         |
| D1            | 6' - 0" X 7' - 0"     | 74" X 86 1/2"     | 1       | ENT.PORCH                       | FIBERGLASS                    | SWING                    | -              | EXTERIOR INSULATED WITH GLASS SIDELITES          |
| D2            | 6' - 3 1/2" X 8' - 6" | 38" X 104 1/2"    | 2       | LIVING ROOM TO COVERED<br>PATIO | VINYL OR ALUMINUM CLAD, GLASS | SLIDING                  | -              | ENERGY STAR TEMPRED GLASS, SCREEN<br>OPTION      |
| D3            | 2' - 8" X 6' - 8"     | 34" X 82 1/2"     | 3       | LAUNDRY/UTILITY,<br>BATHROOM    | HOLLOW CORE WOOD              | POCKET<br>DOOR           | -              | MOISTURE RESISTANT CORE                          |
| D4            | 2' - 4" X 6' - 8"     | 30" X 82 1/2"     | 2       | PWDR ROOM / BATHROOM            | SOLID CORE WOOD OR MDF        | SWING                    | -              | MOISTURE RESISTANT CORE                          |
| D5            | 4' - 6" X 6' -8"      | 56" X 82 1/2"     | 1       | LAUNDRY CLOSET                  | HOLLOW CORE WOOD              | BI-FOLD                  | -              | FIRE-RATED SELF-CLOSING HARDWARE                 |
| D6            | 2' - 0" X 6' - 8"     | 26" X 82 1/2"     | 1       | STORAGE                         | HOLLOW CORE WOOD              | SWING                    | -              | ENERGY STAR TEMPRED GLASS, SCREEN<br>OPTION      |
| D7            | 3' - 0" X 6' - 8"     | 38" X 82 1/2"     | 2       | CLOSET                          | HOLLOW CORE WOOD              | DOUBLE<br>POCKET<br>DOOR | -              | STANDARD CLOSET DOOR                             |
| D8            | 6' - 0" X 6' - 8"     | 74" X 82 1/2"     | 1       | WALK-IN CLOSET                  | HOLLOW CORE WOOD              | SLIDING                  | -              | STANDARD CLOSET DOOR                             |
| D9            | 2' - 8" X 6' - 8"     | 34" X 82 1/2"     | 3       | BEDROOMS                        | SOLID CORE WOOD OR MDF        | SWING                    | -              | PRIVACY LOCKS, STANDARD INTERIOR                 |
| D10           | 2' - 10" X 7' - 0"    | 36" X 86 1/2      | 1       | GARGAE TO EXIT PORCH            | FIBERGLASS                    | SWING                    | -              | EXTERIOR INSULATED, EGRESS COMPLIANT             |
| D11           | 2' - 8" X 6' - 8"     | 34" X 82 1/2"     | 1       | GARAGE TO LOBBY                 | SOLID CORE WOOD OR MDF        | SWING                    | 20-MINUTE      | FIRE-RATED SELF-CLOSING HARDWARE                 |
| D12           | 2' - 8" X 6' - 4"     | 26" X 78 1/2"     | 1       | UNFINISHED ATTIC                | SOLID CORE WOOD OR MDF        | SWING                    | -              | STANDARD INTERIOR                                |
| D13           | 20' - 0" X 7' - 6"    | 20' - 2" X 7' -8" | 1       | GARAGE                          | STEEL (INSULATED)             | OVERHEA<br>D             | -              | INSULATED, AUTOMATIC OPENER, WINDOWS<br>OPTIONAL |

NOTES:

|                                                 |                        |                              |                                 |
|-------------------------------------------------|------------------------|------------------------------|---------------------------------|
| B                                               | Y REVISED              | JS                           |                                 |
| A                                               | X REVISED              | JS                           |                                 |
| REV                                             | DESCRIPTION            | BY                           | DATE                            |
| AMENDMENTS                                      |                        |                              |                                 |
| ARCHITECT'S CONTACT DETAILS                     |                        |                              |                                 |
| NAME:                                           |                        | VICTOR O.                    |                                 |
| EMAIL:                                          |                        | omehvictor@gmail.com         |                                 |
| WEBSITE:                                        |                        | https://victoromeh.github.io |                                 |
| PROJECT TITLE                                   |                        |                              |                                 |
| 3 BEDROOM SINGLE-STORY<br>RESIDENCE WITH ATTIC  |                        |                              |                                 |
| SITE                                            |                        |                              |                                 |
| 2841 BIRCHWOOD COURT,<br>MURFREESBORO, TN 37129 |                        |                              |                                 |
| CLIENT                                          |                        |                              |                                 |
| THOMAS & RACHEL MERCER                          |                        |                              |                                 |
| SCALE                                           | DATE.<br><br>JUNE 2026 |                              | DRAWN BY.<br><br>VICTOR<br>OMEH |
| SHEET NAME. SCHEDULES 1                         |                        |                              | SHEET NO.<br><br><b>A6.1</b>    |
| PROJECT NO. VO-2026-104                         |                        |                              |                                 |

|                                              |             |                              |             |  |
|----------------------------------------------|-------------|------------------------------|-------------|--|
| NOTES:                                       |             |                              |             |  |
|                                              |             |                              |             |  |
| B                                            | Y REVISED   | JS                           |             |  |
| A                                            | X REVISED   | JS                           |             |  |
| REV                                          | DESCRIPTION | BY                           | DATE        |  |
| AMENDMENTS                                   |             |                              |             |  |
| ARCHITECT'S CONTACT DETAILS                  |             |                              |             |  |
| NAME:                                        |             | VICTOR O.                    |             |  |
| EMAIL:                                       |             | omehvictor@gmail.com         |             |  |
| WEBSITE:                                     |             | https://victoromeh.github.io |             |  |
| PROJECT TITLE                                |             |                              |             |  |
| 3 BEDROOM SINGLE-STORY RESIDENCE WITH ATTIC  |             |                              |             |  |
| SITE                                         |             |                              |             |  |
| 2841 BIRCHWOOD COURT, MURFREESBORO, TN 37129 |             |                              |             |  |
| CLIENT                                       |             |                              |             |  |
| THOMAS & RACHEL MERCER                       |             |                              |             |  |
| SCALE                                        | DATE.       |                              | DRAWN BY.   |  |
|                                              | JUNE 2026   |                              | VICTOR OMEH |  |
| SHEET NAME. SCHEDULES 2                      |             |                              | SHEET NO.   |  |
| PROJECT NO. VO-2026-104                      |             |                              | A6.2        |  |

| FIXTURE AND EQUIPMENT SCHEDULE |                       |                               |                                                                                    |                                    |
|--------------------------------|-----------------------|-------------------------------|------------------------------------------------------------------------------------|------------------------------------|
| MARK                           | ITEM                  | SIZE/ DESCRIPTION             | NOTES/ SPECIFICATION                                                               | MAUFACTURER/ MODEL                 |
| X-00                           | REFRIDGERATOR         | 36" WIDE X 70" TALL           | ENERGY STAR CERTIFIED FRENCH DOOR OR SIDE BY SIDE LED LIGHTING WATER/ICE DISPENSER | BLOMBERG, GE OR EQUIVALENT         |
| X-02                           | KITCHEN SINK          | 33"X22" SINGLE BOWL 9" DEEP   | UNDERMOUNT STAINLESS STEEL NOISE DAMPEMING PADS INCLUDES STRAINER AND DISPOSAL     | KOHLER OR EQUIVALENT               |
| X-04                           | GAS HOB               | 36" WIDE, COUNTERTOP DROP IN  | STAINLESS STEEL, SELF-CLEANING CONVECTION OPTION                                   | GE SAMSUNG OR EQUIVALENT           |
| X-06                           | EXHAUST HOOD          | 44"X26" WIDE                  | CEILING MOUNTED, VENTED SENSOR COOKING                                             | GE OR EQUIVALENT                   |
| X-08                           | COUNTERTOP            | 1 1/2" THICK, VARIOUS LENGHTS | QUARTZ SLAB, NON POROUS, EASED OR BEVELED EDGE, LIGHT COLOR                        | CEASARSTONE, CAMBRIA OR EQUIVALENT |
| X-10                           | WALL CABINETS         | VARIOUS WIDTHS 36" HIGH       | PAINTED FINISH SOFT-CLOSE HINGES GLAZED DOORS PREFERRED ON SELECT CABINETS         | IKEA SEKTON OR SEMI-CUSTOM         |
| X-12                           | FLOOR CABINET         | 24" DEEP, 36 INCH HIGH        | SOFTCLOSE DRAWERS AND DOORS, QUARTZ COUNTERTOP                                     | MATCHING CABINET LINE              |
| X-14                           | MICROWAVE & OVEN      | 24"X48" SLIDE IN              | STAINLESS STEEL, SELF-CLEANING CONVECTION OPTION                                   | GE SAMSUNG OR EQUIVALENT           |
| X-16                           | DISHWASHER            | STANDARD 24"                  | QUIET OPERATION (45DB) ENERGY STAR STAINLESS TUB                                   | BOSCH OR KITCHEN AID               |
| X-40                           | WATER CLOSET (TOILET) | ELONGATED BOWL, 12" ROUGH IN  | 1.28 GPF, COMFORT HEIGHT (17"-19"), QUIET CLOSE SEAT                               | KOHLER, AMERICAN STANDARD          |
| X-42                           | BATHTUB               | 60"X30" OR 32" ALCOVE         | ACRYLIC INTEGRAL APRON, TEXTURED BOTTOM                                            | KOHLER                             |
| X44                            | BATHROOM VANITY       | 48"X20"X34                    | QUARTZ COUNTERTOP, UNDERMOUNT RECTANGULAR SINK, SOFT CLOSE                         | LOCAL CABINET OR IKEA              |
| X-46                           | MIRROR                | SIZED TO VANITY               | FRAMELESS, BEVELED EDGE, WALL MOUNTED                                              | -                                  |
| X-48                           | TALL CABINET          | 24"X20"X80"                   | ADJUSTABLE SHELVING OR PULOOUT ORGANIZERS                                          | MATCHING VANITY LINE               |
| X-50                           | MIRROR LIGHT          | -                             | LED, BRUSHED NICKEL OR CHROME FINISH, DIMMABLE                                     | PROGRESS LIGHTING OR EQUIVALENT    |
| X-52                           | SHOWER BASE/ TRAY     | CUSTOM                        | LOW PROFILE SLIP RESISTANT                                                         | MATCHING SHOWER SYSTEM             |
| X-54                           | SHOWER DOOR           | FRAMELESS GLASS, 1/4" THICK   | CLEAR OR FROSTED TEMPERED GLASS CHROME OR BRUSHED NICKEL HARDWARE                  | DREAMLINE OR KOHLER                |
| X-56                           | TOILET PAPER HOLDER   | CHROME                        | CHROME FINISH                                                                      | -                                  |
| X-58                           | TOWEL HOLDER          | CHROME                        | CHROME FINISH                                                                      |                                    |

| MATERIALS SCHEDULE |                       |                                |                                                                  |                                    |
|--------------------|-----------------------|--------------------------------|------------------------------------------------------------------|------------------------------------|
| MARK               | ITEM                  | SIZE/ SPEC                     | MATERIAL/ FINISH                                                 | MANUFACTURER/ NOTES                |
| F-40               | HARDWOOD FLOOR        | 7.5" WIDE PLANKS               | ENGINEERED HARDWOOD - NATURAL OAK OR SIMILAR WARM TONE           | PREFINISHED, FLOATING OR GLUE-DOWN |
| F-42               | FLOOR TILE (WET AREA) | 12X24 OR 24X48                 | PORCELAIN TILE MATTE FINISH RECTIFIED EDGES                      | DALTILE OR EQUIVALENT              |
| F-44               | WALL TILE             | 12X24 OR SUBWAY                | PORCELAIN ORCERAMIC WALL TILE, WATERPROOF INSTALLATION           | DALTILE OR EQUIVALENT              |
| F-46               | GARAGE FLOOR COATING  | FULL COVERAGE                  | EPOXY OR POLYASPATIC GRAY OR FLAKE BROADCAST                     | -                                  |
| F-48               | PORCH/ DECK FLOORING  | 5/4 X 6 COMPOSITE              | COMPOSITE DECKING LOW MAINTENANCE HIDDEN FASTENERS               | TREX, TIMBER OR EQUIVALENT         |
| F-50               | ROOFING               | ARCHITECTURAL SHINGLES         | ASPHALT COMPOSITION SHINGLES, 30-YEAR WARRANTY                   | GAF TIMBERLINE OR CERTAINTeed      |
| F-52               | EXTERIOR SIDING       | 6" LAP                         | FIBER CEMENT SIDING FACTORY PRIMED, PAINTED FINISH               | JAMES HARDIE HARDIE PLANK          |
| F-54               | STONE VENEER          | STANDARD MODULAR               | FACE STONE, MORTAR JOINTS                                        | LOCAL SUPPLIER                     |
| F-56               | RIDGE CAP             | MATCHING ROOF SLOPE            | ARCHITECTURAL RIDGE CAP SHINGLES OR METAL RIDGE VENT             | MATCHING ROOFING MANUFACTURER      |
| F-58               | GUTTERS AND DOWNSPOUT | 5" OR 6" K STYLE               | ALUMINUM OR GALVALUME SEAMLESS                                   | -                                  |
| F-60               | CROWN MOULDING        | 5 1/4 PROFILE                  | WOOD OR MDF, PAINTED                                             | -                                  |
| F-62               | BASE MOULDING         | 5 1/4" OR TALLER               | MATCHING FLOOR OR PAINTED WOOD                                   | -                                  |
| F-64               | BED MOULDING          | -                              | WOOD OR MDF, PAINTED TO MATCH COLUMN                             | -                                  |
| F-66               | BACK PORCH COLUMN     | 12X12 BASE TAPERING TO 9X9 TOP | LOWER: BRICK VENEER; UPPER: TAPERED TIMBER POST(PAINTED/ STAINED | PRESSURE TREATED OR CEDAR TIMBER   |



1 AXONOMETRIC VIEW

NOTES:

|     |             |    |      |
|-----|-------------|----|------|
| B   | Y REVISED   | JS |      |
| A   | X REVISED   | JS |      |
| REV | DESCRIPTION | BY | DATE |

AMENDMENTS

ARCHITECT'S CONTACT DETAILS

NAME: VICTOR O.

EMAIL: omehvictor@gmail.com

WEBSITE: https://victoromeh.github.io

PROJECT TITLE

3 BEDROOM SINGLE-STORY  
RESIDENCE WITH ATTIC

SITE

2841 BIRCHWOOD COURT,  
MURFREESBORO, TN 37129

CLIENT

THOMAS & RACHEL MERCER

|       |                    |                             |
|-------|--------------------|-----------------------------|
| SCALE | DATE:<br>JUNE 2026 | DRAWN BY:<br>VICTOR<br>OMEH |
|-------|--------------------|-----------------------------|

SHEET NAME: AXONOMETRIC  
VIEW

SHEET NO.

PROJECT NO. VO-2026-104

A7.0



3D View 2



3D View 3

NOTES:

| B   | Y REVISED   | JS |      |
|-----|-------------|----|------|
| A   | X REVISED   | JS |      |
| REV | DESCRIPTION | BY | DATE |

AMENDMENTS

ARCHITECT'S CONTACT DETAILS

NAME: VICTOR O.

EMAIL: omehvictor@gmail.com

WEBSITE: https://victoromeh.github.io

PROJECT TITLE

3 BEDROOM SINGLE-STORY  
RESIDENCE WITH ATTIC

SITE

2841 BIRCHWOOD COURT,  
MURFREESBORO, TN 37129

CLIENT

THOMAS & RACHEL MERCER


|       |                    |                             |
|-------|--------------------|-----------------------------|
| SCALE | DATE:<br>JUNE 2026 | DRAWN BY:<br>VICTOR<br>OMEH |
|-------|--------------------|-----------------------------|

SHEET NAME. EXTERIOR  
PERSPECTIVE

PROJECT NO. VO-2026-104

SHEET NO.

A7.1

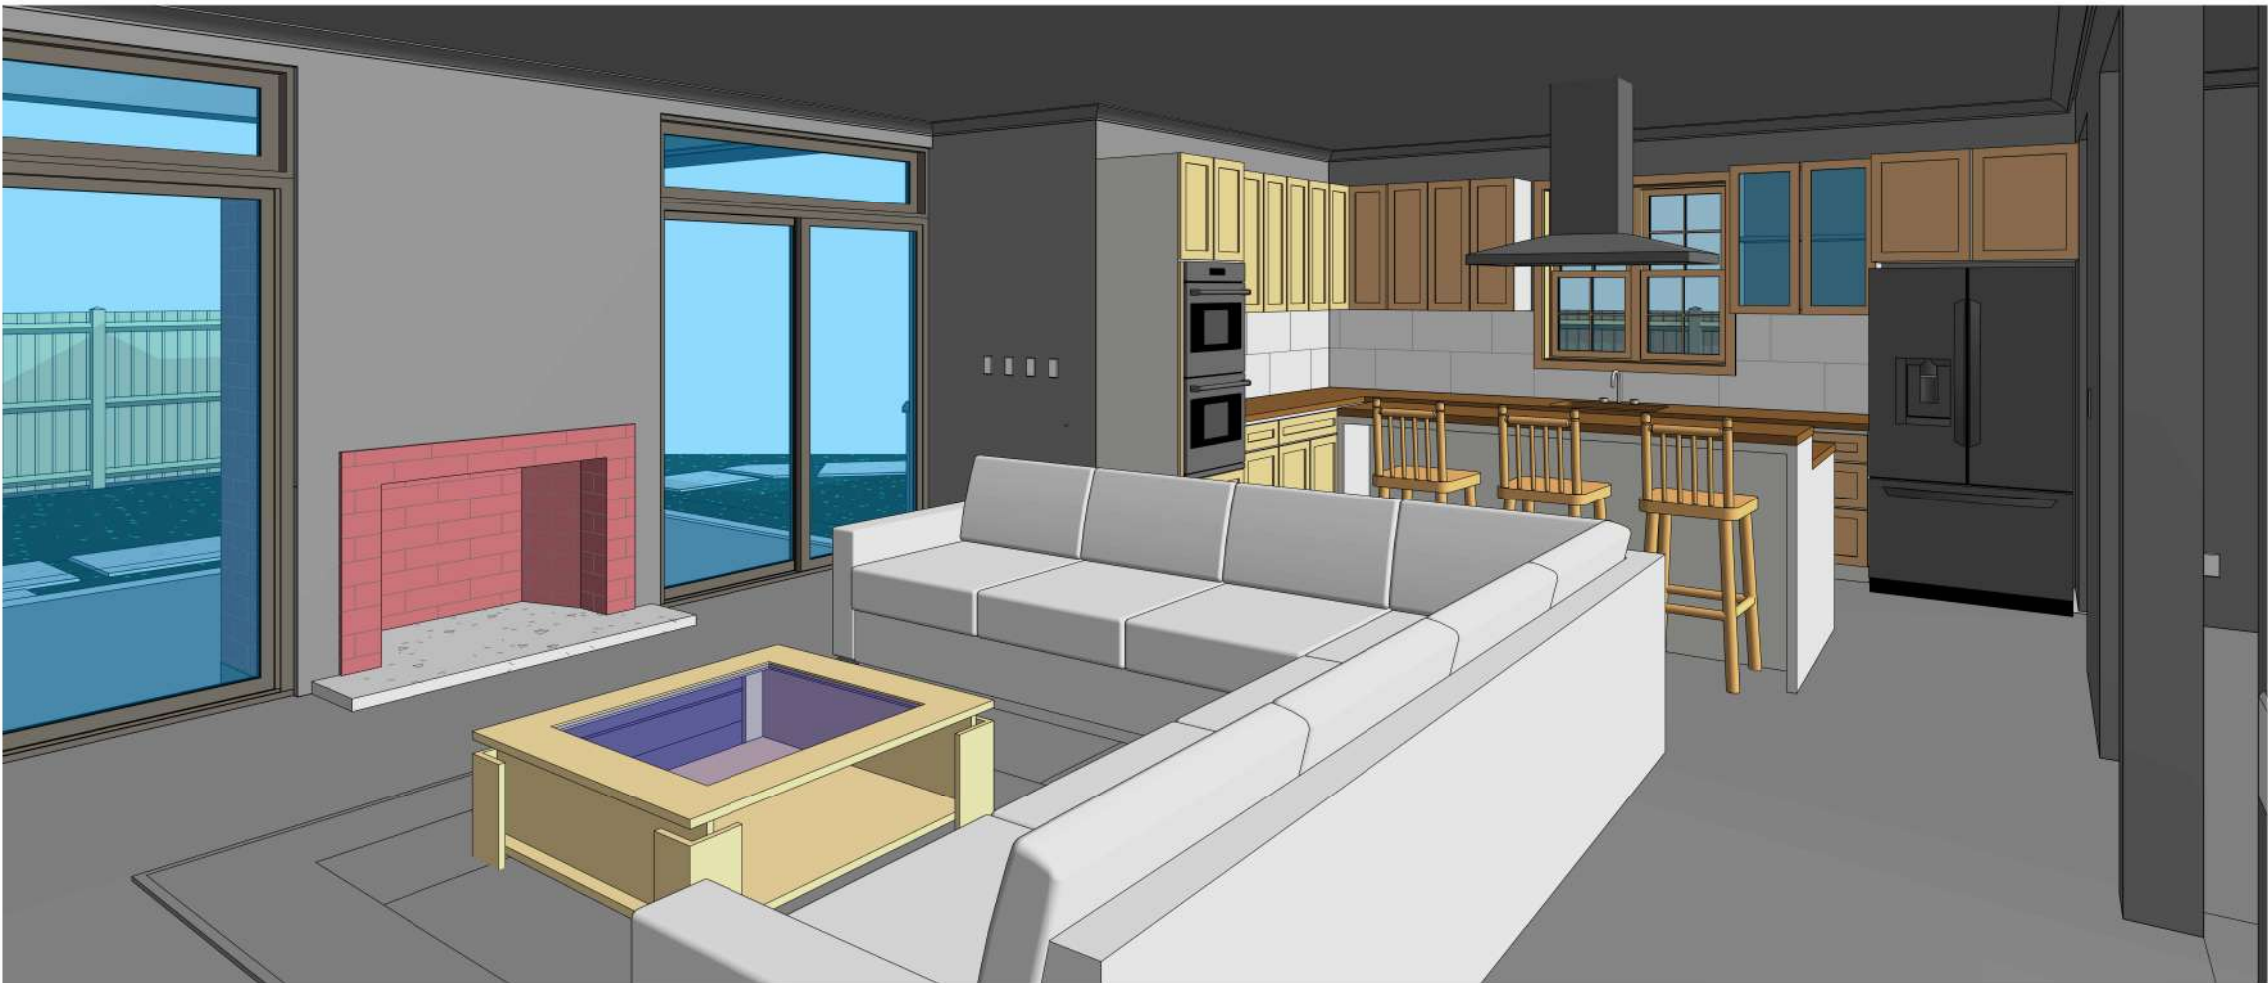

1 3D View 1



2 INTERIOR PERSPECTIVE

NOTES:

|     |             |    |      |
|-----|-------------|----|------|
| B   | Y REVISED   | JS |      |
| A   | X REVISED   | JS |      |
| REV | DESCRIPTION | BY | DATE |

AMENDMENTS

ARCHITECT'S CONTACT DETAILS

NAME: VICTOR O.

EMAIL: omehvictor@gmail.com

WEBSITE: https://victoromeh.github.io

PROJECT TITLE

3 BEDROOM SINGLE-STORY  
RESIDENCE WITH ATTIC

SITE

2841 BIRCHWOOD COURT,  
MURFREESBORO, TN 37129

CLIENT

THOMAS & RACHEL MERCER

|       |                    |                             |
|-------|--------------------|-----------------------------|
| SCALE | DATE:<br>JUNE 2026 | DRAWN BY:<br>VICTOR<br>OMEH |
|-------|--------------------|-----------------------------|

SHEET NAME. INTERIOR  
PERSPECTIVE

PROJECT NO. VO-2026-104

SHEET NO.

A7.2



1 3D KITCHEN



2 3D BATHROOM

NOTES:

|     |             |    |      |
|-----|-------------|----|------|
| B   | Y REVISED   | JS |      |
| A   | X REVISED   | JS |      |
| REV | DESCRIPTION | BY | DATE |

AMENDMENTS

ARCHITECT'S CONTACT DETAILS

NAME: VICTOR O.

EMAIL: omehvictor@gmail.com

WEBSITE: https://victoromeh.github.io

PROJECT TITLE

3 BEDROOM SINGLE-STORY  
RESIDENCE WITH ATTIC

SITE


2841 BIRCHWOOD COURT,  
MURFREESBORO, TN 37129

CLIENT


THOMAS & RACHEL MERCER

|       |                    |                             |
|-------|--------------------|-----------------------------|
| SCALE | DATE.<br>JUNE 2026 | DRAWN BY.<br>VICTOR<br>OMEH |
|-------|--------------------|-----------------------------|

|                                 |                   |
|---------------------------------|-------------------|
| SHEET NAME. 3D VIEW<br>INTERIOR | SHEET NO.<br>A7.3 |
| PROJECT NO. VO-2026-104         |                   |

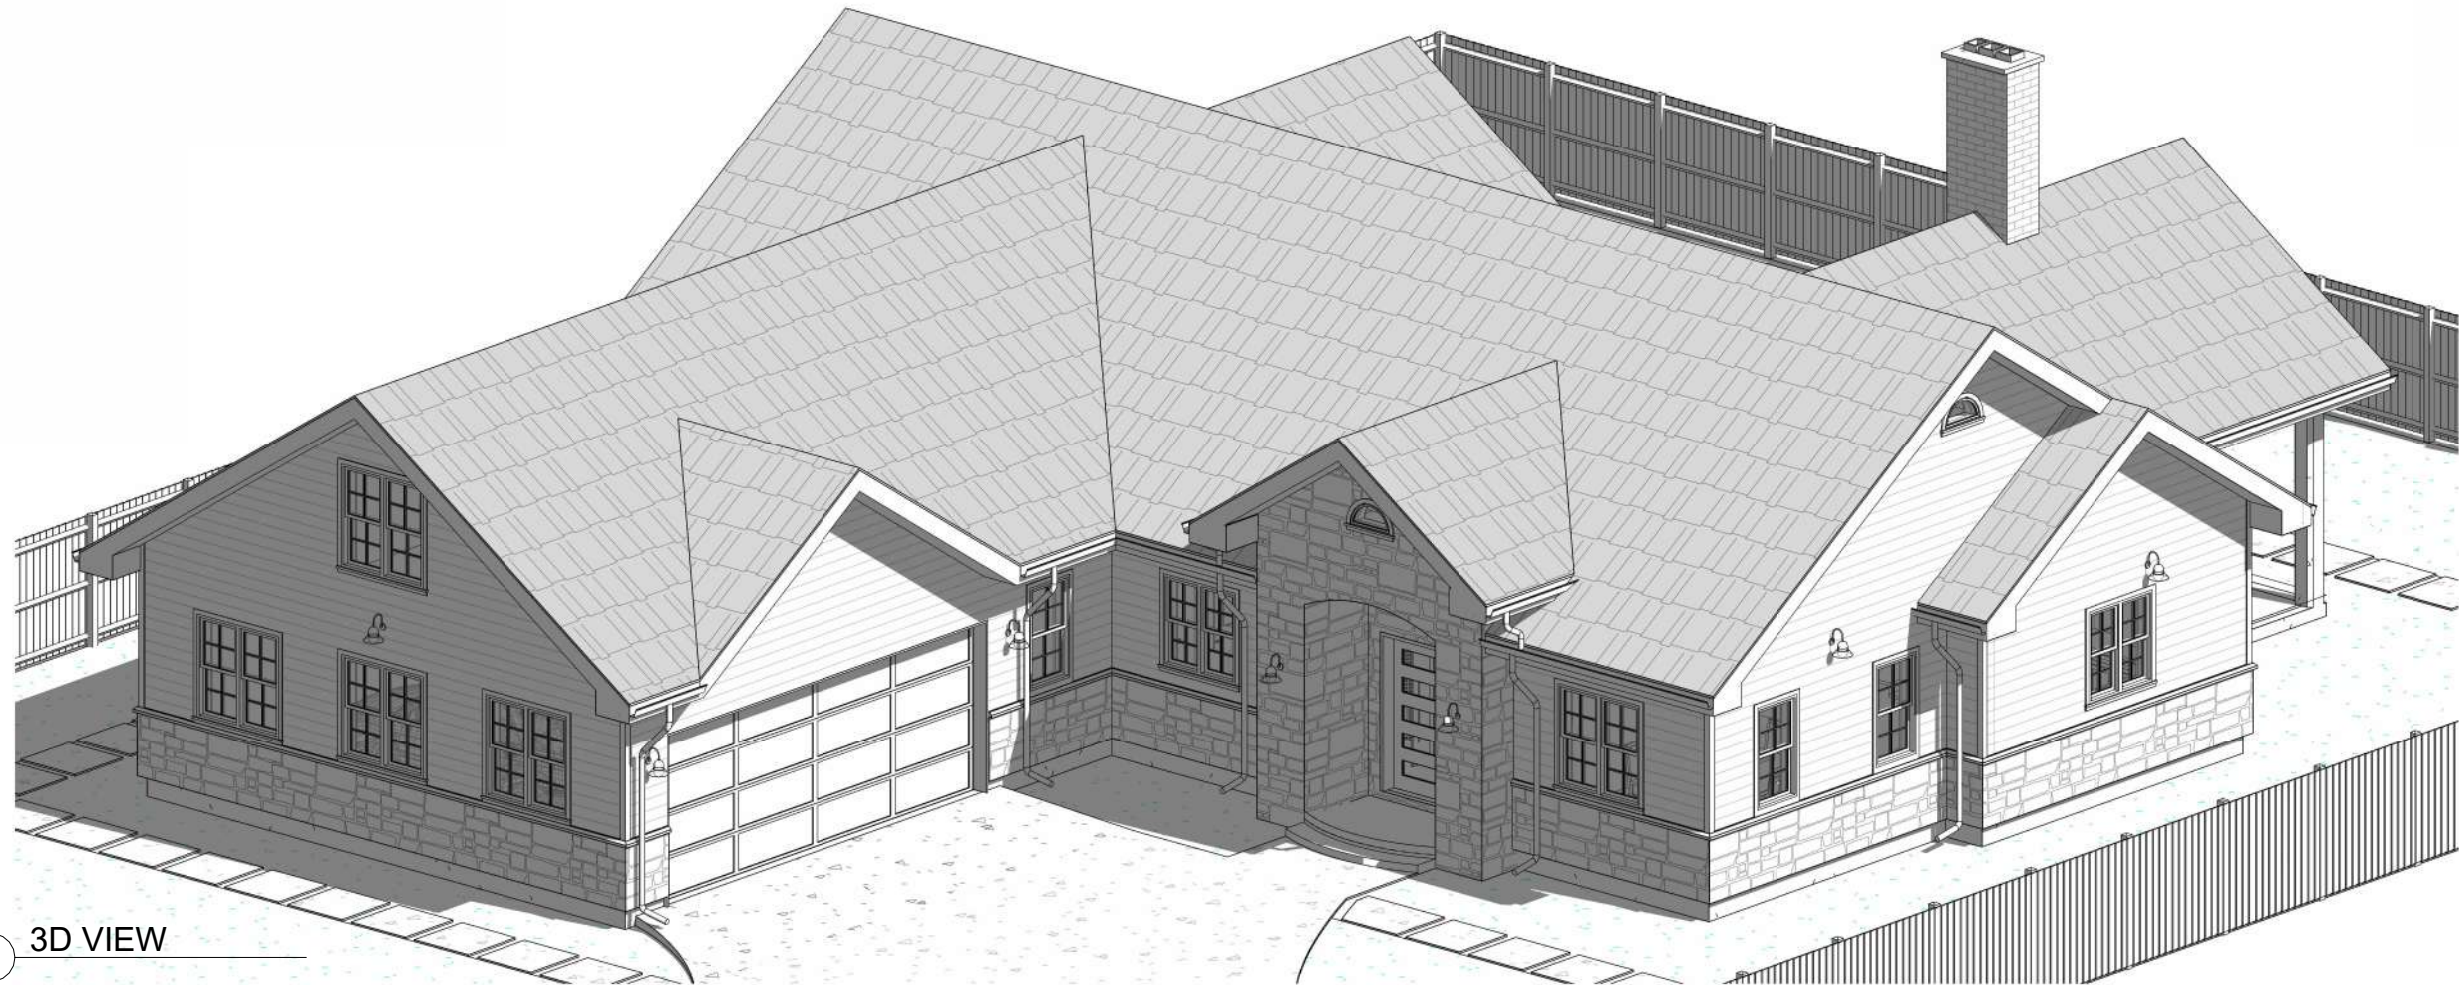

1 3D VIEW

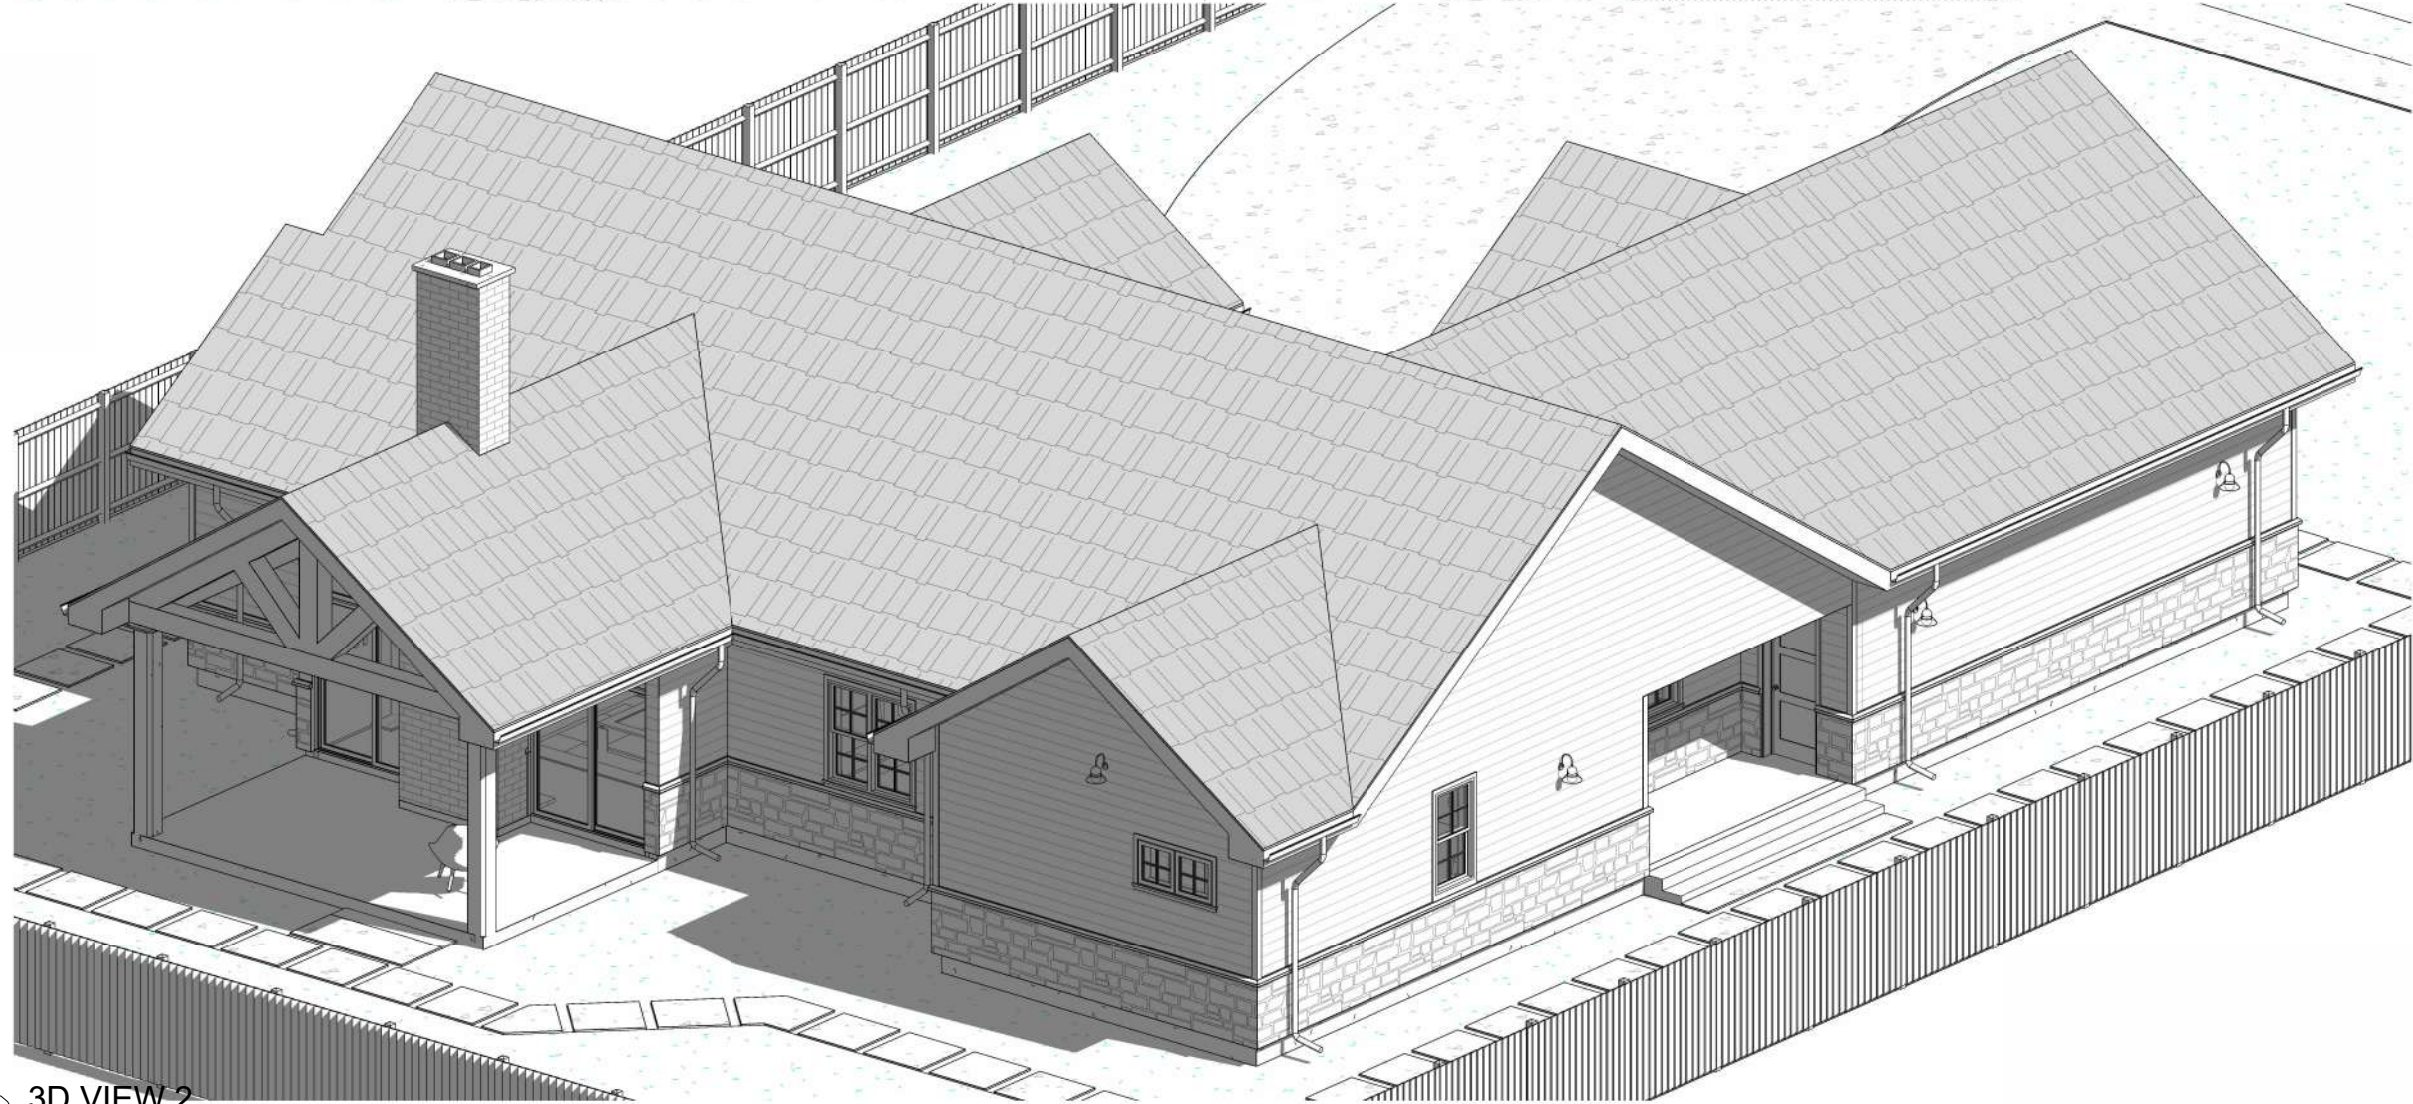

2 3D VIEW 2

NOTES:

| B   | Y REVISED   | JS |      |
|-----|-------------|----|------|
| A   | X REVISED   | JS |      |
| REV | DESCRIPTION | BY | DATE |

AMENDMENTS

| ARCHITECT'S CONTACT DETAILS |                              |  |  |
|-----------------------------|------------------------------|--|--|
| NAME:                       | VICTOR O.                    |  |  |
| EMAIL:                      | omehvictor@gmail.com         |  |  |
| WEBSITE:                    | https://victoromeh.github.io |  |  |

| PROJECT TITLE                               |
|---------------------------------------------|
| 3 BEDROOM SINGLE-STORY RESIDENCE WITH ATTIC |

| SITE                                         |
|----------------------------------------------|
| 2841 BIRCHWOOD COURT, MURFREESBORO, TN 37129 |

| CLIENT                 |
|------------------------|
| THOMAS & RACHEL MERCER |

|       |                    |                          |
|-------|--------------------|--------------------------|
| SCALE | DATE:<br>JUNE 2026 | DRAWN BY:<br>VICTOR OMEH |
|-------|--------------------|--------------------------|

|                         |           |
|-------------------------|-----------|
| SHEET NAME: 3D VIEW     | SHEET NO. |
| PROJECT NO: VO-2026-104 | A7.4      |