

PROJECT TEAM

DESIGNED BY: VICTOR OMEH
EMAIL: omehvictor@gmail.com
WEBSITE: www.victoromeh.github.io

CLIENT / OWNER

OWNER: MICHAEL & SARAH WHITFIELD
LOCATION: 509 BROOKHAVEN LANE,
WESTFIELD, IN 46074

APPLICABLE CODES

INTERNATIONAL RESIDENTIAL CODE (IRC),
2021 EDITION
INTERNATIONAL FIRE CODE (IFC),
2021 EDITION
INTERNATIONAL PLUMBING CODE (IPC),
2021 EDITION
INTERNATIONAL MECHANICAL CODE (IMC),
2021 EDITION
INTERNATIONAL FUEL GAS CODE (IFGC),
2021 EDITION
NATIONAL ELECTRICAL CODE (NEC),
2023 EDITION
INTERNATIONAL ENERGY CONSERVATION
CODE (IECC), 2021 EDITION.

VICINITY MAP



PROJECT DATA

PROJECT DESCRIPTION

SINGLE FAMILY HOME

📍 4127 BROOKHAVEN LANE, WESTFIELD, IN 46074

ZONING: SF5-- HIGH DENSITY SINGLE FAMILY
RESIDENTIAL
JURISDICTION: CITY OF WESTFIELD, INDIANA
BUILDING USE: SINGLE FAMILY RESIDENCE
DENSITY: 1 DWELLING UNIT/ 6930SQFT
FRONT SETBACK: 35FT
SIDE SETBACK: 12FT
REAR SETBACK: 21FT
MAX BLDG HEIGHT: 31FT
SITE SQ FOOTAGE: 6930SQFT

PERSPECTIVE



SHEET INDEX

- A0.0 COVER PAGE
A0.1 GENERAL NOTES
- A1.0 SITE PLAN
A1.1 BASEMENT/ FOUNDATION PLAN
A1.2 1ST FLOOR PLAN
A1.3 2ND FLOOR PLAN
A1.4 ROOF PLAN
A1.5 1ST RCP/ELECTRICAL
A1.6 2ND RCP/ELECTRICAL
- A2.0 SOUTH ELEVATION
A2.1 NORTH ELEVATION
A2.2 EAST ELEVATION
A2.3 WEST ELEVATION
- A3.0 LONGITUDINAL SECTION
A3.1 TRANSVERSE SECTION 1
A3.2 TRANSVERSE SECTION 2
- A4.0 KITCHEN/ BATHROOM C.P
A4.1 KITCHEN ELEVATION
A4.2 BATHROOM ELEVATION
- A5.0 TYPICAL DETAILS
A5.1 DETAILS
A5.2 WALL DETAILS
- A6.0 DOORS & WINDOWS
A6.1 SCHEDULES 1
A6.2 SCHEDULES 2
- A7.0 AXONOMETRIC VIEW (BASEMENT)
A7.1 AXONOMETRIC VIEW (1ST FLOOR)
A7.2 AXONOMETRIC VIEW (2ND FLOOR)
A7.3 FRONT PERSPECTIVE
A7.4 REAR PERSPECTIVE
A7.5 3D VIEW (KITCHEN)
A7.6 3D VIEW (BATHROOM)

SYMBOLS LEGEND

- SECTION MARKER
ELEVATION MARKER
INT ELEVATIONS
DETAIL CALLOUT
COMPASS (TRUE)
DATUM MARKER
WINDOW CALLOUT
DOOR CALLOUT
FIXTURE CALLOUT
- SOIL
CONCRETE
BRICK
CMU BLOCK
RIGID INSULATION
BATT INSULATION
FINISH CALLOUT
CONTOURS (FEET)

NOTES:

B	Y REVISED	JS	
A	X REVISED	JS	
REV	DESCRIPTION	BY	DATE

AMENDMENTS

ARCHITECT'S CONTACT DETAILS

NAME: VICTOR OMEH
EMAIL: omehvictor@gmail.com
WEBSITE: www.victoromeh.github.io

PROJECT TITLE

SINGLE FAMILY HOME

SITE

509 BROOKHAVEN LANE,
WESTFIELD, IN 46074

CLIENT


MICHAEL & SARAH WHITFIELD

SCALE	DATE	DRAWN BY
	JAN 2026	VICTOR OMEH

SHEET NAME	COVER PAGE	SHEET NO.
PROJECT NO.	VO-2026-101	A0.0

GENERAL NOTES			
1. WORK SHALL CONFORM TO ALL APPLICABLE CODES AND ORDINANCES, INCLUDING BUT NOT LIMITED TO: BUILDING, PLUMBING, ELECTRICAL, AND MECHANICAL CODES.	15. DEPICTED FOUNDATION SHOWS ONLY A PROPOSED DESIGN BASED ON FICTIONAL CONDITIONS. CONDUCT A SOIL TEST AND STRUCTURAL ENGINEERING FOR A SITE-SPECIFIC FOUNDATION.	31. ALL CONSTRUCTION SHALL BE TRUE, PLUMB, LEVEL, SQUARE, AND IN PROPER ALIGNMENT.	
2. ANY ERRORS, OMISSIONS, OR CONFLICTS FOUND WITHIN THESE DRAWINGS SHALL BE BROUGHT TO THE ATTENTION OF THE OWNER OR THEIR REPRESENTATIVE BEFORE PROCEEDING WITH THE WORK.	16. FOOTINGS SHALL EXTEND DOWN BEYOND THE LOCAL FROST LINE.	32. THE GENERAL CONTRACTOR SHALL MAINTAIN A CURRENT AND COMPLETE SET OF DRAWINGS ON THE JOB SITE DURING ALL PHASES OF CONSTRUCTION. ALL SUBCONTRACTORS SHALL BE PROVIDED WITH A SET OF DRAWINGS.	
3. DO NOT SCALE THESE DRAWINGS. WRITTEN DIMENSIONS TAKE PRECEDENCE OVER MEASUREMENTS.	17. PERFORATED DRAIN PIPES SHALL BE LOCATED WITHIN A GRAVEL PERIMETER AROUND THE FOUNDATION, WITH MULTIPLE DRAINAGE OUTLETS LEADING DOWNSLOPE AWAY FROM THE BUILDING.	33. THE GENERAL CONTRACTOR SHALL VERIFY AND ASSUME RESPONSIBILITY FOR ALL DIMENSIONS AND SITE CONDITIONS, AS WELL AS INSPECT THE PREMISES AND TAKE NOTE OF EXISTING CONDITIONS PRIOR TO SUBMITTING PRICES. NO CLAIM SHALL BE ALLOWED FOR PROBLEMS WHICH COULD HAVE BEEN PREVENTED BY A THOROUGH EXAMINATION.	
4. DIMENSIONS ARE TAKEN FROM FACE OF FRAMING LUMBER, FACE OF CONCRETE/ MASONRY, CENTER OF COLUMN, AND CENTERLINE OF FIXTURE, UNLESS NOTED OTHERWISE.	18. FIRE BLOCKING AND FIRE-RATED SHEATHING SHALL BE PROVIDED AS REQUIRED AT CEILINGS, FLOORS, AND ENCLOSED USABLE SPACE UNDER STAIRS.	34. PROVIDE TEMPORARY SUPPORT AS NECESSARY TO ENSURE THE STRUCTURAL INTEGRITY OF THE BUILDING UNDER CONSTRUCTION. THE GENERAL CONTRACTOR IS RESPONSIBLE FOR ALL CONSTRUCTION-RELATED ACTIVITIES.	
5. ALL DIMENSIONS NOTED "VERIFY IN FIELD (V.I.F.)" SHALL BE MEASURED BY THE CONTRACTOR PRIOR TO CONSTRUCTION. REPORT ANY DISCREPANCIES TO THE OWNER OR THEIR REPRESENTATIVE.	19. ALL WOOD WITHIN 8 INCHES OF THE GROUND SHALL BE PRESSURE TREATED OR COMPRISE A SUITABLY ROT RESISTANT MATERIAL. METAL CONNECTIONS WHICH TOUCH THIS WOOD SHOULD BE GALVANIZED OR STAINLESS STEEL.	35. INSTALL FIXTURES, MATERIALS, AND EQUIPMENT ACCORDING TO MANUFACTURER'S SPECIFICATIONS. SHOULD THOSE SPECS CONFLICT WITH THE DRAWINGS, IMMEDIATELY NOTIFY THE OWNER OR THE OWNER'S REPRESENTATIVE.	
6. DETAILS SHOWN ARE TYPICAL. SIMILAR DETAILS APPLY IN SIMILAR SITUATIONS.	20. PROVIDE ADEQUATE BLOCKING AROUND CABINETRY, PLUMBING FIXTURES, AND OTHER APPLICABLE AREAS.	36. VERIFY CLEARANCES FOR FIXTURES, VENTS, CHASES, ETC. BEFORE ORDERING OR INSTALLING RELATED WORK ITEMS.	
7. IN THE CASE OF DISCREPANCIES WITHIN DESCRIPTIONS OF SIMILAR ITEMS, PRECEDENCE SHALL BE GIVEN TO NOTES & DRAWINGS OF GREATER DETAIL.	21. PROVIDE MINIMUM R-13 INSULATION IN ALL EXTERIOR WALLS AND R-21 INSULATION AT ROOFS OF CONDITIONED SPACES.	37. COORDINATE ALL WORK WITH EXISTING CONDITIONS, INCLUDING BUT NOT LIMITED TO: IRRIGATION PIPES, ELECTRICAL CONDUITS, WATER LINES, GAS LINES, AND DRAINAGE LINES.	
8. ALL REQUIRED EXITS SHALL BE OPERABLE FROM THE INSIDE, WITHOUT THE USE OF A KEY OR ANY SPECIAL KNOWLEDGE.	22. DEPICTED WEATHERPROOFING METHODS (SUCH AS SEALANT, CAULKING, AND FLASHING) ARE NOT COMPREHENSIVE. FOLLOW REQUIREMENTS AND RECOMMENDATIONS OF BUILDING CODES, PRODUCT MANUFACTURERS, AND CONSTRUCTION BEST PRACTICES.	38. THE GENERAL CONTRACTOR SHALL BE RESPONSIBLE FOR REGULARLY REMOVING THE WASTE MATERIALS OF ALL SUBCONTRACTORS, AND MAINTAIN STRICT CONTROL OVER JOB CLEANING TO PREVENT DUST AND RUBBISH FROM INTERFERING WITH OPERATIONS.	
9. ANY ELECTRICAL, PLUMBING AND/OR HVAC SYSTEMS INCLUDED IN THE WORK SHALL BE INSTALLED ON A DESIGN-BUILD BASIS, AND SHALL NOT SIGNIFICANTLY ALTER THE STRUCTURE OR FINISHES.	23. CONTRACTOR TO ENSURE THAT INTERIOR SHEATHING IS FLUSH, CLEAN AND FREE OF DUST AND DEFECTS BEFORE APPLICATION OF PAINT COATINGS.	39. CONSTRUCTION EQUIPMENT NOISE SHALL BE MINIMIZED DURING THE CONSTRUCTION PHASES BY MUFFLING AND SHIELDING IMPACT TOOLS WHENEVER POSSIBLE.	
10. SMOKE DETECTORS AND CARBON MONOXIDE DETECTORS SHALL BE INSTALLED PER APPLICABLE CODES.	24. FLOOR MATERIAL TRANSITIONS OCCUR AT THE CENTERLINE OF DOORS OR FRAMED OPENINGS.		
11. GRADING AND SITEWORK SHALL BE MINIMAL IN ALL AREAS NOT DIRECTLY AFFECTED BY THE NEW CONSTRUCTION. FOLLOW BEST PRACTICES AND LOCAL REQUIREMENTS IN ORDER TO MINIMIZE ENVIRONMENTAL DAMAGE.	25. PROVIDE ONE COAT PRIMER AND TWO FINISH COATS OF PAINT AT INTERIOR AND EXTERIOR SURFACES.		
12. FINISH GRADE MUST SLOPE AWAY FROM EXTERIOR FOUNDATION WALL, AT A HEIGHT OF 6 INCHES OVER A 10 FOOT DISTANCE.	26. ALL GLASS SHALL CONFORM WITH HUMAN IMPACT AND SAFETY REQUIREMENTS.		
13. ANY SURVEY MARKERS WITHIN THE AREA OF CONSTRUCTION SHALL BE PRESERVED OR RESET BY A REGISTERED CIVIL ENGINEER OR LICENSED LAND SURVEYOR.	27. THE MINIMUM STAIRCASE TREAD SHALL BE 10" AND THE MINIMUM RISER 7.75", WITH A MAXIMUM 3⁄8" VARIATION WITHIN A FLIGHT.		
14. BEFORE GRADING OPERATIONS, A TEMPORARY PROTECTION FENCE SHALL BE CONSTRUCTED AROUND ANY TREE WITHIN 30 FEET OF THE FOUNDATION, AND A SILT FENCE MUST BE CONSTRUCTED DOWNSLOPE OF ANY AREA WHERE THE SOIL IS DISTURBED.	28. HANDRAILS SHALL BE LOCATED 34-38 INCHES ABOVE STAIR TREADS, AS MEASURED FROM THE NOSINGS.		
	29. GUARDRAILS SHALL BE LOCATED ALONG ANY FLOOR EDGES THAT DROP 30 INCHES OR MORE TO THE FLOOR OR GROUND BELOW.		
	30. DO NOT USE SCREW-ON, NON-OPERABLE WINDOW SHUTTERS. THEY ARE AS TACKY AS CLIP-ON TIES. DO NOT USE VINYL OR ALUMINUM SIDING. THAT WOULD MAKE THIS HOUSE LOOK LIKE A CHEAP PLASTIC TOY. IT IS ABSOLUTELY FORBIDDEN.		

NOTES:			
B	Y REVISED	JS	
A	X REVISED	JS	
REV	DESCRIPTION	BY	DATE
AMENDMENTS			
ARCHITECT'S CONTACT DETAILS			
NAME:	VICTOR OMEH		
EMAIL:	omehvictor@gmail.com		
WEBSITE:	www.victoromeh.github.io		
PROJECT TITLE			
SINGLE FAMILY HOME			
SITE			
509 BROOKHAVEN LANE, WESTFIELD, IN 46074			
CLIENT			
MICHAEL & SARAH WHITFIELD			
SCALE	DATE. JAN 2026	DRAWN BY. VICTOR OMEH	
SHEET NAME GENERAL NOTES		SHEET NO.	
PROJECT NO.	VO-2026-101		
		A0.1	

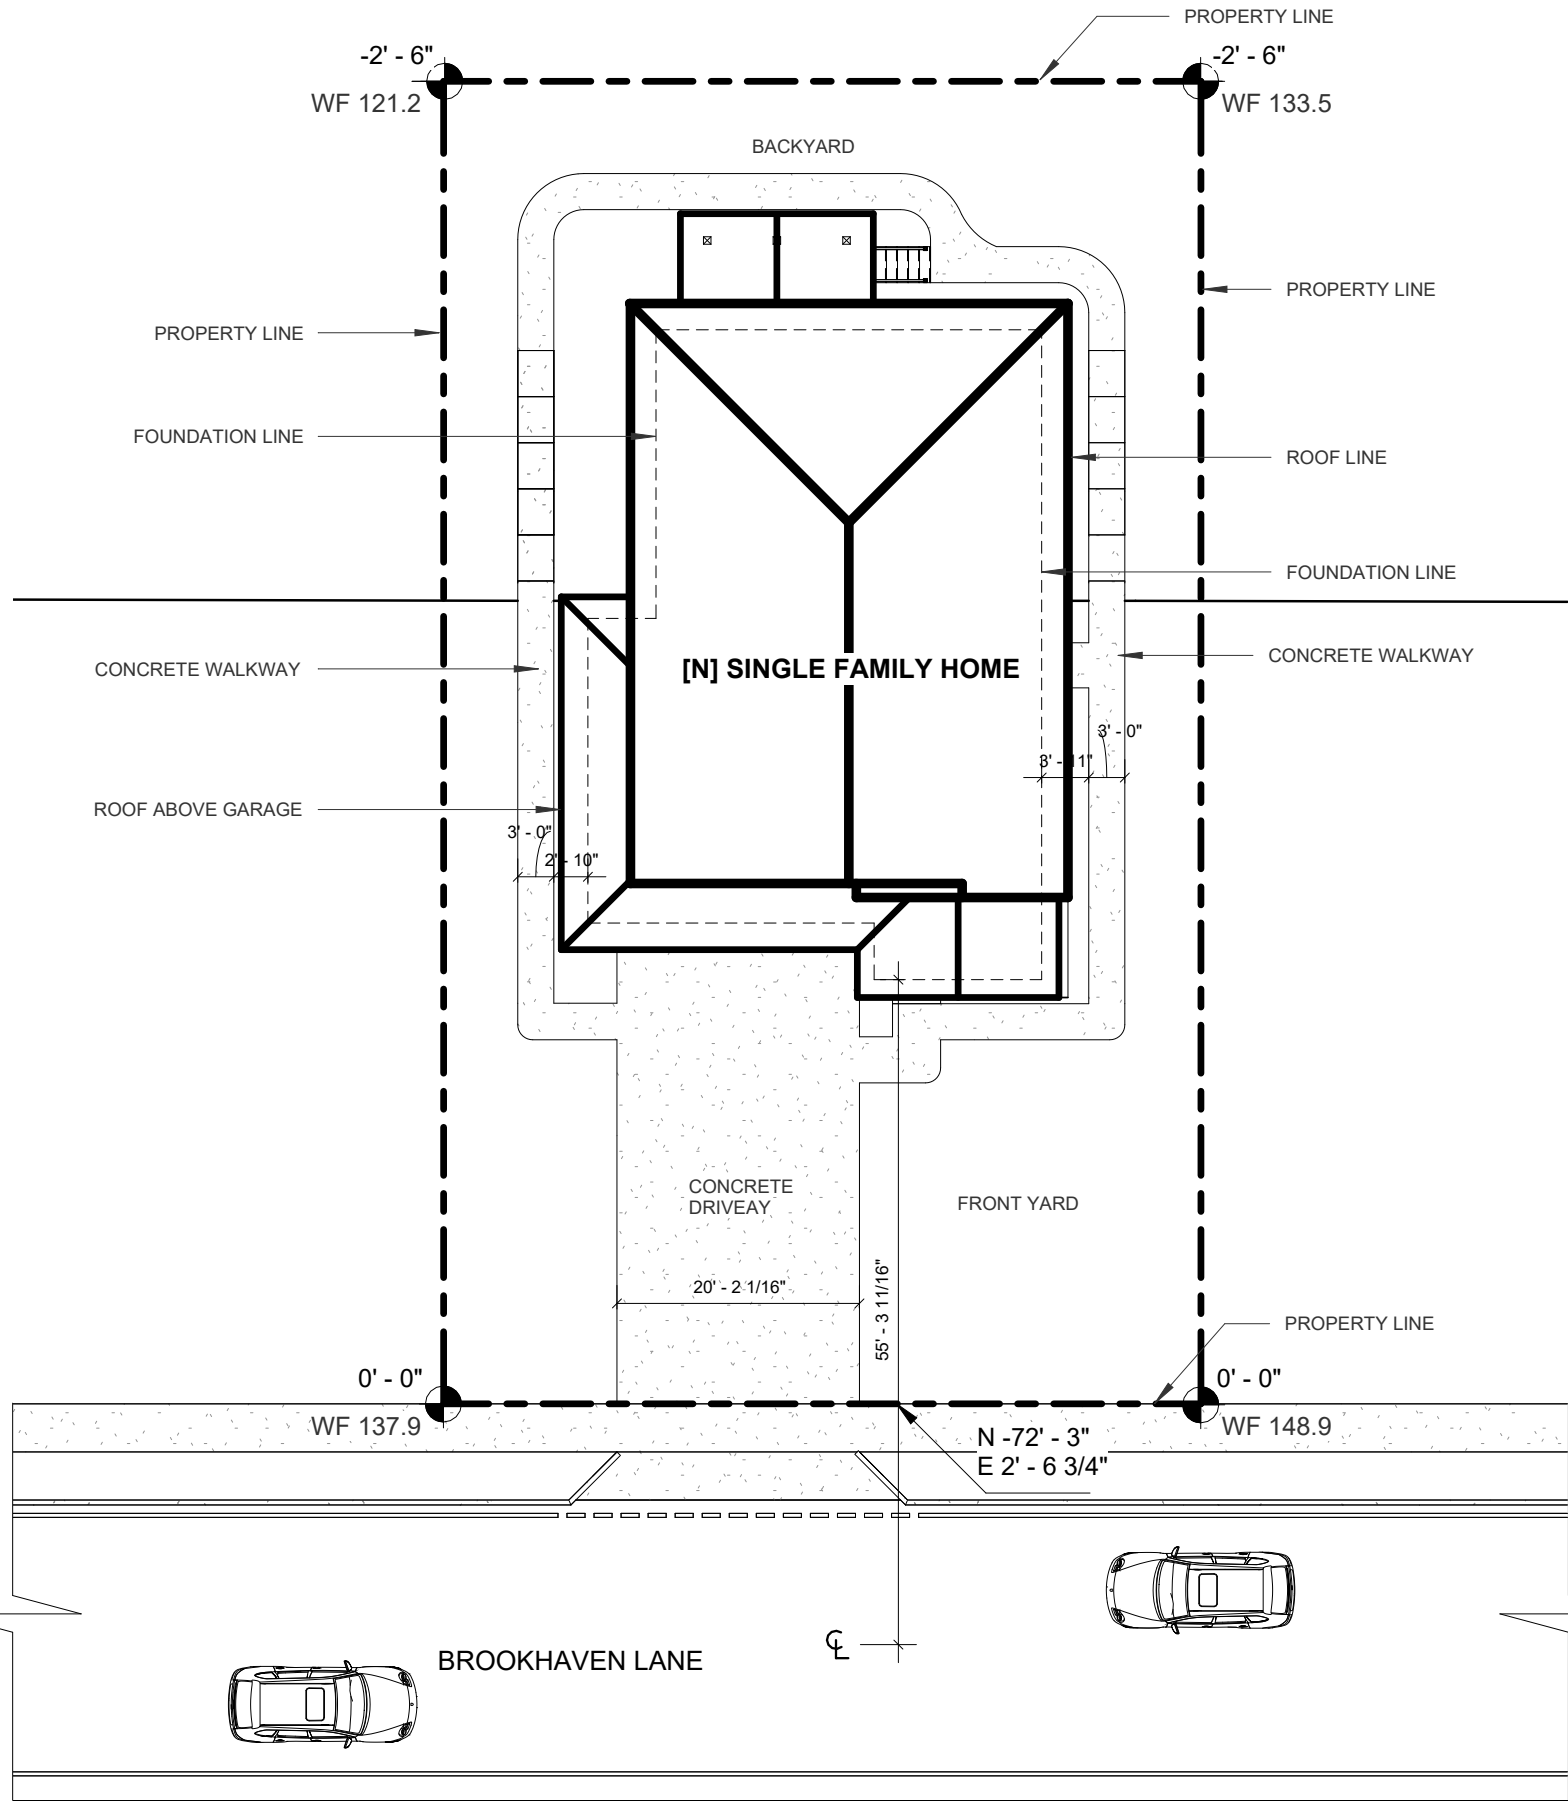

SITE DATA	
ITEM	VALUE
ZONING	SF5 HIGH DENSITY
JURISDICTION	CITY OF WESTFIELD, INDIANA
BUILDING USE	SINGLE FAMILY RESIDENCE
DENSITY	1 DWELLING UNIT
OCCUPANCY TYPE	SF5
CONSTRUCTION TYPE	TYPE V-B,WOOD FRAME
FRONT SETBACK	35 FT
REAR SETBACK	20 FT
SIDE SETBACK (LEFT)	12 FT
SIDE SETBACK (RIGHT)	13 FT
MAX BUILDING HEIGHT	31 FT
BASEMENT SQUARE FOOTAGE	1065 SQ FT
FIRST FLOOR SQUARE FOOTAGE	1892 SQ FT
FIRST FLOOR SQUARE FOOTAGE (CONDITIONED)	1669 SQ FT
SECOND FLOOR SQUARE FOOTAGE (CONDITIONED)	1423 SQ FT
TOTAL FLOOR SQUARE FOOTAGE (CONDITIONED)	4157 SQ FT
IMPERVIOUS SURFACE COVERAGE	3245 SQ FT
SITE SQUARE FOOTAGE	6930 SQ FT
LOT COVERAGE	48%
PARKING	2 SPACES

NOTES:

B	Y REVISED	JS	
A	X REVISED	JS	
REV	DESCRIPTION	BY	DATE

AMENDMENTS

ARCHITECT'S CONTACT DETAILS

NAME: VICTOR OMEH.
EMAIL: omehvictor@gmail.com
WEBSITE: www.victoromeh.github.io

PROJECT TITLE

SINGLE FAMILY HOME

SITE


509 BROOKHAVEN LANE,
WESTFIELD, IN 46074

CLIENT

MICHAEL & SARAH WHITFIELD

SCALE	DATE	DRAWN BY.
1/16" = 1'-0"	JAN 2026	VICTOR OMEH

SHEET NAME. SITE PLAN	SHEET NO. A1.0
PROJECT NO. VO-2026-101	

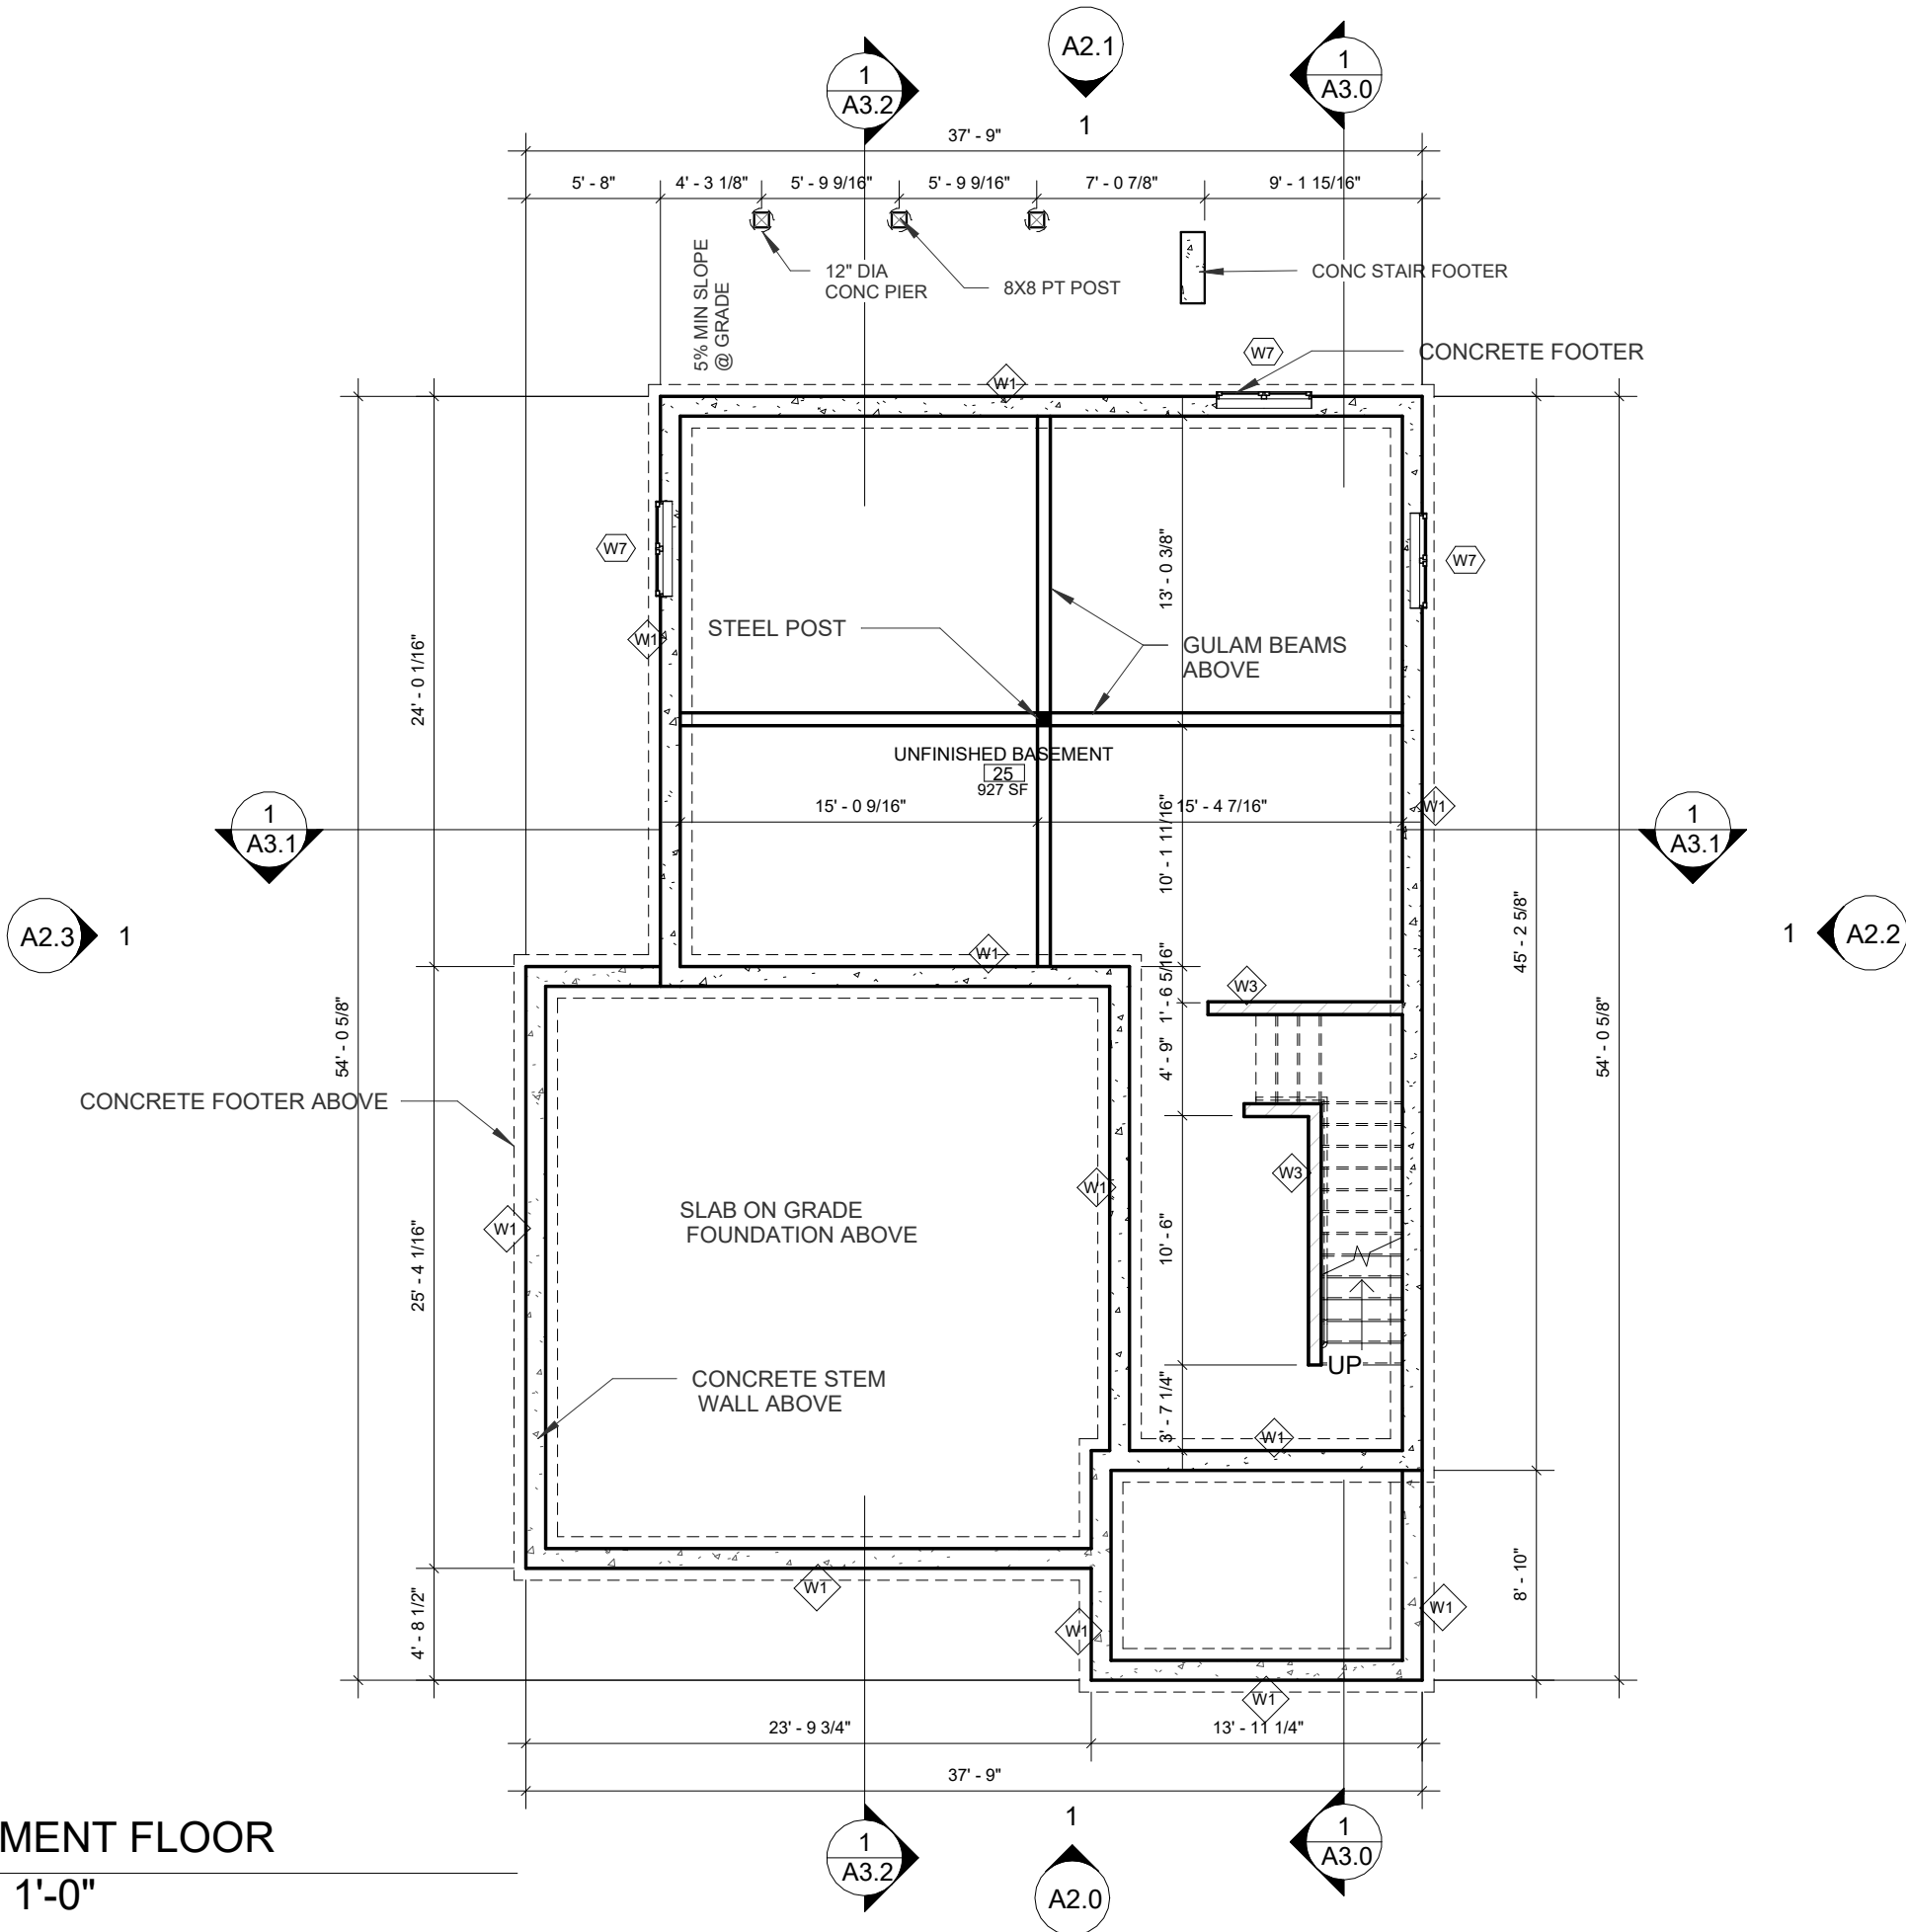

NOTES:

B	Y REVISED	JS	
A	X REVISED	JS	
REV	DESCRIPTION	BY	DATE

AMENDMENTS

ARCHITECT'S CONTACT DETAILS

NAME: VICTOR OMEH.

EMAIL: omehvictor@gmail.com

WEBSITE: www.victoromeh.github.io

PROJECT TITLE

SINGLE FAMILY HOME

SITE

509 BROOKHAVEN LANE,
WESTFIELD, IN 46074

CLIENT

MICHAEL & SARAH WHITFIELD


SCALE	DATE.	DRAWN BY.
1/8" = 1'-0"	JAN 2026	VICTOR OMEH

SHEET NAME. FOUNDATION/
BASEMENT PLAN

PROJECT NO. VO-2026-101

SHEET NO.

A1.1

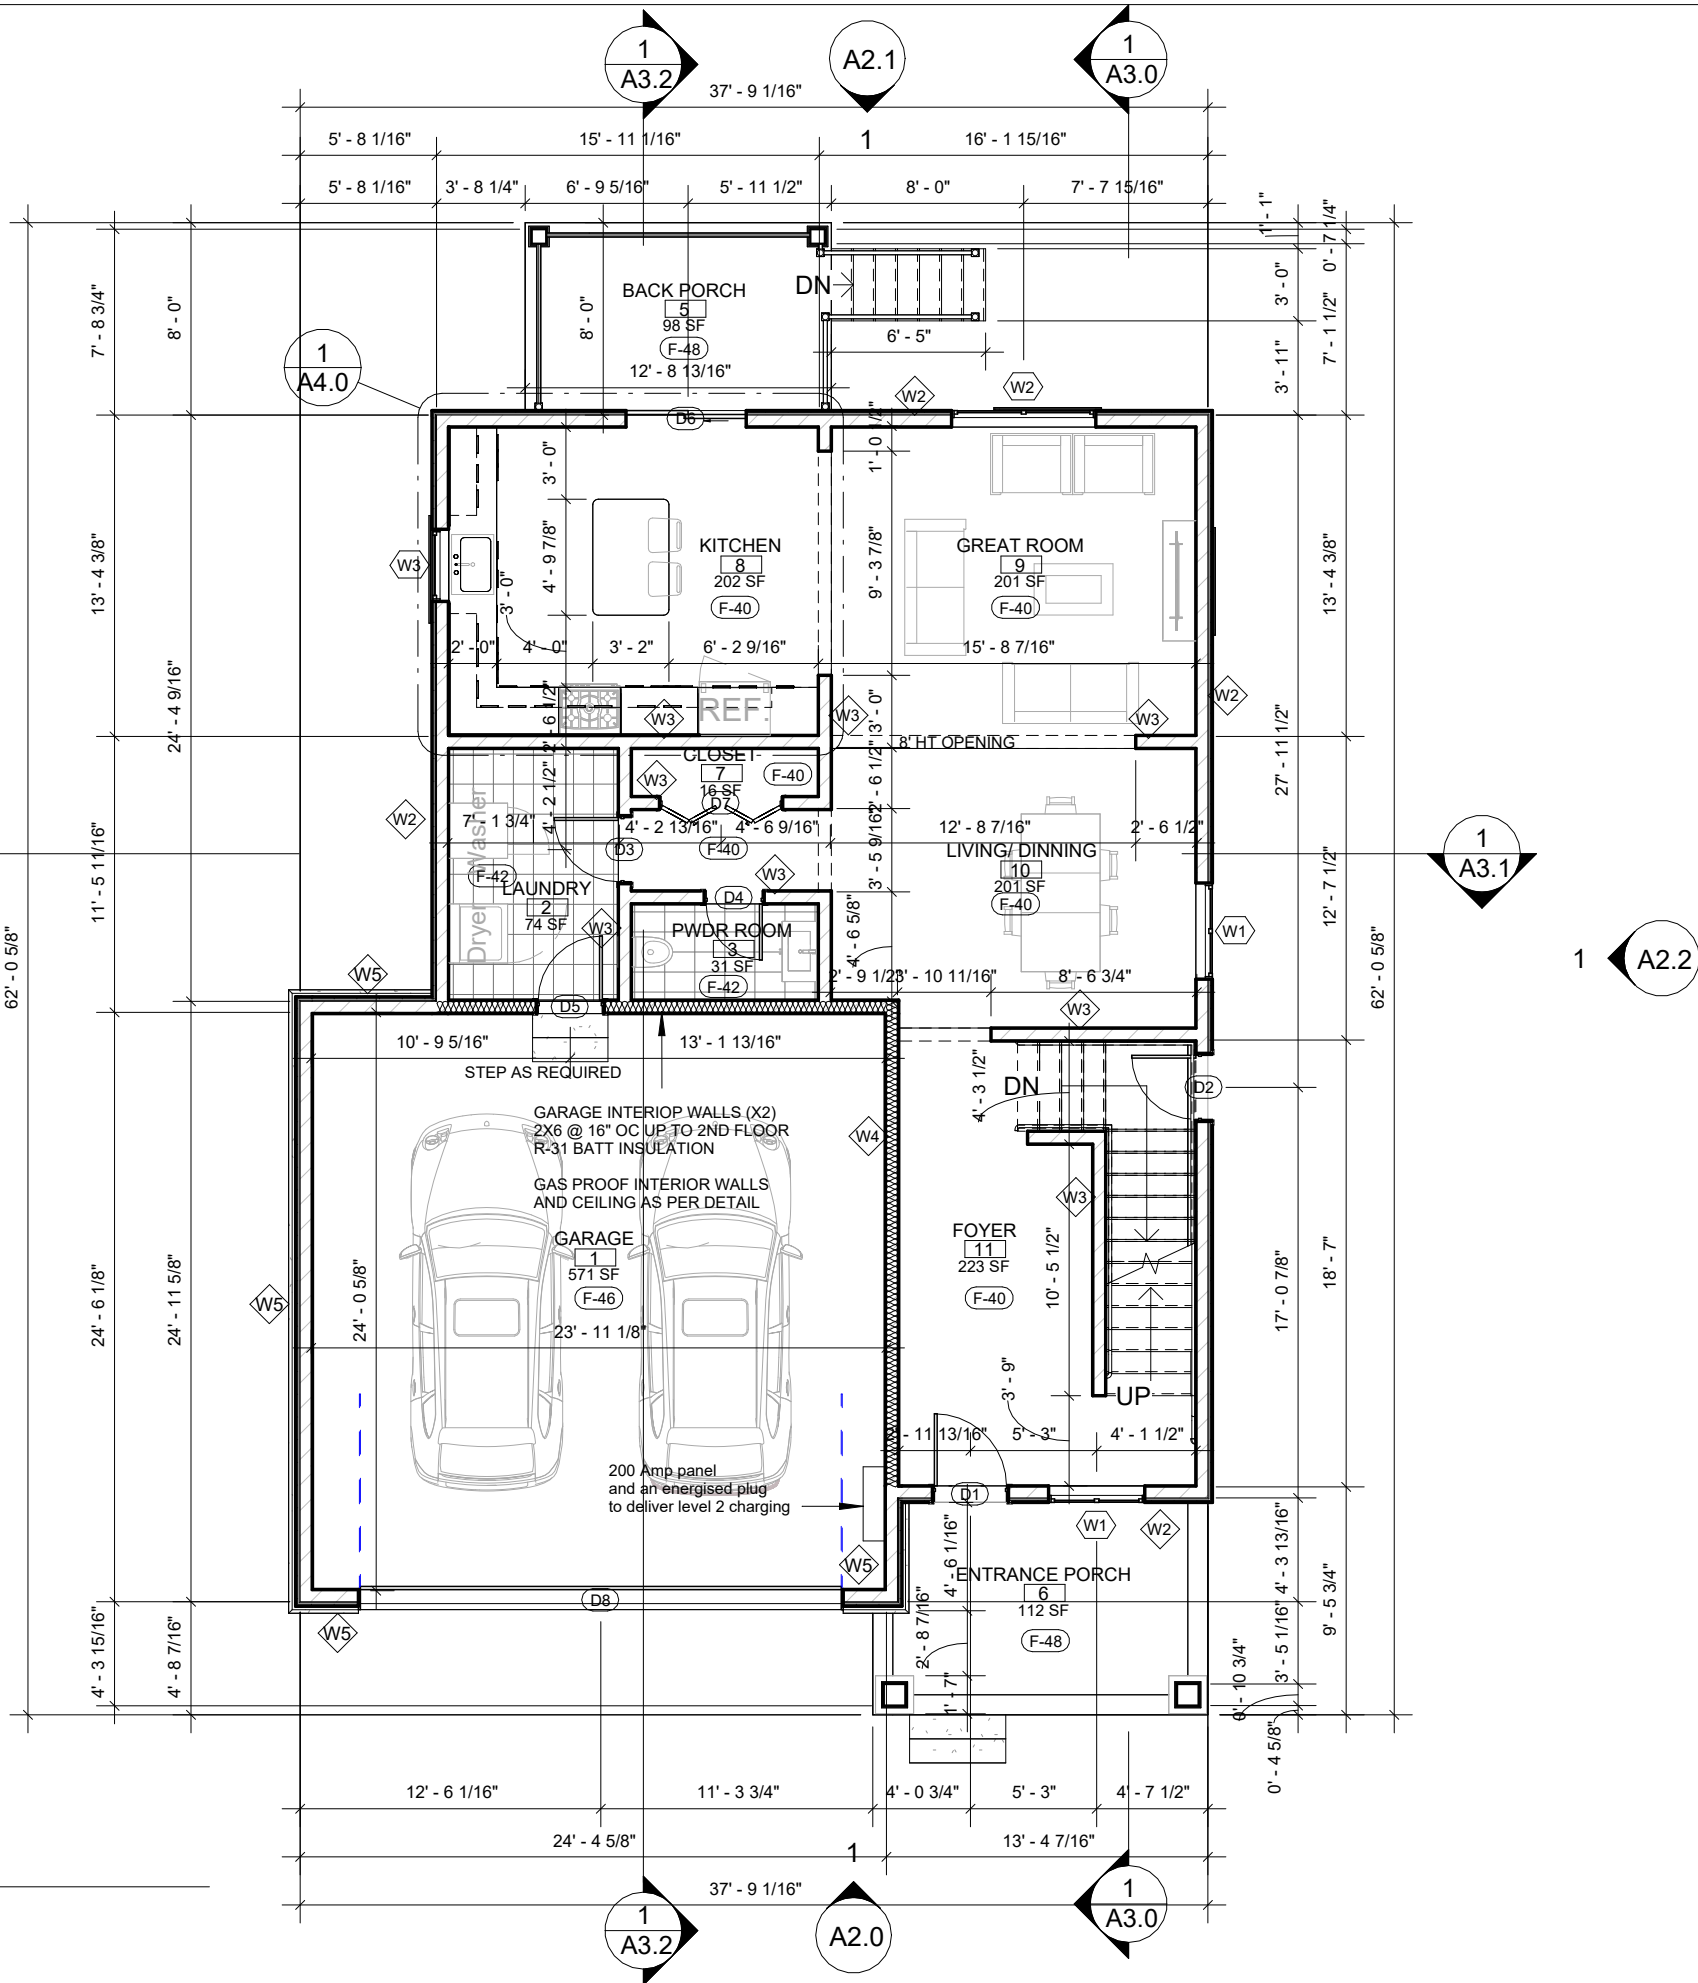

1
FIRST FLOOR
1/8" = 1'-0"

NOTES:

B	Y REVISED	JS	
A	X REVISED	JS	
REV	DESCRIPTION	BY	DATE

AMENDMENTS

ARCHITECT'S CONTACT DETAILS

NAME: VICTOR OMEH.

EMAIL: omehvictor@gmail.com

WEBSITE: www.victoromeh.github.io

PROJECT TITLE

SINGLE FAMILY HOME

SITE


509 BROOKHAVEN LANE,
WESTFIELD, IN 46074

CLIENT

MICHAEL & SARAH WHITFIELD

SCALE	DATE	DRAWN BY.
1/8" = 1'-0"	JAN 2026	VICTOR OMEH

SHEET NAME. FIRST FLOOR PLAN	SHEET NO.
PROJECT NO. VO-2026-101	A1.2

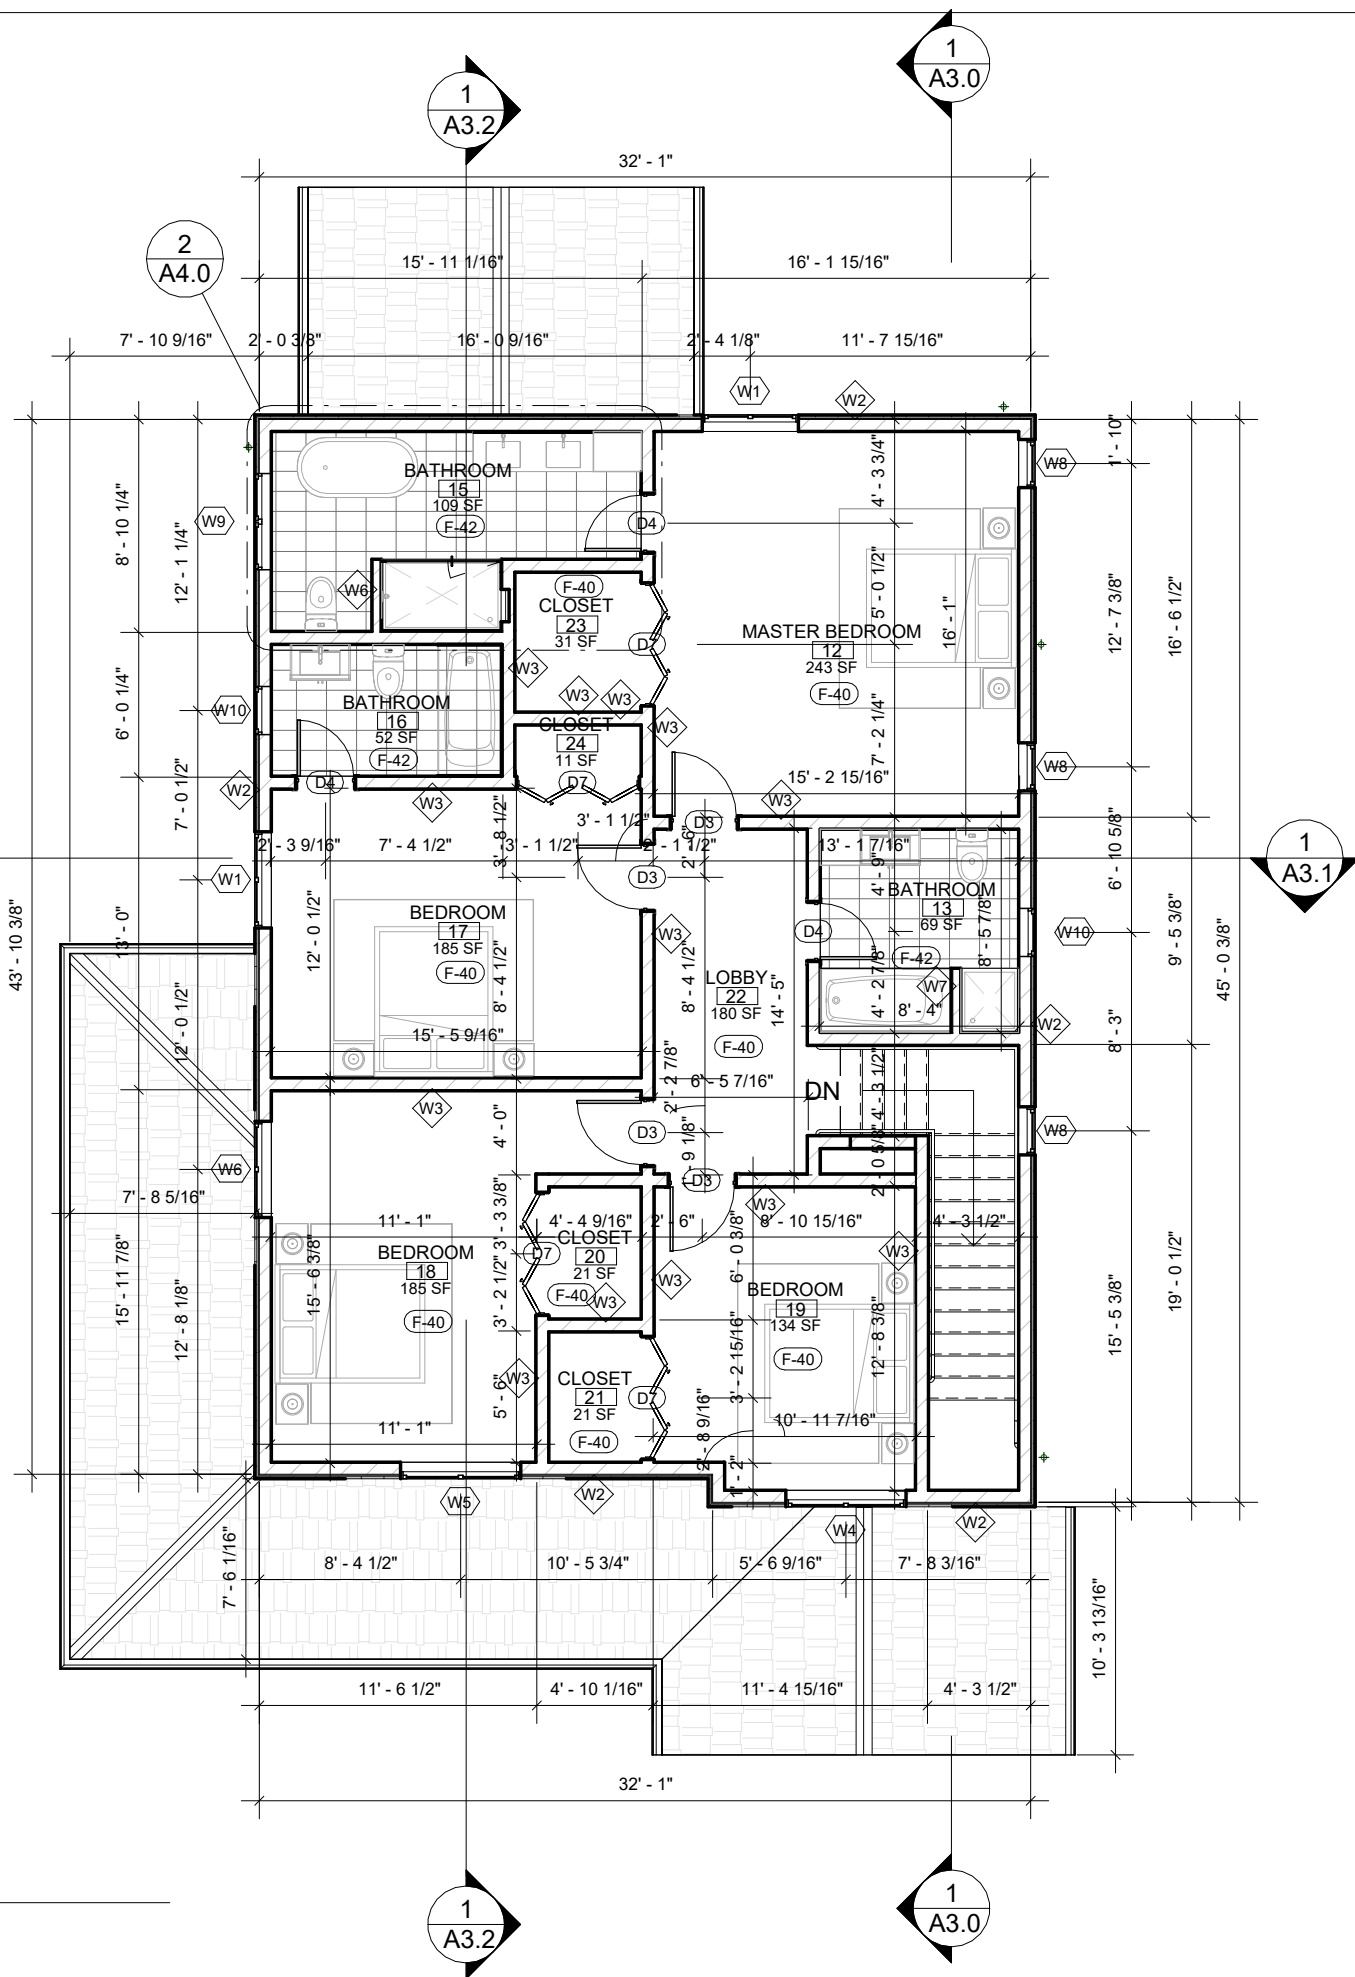

1

SECOND FLOOR
1/8" = 1'-0"

NOTES:

B	Y REVISED	JS	
A	X REVISED	JS	
REV	DESCRIPTION	BY	DATE

AMENDMENTS

ARCHITECT'S CONTACT DETAILS

NAME: VICTOR OMEH.

EMAIL: omehvictor@gmail.com

WEBSITE: www.victoromeh.github.io

PROJECT TITLE

SINGLE FAMILY HOME

SITE


509 BROOKHAVEN LANE,
WESTFIELD, IN 46074

CLIENT


MICHAEL & SARAH WHITFIELD

SCALE	DATE	DRAWN BY.
1/8" = 1'-0"	JAN 2026	VICTOR OMEH

SHEET NAME. SECOND FLOOR PLAN	SHEET NO.
PROJECT NO. VO-2026-101	A1.3

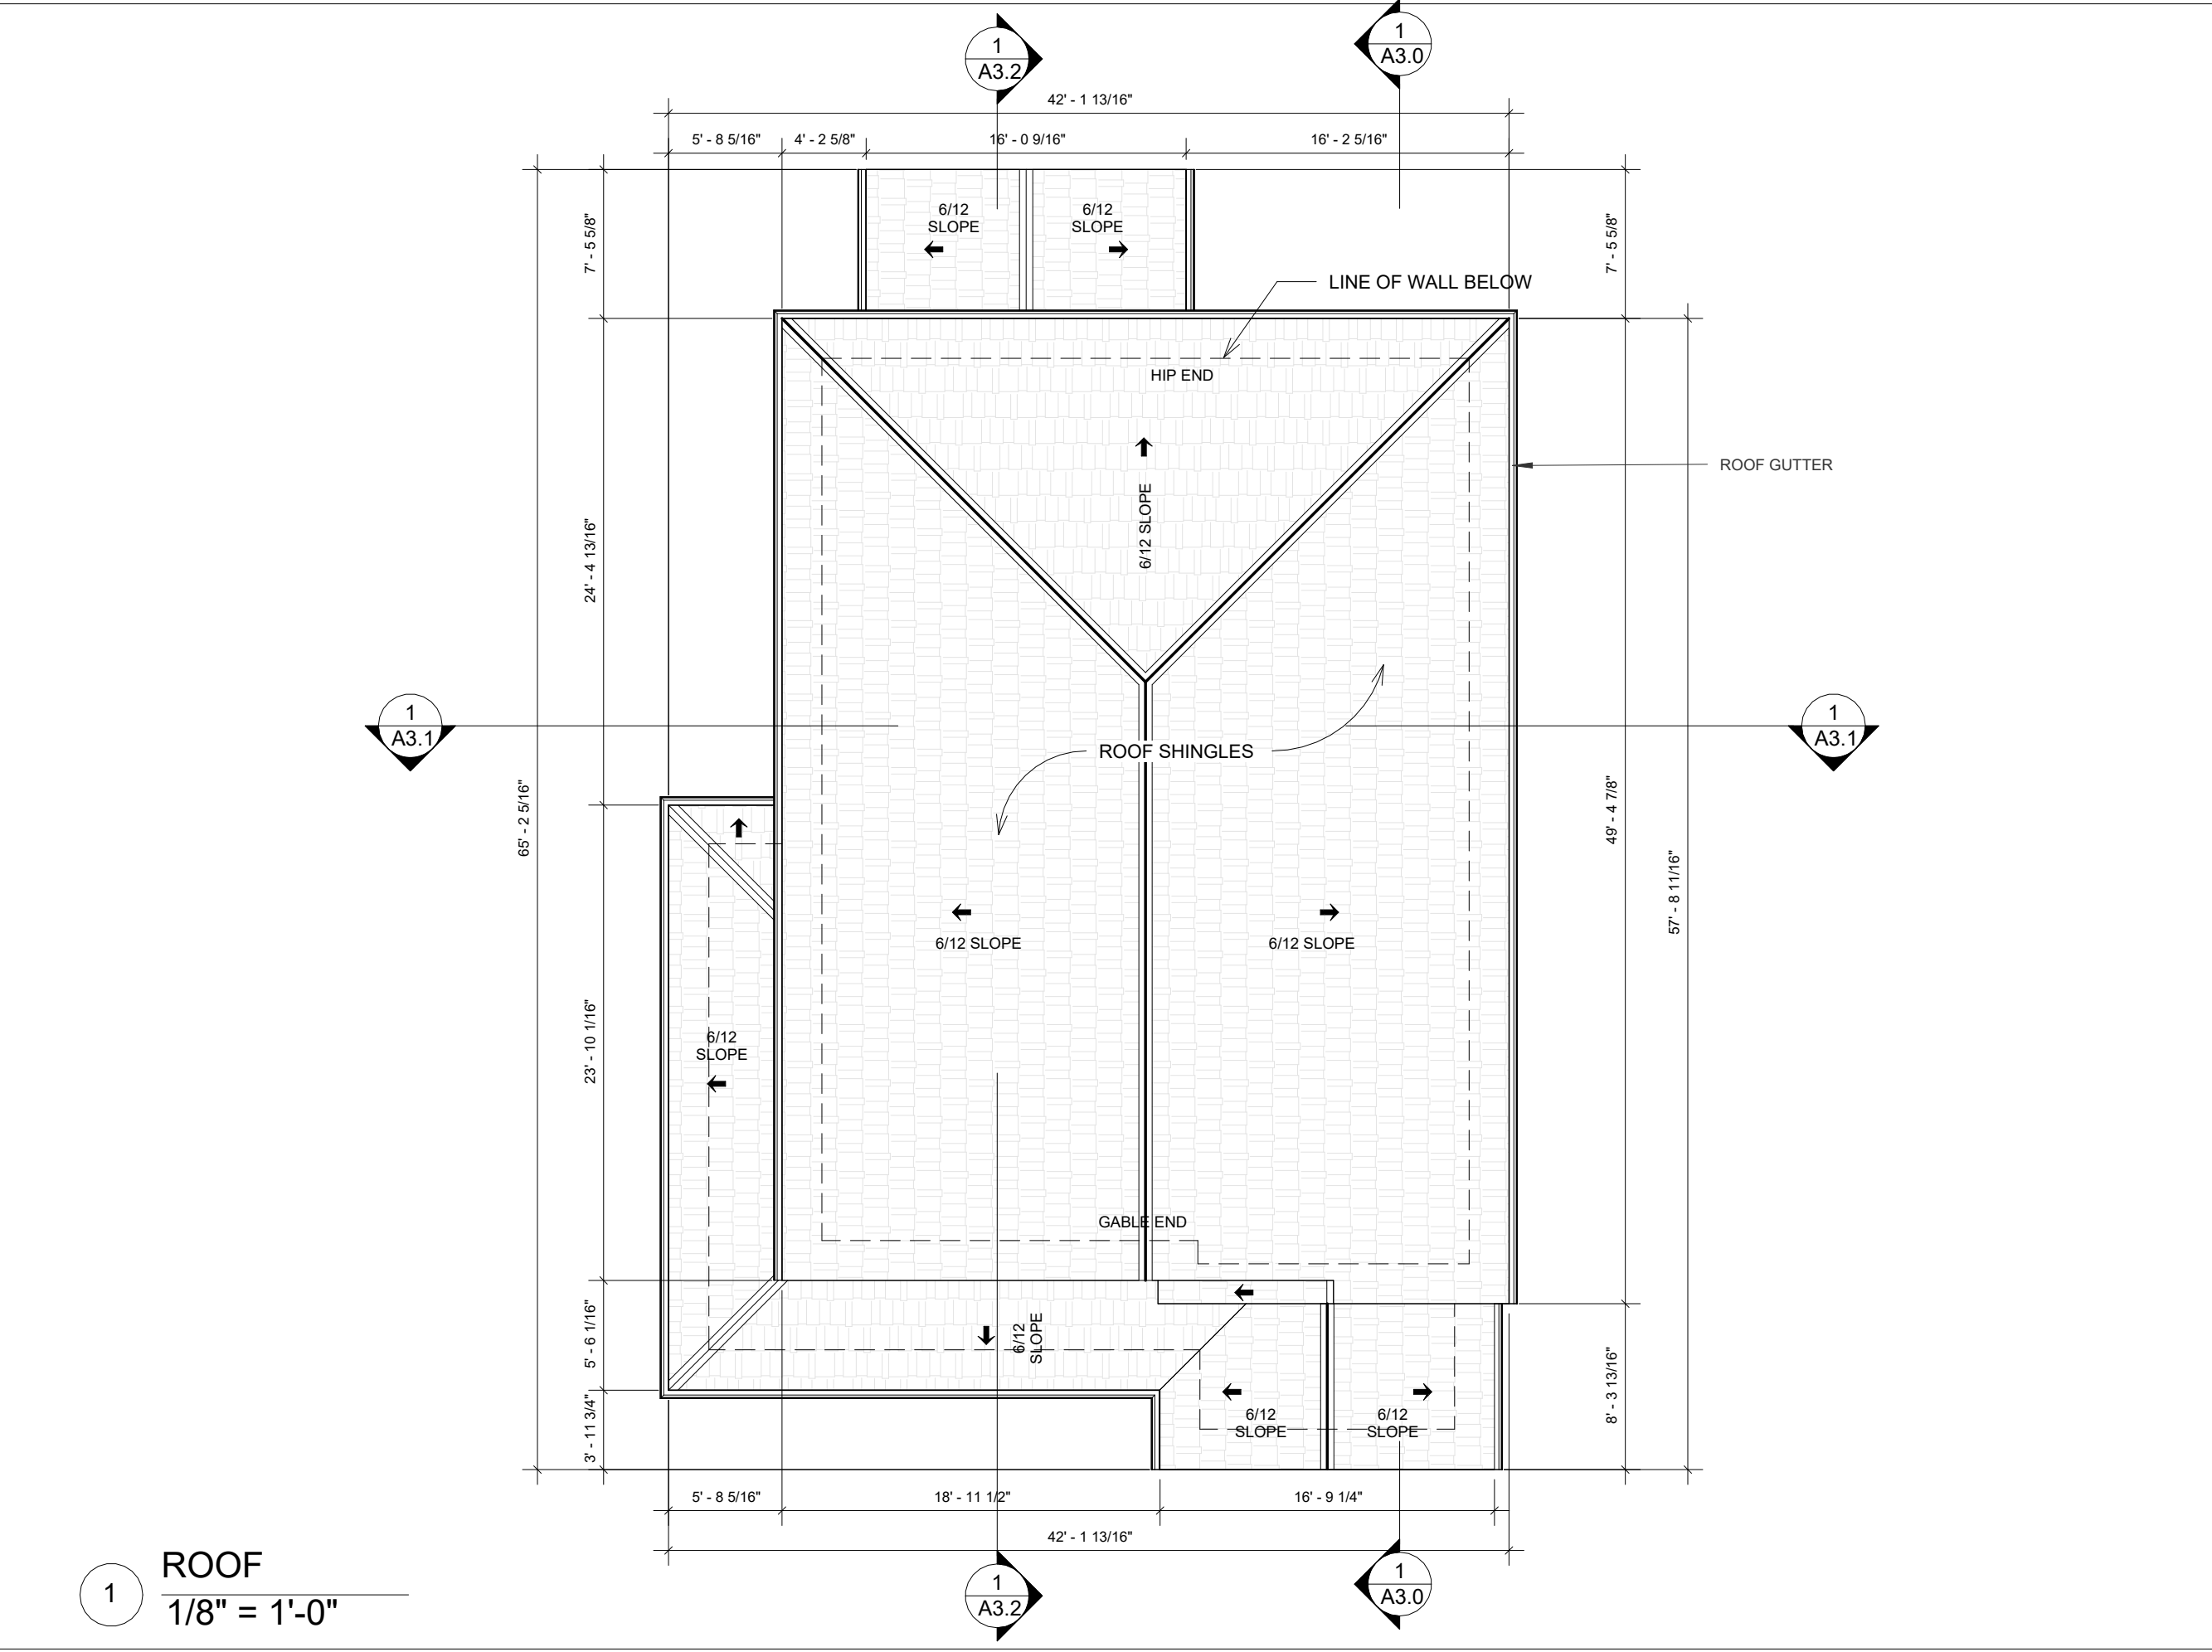

NOTES:			
B	Y REVISED	JS	
A	X REVISED	JS	
REV	DESCRIPTION	BY	DATE
AMENDMENTS			
ARCHITECT'S CONTACT DETAILS			
NAME:		VICTOR OMEH.	
EMAIL:		omehvictor@gmail.com	
WEBSITE:		www.victoromeh.github.io	
PROJECT TITLE			
SINGLE FAMILY HOME			
SITE			
509 BROOKHAVEN LANE, WESTFIELD, IN 46074			
CLIENT			
MICHAEL & SARAH WHITFIELD			
SCALE	DATE.		DRAWN BY.
1/8" = 1'-0"	JAN 2026		VICTOR OMEH
SHEET NAME. ROOF PLAN			SHEET NO.
PROJECT NO. VO-2026-101			A1.4

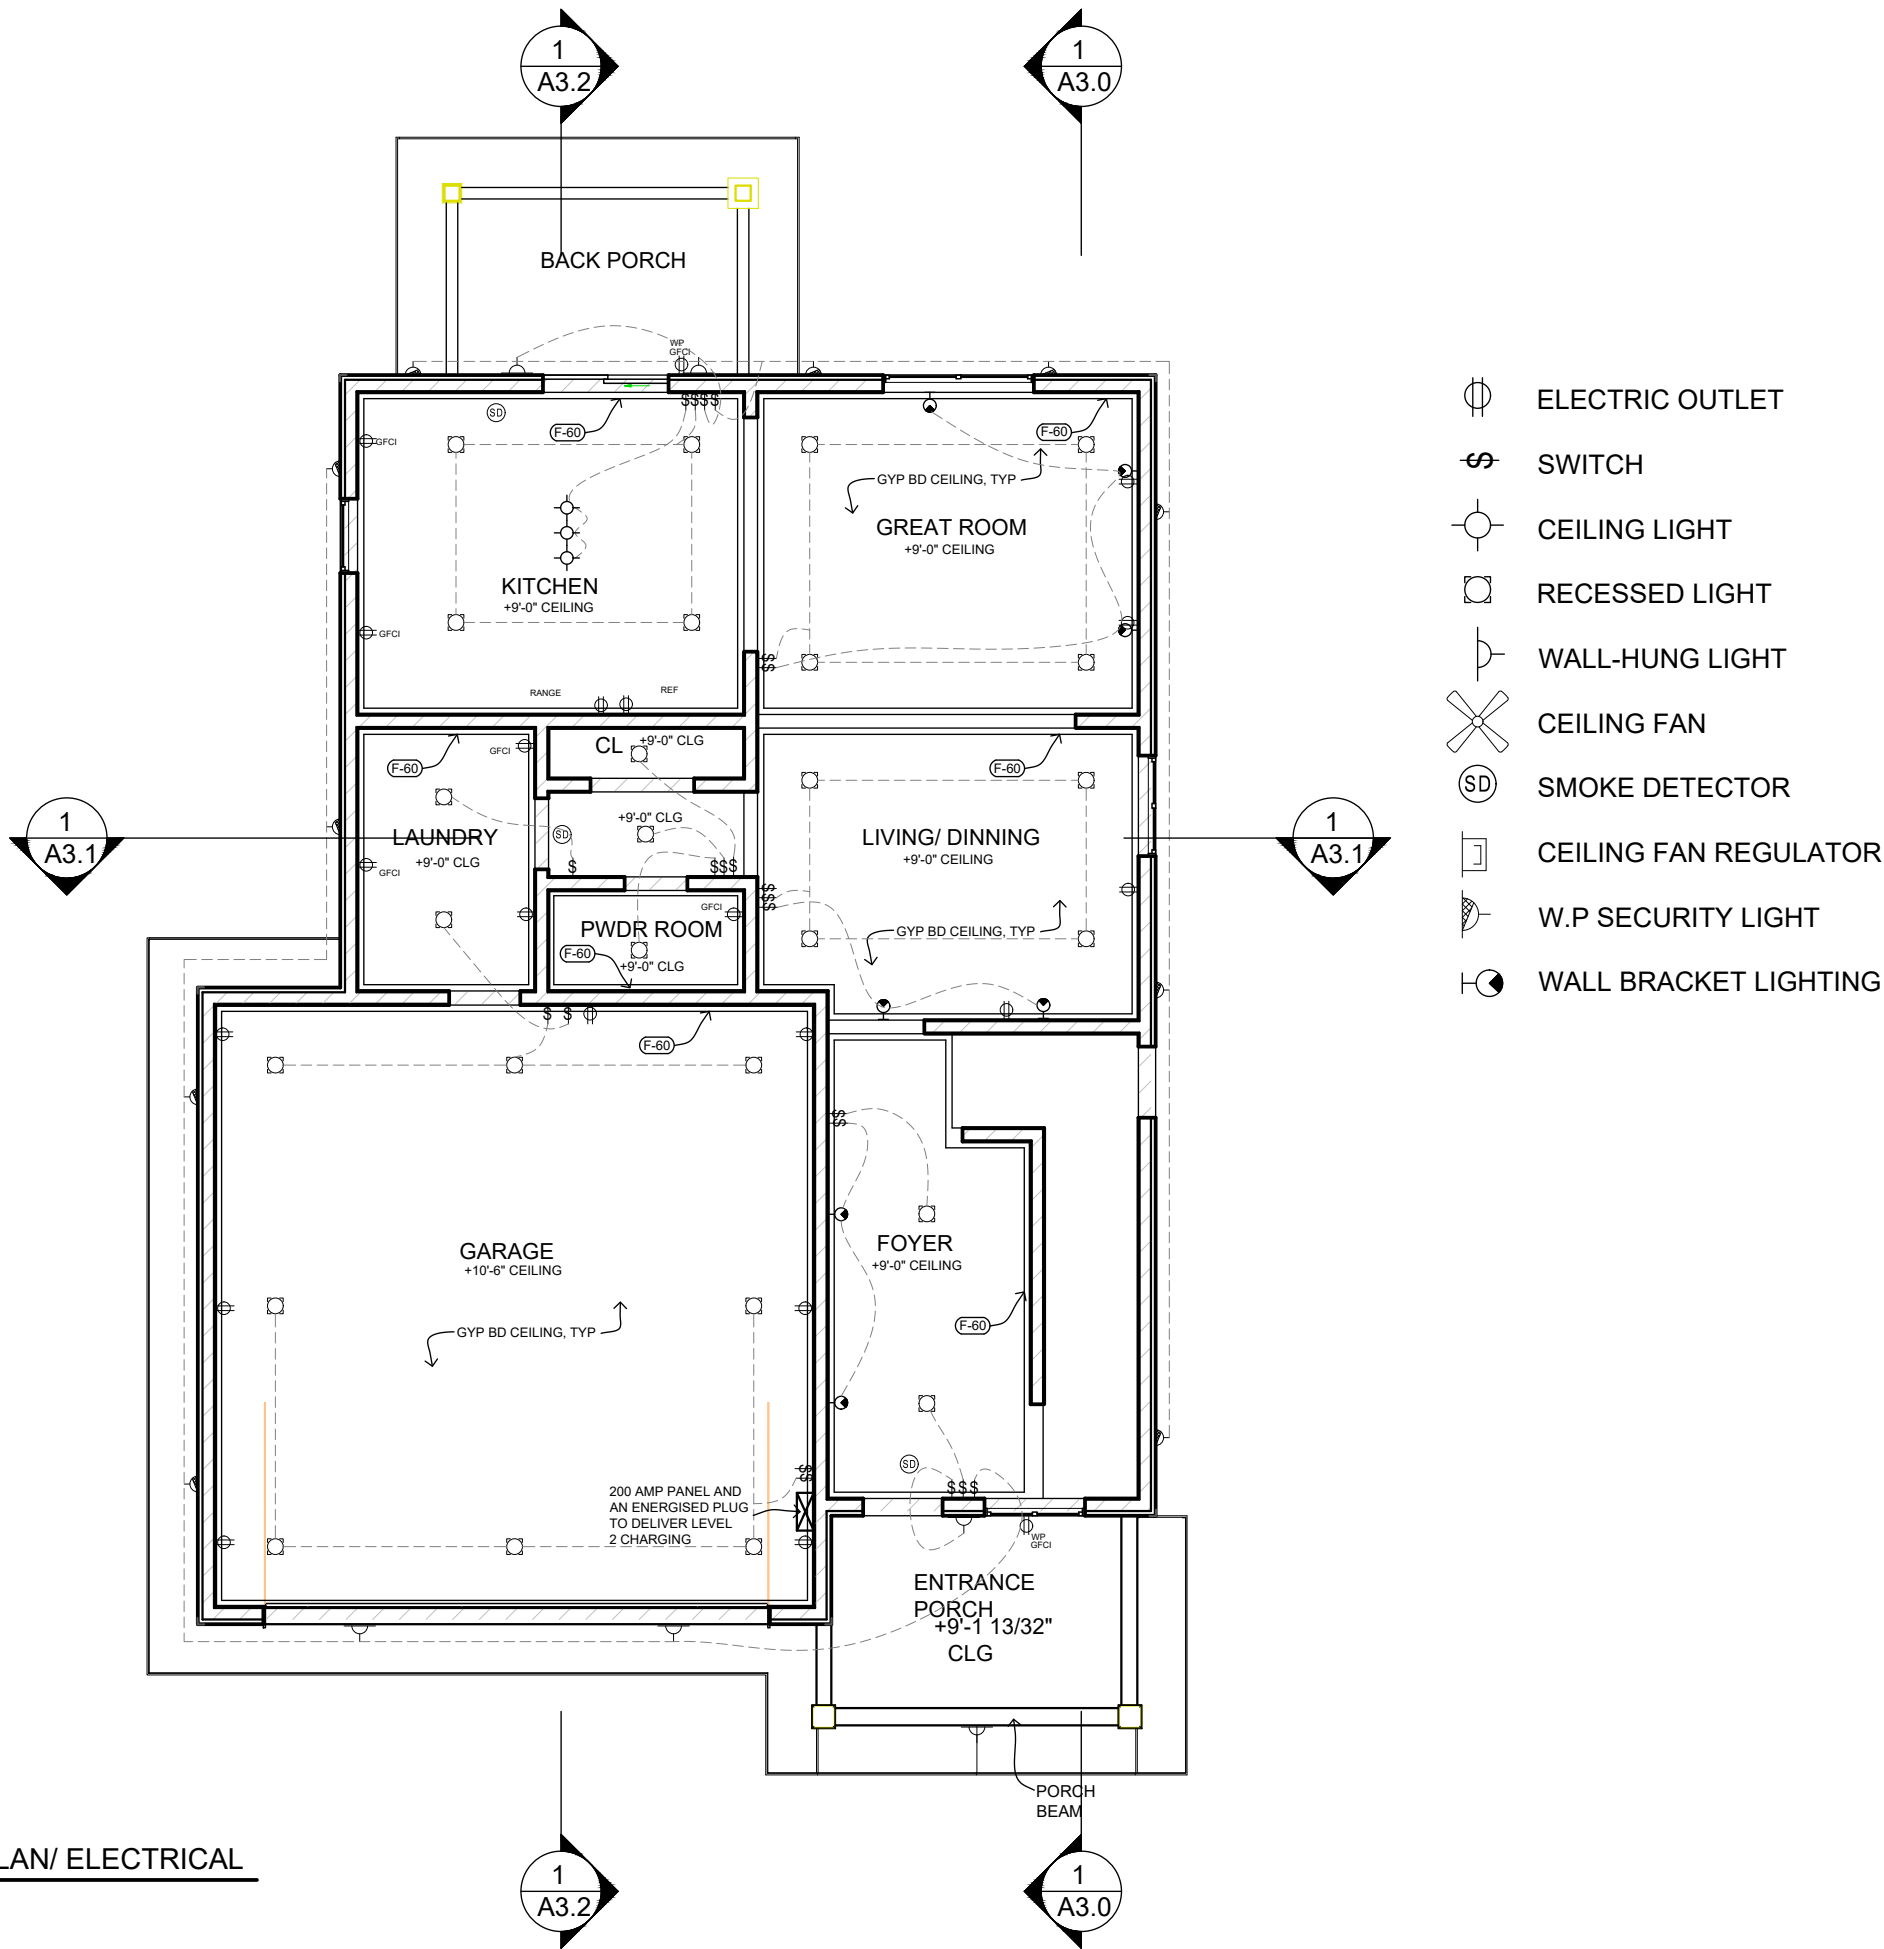

1 1ST FLOOR REFLECTED CEILING PLAN/ ELECTRICAL

NOTES:

B	Y REVISED	JS	
A	X REVISED	JS	
REV	DESCRIPTION	BY	DATE

AMENDMENTS

ARCHITECT'S CONTACT DETAILS

NAME: VICTOR OMEH
EMAIL: omehvictor@gmail.com
WEBSITE: www.victoromeh.github.io

PROJECT TITLE

SINGLE FAMILY HOME

SITE


509 BROOKHAVEN LANE,
WESTFIELD, IN 46074

CLIENT

MICHAEL & SARAH WHITFIELD

SCALE	DATE. JAN 2026	DRAWN BY. VICTOR OMEH
-------	-------------------	--------------------------

SHEET NAME REFLECTED CEILING PLAN	SHEET NO. A1.5
PROJECT NO. VO-2026-101	

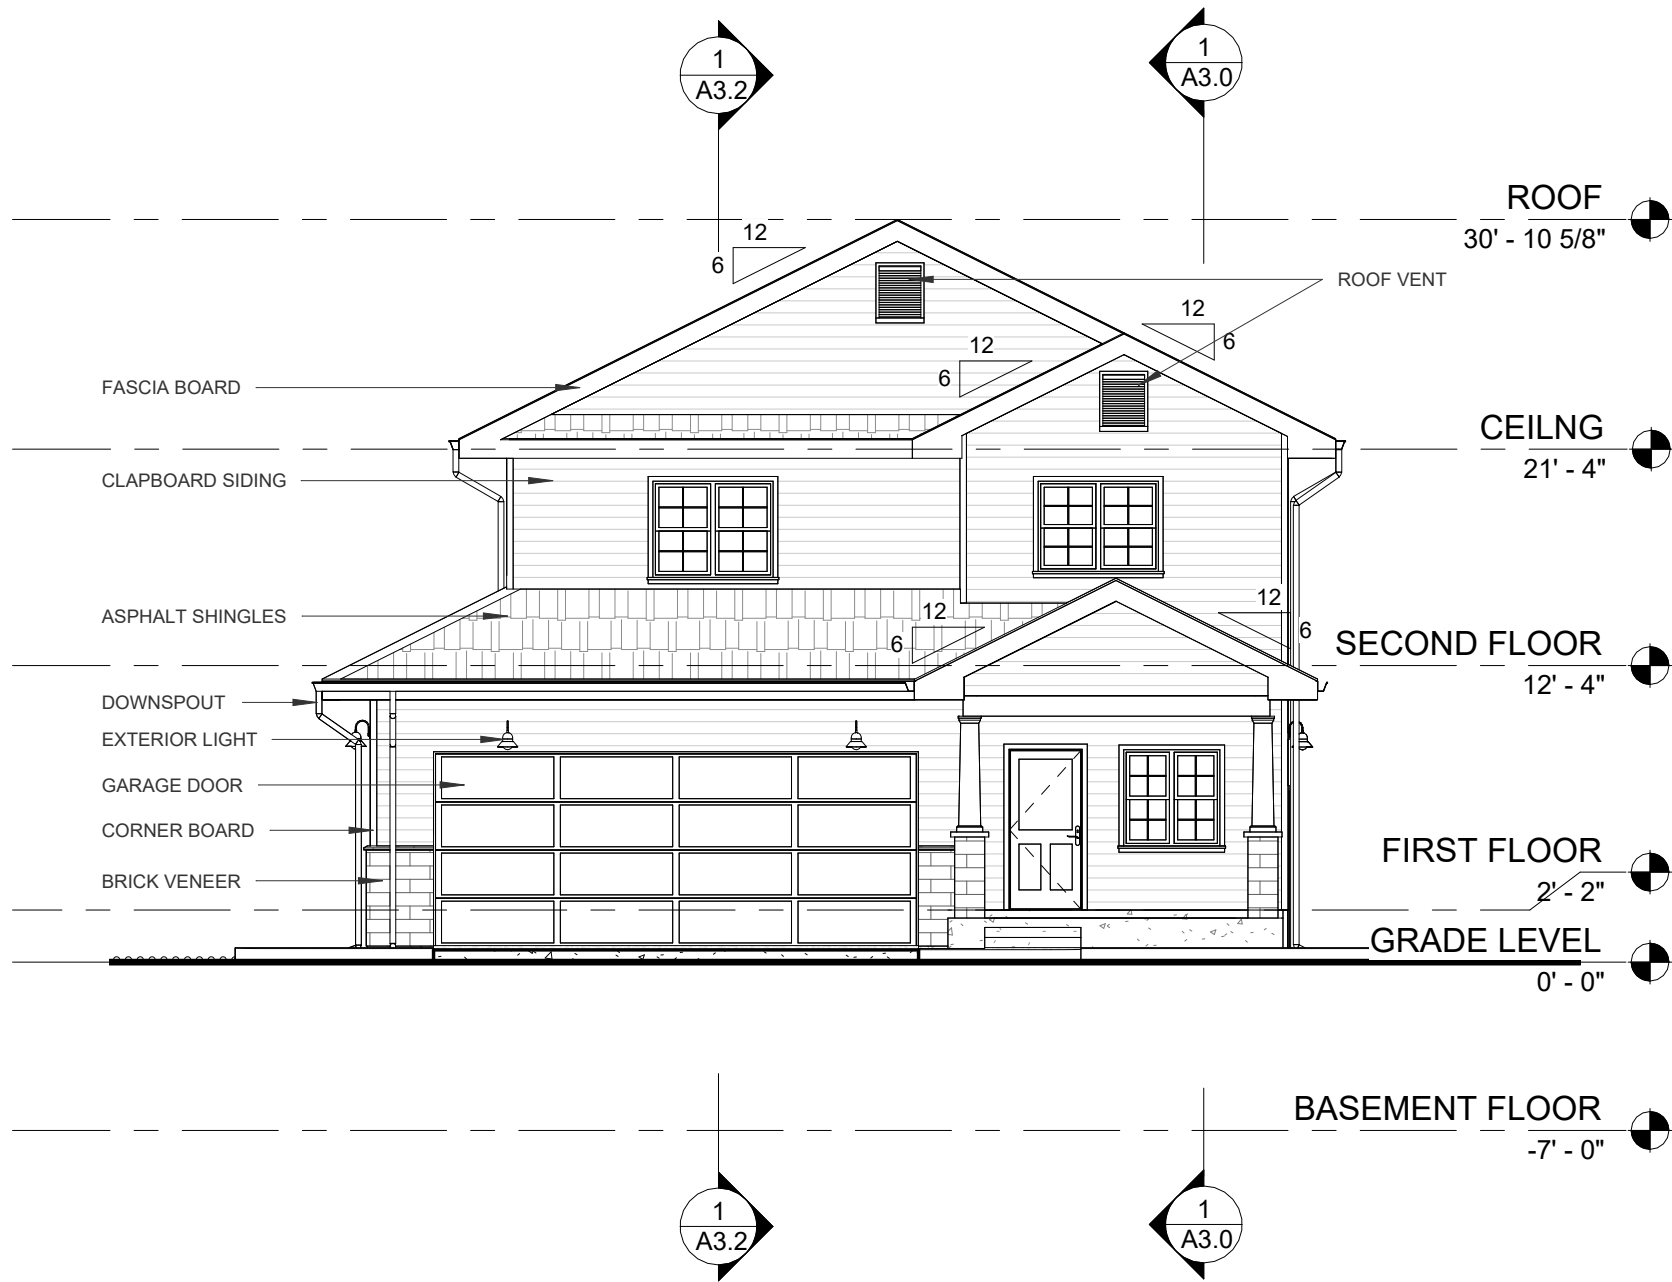

1 SOUTH ELEVATION
1/8" = 1'-0"

NOTES:

B	Y REVISED	JS	
A	X REVISED	JS	
REV	DESCRIPTION	BY	DATE

AMENDMENTS

ARCHITECT'S CONTACT DETAILS

NAME: VICTOR OMEH.

EMAIL: omehvictor@gmail.com

WEBSITE: www.victoromeh.github.io

PROJECT TITLE

SINGLE FAMILY HOME

SITE


509 BROOKHAVEN LANE,
WESTFIELD, IN 46074

CLIENT

MICHAEL & SARAH WHITFIELD

SCALE	DATE.	DRAWN BY.
1/8" = 1'-0"	JAN 2026	VICTOR OMEH

SHEET NAME. SOUTH ELEVATION		SHEET NO. A2.0
PROJECT NO. VO-2026-101		

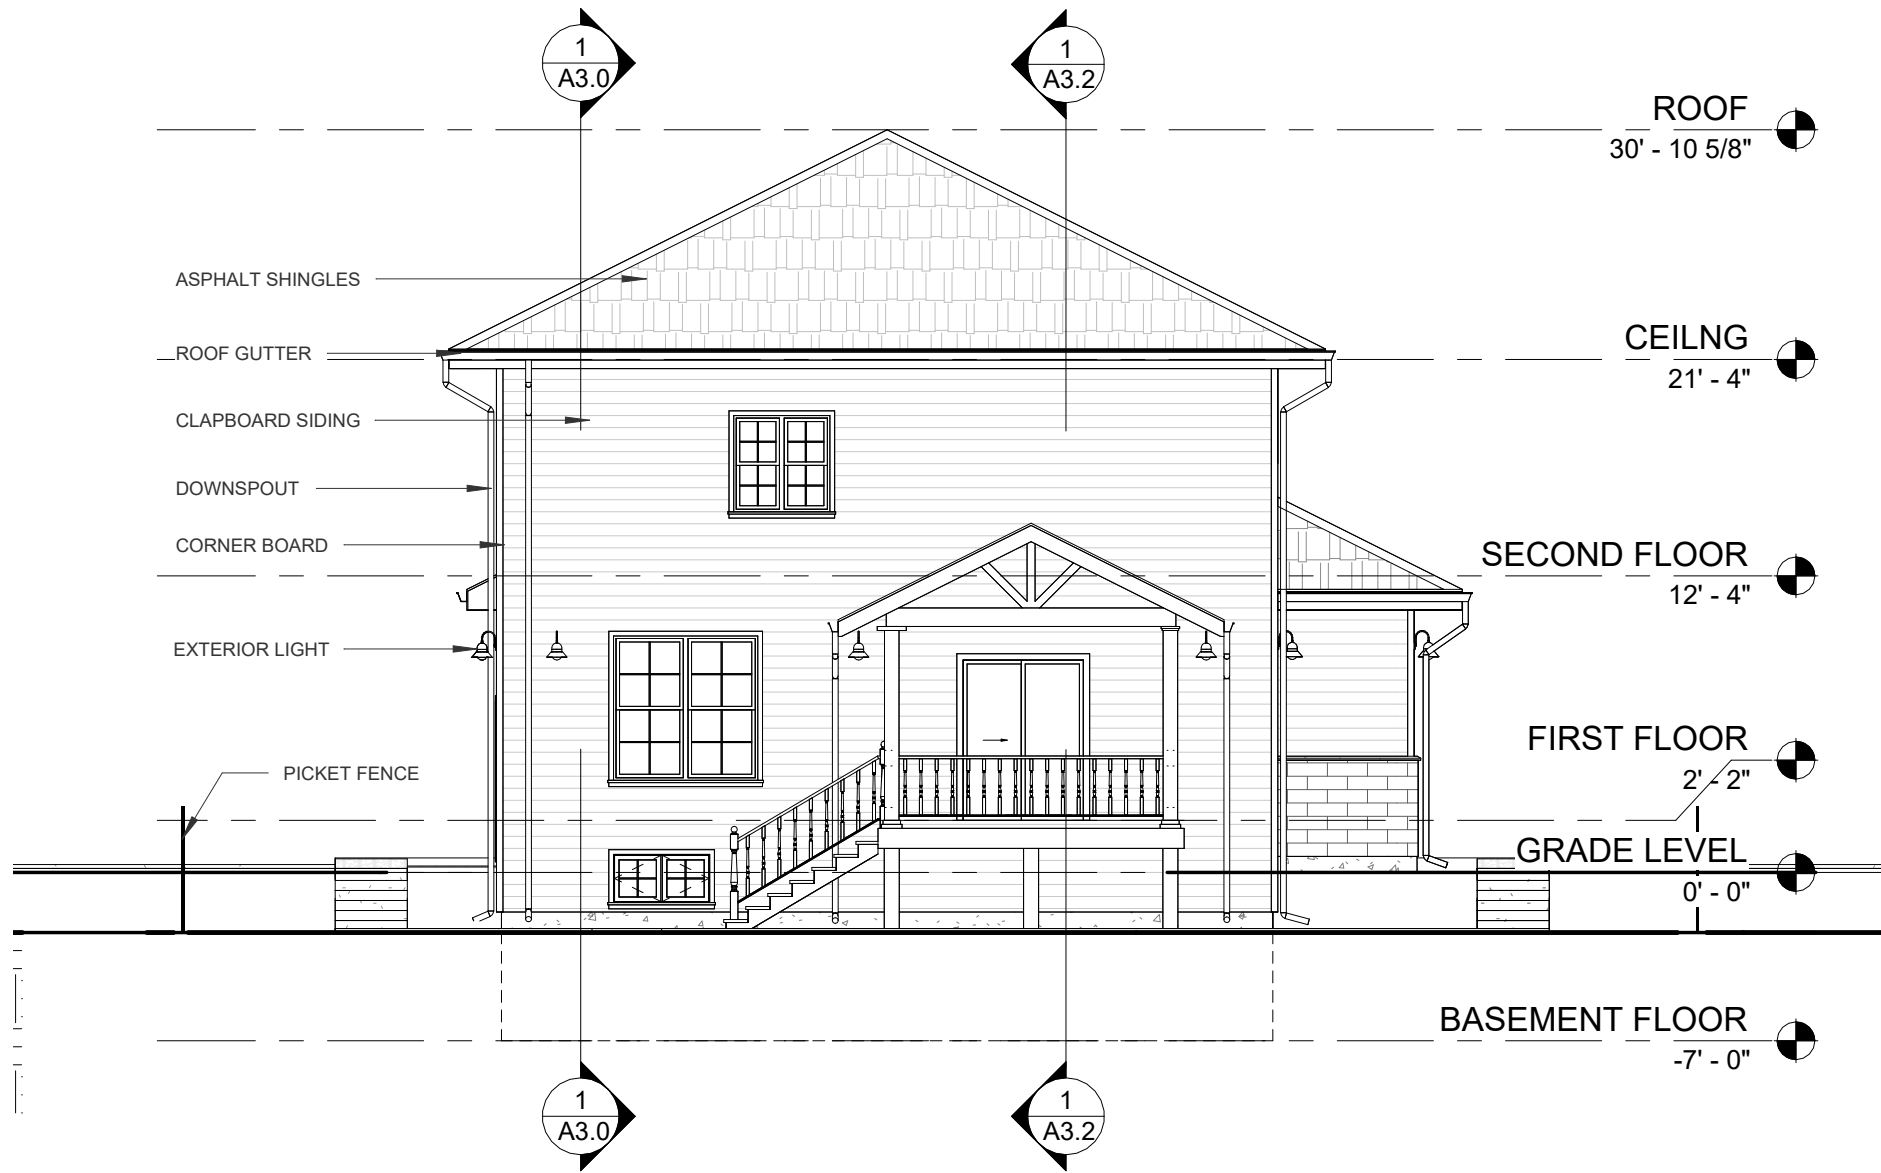

1 NORTH ELEVATION
1/8" = 1'-0"

NOTES:

B	Y REVISED	JS	
A	X REVISED	JS	
REV	DESCRIPTION	BY	DATE

AMENDMENTS

ARCHITECT'S CONTACT DETAILS

NAME: VICTOR OMEH.
EMAIL: omehvictor@gmail.com
WEBSITE: www.victoromeh.github.io

PROJECT TITLE

SINGLE FAMILY HOME

SITE


509 BROOKHAVEN LANE,
WESTFIELD, IN 46074

CLIENT

MICHAEL & SARAH WHITFIELD

SCALE 1/8" = 1'-0"	DATE JAN 2026	DRAWN BY. VICTOR OMEH
--------------------------	------------------	-----------------------------

SHEET NAME. NORTH ELEVATION	SHEET NO. A2.1
PROJECT NO. VO-2026-101	

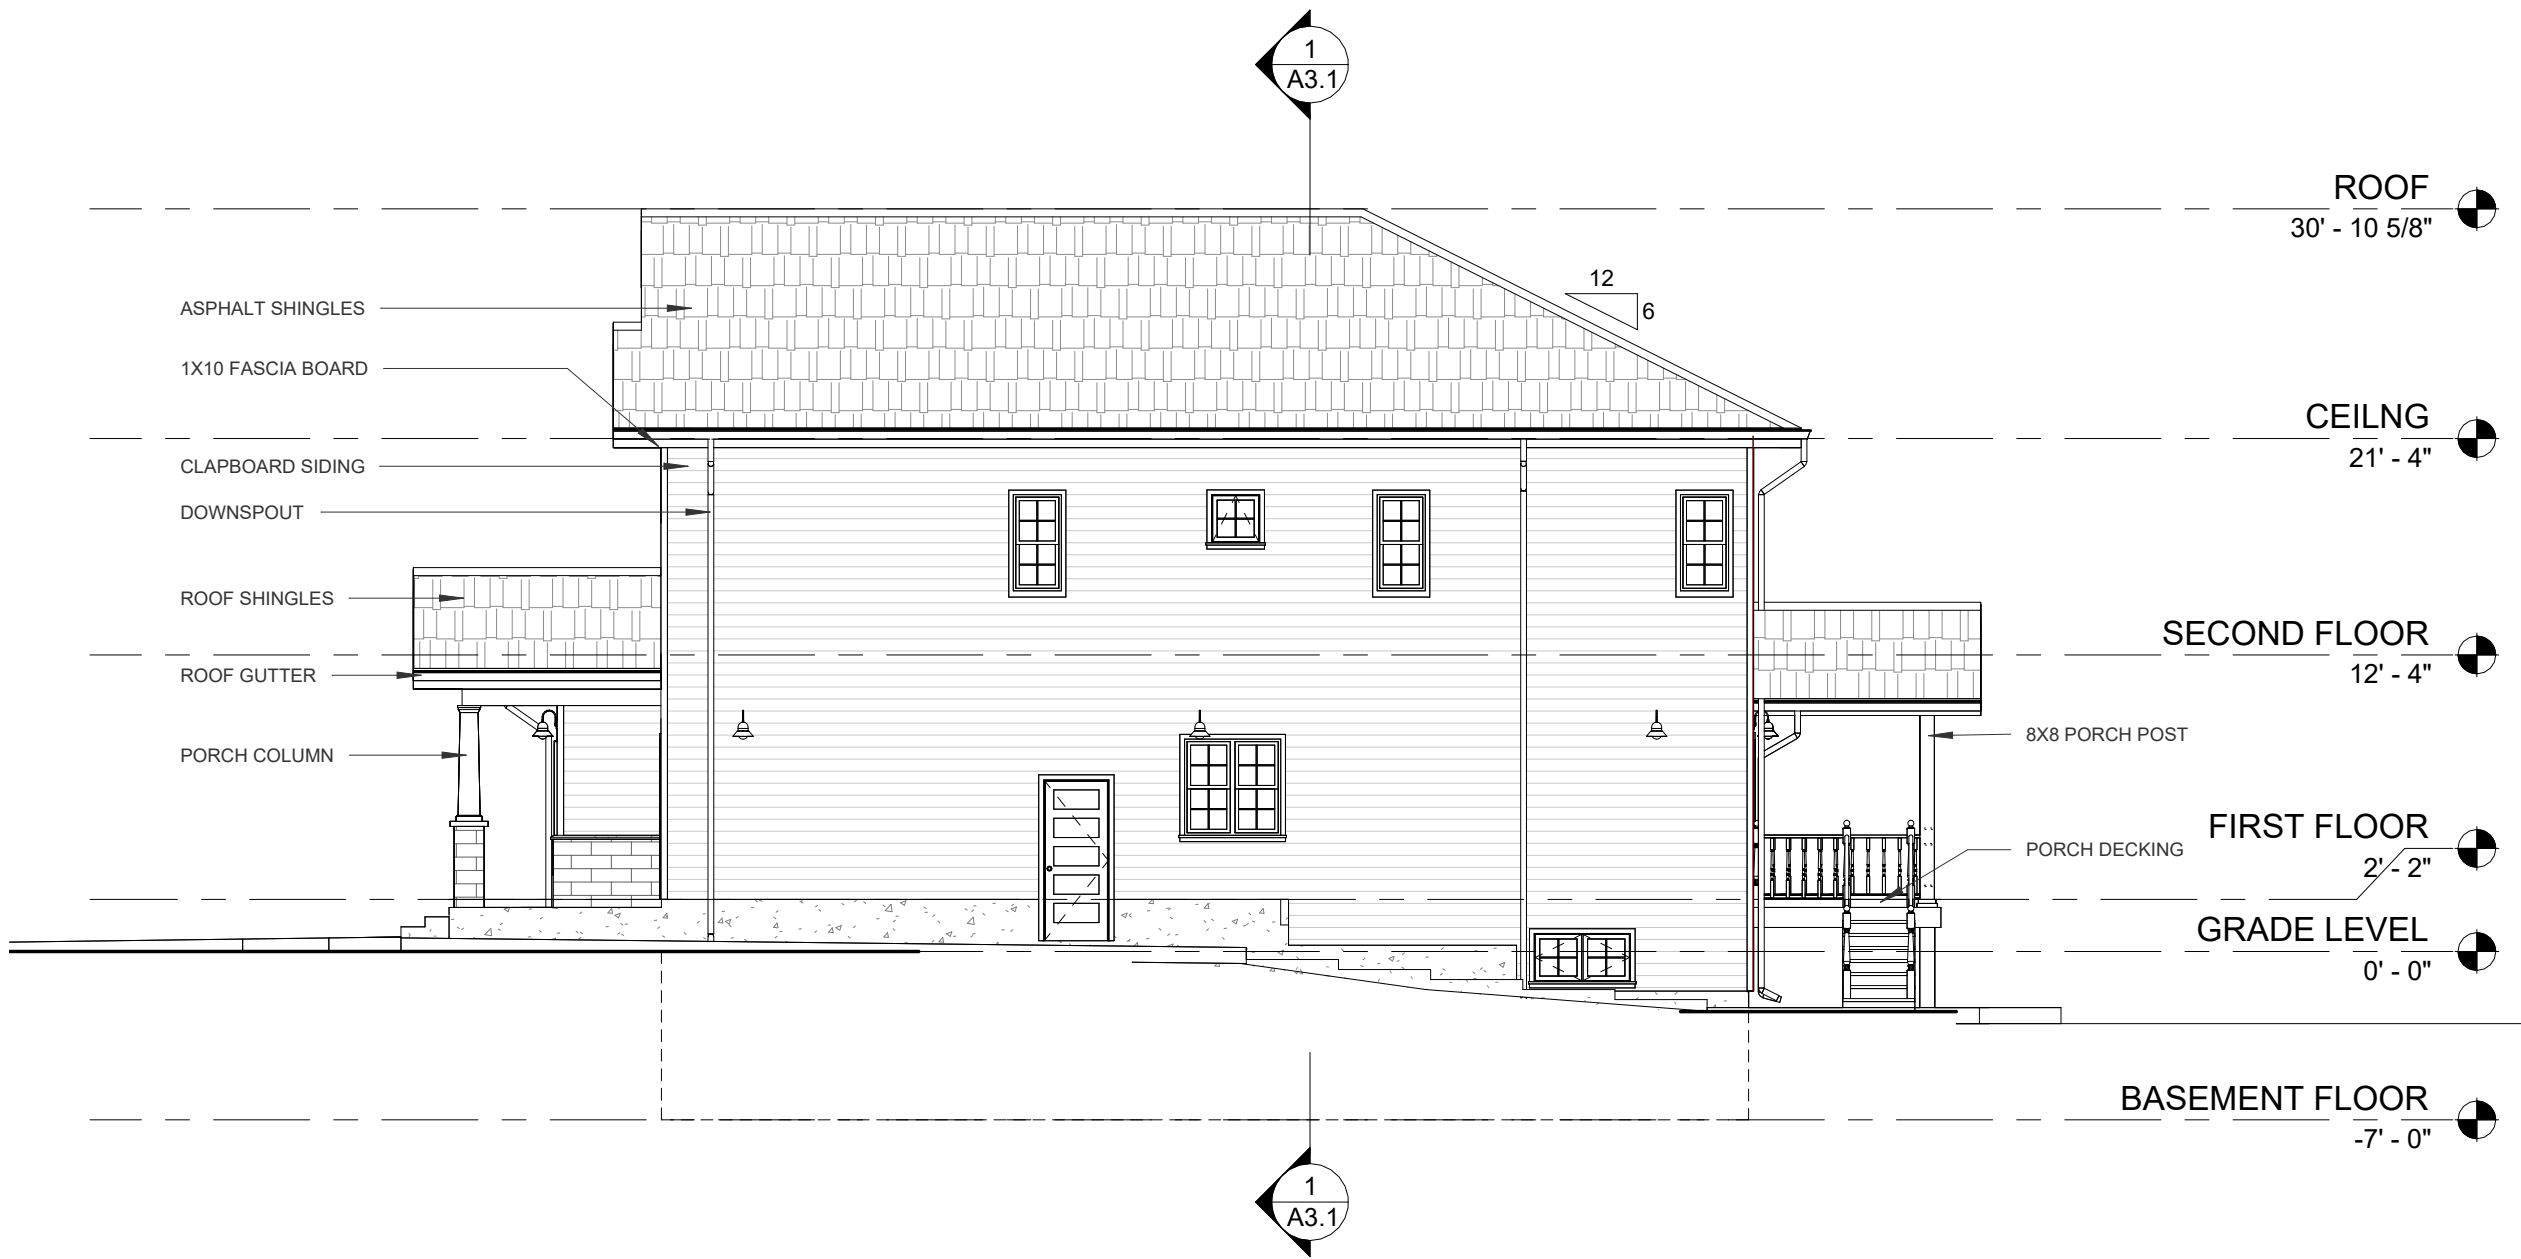

EAST ELEVATION
1/8" = 1'-0"

NOTES:

B	Y REVISED	JS	
A	X REVISED	JS	
REV	DESCRIPTION	BY	DATE

AMENDMENTS

ARCHITECT'S CONTACT DETAILS

NAME: VICTOR OMEH.

EMAIL: omehvictor@gmail.com

WEBSITE: www.victoromeh.github.io

PROJECT TITLE

SINGLE FAMILY HOME

SITE


**509 BROOKHAVEN LANE,
WESTFIELD, IN 46074**

CLIENT

MICHAEL & SARAH WHITFIELD

SCALE 1/8" = 1'-0"	DATE. JAN 2026	DRAWN BY. VICTOR OMEH
---------------------------------	--------------------------	------------------------------------

SHEET NAME. EAST ELEVATION		SHEET NO. A2.2
PROJECT NO. VO-2026-101		

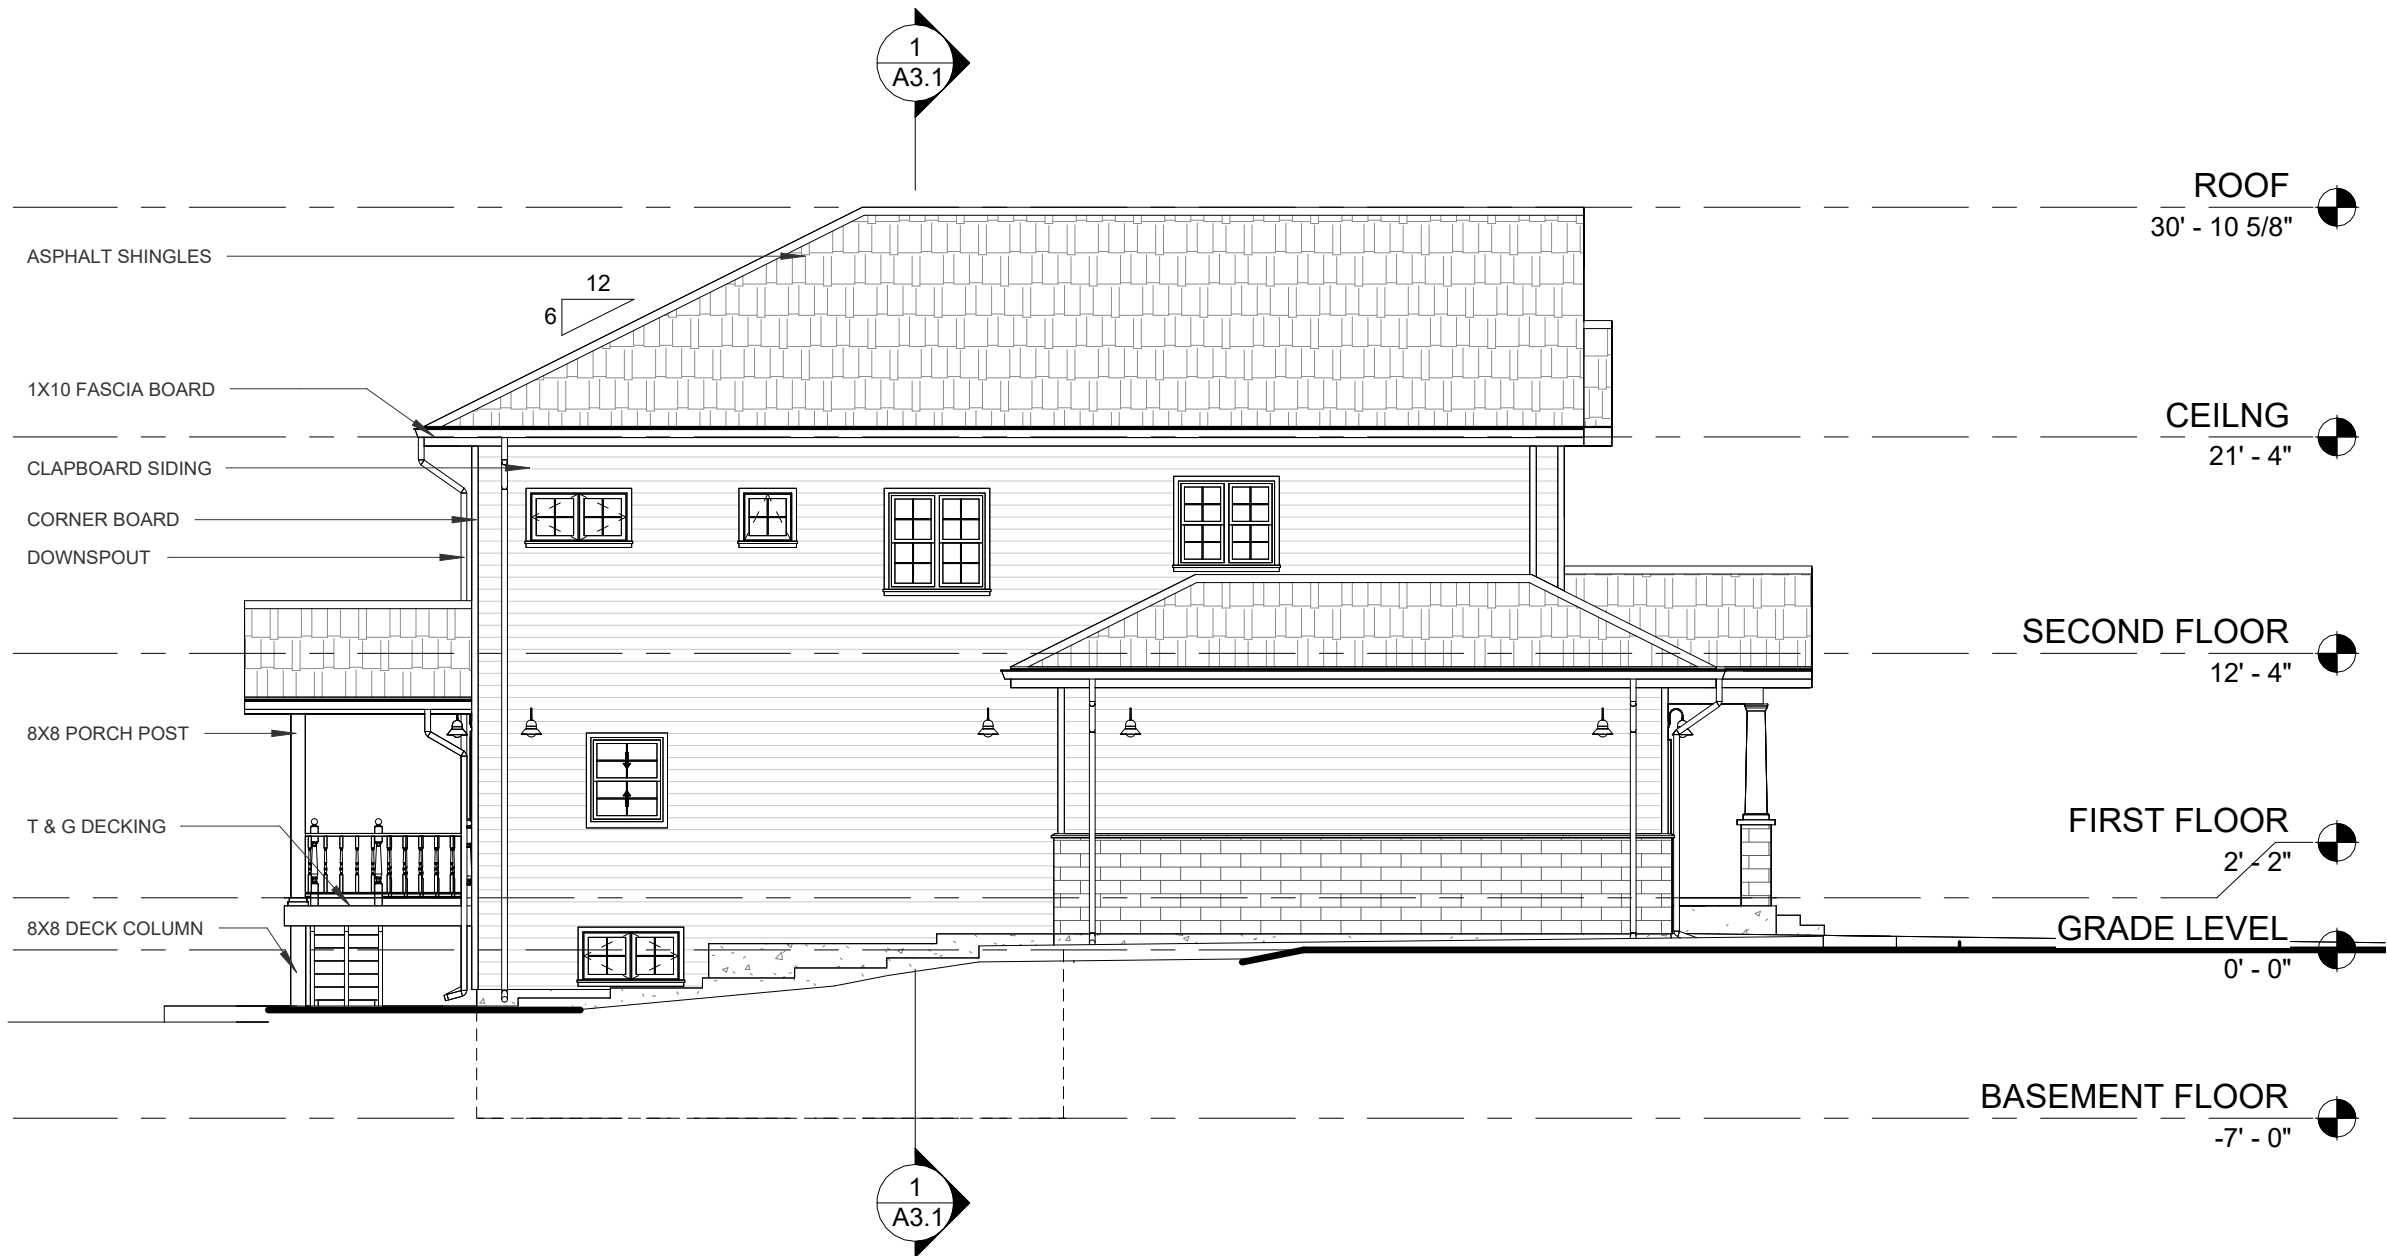

1

WEST ELEVATION
1/8" = 1'-0"

NOTES:

B	Y REVISED	JS	
A	X REVISED	JS	
REV	DESCRIPTION	BY	DATE

AMENDMENTS

ARCHITECT'S CONTACT DETAILS

NAME: VICTOR OMEH.
EMAIL: omehvictor@gmail.com
WEBSITE: www.victoromeh.github.io

PROJECT TITLE

SINGLE FAMILY HOME

SITE

509 BROOKHAVEN LANE,
WESTFIELD, IN 46074

CLIENT


MICHAEL & SARAH WHITFIELD

SCALE	DATE	DRAWN BY.
1/8" = 1'-0"	JAN 2026	VICTOR OMEH

SHEET NAME. WEST ELEVATION SHEET NO.

PROJECT NO. VO-2026-101

A2.3

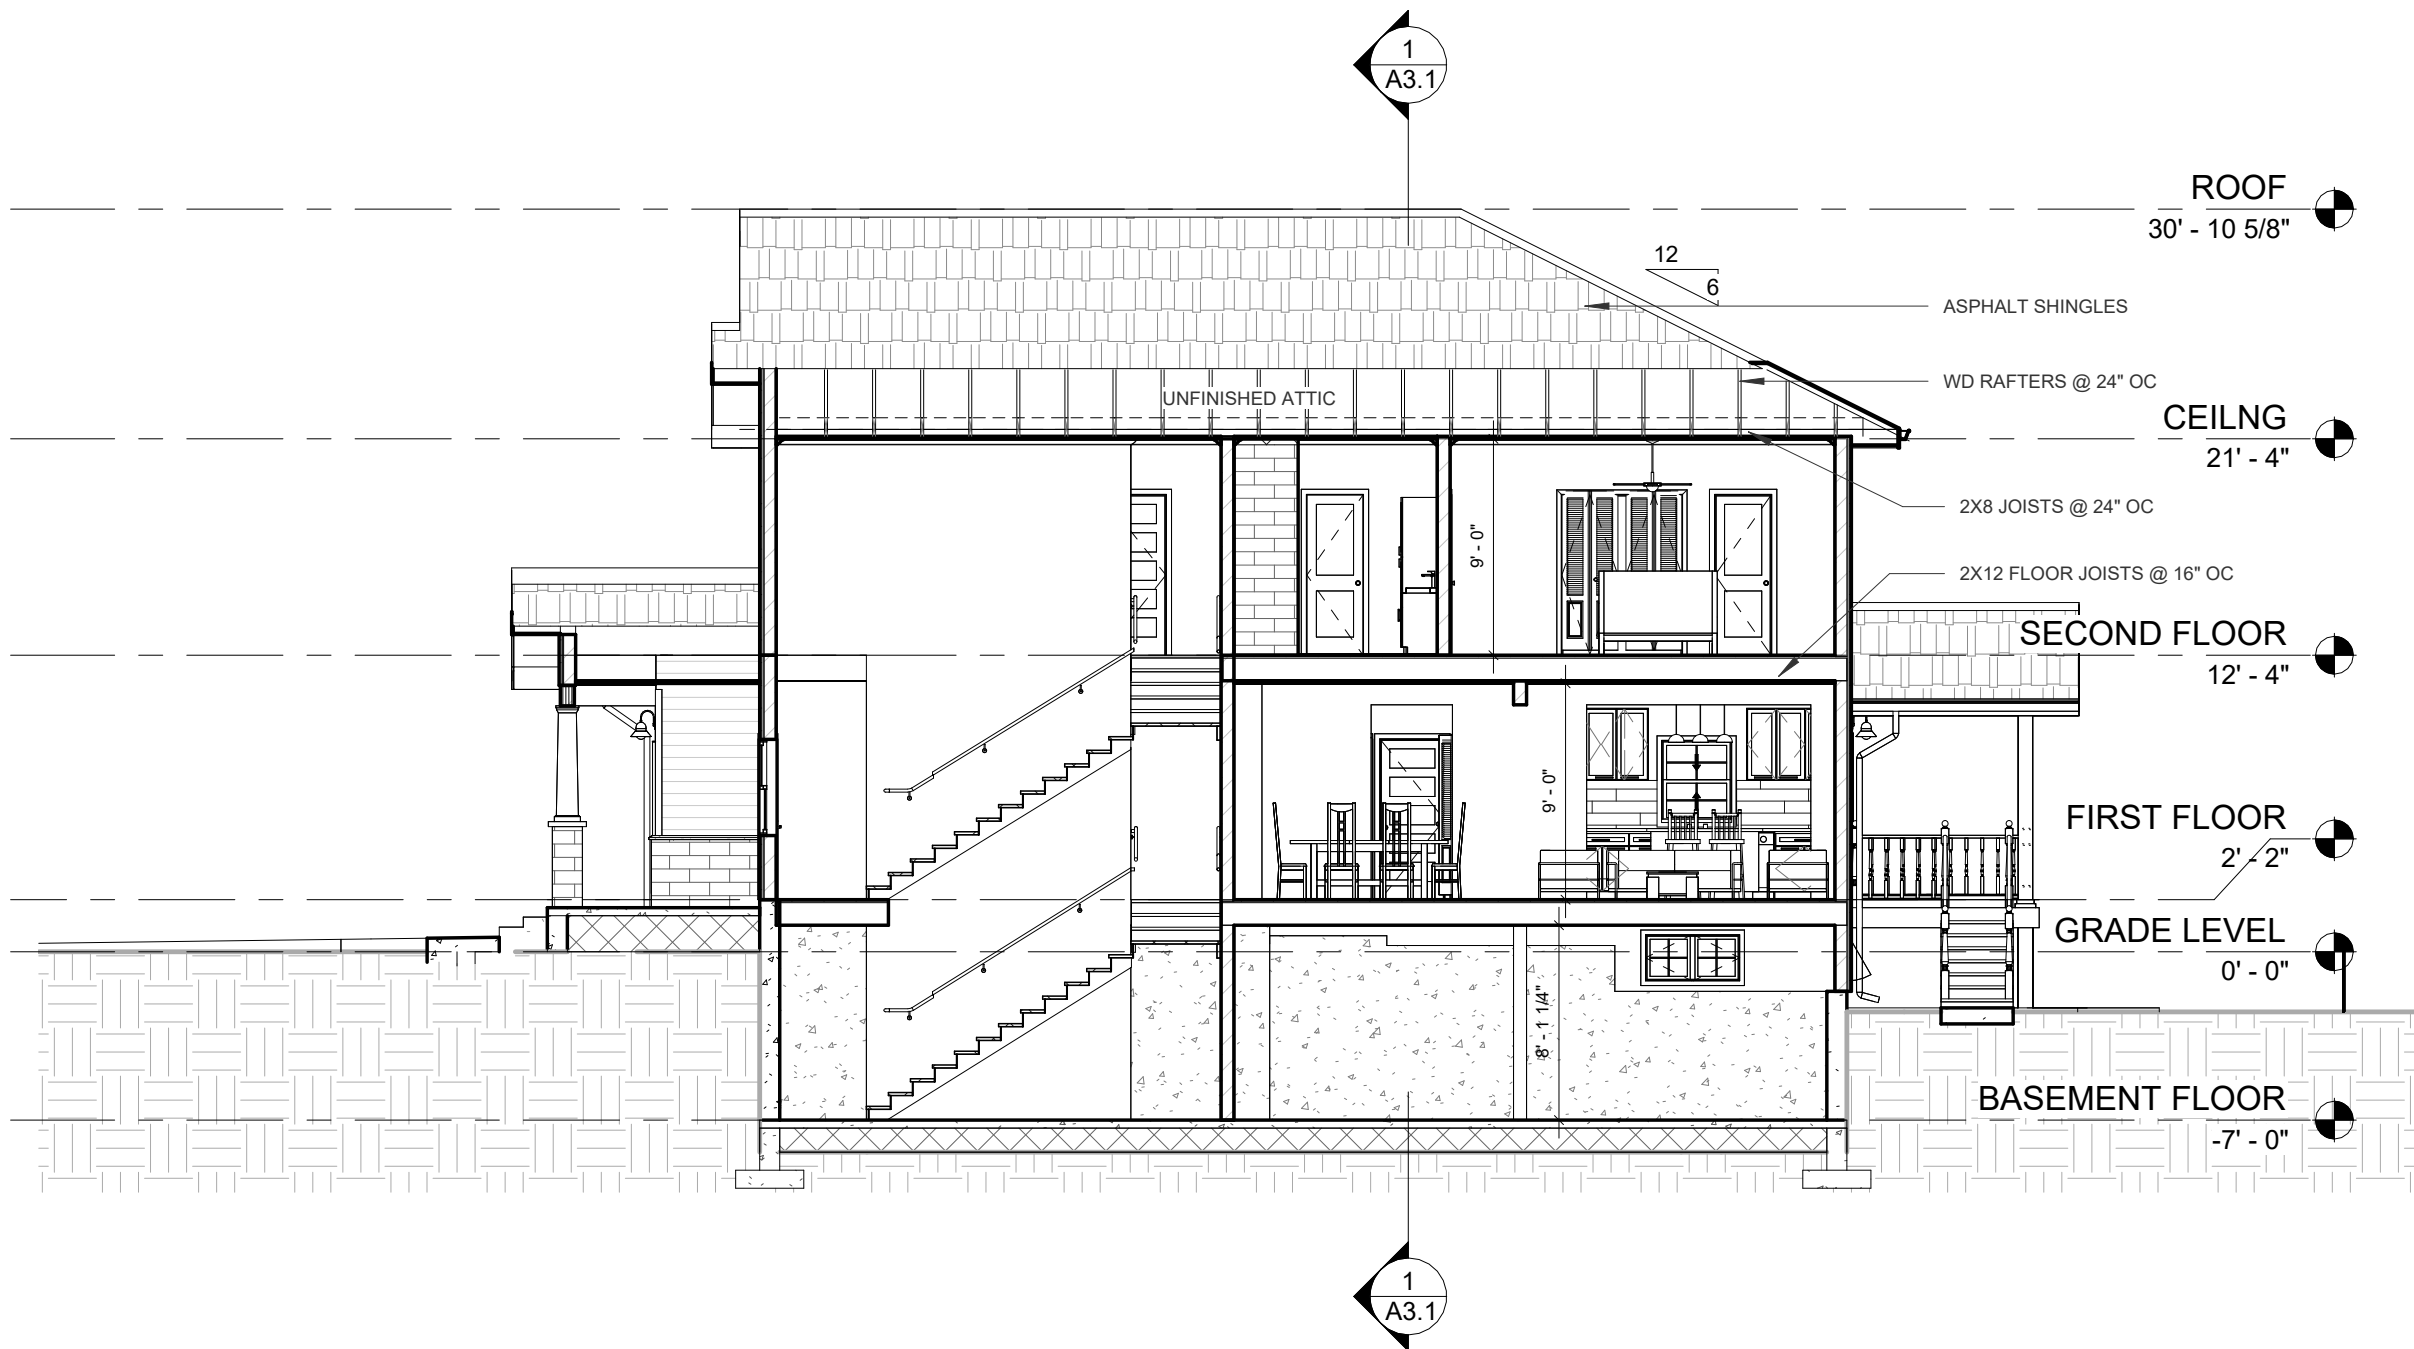

NOTES:

B	Y REVISED	JS	
A	X REVISED	JS	
REV	DESCRIPTION	BY	DATE

AMENDMENTS

ARCHITECT'S CONTACT DETAILS

NAME: VICTOR OMEH.
EMAIL: omehvictor@gmail.com
WEBSITE: www.victoromeh.github.io

PROJECT TITLE

SINGLE FAMILY HOME

SITE


509 BROOKHAVEN LANE,
WESTFIELD, IN 46074

CLIENT

MICHAEL & SARAH WHITFIELD

SCALE	DATE.	DRAWN BY.
1/8" = 1'-0"	JAN 2026	VICTOR OMEH

SHEET NAME. LONGITUDINAL SECTION		SHEET NO. A3.0
PROJECT NO.	VO-2026-101	

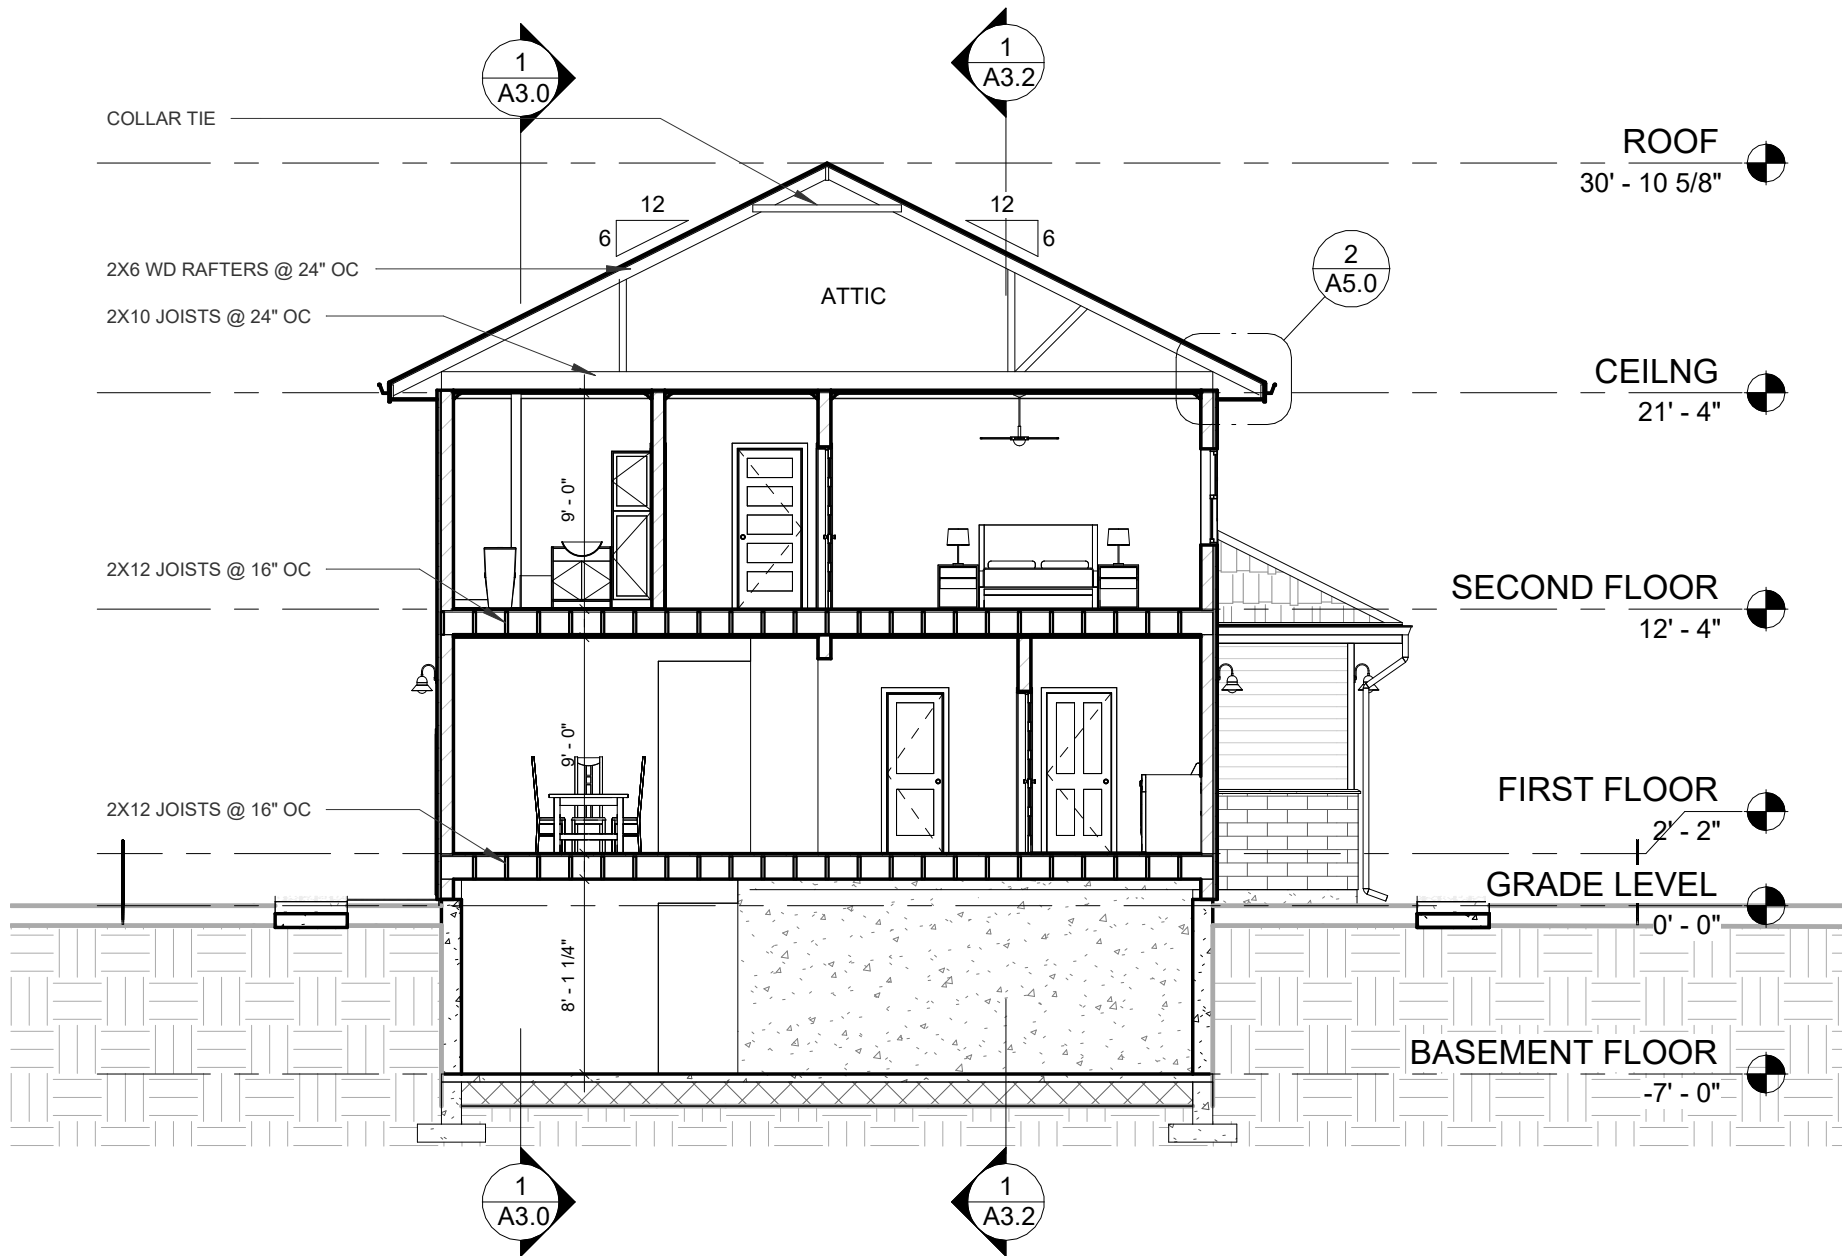

1 SECTION 2
1/8" = 1'-0"

NOTES:

B	Y REVISED	JS	
A	X REVISED	JS	
REV	DESCRIPTION	BY	DATE

AMENDMENTS

ARCHITECT'S CONTACT DETAILS

NAME: VICTOR OMEH.

EMAIL: omehvictor@gmail.com

WEBSITE: www.victoromeh.github.io

PROJECT TITLE

SINGLE FAMILY HOME

SITE

509 BROOKHAVEN LANE,
WESTFIELD, IN 46074

CLIENT

MICHAEL & SARAH WHITFIELD

SCALE	DATE.	DRAWN BY.
1/8" = 1'-0"	JAN 2026	VICTOR OMEH

SHEET NAME. TRANSVERSE
SECTION

PROJECT NO. VO-2026-101

SHEET NO.

A3.1



NOTES:

B	Y REVISED	JS	
A	X REVISED	JS	
REV	DESCRIPTION	BY	DATE

AMENDMENTS

ARCHITECT'S CONTACT DETAILS

NAME: VICTOR OMEH.
EMAIL: omehvictor@gmail.com
WEBSITE: www.victoromeh.github.io

PROJECT TITLE

SINGLE FAMILY HOME

SITE

509 BROOKHAVEN LANE,
WESTFIELD, IN 46074

CLIENT

MICHAEL & SARAH WHITFIELD

SCALE 1/8" = 1'-0"	DATE JAN 2026	DRAWN BY. VICTOR OMEH
--------------------------	------------------	-----------------------------

SHEET NAME. LONGITUDINAL SECTION 2	SHEET NO. A3.2
PROJECT NO. VO-2026-101	

SECTION 3 1/8" = 1'-0"

2

KITCHEN ELEVATION 2
1/2" = 1'-0"



- KEYNOTES
SEE SCHEDULE ON 5.0
- X-00 REFRIFGERATOR
 - X-02 KITCHEN SINK
 - X-04 RANGE/ OVEN
 - X-06 MICROWAVE/ HOOD
 - X-08 COUNTERTOP
 - X-10 WALL CABINET
 - X-12 FLOOR CABINET
 - X-14 TALL CABINET
 - X-16 DISHWASHER

NOTES:

B	Y REVISED	JS	
A	X REVISED	JS	
REV	DESCRIPTION	BY	DATE

AMENDMENTS

ARCHITECT'S CONTACT DETAILS

NAME: VICTOR OMEH.
EMAIL: omehvictor@gmail.com
WEBSITE: www.victoromeh.github.io

PROJECT TITLE

SINGLE FAMILY HOME

SITE

509 BROOKHAVEN LANE,
WESTFIELD, IN 46074

CLIENT


MICHAEL & SARAH WHITFIELD


SCALE 1/2" = 1'-0"	DATE JAN 2026	DRAWN BY. VICTOR OMEH
-----------------------	------------------	--------------------------

SHEET NAME. KITCHEN ELEVATIONS	SHEET NO. A4.1
PROJECT NO. VO-2026-101	


1

KITCHEN ELEVATION 1
1/2" = 1'-0"

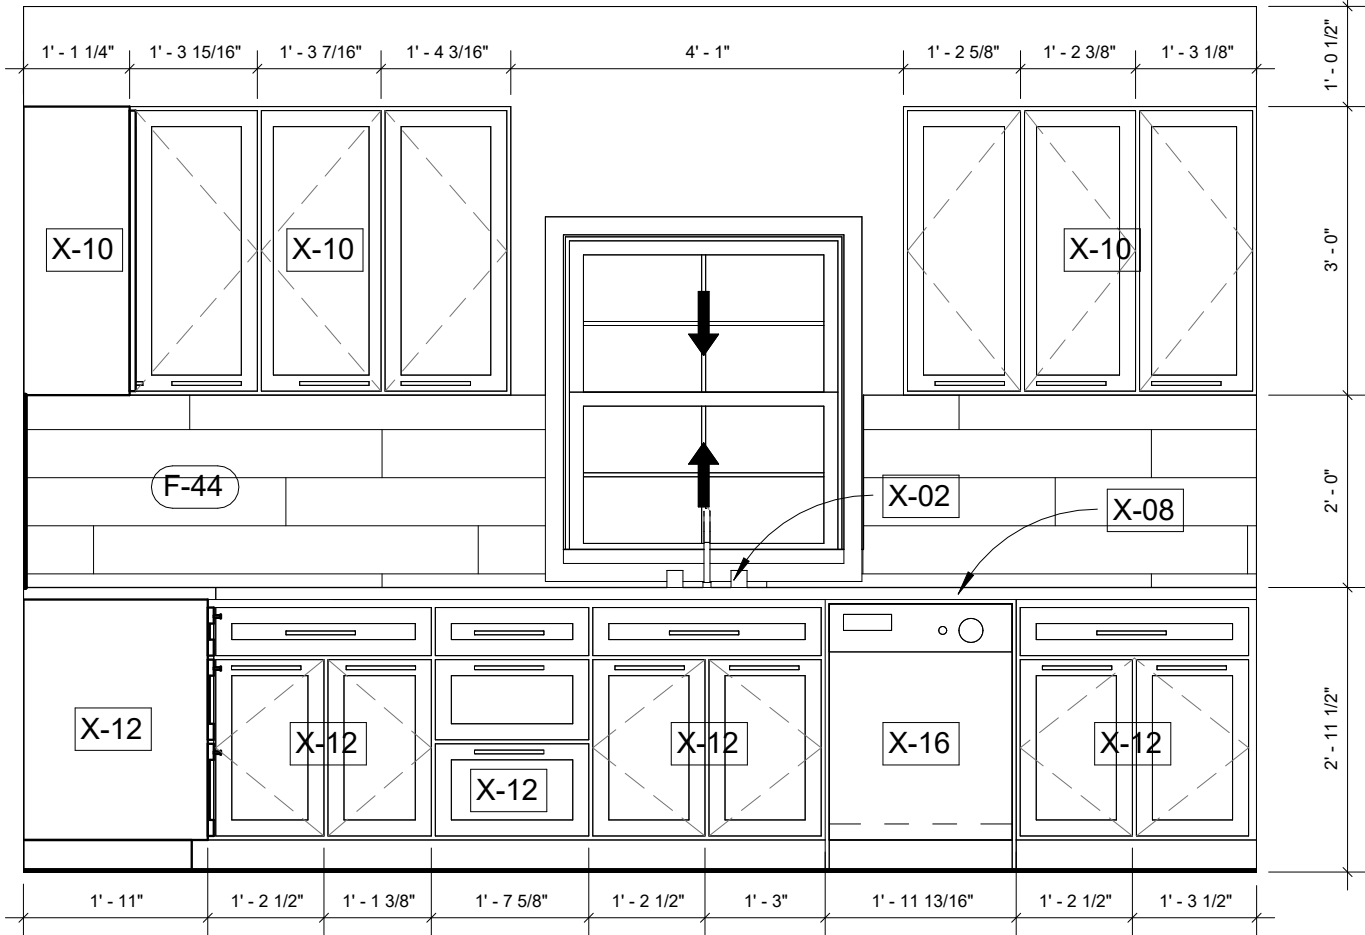


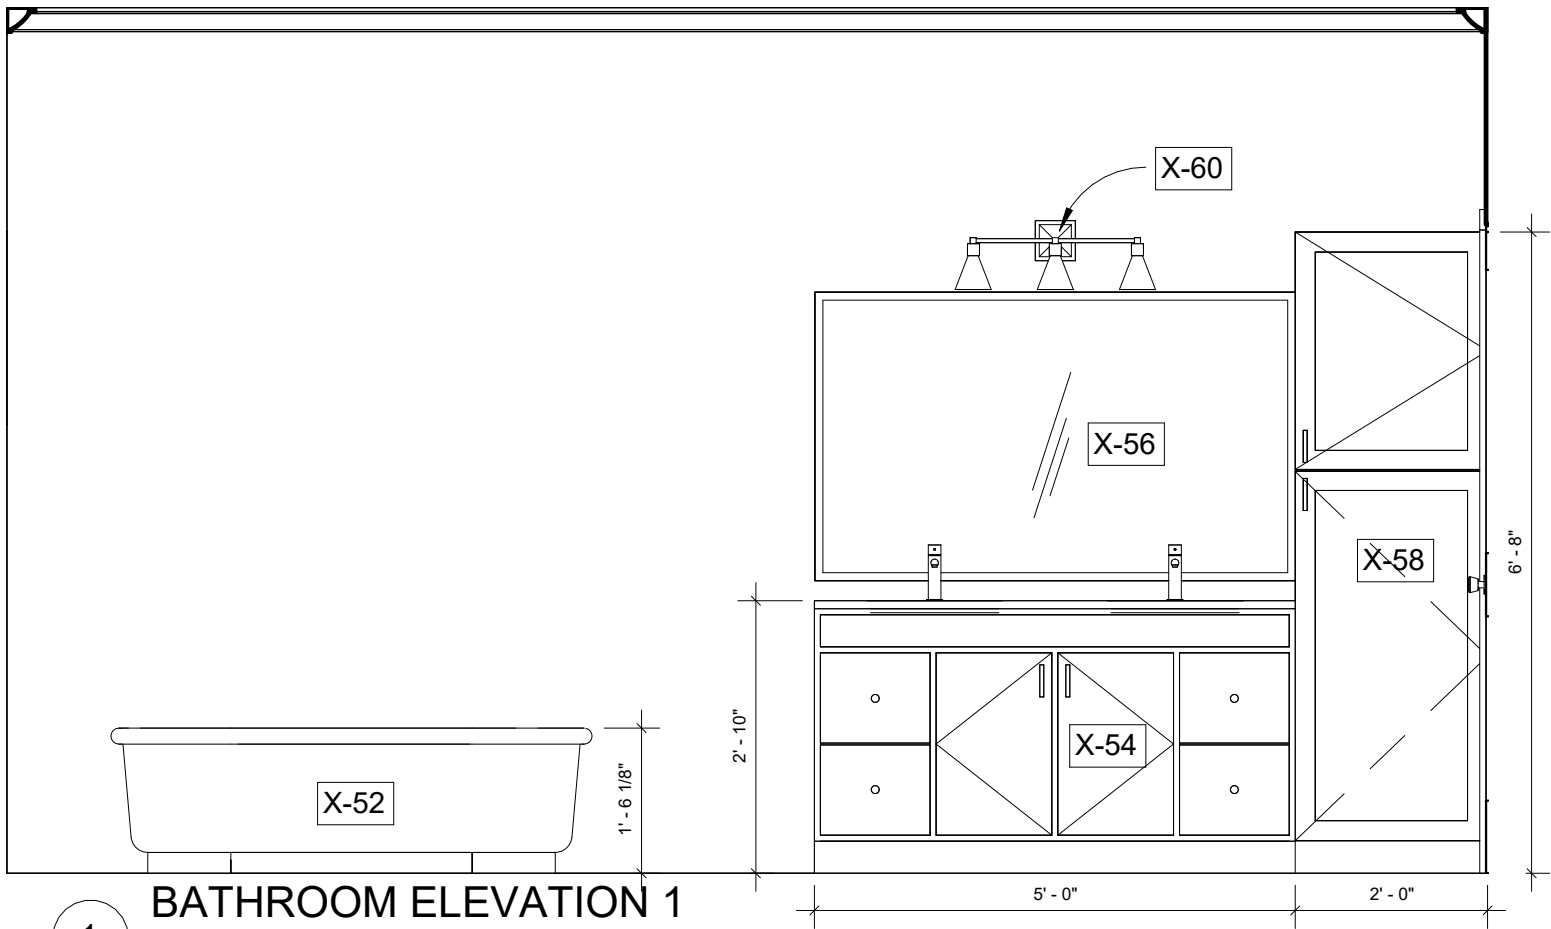


1 BATHROOM ELEVATION 1
1/2" = 1'-0"

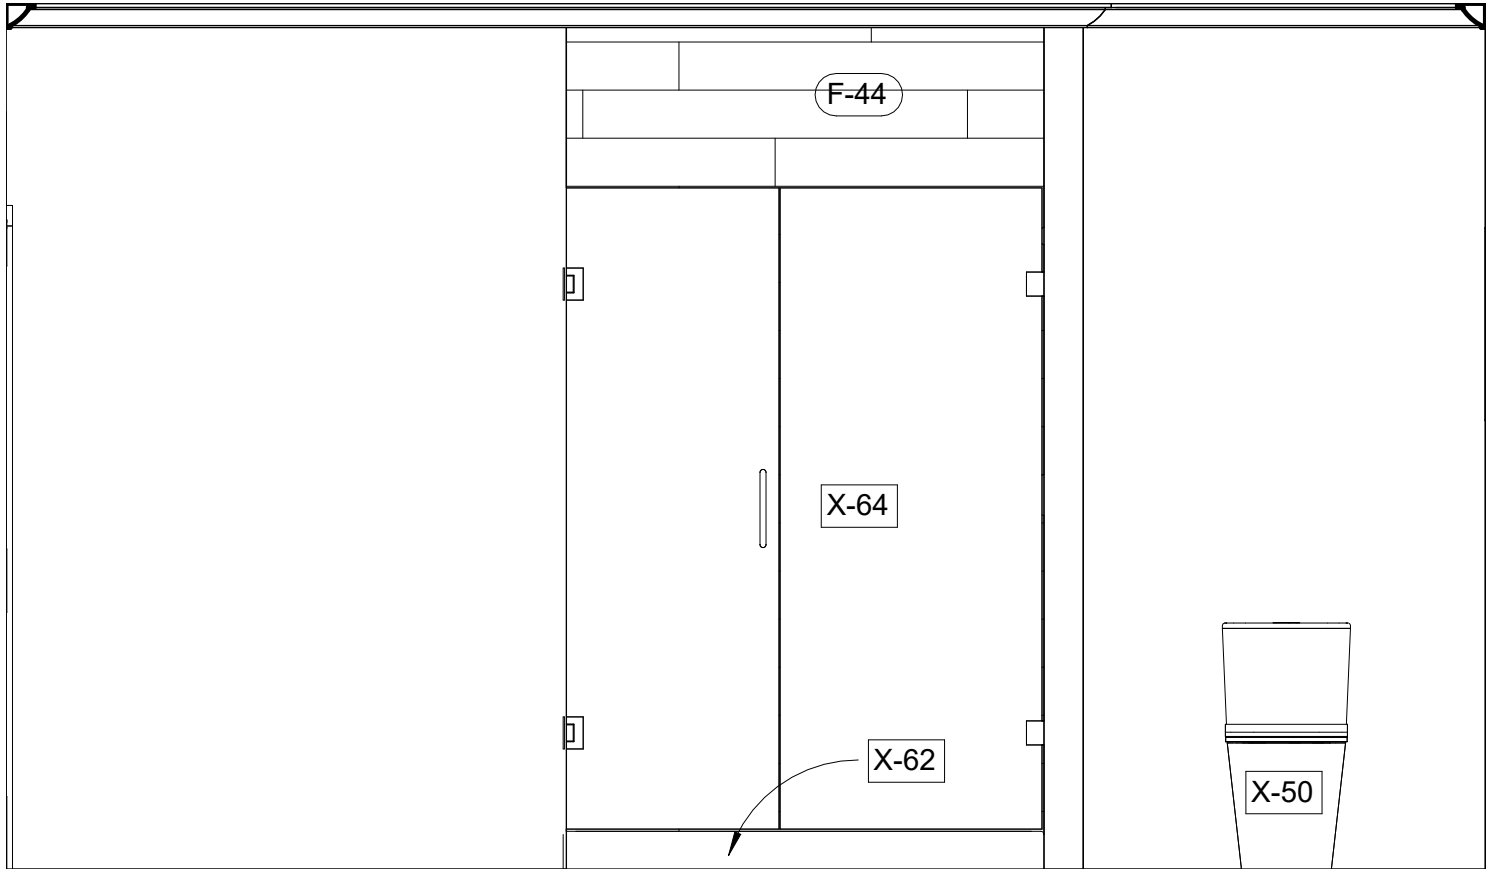

3 BATHROOM ELEVATION 3
1/2" = 1'-0"

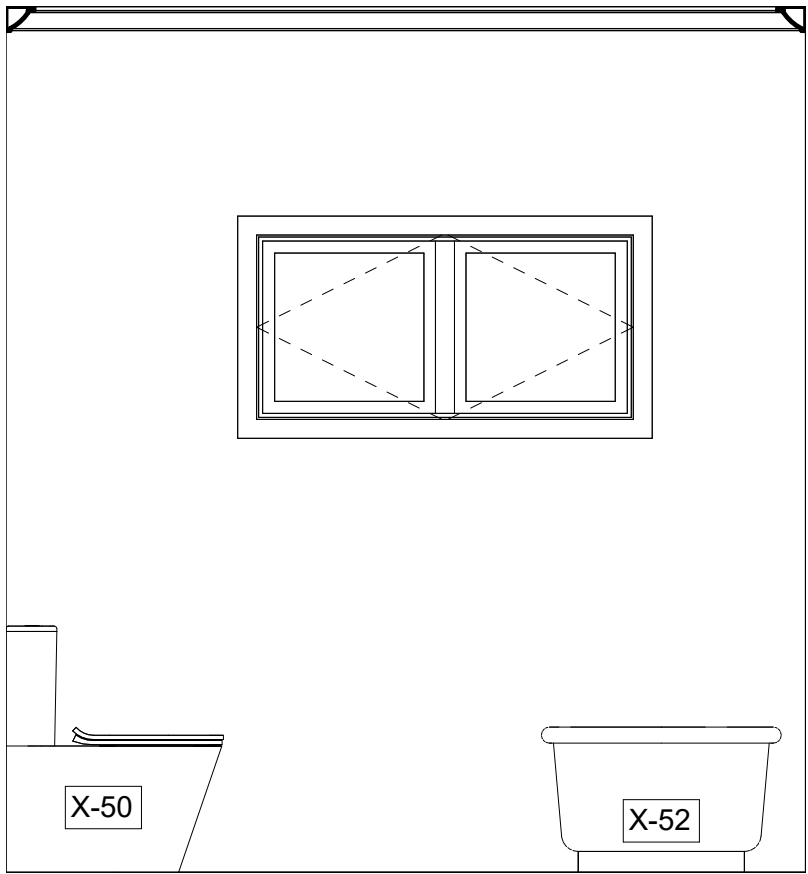

2 BATHROOM ELEVATION 2
1/2" = 1'-0"

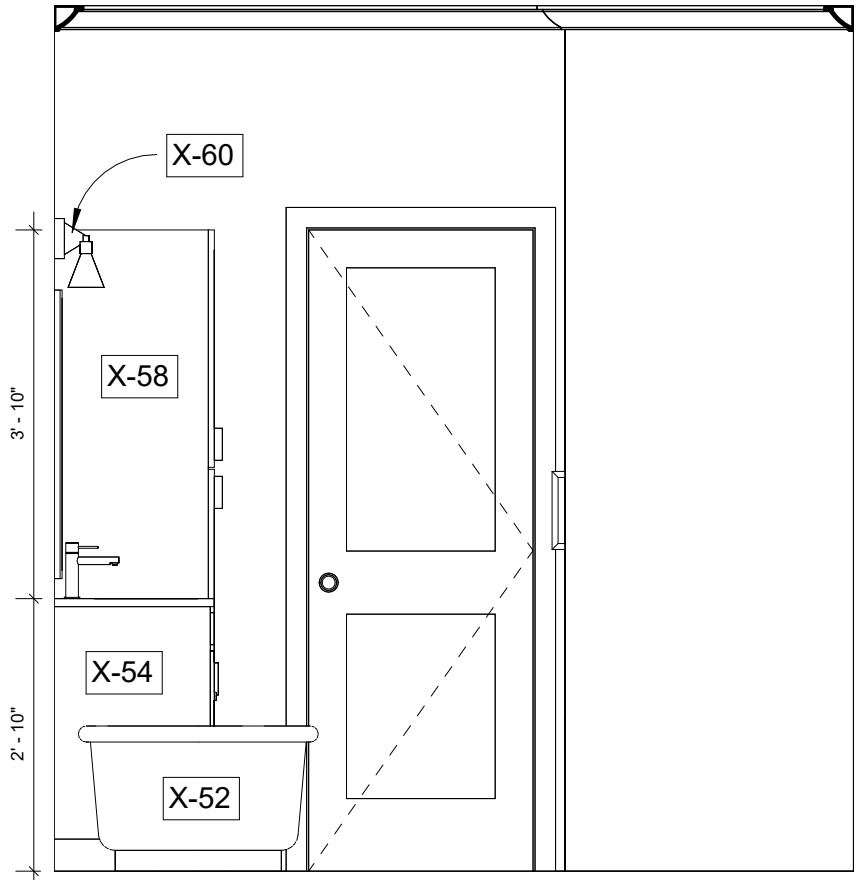

4 BATHROOM ELEVATION 4
1/2" = 1'-0"

NOTES:

B	Y REVISED	JS	
A	X REVISED	JS	
REV	DESCRIPTION	BY	DATE

AMENDMENTS

ARCHITECT'S CONTACT DETAILS

NAME: VICTOR OMEH.

EMAIL: omehvictor@gmail.com

WEBSITE: www.victoromeh.github.io

PROJECT TITLE

SINGLE FAMILY HOME

SITE


509 BROOKHAVEN LANE,
WESTFIELD, IN 46074

CLIENT


MICHAEL & SARAH WHITFIELD

SCALE	DATE	DRAWN BY.
1/2" = 1'-0"	JAN 2026	VICTOR OMEH


SHEET NAME. BATHROOM ELEVATION	SHEET NO.
PROJECT NO. VO-2026-101	A4.2

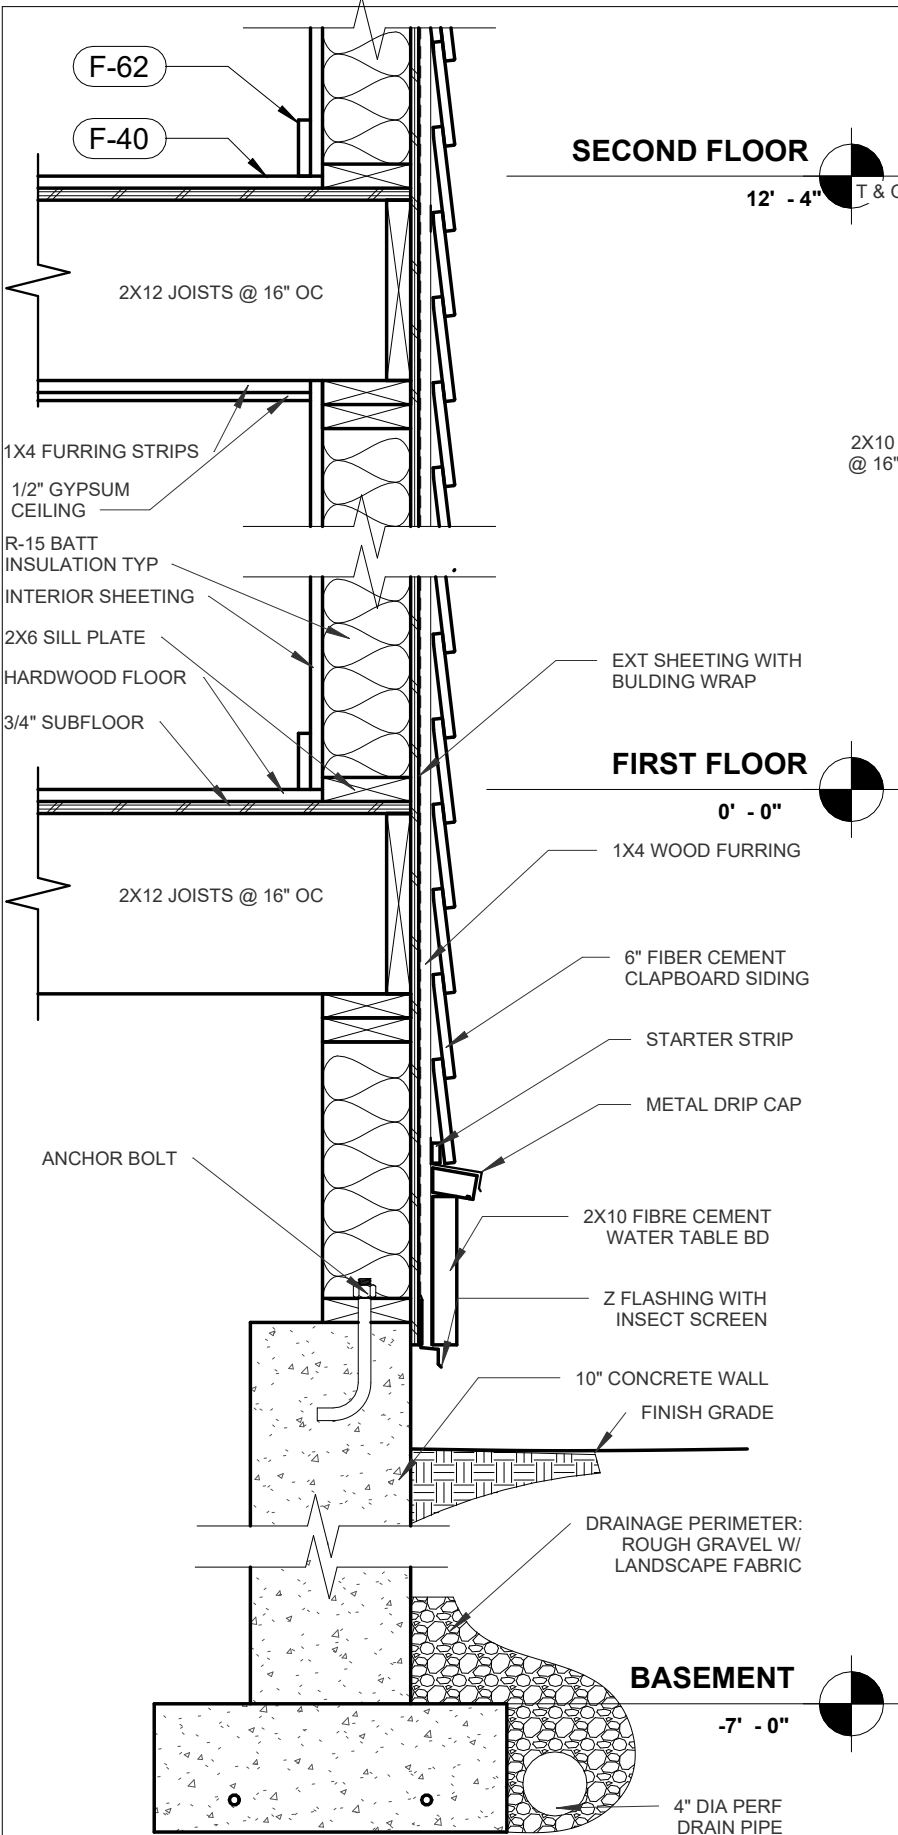


1 WALL SECTION DETAILS
1" = 1'-0"

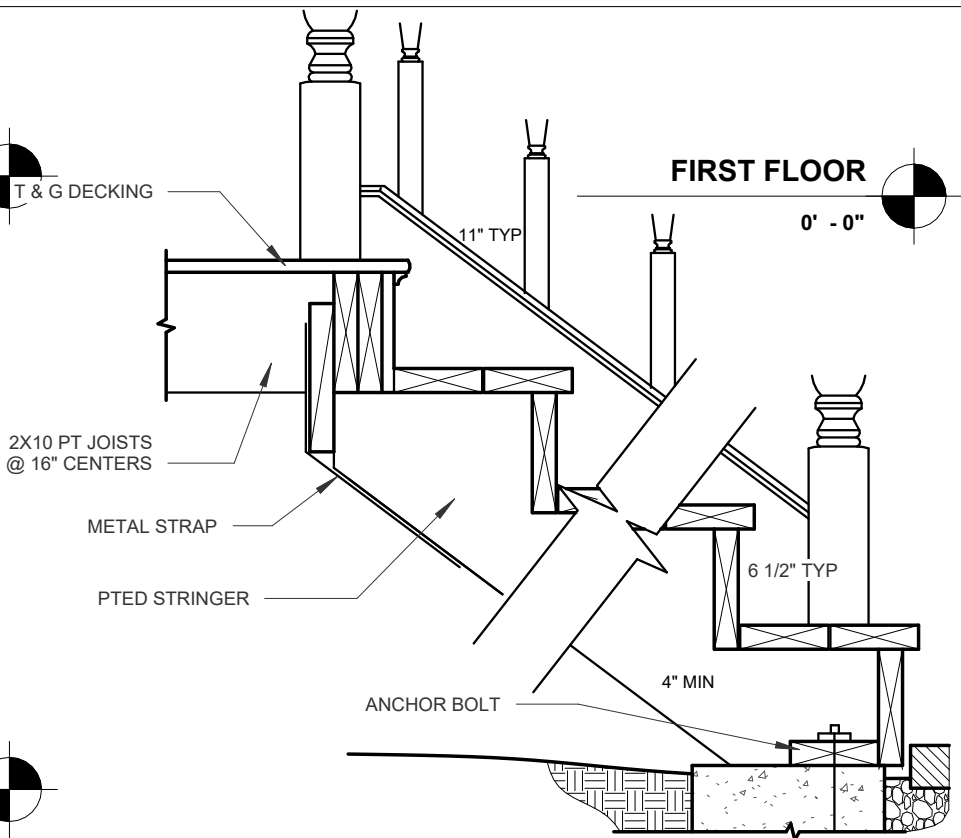

3 DECK STAIRS DETAILS
1" = 1'-0"

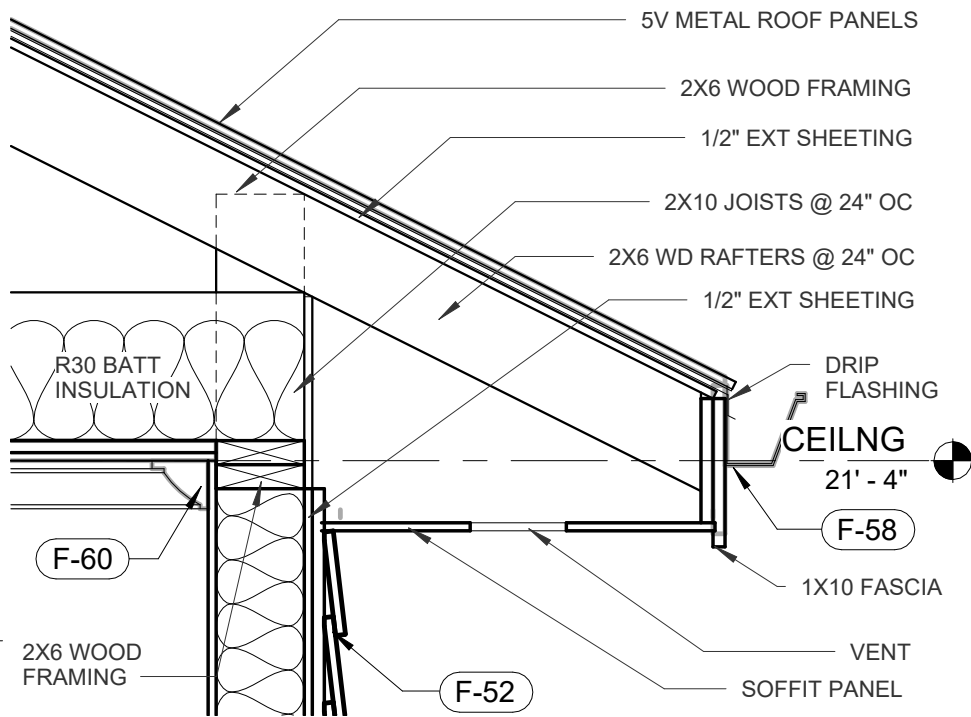

2 ROOF EAVE DETAIL
1" = 1'-0"

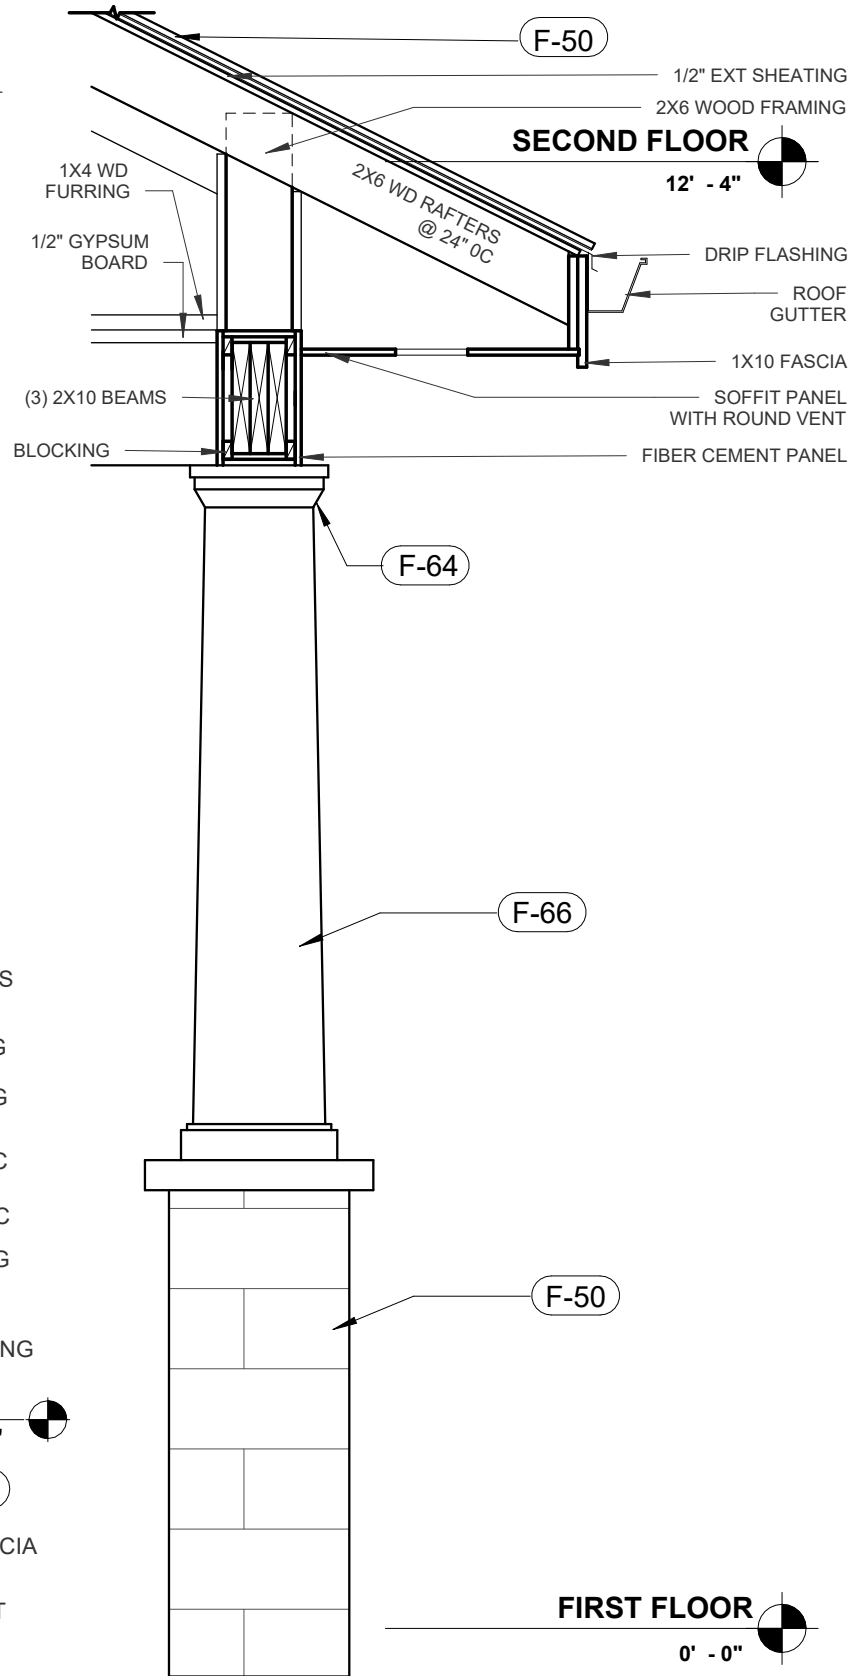

4 FRONT PORCH COLUMN
3/4" = 1'-0"

NOTES:

B	Y REVISED	JS	
A	X REVISED	JS	
REV	DESCRIPTION	BY	DATE

AMENDMENTS

ARCHITECT'S CONTACT DETAILS

NAME: VICTOR OMEH.
EMAIL: omehvictor@gmail.com
WEBSITE: www.victoromeh.github.io

PROJECT TITLE

SINGLE FAMILY HOME

SITE

509 BROOKHAVEN LANE,
WESTFIELD, IN 46074

CLIENT


MICHAEL & SARAH WHITFIELD

SCALE	DATE	DRAWN BY.
As indicated	JAN 2026	VICTOR OMEH

SHEET NAME. TYPICAL DETAILS SHEET NO.


PROJECT NO. VO-2026-101

A5.0

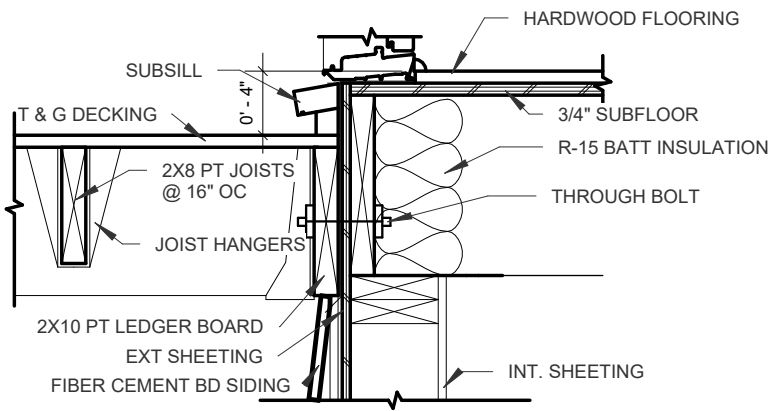


BACKYARD DECK DETAILS

1" = 1'-0"

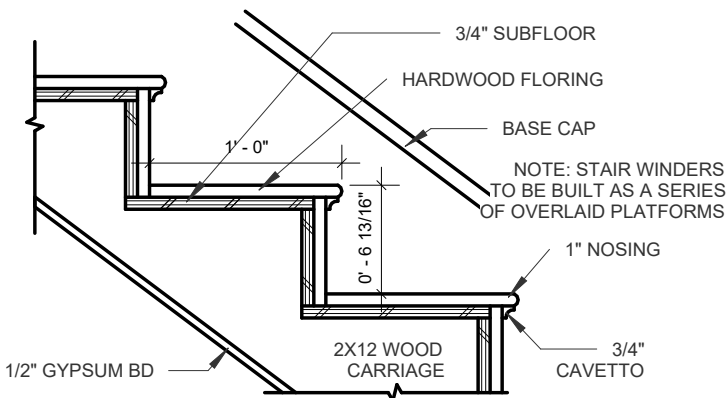


STAIR SECTION DETAILS

1" = 1'-0"

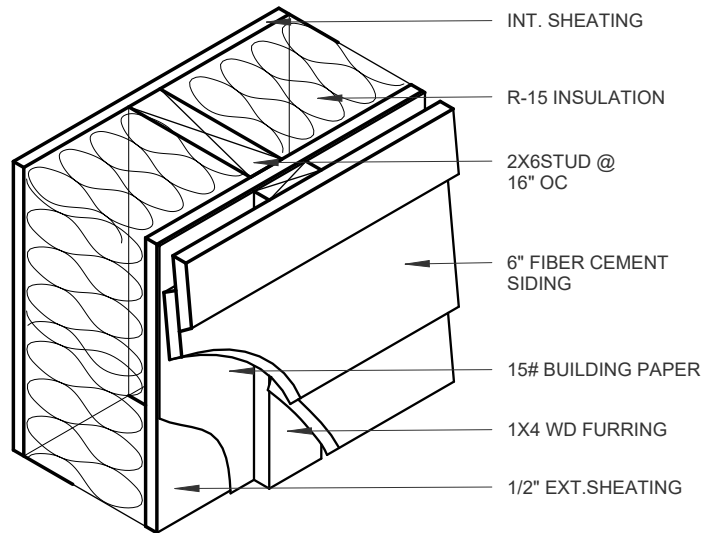


TYP EXT WALL

1 1/2" = 1'-0"

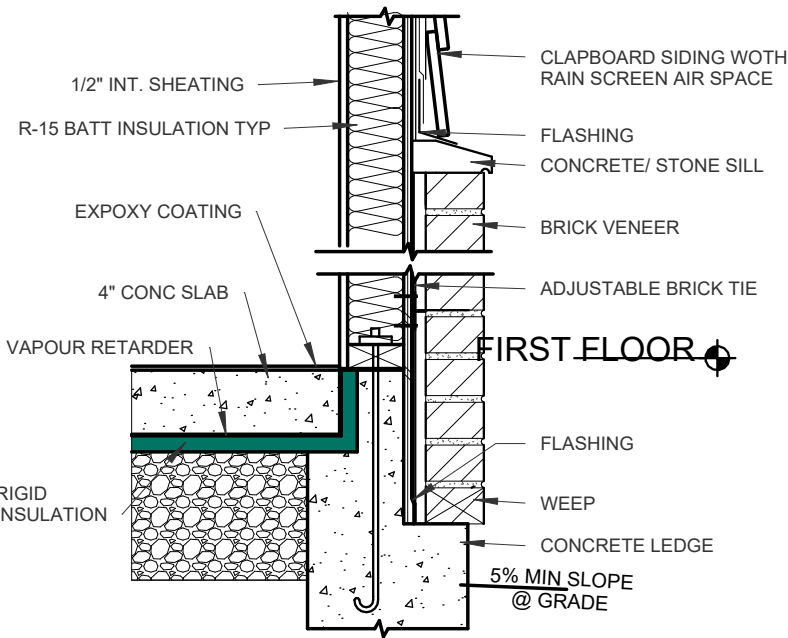

WALL DETAIL @ GARAGE

1" = 1'-0"

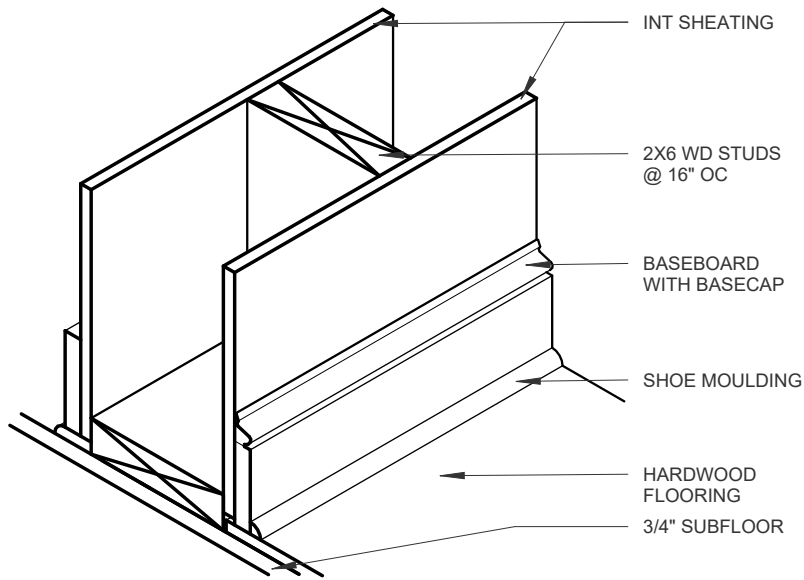

TYP INT WALL

1 1/2" = 1'-0"

NOTES:

B	Y REVISED	JS	
A	X REVISED	JS	
REV	DESCRIPTION	BY	DATE

AMENDMENTS

ARCHITECT'S CONTACT DETAILS

NAME: VICTOR OMEH.

EMAIL: omehvictor@gmail.com

WEBSITE: www.victoromeh.github.io

PROJECT TITLE

SINGLE FAMILY HOME

SITE


509 BROOKHAVEN LANE,
WESTFIELD, IN 46074

CLIENT

MICHAEL & SARAH WHITFIELD


SCALE	DATE.	DRAWN BY.
As indicated	JAN 2026	VICTOR OMEH

SHEET NAME. TYPICAL DETAIL	SHEET NO.
2	A5.1
PROJECT NO. VO-2026-101	

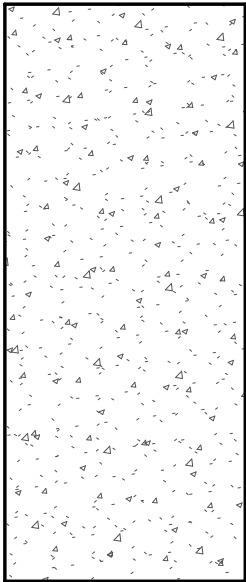


FOUNDATION WALL
10" THICK Mpa POURED
CONC. FOUNDATION WALL
MIX WITH 6% AIR
ENTRAINMENT
NOTE: FILL & SEAL ALL
THE AIR HOLES

W1

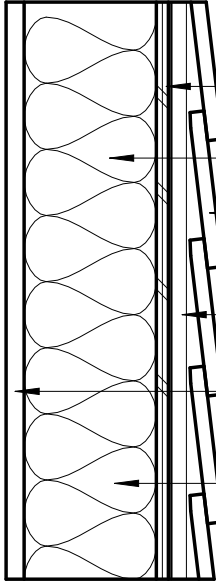


EXT SHEATING
R15 INSULATION
6" FIBER CEMENT
SIDING
1X4 WD FURRING
INTERIOR SHEATING
2X6 STUDS @ 16" OC

W2

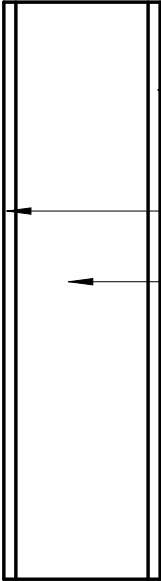


INTERIOR SHEATING
INTERIOR SHEATING
2X6 STUDS @ 16" OC

W3

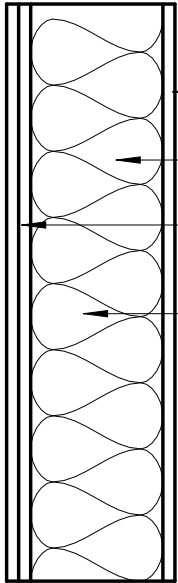


INTERIOR SHEATING
R31 INSULATION
FIRE RATED
INTERIOR SHEATING (X2)
2X6 STUDS @ 16" OC

W4

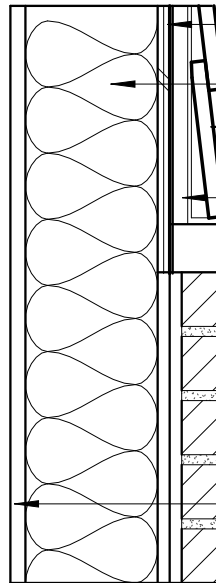


EXT SHEATING
R15 INSULATION
6" FIBER CEMENT
SIDING
1X4 WD FURRING
FLASHING
CONCRETE/ STONE
SILL
BRICK VENEER
INTERIOE SHEATING

W5

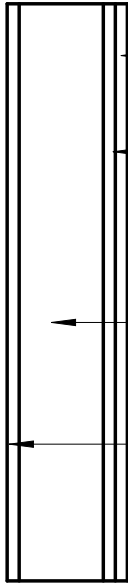


CERAMIC/ PORCELAIN
WALL TILES
MOISTURE RESISTANT
FIBRE CEMENT BACKER
BOARD
2X4 STUDS @ 16" OC
INTERIOR SHEATING

W6

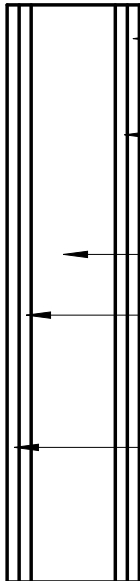


CERAMIC/ PORCELAIN
WALL TILES
MOISTURE RESISTANT
FIBRE CEMENT BACKER
BOARD
2X4 STUDS @ 16" OC
MOISTURE RESISTANT
FIBRE CEMENT BACKER
BOARD
CERAMIC/ PORCELAIN
WALL TILES

W7

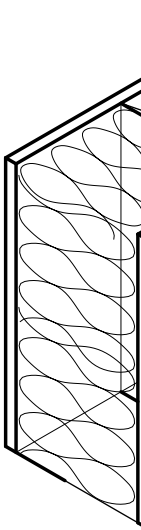

INT. SHEATING
R-15 INSULATION
2X6STUD @
16" OC
6" FIBER CEMENT
SIDING
15# BUILDING PAPER
1X4 WD FURRING
1/2" EXT.SHEATING

W2

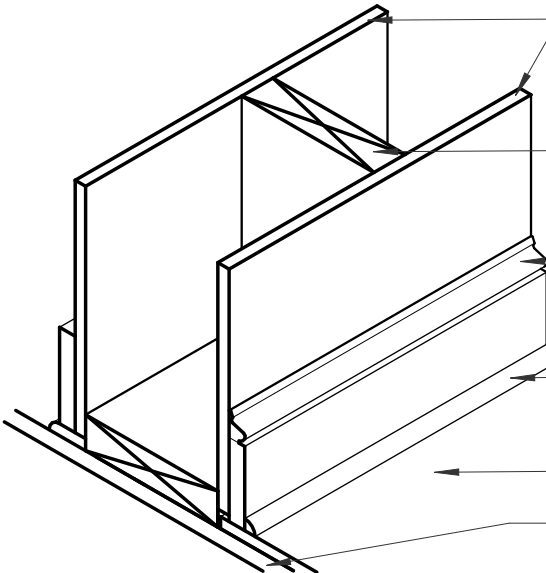

INT SHEATING
2X6 WD STUDS
@ 16" OC
BASEBOARD
WITH BASECAP
SHOE MOULDING
HARDWOOD
FLOORING
3/4" SUBFLOOR

W3

NOTES:

B	Y REVISED	JS	
A	X REVISED	JS	
REV	DESCRIPTION	BY	DATE

AMENDMENTS

ARCHITECT'S CONTACT DETAILS

NAME: VICTOR OMEH.
EMAIL: omehvictor@gmail.com
WEBSITE: www.victoromeh.github.io

PROJECT TITLE

SINGLE FAMILY HOME

SITE

509 BROOKHAVEN LANE,
WESTFIELD, IN 46074

CLIENT

MICHAEL & SARAH WHITFIELD











SCALE	DATE.	DRAWN BY.
1 1/2" = 1'-0"	JAN 2026	VICTOR OMEH

SHEET NAME. WALL DETAILS

PROJECT NO. VO-2026-101










SHEET NO.

A5.2

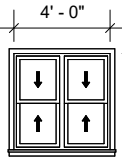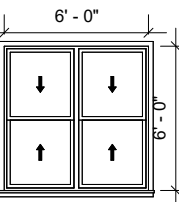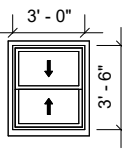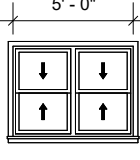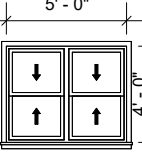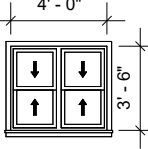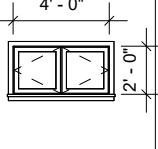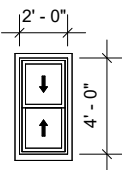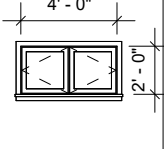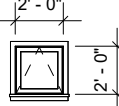PLAN VIEW										
ELEVATION VIEW										
WINDOW TAG.	W1	W2	W3	W4	W5	W6	W7	W8	W9	W10

WINDOW LEGEND

1/8" = 1'-0"

 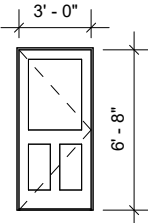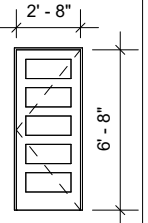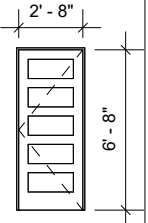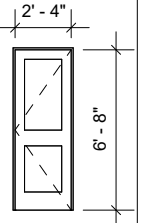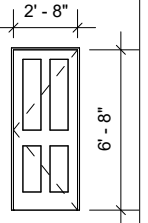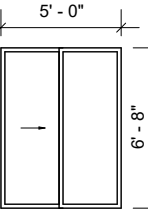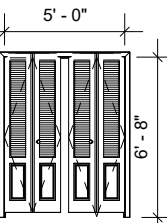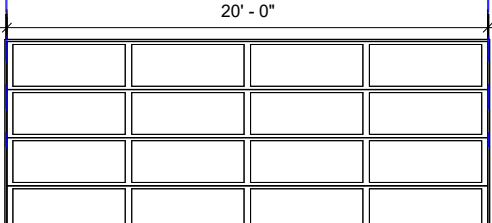PLAN VIEW								
ELEVATION VIEW								
DOOR TAG	D1	D2	D3	D4	D5	D6	D7	D8

DOOR LEGEND

1/8" = 1'-0"

DOOR SCHEDULE								
MAR K	SIZE	ROUGH OPENING	QT Y	LOCATION	MATERIAL	OPERATIO N	FIRE RATING	COMMENTS
D1	3' - 0" X 6' -8"	38" X 82 1/2"	1	ENT.PORCH	FIBERGLASS	SWING	-	EXTERIOR INSULATED WITH GLASS SIDELITES
D2	2' - 8" X 6' -8"	38" X 82 1/2"	1	SIDE EXIT(BY STAIRS)	FIBERGLASS	SWING	-	EXTERIOR, INSULATED, EGRESS COMPLIANT
D3	2' - 8" X 6' -8"	34" X 82 1/2"	5	BEDROOMS	SOLID CORE WOOD OR MDF	SWING	-	PRIVACY LOCKS, STANDARD INTERIOR
D4	2' - 4" X 6' -8"	32" X 82 1/2"	4	PWDR ROOM / BATHROOM	SOLID CORE WOOD OR MDF	SWING	-	MOISTURE RESISTANT CORE
D5	2' - 8" X 6' -8"	38" X 82 1/2"	1	GARAGE TO LAUNDRY	STEEL (PRE-PRIMED)	SWING	20-MINUTE	FIRE-RATED SELF-CLOSING HARDWARE
D6	5' - 0" X 6' -8"	16' - 2" X 7' - 2"	1	KITCHEN TO BACKPORCH	VINYL OR ALUMINUM CLAD	SLIDING	-	ENERGY STAR TEMPRED GLASS, SCREEN OPTION
D7	5' - 0" X 6' -8"	62" X 82 1/2"	5	CLOSET	HOLLOW CORE WOOD	BI-FOLD	-	STANDARD CLOSET BIFOLD DOORS
D8	20' - 0" X 8' -0"	20' - 2" X 8' -2"	1	GARAGE	STEEL (INSULATED)	OVERHEAD	-	INSULATED, AUTOMATIC OPENER, WINDOWS OPTIONAL

NOTES:

B	Y REVISED	JS	
A	X REVISED	JS	
REV	DESCRIPTION	BY	DATE

AMENDMENTS

ARCHITECT'S CONTACT DETAILS

NAME: VICTOR OMEH.

EMAIL: omehvictor@gmail.com

WEBSITE: www.victoromeh.github.io

PROJECT TITLE

SINGLE FAMILY HOME

SITE

509 BROOKHAVEN LANE,
WESTFIELD, IN 46074

CLIENT

MICHAEL & SARAH WHITFIELD

SCALE	DATE.	DRAWN BY.
1/8" = 1'-0"	JAN 2026	VICTOR OMEH

SHEET NAME. DOORS & WINDOWS		SHEET NO. A6.0
PROJECT NO.	VO-2026-101	

WINDOW SCHEDULE									
W_MAR K	W_SIZE	W_ROUGH OPENING	W_SILL HEIGHT	W_QTY	W_LOCATION	W_MATERIAL	W_OPERATION	W_EGRES S	W_COMMENTS
W1	4' - 0" X 4' - 0"	50" X 50"	2' 8"	4	ENT PORCH, LIVING BEDROOM, MASTER	COMPOSITE/ VINYL	DOUBLE HUNG	Yes	EXTERIOR LOW-E GLASS
W2	6' - 0" X 6' - 0"	74" X 74.5"	1' 8"	1	GREAT ROOM	COMPOSITE/ VINYL	DOUBLE HUNG	No	LARGE PICTURE STYLE VIEW
W3	3' - 0" X 3' - 6"	38" X 44.5"	3' 2"	1	KITCHEN	COMPOSITE/ VINYL	DOUBLE HUNG	No	ABOVE SINK
W4	5' - 0" X 3' - 9"	62" X 47.5"	3' 11"	1	BEDROOM	COMPOSITE/ VINYL	DOUBLE HUNG	Yes	-
W5	5' - 0" X 4' - 0"	62" X 50.5"	3' 8"	1	BEDROOM	COMPOSITE/ VINYL	DOUBLE HUNG	Yes	-
W6	4' - 0" X 3' - 6"	50" X 44.5"	3' 8"	1	BEDROOM	COMPOSITE/ VINYL	DOUBLE HUNG	Yes	-
W7	4' - 0" X 2' - 0"	50" X 26.5"	5' 9"	3	UNFINISHED BASEMENT	COMPOSITE/ VINYL	AWNING	No	-
W8	2' - 0" X 4' - 0"	26" X 50.5"	2' 8"	3	MASTER BEDROOM, STAIRS	COMPOSITE/ VINYL	DOUBLE HUNG	Yes	PRIVAVY / VENTILATION
W9	4' - 0" X 2' - 0"	50" X 26.5"	4' 8"	1	MASTER BATHROOM	COMPOSITE/ VINYL	AWNING	No	EGRESS WINDOWS (ONE PER BEDROOM)
W10	2' - 0" X 2' - 0"	26" X 26.5"	4' 8"	2	BATHROOM		AWNING	No	-

ROOM SCHEDULE							
Number	Name	Area	Floor Finish	Ceiling Finish	Ceiling Height	Wall Finish	Comments
1	GARAGE	571 SF	EPOXY/ POLYASPATIC	GYPSUM BOARD	10' - 6"	PAINTED CMU/ GYPSUM	UNHEATED
2	LAUNDRY	74 SF	PORCELAIN/ CERAMIC TILE	GYPSUM BOARD	9' - 0"	GYPSUM BOARD, PAINT	WATERPROOF MEMBRANE
3	PWDR ROOM	31 SF	PORCELAIN/ CERAMIC TILE	GYPSUM BOARD	9' - 0"	MOISTURE RESISTANT GYP. BD. PAINT	WATERPROOF MEMBRANE
5	BACK PORCH	98 SF	COMPOSITE DECKING	FIBER CEMENT	9' - 4"	FIBER CEMENT SIDING PAINTED	UNHEATED
6	ENTRANCE PORCH	112 SF	COMPOSITE DECKING	FIBER CEMENT	9' - 4"	FIBER CEMENT SIDING PAINTED	UNHEATED
7	CLOSET	16 SF	ENGINEERED HARDWOOD	GYPSUM BOARD	9' - 0"	GYPSUM BOARD, PAINT	UNHEATED
8	KITCHEN	202 SF	ENGINEERED HARDWOOD	GYPSUM BOARD	9' - 0"	GYPSUM BOARD, PAINT	UNHEATED
9	GREAT ROOM	201 SF	ENGINEERED HARDWOOD	GYPSUM BOARD	9' - 0"	GYPSUM BOARD, PAINT	UNHEATED
10	LIVING/ DINNING	201 SF	ENGINEERED HARDWOOD	GYPSUM BOARD	9' - 0"	GYPSUM BOARD, PAINT	UNHEATED
11	FOYER	223 SF	ENGINEERED HARDWOOD	GYPSUM BOARD	9' - 0"	GYPSUM BOARD, PAINT	UNHEATED
12	MASTER BEDROOM	243 SF	ENGINEERED HARDWOOD	GYPSUM BOARD	9' - 0"	GYPSUM BOARD, PAINT	UNHEATED
13	BATHROOM	69 SF	PORCELAIN/ CERAMIC TILE	GYPSUM BOARD	9' - 0"	MOISTURE RESISTANT GYP. BD. PAINT	WATERPROOF MEMBRANE
15	BATHROOM	109 SF	PORCELAIN/ CERAMIC TILE	GYPSUM BOARD	9' - 0"	MOISTURE RESISTANT GYP. BD. PAINT	WATERPROOF MEMBRANE
16	BATHROOM	52 SF	PORCELAIN/ CERAMIC TILE	GYPSUM BOARD	9' - 0"	MOISTURE RESISTANT GYP. BD. PAINT	WATERPROOF MEMBRANE
17	BEDROOM	185 SF	ENGINEERED HARDWOOD	GYPSUM BOARD	9' - 0"	GYPSUM BOARD, PAINT	UNHEATED
18	BEDROOM	185 SF	ENGINEERED HARDWOOD	GYPSUM BOARD	9' - 0"	GYPSUM BOARD, PAINT	UNHEATED
19	BEDROOM	134 SF	ENGINEERED HARDWOOD	GYPSUM BOARD	9' - 0"	GYPSUM BOARD, PAINT	UNHEATED
20	CLOSET	21 SF	ENGINEERED HARDWOOD	GYPSUM BOARD	9' - 0"	GYPSUM BOARD, PAINT	UNHEATED
21	CLOSET	21 SF	ENGINEERED HARDWOOD	GYPSUM BOARD	9' - 0"	GYPSUM BOARD, PAINT	UNHEATED
22	LOBBY	180 SF	ENGINEERED HARDWOOD	GYPSUM BOARD	9' - 0"	GYPSUM BOARD, PAINT	UNHEATED
23	CLOSET	31 SF	ENGINEERED HARDWOOD	GYPSUM BOARD	9' - 0"	GYPSUM BOARD, PAINT	UNHEATED
24	CLOSET	11 SF	ENGINEERED HARDWOOD	GYPSUM BOARD	9' - 0"	GYPSUM BOARD, PAINT	UNHEATED
25	UNFINISHED BASEMENT	927 SF	CONCRETE SLAB	UNFINISHED	VARIES	CONCRETE / FRAMING	FUTURE FINISH OPTIONAL


NOTES:			
B	Y REVISED	JS	
A	X REVISED	JS	
REV	DESCRIPTION	BY	DATE
AMENDMENTS			
ARCHITECT'S CONTACT DETAILS			
NAME:		VICTOR OMEH.	
EMAIL:		omehvictor@gmail.com	
WEBSITE:		www.victoromeh.github.io	
PROJECT TITLE			
SINGLE FAMILY HOME			
SITE			
509 BROOKHAVEN LANE, WESTFIELD, IN 46074			
CLIENT			
MICHAEL & SARAH WHITFIELD			
SCALE	DATE. JAN 2026		DRAWN BY. VICTOR OMEH
SHEET NAME. SCHEDULES 1			SHEET NO. A6.1
PROJECT NO. VO-2026-101			

FIXTURE AND EQUIPMENT SCHEDULE				
X_MARK	X_ITEM	X_SIZE/ DESCRIPTION	X_NOTES/ SPECIFICATION	X_MAUFACTURER/MODEL
X-00	REFRIDGERATOR	36" WIDE X 70" TALL	ENERGY STAR CERTIFIED FRENCH DOOR OR SIDE BY SIDE LED LIGHTING WATER/ICE DISPENSER	BLOMBERG, GE OR EQUIVALENT
X-02	KITCHEN SINK	33"X22" SINGLE BOWL 9" DEEP	UNDERMOUNT STAINLESS STEEL NOISE DAMPEMING PADS INCLUDES STRAINER AND DISPOSAL	KOHLER OR EQUIVALENT
X-04	RANGE/ OVEN	30" FREESTANDING OR SLIDE-IN	STAINLESS STEEL, SELF-CLEANING CONVECTION OPTION	GE SAMSUNG OR EQUIVALENT
X-06	MICROWAVE/ HOOD COMBO	30" WIDE	OVER-THE-RANGE VENTED SENSOR COOKING	GE OR EQUIVALENT
X-08	COUNTERTOP	1 1/2" THICK, VARIOUS LENGHTS	QUARTZ SLAB, NON POROUS, EASED OR BEVELED EDGE, LIGHT COLOR	CEASARSTONE, CAMBRIA OR EQUIVALENT
X-10	WALL CABINETS	VARIOUS WIDTHS 36" HIGH	PAINTED FINISH SOFT-CLOSE HINGES GLAZED DOORS PREFERRED ON SELECT CABINETS	IKEA SEKTON OR SEMI-CUSTOM
X-12	FLOOR CABINET	24" DEEP, 36 INCH HIGH	SOFTCLOSE DRAWERS AND DOORS, QUARTZ COUNTERTOP	MATCHING CABINET LINE
X-14	TALL PANTRY/ CABINET	24"X 96" X 24" DEEP	ADJUSTABLE SHELIVING, PANTRY PULL-OUTS WHERE POSSIBLE	MATCHING CABINET LINE
X-16	DISHWASHER	STANDARD 24"	QUIET OPERATION (45DB) ENERGY STAR STAINLESS TUB	BOSCH OR KITCHEN AID
X-50	WATER CLOSET (TOILET)	ELONGATED BOWL, 12" ROUGH IN	1.28 GPF, COMFORT HEIGHT (17"-19"), QUIET CLOSE SEAT	KOHLER, AMERICAN STANDARD
X-52	BATHTUB	60"X30" OR 32" ALCOVE	ACRYLIC INTEGRAL APRON, TEXTURED BOTTOM	KOHLER
X-54	BATHROOM VANITY	60"X20"X34	QUARTZ COUNTERTOP, UNDERMOUNT RECTANGULAR SINK, SOFT CLOSE	LOCAL CABINET OR IKEA
X-56	MIRROR	SIZED TO VANITY	FRAMELESS, BEVELED EDGE, WALL MOUNTED	-
X-58	TALL CABINET	24"X20"X80"	ADJUSTABLE SHELIVING OR PULOOOUT ORGANIZERS	MATCHING VANITY LINE
X-60	MIRROR LIGHT	-	LED, BRUSHED NICKEL OR CHROME FINISH, DIMMABLE	PROGRESS LIGHTING OR EQUIVALENT
X-62	SHOWER BASE/ TRAY	36"X80"X5" OR CUSTOM	LOW PROFILE SLIP RESISTANT	MATCHING SHOWER SYSTEM
X-64	SHOWER DOOR	FRAMELESS GLASS, 1/4" THICK	CLEAR OR FROSTED TEMPERED GLASS CHROME OR BRUSHED NICKEL HARDWARE	DREAMLINE OR KOHLER

MATERIALS SCHEDULE				
F_MARK	F_ITEM	F_SIZE/ SPEC	F_MATERIAL/ FINISH	F_MANUFACTURER/NOTES
F-40	HARDWOOD FLOOR	7.5" WIDE PLANKS	ENGINEERED HARDWOOD - NATURAL OAK OR SIMILAR WARM TONE	PREFINISHED, FLOATING OR GLUE-DOWN
F-42	FLOOR TILE (WET AREA)	12X24 OR 24X48	PORCELAIN TILE MATTE FINISH RECTIFIED EDGES	DALTILE OR EQUIVALENT
F-44	WALL TILE	12X24 OR SUBWAY	PORCELAIN ORCERAMIC WALL TILE, WATERPROOF INSTALLATION	DALTILE OR EQUIVALENT
F-46	GARAGE FLOOR COATING	FULL COVERAGE	EPOXY OR POLYASPATIC GRAY OR FLAKE BROADCAST	-
F-48	PORCH/ DECK FLOORING	5/4 X 6 COMPOSITE	COMPOSITE DECKING LOW MAINTENANCE HIDDEN FASTENERS	TREX, TIMBER OR EQUIVALENT
F-50	ROOFING	ARCHITECTURAL SHINGLES	ASPHALT COMPOSITION SHINGLES, 30-YEAR WARRANTY	GAF TIMBERLINE OR CERTAINTEED
F-52	EXTERIOR SIDING	6" LAP	FIBER CEMENT SIDING FACTORY PRIMED, PAINTED FINISH	JAMES HARDIE HARDIE PLANK
F-54	BRICK	STANDARD MODULAR	FACE BRICK, MORTAR JOINTS	LOCAL SUPPLIER
F-56	RIDGE CAP	MATCHING ROOF SLOPE	ARCHITECTURAL RIDGE CAP SHINGLES OR METAL RIDGE VENT	MATCHING ROOFING MANUFACTURER
F-58	GUTTERS AND DOWNSPOUT	5" OR 6" K STYLE	ALUMINUM OR GALVALUME SEAMLESS	-
F-60	CROWN MOULDING	5 1/4 PROFILE	WOOD OR MDF, PAINTED	-
F-62	BASE MOULDING	5 1/4" OR TALLER	MATCHING FLOOR OR PAINTED WOOD	-
F-64	BED MOULDING	-	WOOD OR MDF, PAINTED TO MATCH COLUMN	-
F-66	FRONT PORCH COLUMN	12X12 BASE TAPERING TO 9X9 TOP	LOWER: BRICK VENEER; UPPER: TAPERED TIMBER POST(PAINTED/ STAINED	PRESSURE TREATED OR CEDAR TIMBER

NOTES:

B	Y REVISED	JS	
A	X REVISED	JS	
REV	DESCRIPTION	BY	DATE
AMENDMENTS			
ARCHITECT'S CONTACT DETAILS			
NAME:		VICTOR OMEH.	
EMAIL:		omehvictor@gmail.com	
WEBSITE:		www.victoromeh.github.io	
PROJECT TITLE			
SINGLE FAMILY HOME			
SITE			
509 BROOKHAVEN LANE, WESTFIELD, IN 46074			
CLIENT			
MICHAEL & SARAH WHITFIELD			
SCALE	DATE.	DRAWN BY.	
	JAN 2026	VICTOR OMEH	
SHEET NAME. SCHEDULES 2		SHEET NO.	
PROJECT NO. VO-2026-101		A6.2	

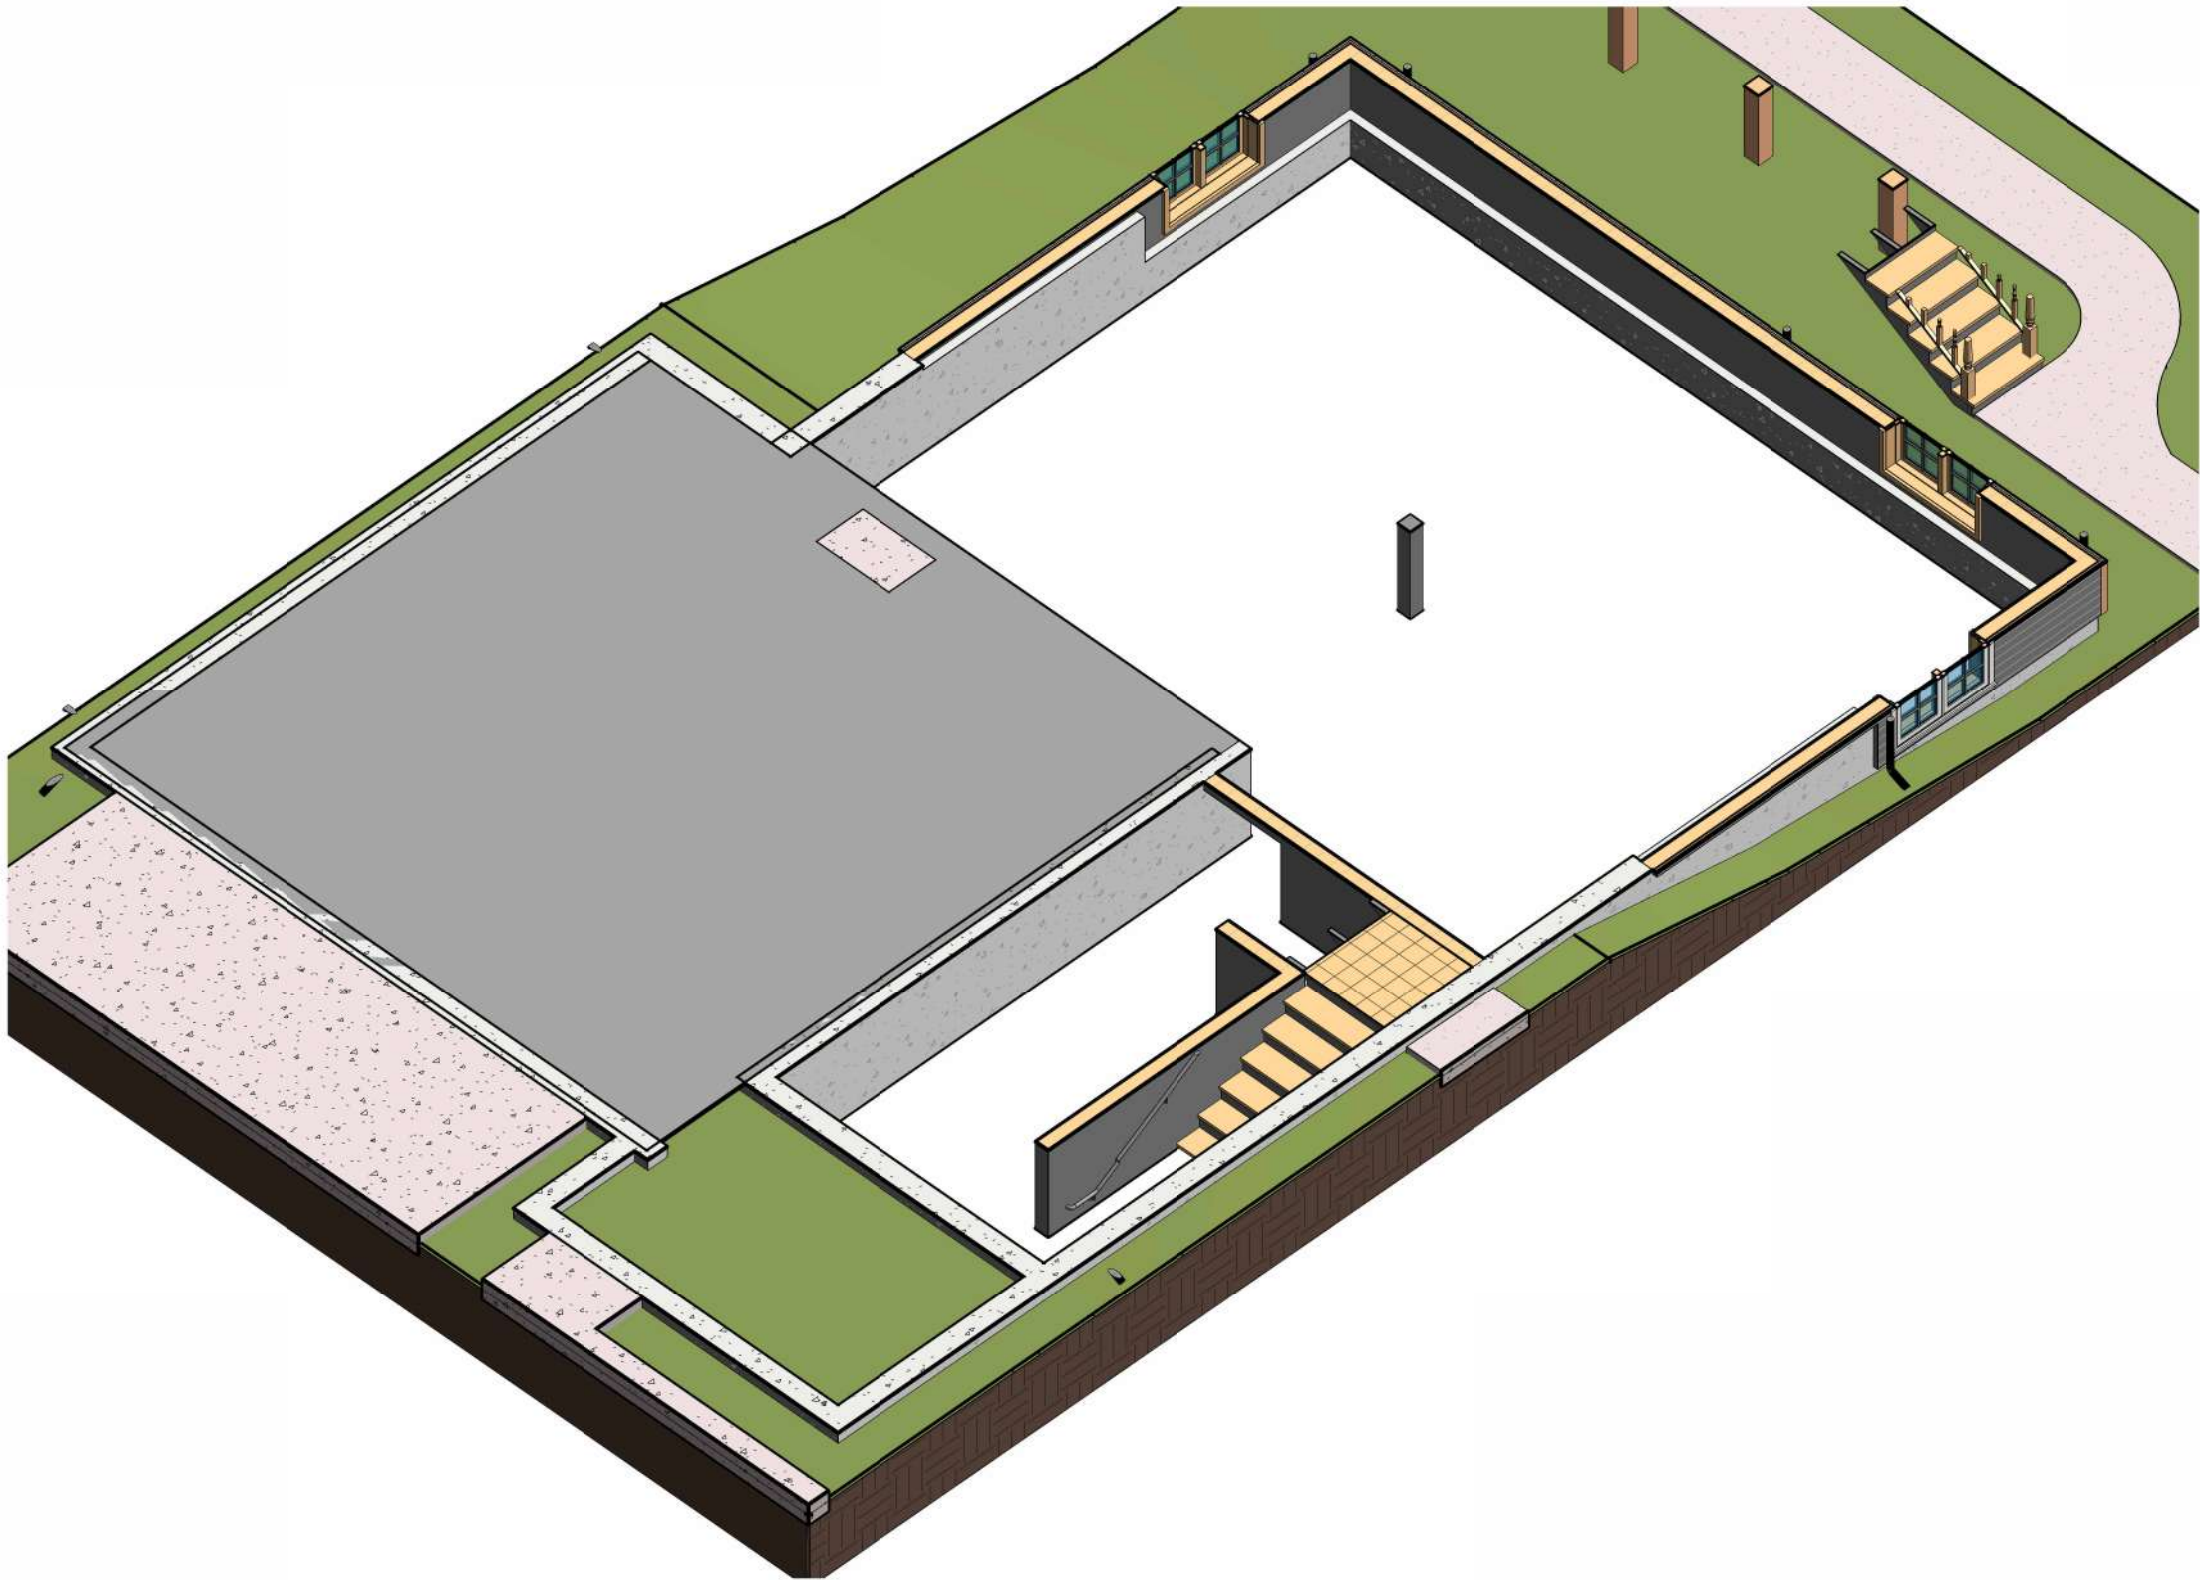

1

AXONOMETRIC VIEW (BASEMENT)

NOTES:

B	Y REVISED	JS	
A	X REVISED	JS	
REV	DESCRIPTION	BY	DATE

AMENDMENTS

ARCHITECT'S CONTACT DETAILS

NAME: VICTOR OMEH.
EMAIL: omehvictor@gmail.com
WEBSITE: www.victoromeh.github.io

PROJECT TITLE

SINGLE FAMILY HOME

SITE


509 BROOKHAVEN LANE,
WESTFIELD, IN 46074

CLIENT

MICHAEL & SARAH WHITFIELD

SCALE	DATE. JAN 2026	DRAWN BY. VICTOR OMEH
-------	-------------------	-----------------------------

SHEET NAME. AXONOMETRIC VIEW (BASEMENT)	SHEET NO. A7.0
PROJECT NO. VO-2026-101	

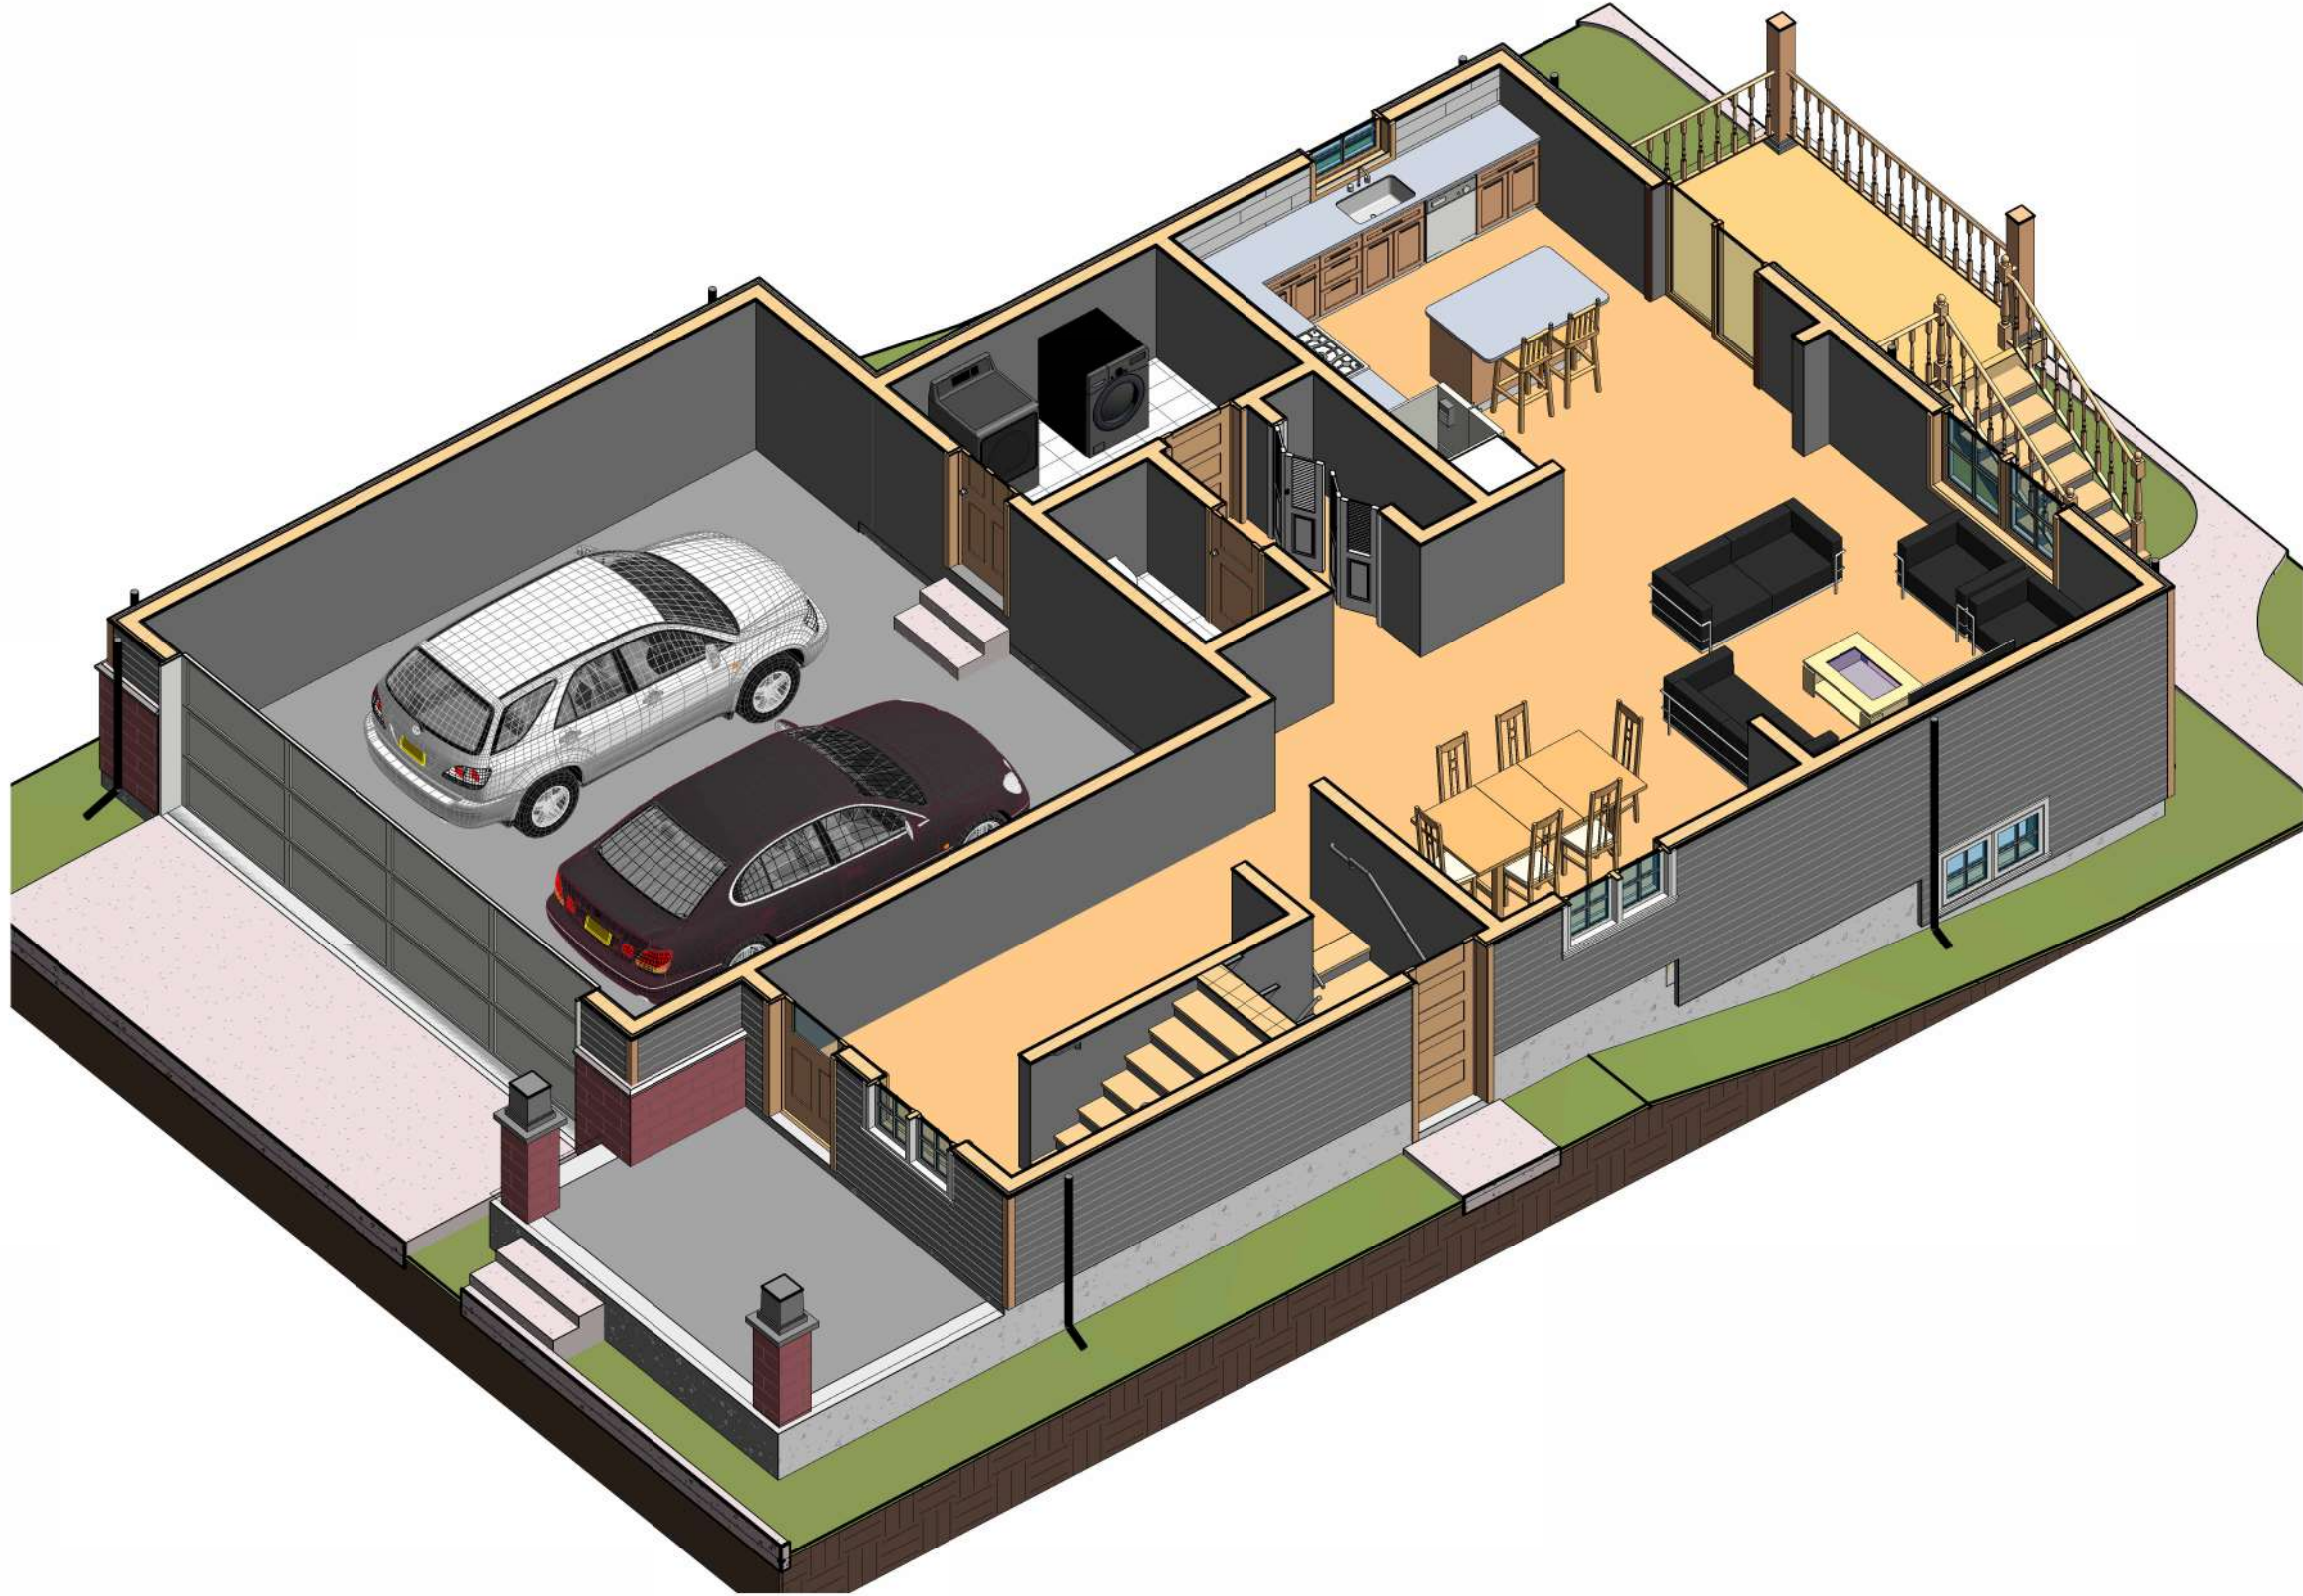

AXONOMETRIC VIEW (1ST FLOOR)

1

NOTES:

B	Y REVISED	JS	
A	X REVISED	JS	
REV	DESCRIPTION	BY	DATE

AMENDMENTS

ARCHITECT'S CONTACT DETAILS

NAME: VICTOR OMEH.

EMAIL: omehvictor@gmail.com

WEBSITE: www.victoromeh.github.io

PROJECT TITLE

SINGLE FAMILY HOME

SITE

509 BROOKHAVEN LANE,
WESTFIELD, IN 46074

CLIENT

MICHAEL & SARAH WHITFIELD

SCALE	DATE. JAN 2026	DRAWN BY. VICTOR OMEH
-------	-------------------	-----------------------------

SHEET NAME. AXONOMETRIC VIEW (FIRST FLOOR)	SHEET NO. A7.1
PROJECT NO. VO-2026-101	



AXONOMETRIC VIEW (2ND FLOOR)

NOTES:

B	Y REVISED	JS	
A	X REVISED	JS	
REV	DESCRIPTION	BY	DATE

AMENDMENTS

ARCHITECT'S CONTACT DETAILS

NAME: VICTOR OMEH.
EMAIL: omehvictor@gmail.com
WEBSITE: www.victoromeh.github.io

PROJECT TITLE

SINGLE FAMILY HOME

SITE

509 BROOKHAVEN LANE,
WESTFIELD, IN 46074

CLIENT

MICHAEL & SARAH WHITFIELD

SCALE	DATE. JAN 2026	DRAWN BY. VICTOR OMEH
-------	-------------------	-----------------------------

SHEET NAME. AXONOMETRIC VIEW (SECOND FLOOR)	SHEET NO. A7.2
PROJECT NO. VO-2026-101	



1

FRONT PERSPECTIVE

NOTES:

B	Y REVISED	JS	
A	X REVISED	JS	
REV	DESCRIPTION	BY	DATE

AMENDMENTS

ARCHITECT'S CONTACT DETAILS

NAME: VICTOR OMEH.
EMAIL: omehvictor@gmail.com
WEBSITE: www.victoromeh.github.io

PROJECT TITLE

SINGLE FAMILY HOME

SITE

509 BROOKHAVEN LANE,
WESTFIELD, IN 46074

CLIENT

MICHAEL & SARAH WHITFIELD

SCALE	DATE. JAN 2026	DRAWN BY. VICTOR OMEH
-------	-------------------	--------------------------

SHEET NAME. FRONT PERSPECTIVE		SHEET NO. A7.3
PROJECT NO. VO-2026-101		



NOTES:

B	Y REVISED	JS	
A	X REVISED	JS	
REV	DESCRIPTION	BY	DATE

AMENDMENTS

ARCHITECT'S CONTACT DETAILS

NAME: VICTOR OMEH.
EMAIL: omehvictor@gmail.com
WEBSITE: www.victoromeh.github.io

PROJECT TITLE

SINGLE FAMILY HOME

SITE

509 BROOKHAVEN LANE,
WESTFIELD, IN 46074

CLIENT

MICHAEL & SARAH WHITFIELD

SCALE	DATE. JAN 2026	DRAWN BY. VICTOR OMEH
-------	-------------------	--------------------------

SHEET NAME. REAR PERSPECTIVE	SHEET NO. A7.4
PROJECT NO. VO-2026-101	



3D VIEW (KITCHEN)

NOTES:

B	Y REVISED	JS	
A	X REVISED	JS	
REV	DESCRIPTION	BY	DATE

AMENDMENTS

ARCHITECT'S CONTACT DETAILS

NAME: VICTOR OMEH.
EMAIL: omehvictor@gmail.com
WEBSITE: www.victoromeh.github.io

PROJECT TITLE

SINGLE FAMILY HOME

SITE

509 BROOKHAVEN LANE,
WESTFIELD, IN 46074

CLIENT

MICHAEL & SARAH WHITFIELD

SCALE	DATE. JAN 2026	DRAWN BY. VICTOR OMEH
-------	-------------------	-----------------------------

SHEET NAME. 3D VIEW (KITCHEN)		SHEET NO. A7.5
PROJECT NO. VO-2026-101		



1

3D VIEW (BATHROOM)

NOTES:

B	Y REVISED	JS	
A	X REVISED	JS	
REV	DESCRIPTION	BY	DATE

AMENDMENTS

ARCHITECT'S CONTACT DETAILS

NAME: VICTOR OMEH.
EMAIL: omehvictor@gmail.com
WEBSITE: www.victoromeh.github.io

PROJECT TITLE

SINGLE FAMILY HOME

SITE

509 BROOKHAVEN LANE,
WESTFIELD, IN 46074

CLIENT

MICHAEL & SARAH WHITFIELD

SCALE	DATE. JAN 2026	DRAWN BY. VICTOR OMEH
-------	-------------------	--------------------------

SHEET NAME. 3D VIEW
(BATHROOM)

PROJECT NO. VO-2026-101

SHEET NO.

A7.6